


NOTE:

This sign must not be used on road network. It is to be installed at exit from properties, car parks etc. only.

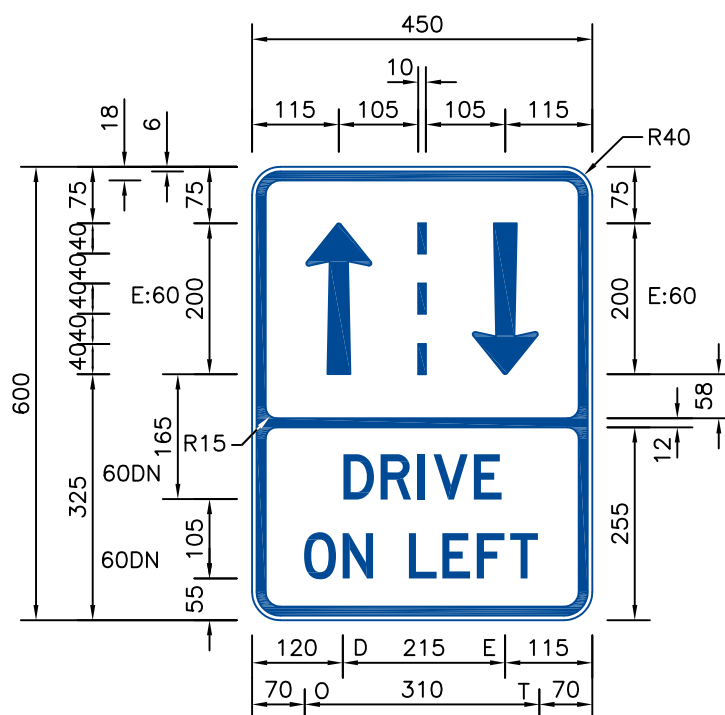

ADDITIONAL REFERENCE NOTES:
TES 12737(E Series) – Arrow
Detail Sheet.



Blue class 1

White class 1

Scale: 1:10

ALL DIMENSIONS ARE IN MILLIMETRES

Total Sign Area: 0.27 sqm

Sign Type: Road Safety

Location: Various

Drawn: Darren Blasdale
Edition: A Rev: 0
Date: 16 May, 2011

Authorisation:

Date:

AB Clark

TES 18546