




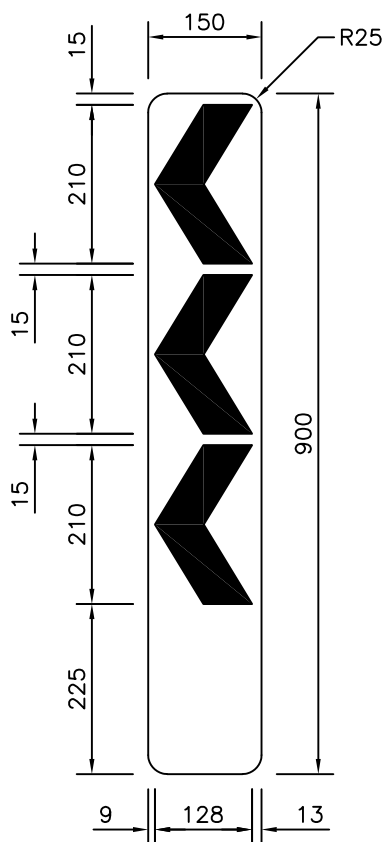

Left Construction

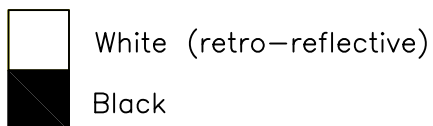

Right Construction

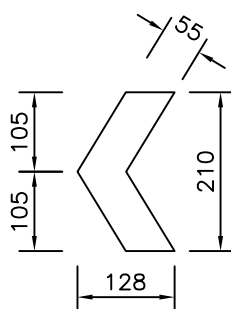

Note: Letters & Numerals AS1744:2015.

 Government of South Australia Department of Planning, Transport and Infrastructure	HAZARD MARKER 'Vertical Chevron Marker'	
Road and Marine Services Traffic Services, Traffic Solutions Unit Drawn: A. Simister	Authorisation:  Date: 26 November, 2019	D4-SA101(LorR)
	Scale: 1:10	