


SIGN SIZE, mm
W3-3-1A 600 x 600
W3-3-1B (Illust.) 750 x 750
W3-3-1C 900 x 900
W3-3-1D 1200 x 1200

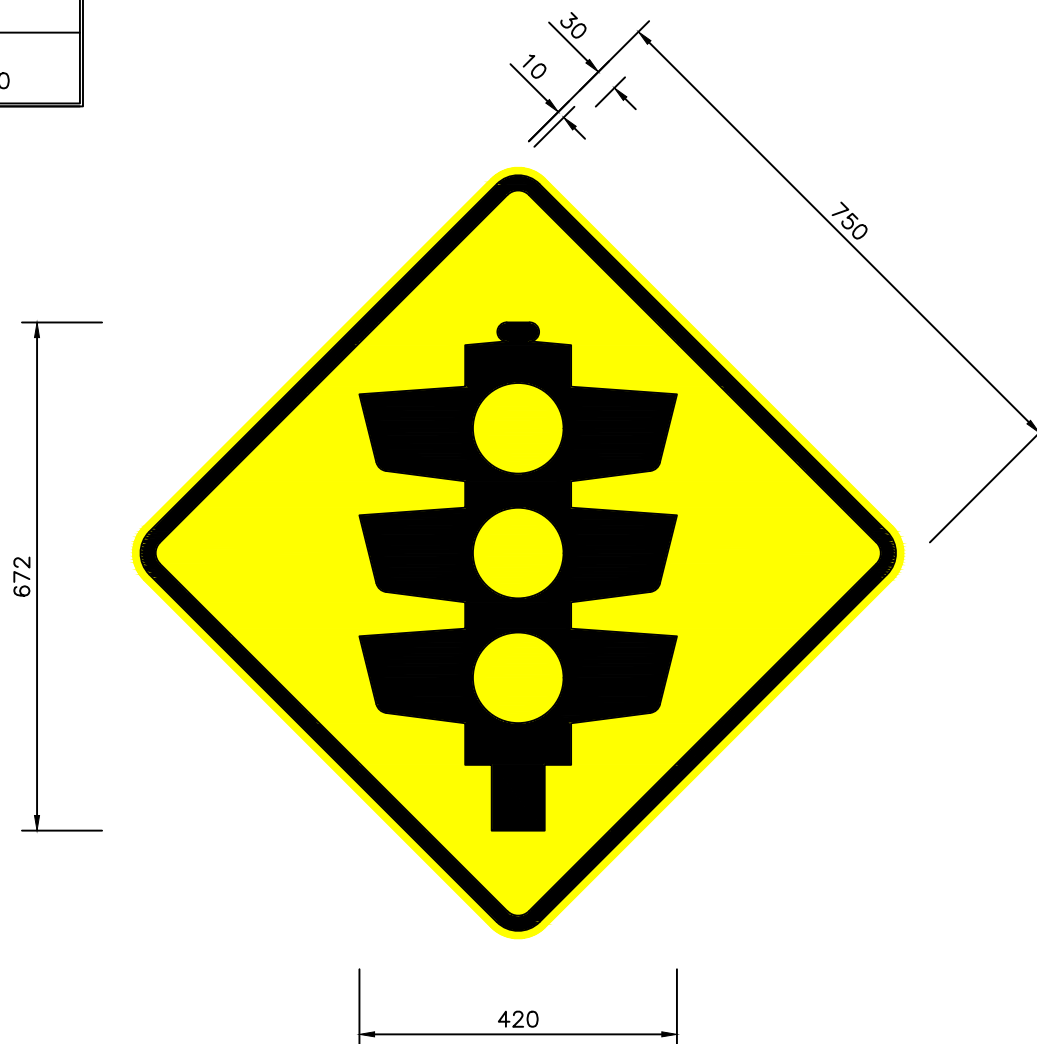

Signals Ahead (Use fluorescent yellow-green colour for mid-block pedestrian crossings only W3-3-2)



Black

Yellow class 400

Note: Letters & Numerals AS1744:2015.



Government of South Australia
Department for Infrastructure
and Transport

Road and Marine Services
Network Management Services, Traffic Solutions Unit

Authorisation:

Date: 19 July, 2022

WARNING SIGN
'Signals Ahead'

W3-3-1

Drawn: M. Douglas

Scale: 1:10