


Transport SA
Statewide Operational Coordination Group
Specific Road Signs - Specifications, South Australia

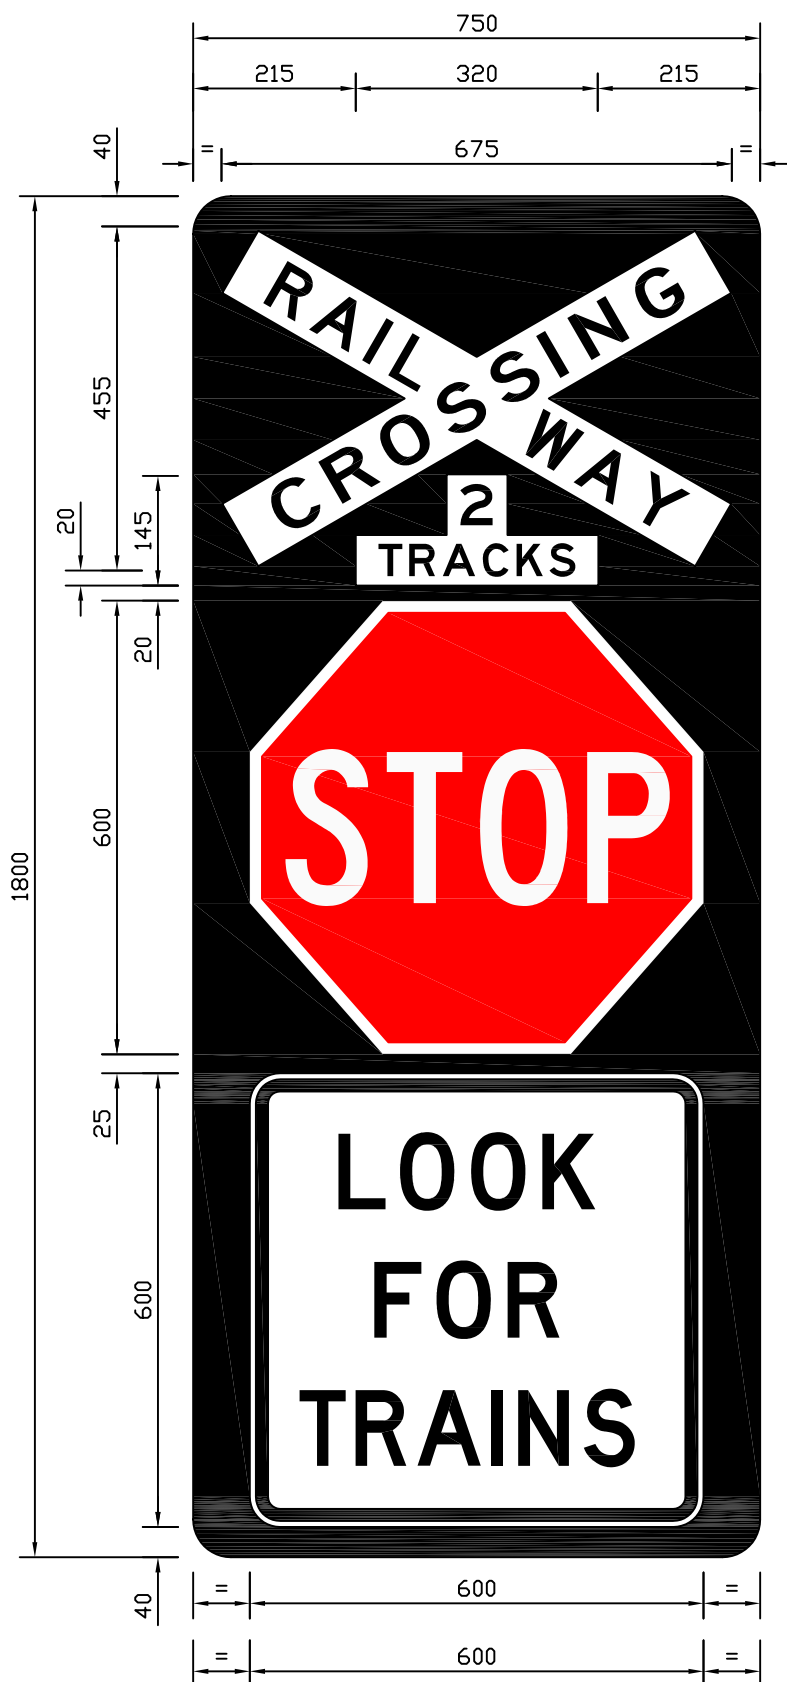

W7-1A (modified) (53.5%)

W7-2A (modified) (53.5%)

R1-1A

G9-48A

NOTES:

SIGNS:

W7-1A (53.5%) (modified)

W7-2A (53.5%) (modified)

R1-1A

G9-48A

Refer to AS1743-2001 for details.

TARGET BOARD:

Colour: Black background.

Border: Outer corner radius = 40mm.

Sign corner radius = 50mm.

Total Area = 1.35 sq.m

SCALE 1:10 ALL DIMENSIONS ARE IN MILLIMETRES.

Sign Type: Regulatory Sign

Location: Non-Public Roads – Double Track Crossings

Drawn: A. Watt
 Edition: A Rev: 0

Date: 21 November, 2001

Authorisation:

Date:

AB Clark

TES 13908(2)