
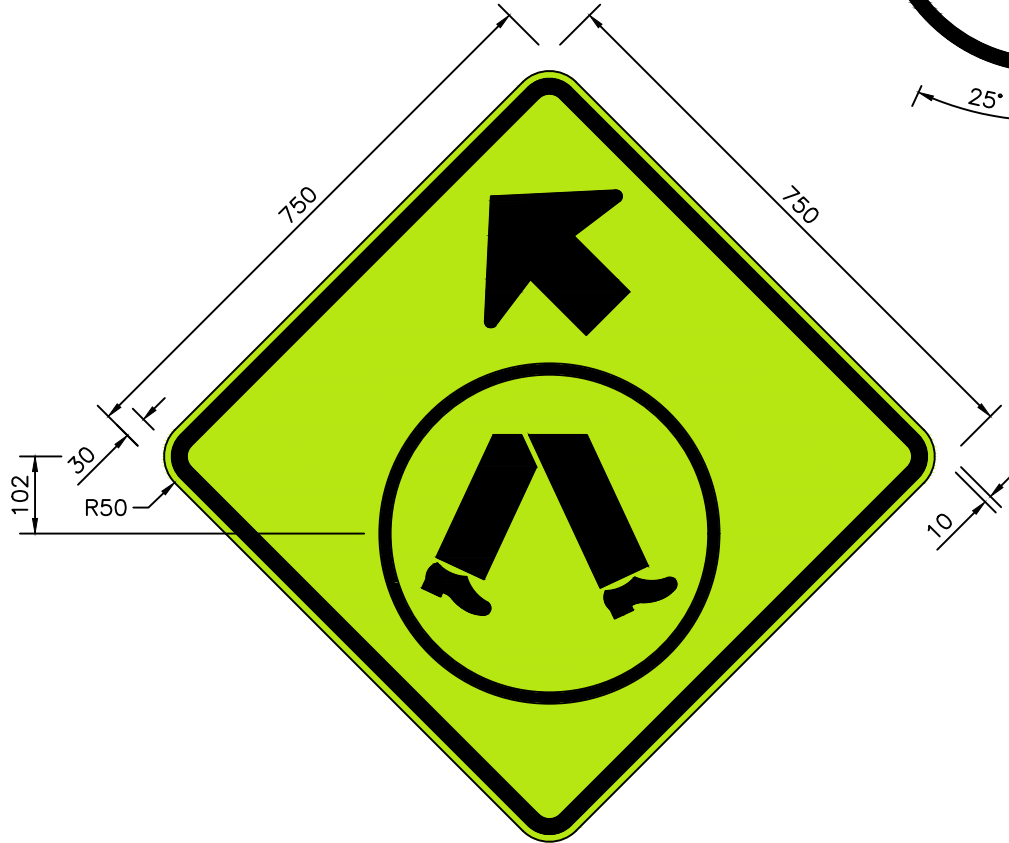


SIGN SIZE, mm
W6-2-2A 600 x 600
W6-2-2B(Illust.) 750 x 750
W6-2-2C 900 x 900

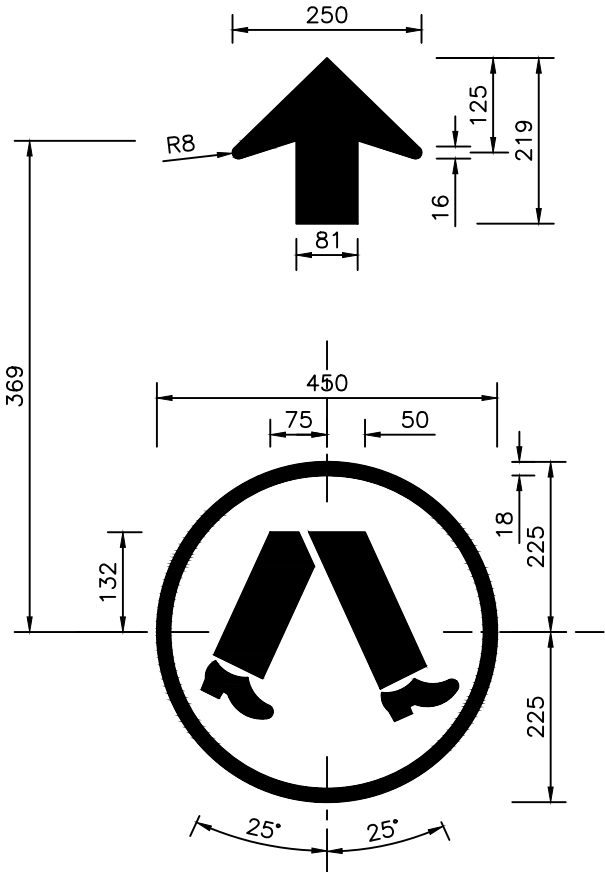

Black

Fluorescent Yellow Green (retroreflective)

Note: Letters & Numerals AS1744:2015.

 Government of South Australia Department for Infrastructure and Transport	WARNING SIGN 'Pedestrian Crossing Ahead 45 Deg LorR'	
Road and Marine Services Network Management Services, Traffic Solutions Unit	Authorisation: 	W6-2-2 Left or Right
Drawn: M. Douglas	Scale: 1: 10	Date: 23 July, 2024