


SIGN SIZE, mm
W7-SA103B(Illust.) 750x750
W7-SA103C 900x900

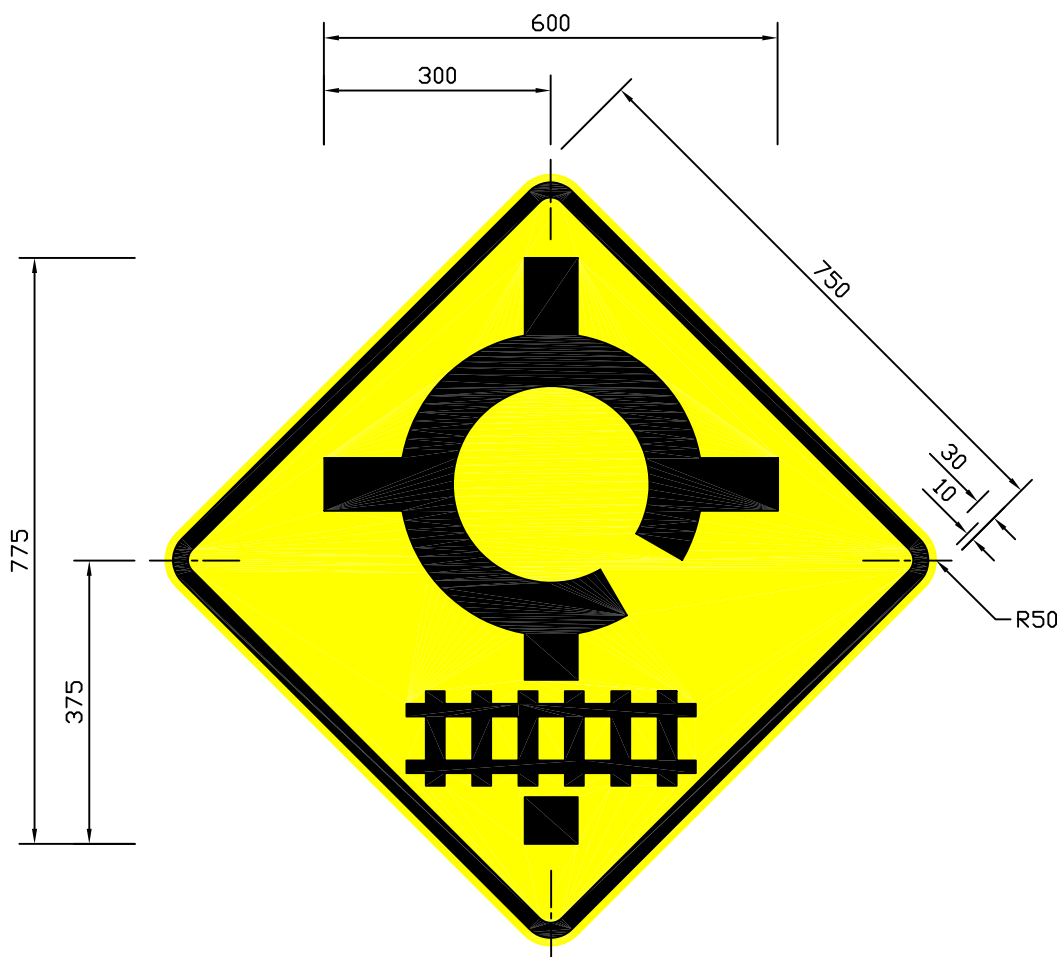

Yellow (retro-reflective)



Black

Note: Letters & Numerals AS1744.

TRANSPORT SA

Statewide Operational Coordination Group
Traffic Management Unit

Drawn: G.Roberts

Scale: 1:10

WARNING SIGN

'Diagrammatic Warning on Main
Road (before Roundabout)

Authorisation:

A.B. Clark

Date: 19 June, 2002

W7-SA103