


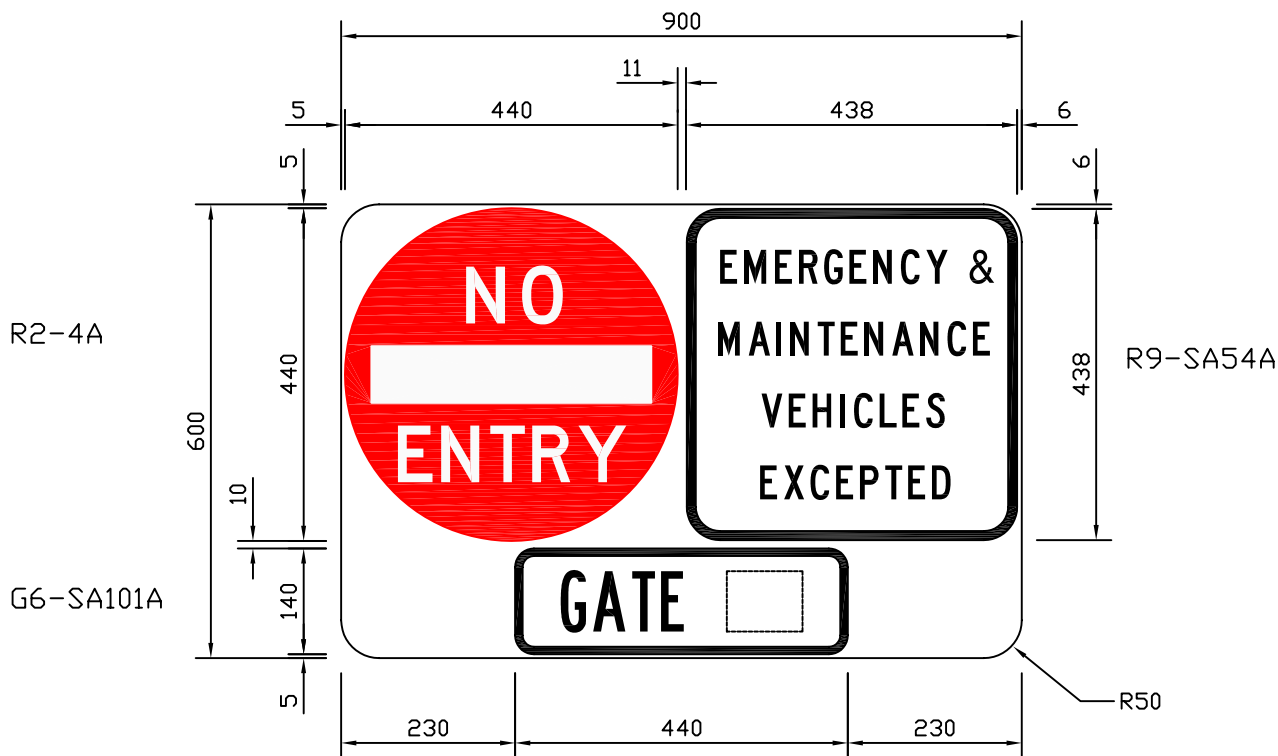

Red (retro-reflective)



White (retro-reflective)



Black

Note: Letters & Numerals AS1744.



REGULATORY SIGN

'No Entry—Emergency And Maintenance Vehicles Excepted Gate X'

Statewide Operational Coordination Group
Traffic Management Unit

Authorisation:

AB Clark

Date: 8 April, 2002

R2-SA101

Drawn: G. Roberts

Scale: 1:10