


| SIGN SIZE, mm                 |
|-------------------------------|
| R2-SA103A<br>600x960          |
| R2-SA103B(Illus.)<br>750x1200 |
| R2-SA103C<br>900x1440         |

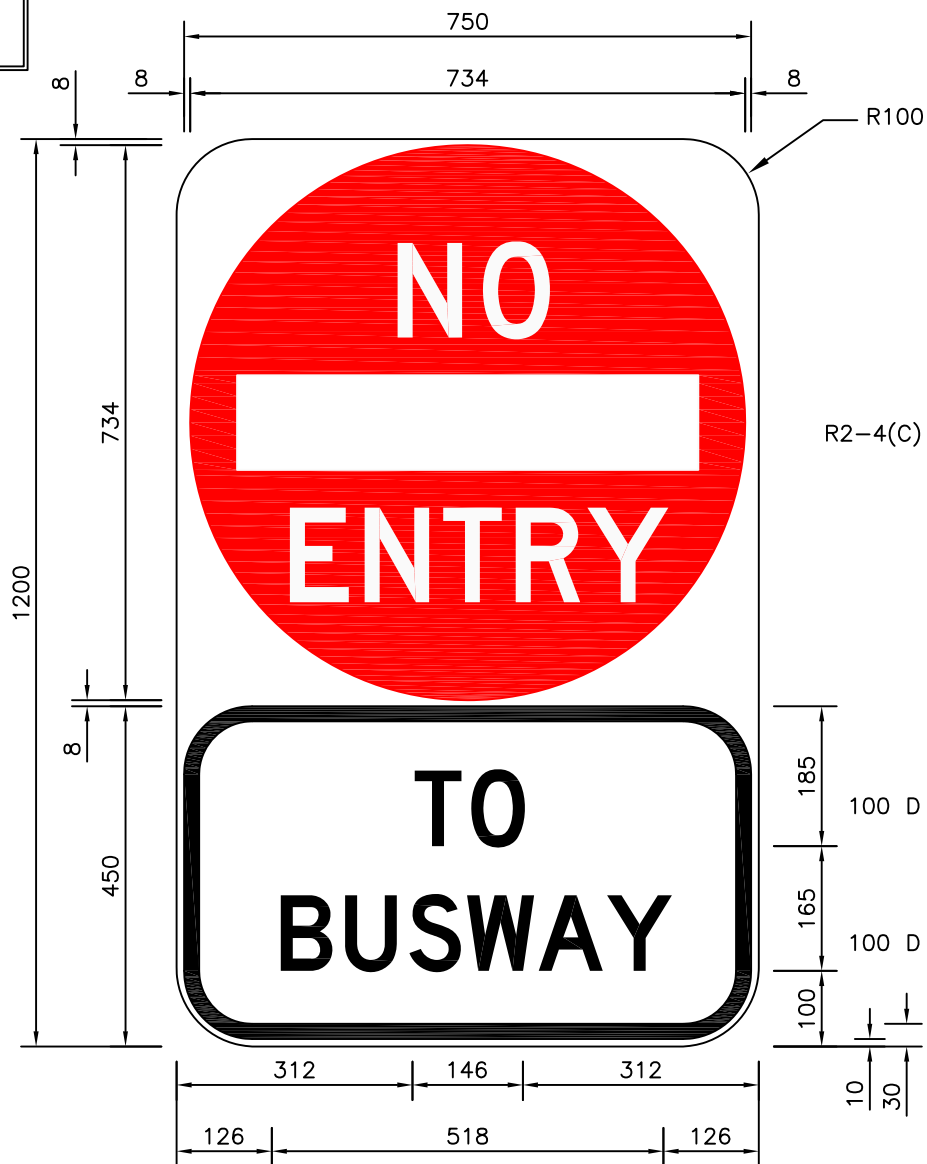

Red (retro-reflective)



White (retro-reflective)



Black

Note: Letters & Numerals AS1744:2015.



**Government of South Australia**  
Department of Planning,  
Transport and Infrastructure

REGULATORY SIGN

'No Entry To Busway'

Technical Services  
Safety and Service Division

Authorisation:

Date: 15 April, 2015

**R2-SA103**

Drawn: A. Simister

Scale: 1:10