


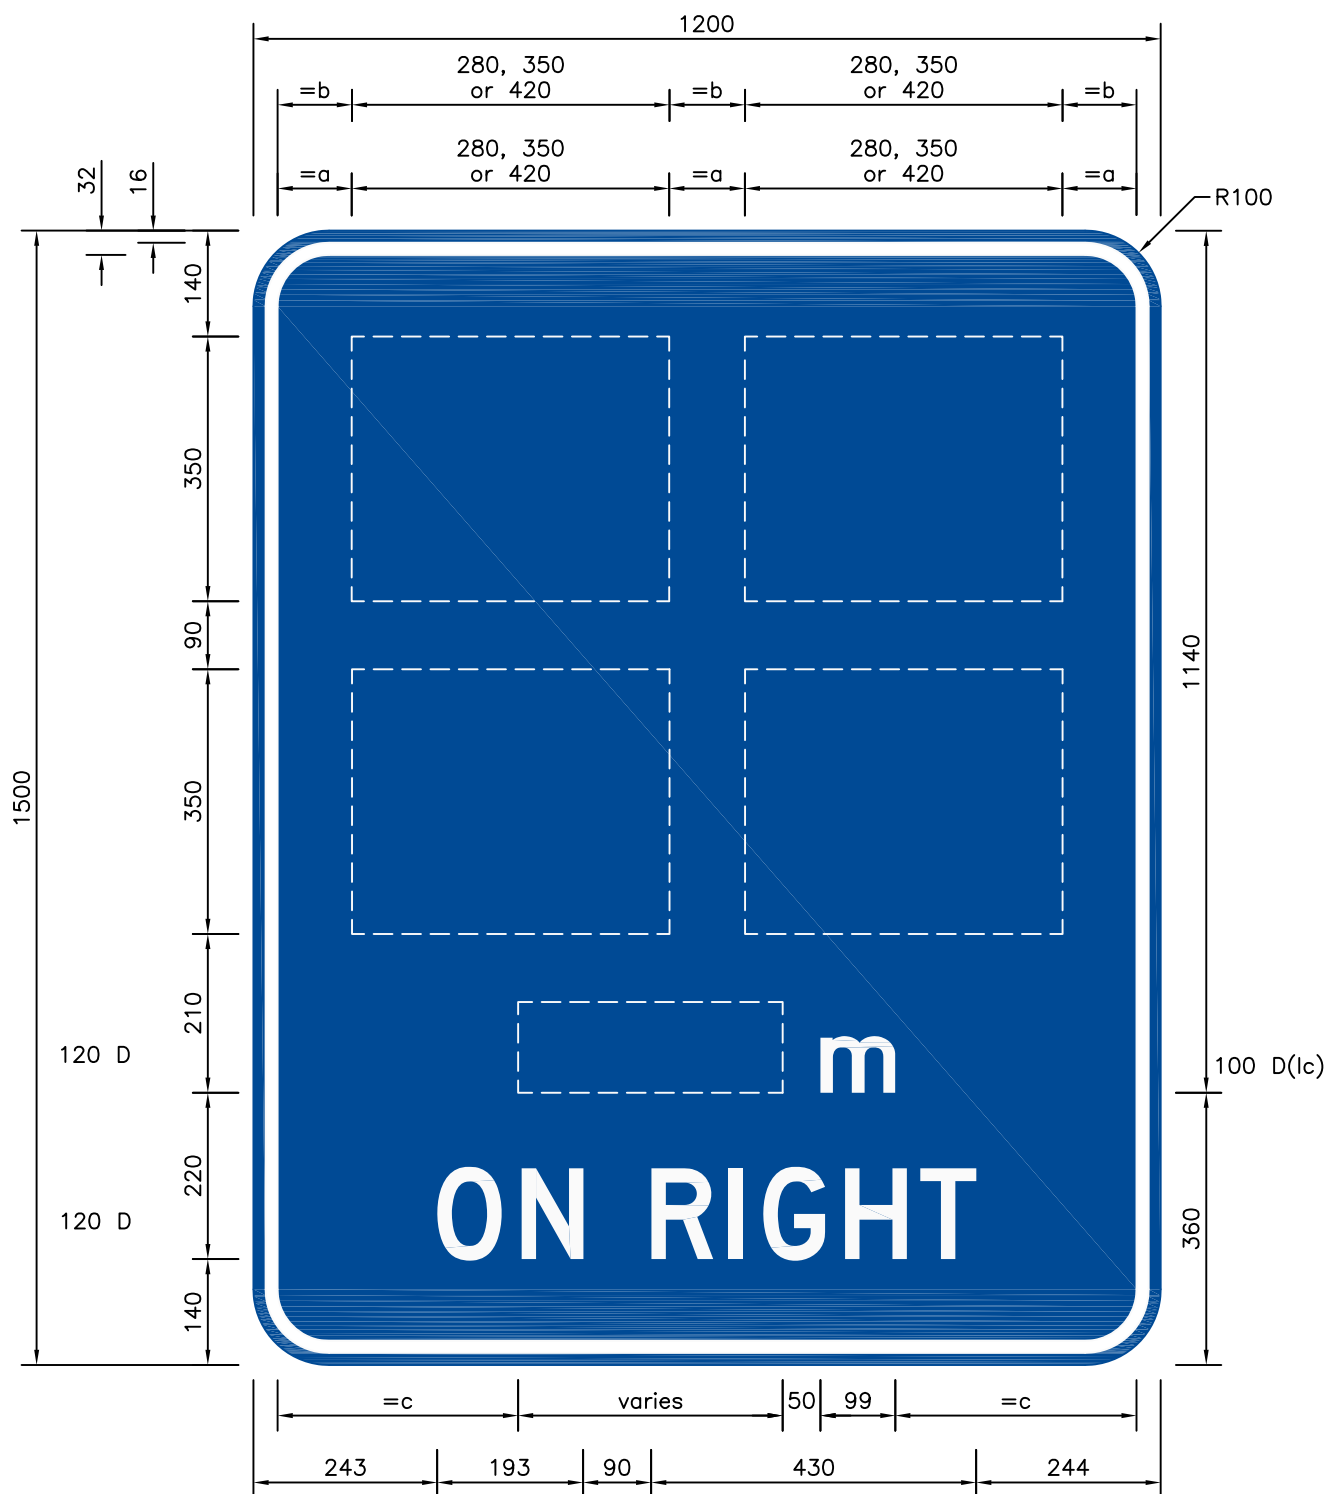

- White (retro-reflective)
- Blue (retro-reflective)

Note: Letters & Numerals AS1744:2015.

 Government of South Australia Department of Planning, Transport and Infrastructure	GUIDE SIGN 'Advance Sign – Service Symbol XXXm on Right (4)'	
Technical Services Safety and Service Division	Authorisation: 	G7-2-4A (MOD)
	Drawn: A. Simister	
	Scale: 1:10	Date: 5 May, 2015