


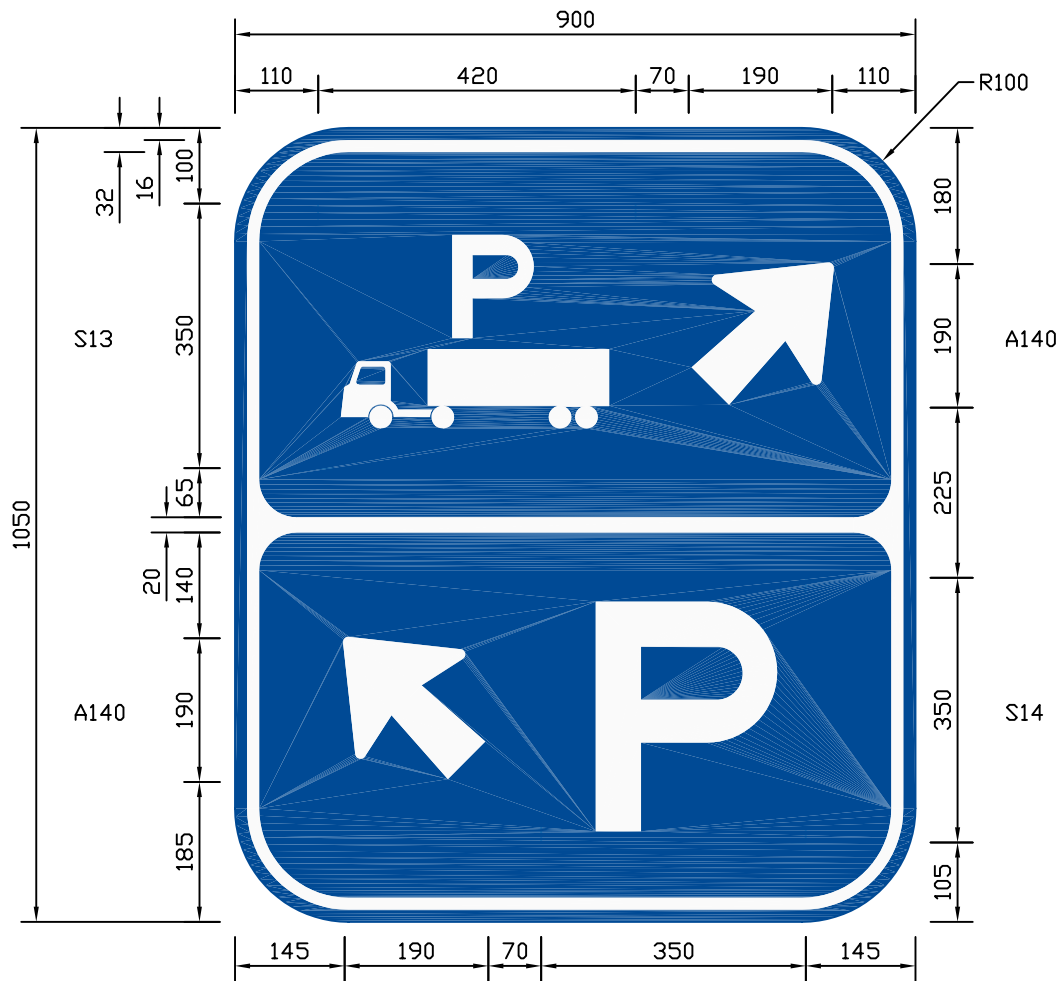

Blue (retro-reflective)

White (retro-reflective)

Note: Letters & Numerals AS1744.

TRANSPORT SA

Statewide Operational Coordination Group
Traffic Management Unit

Drawn: A. Watt

Scale: 1:10

GUIDE SIGN
'Location/Position Sign – Truck Parking / \\
Car Parking Rest Area Complex'

Authorisation:

A. B. Clark
Date: 29 April, 2002

G7-SA124-1