


SIGN SIZE, mm
R3-SA56A(Illus.) 450x1200
R3-SA56B 600x1600

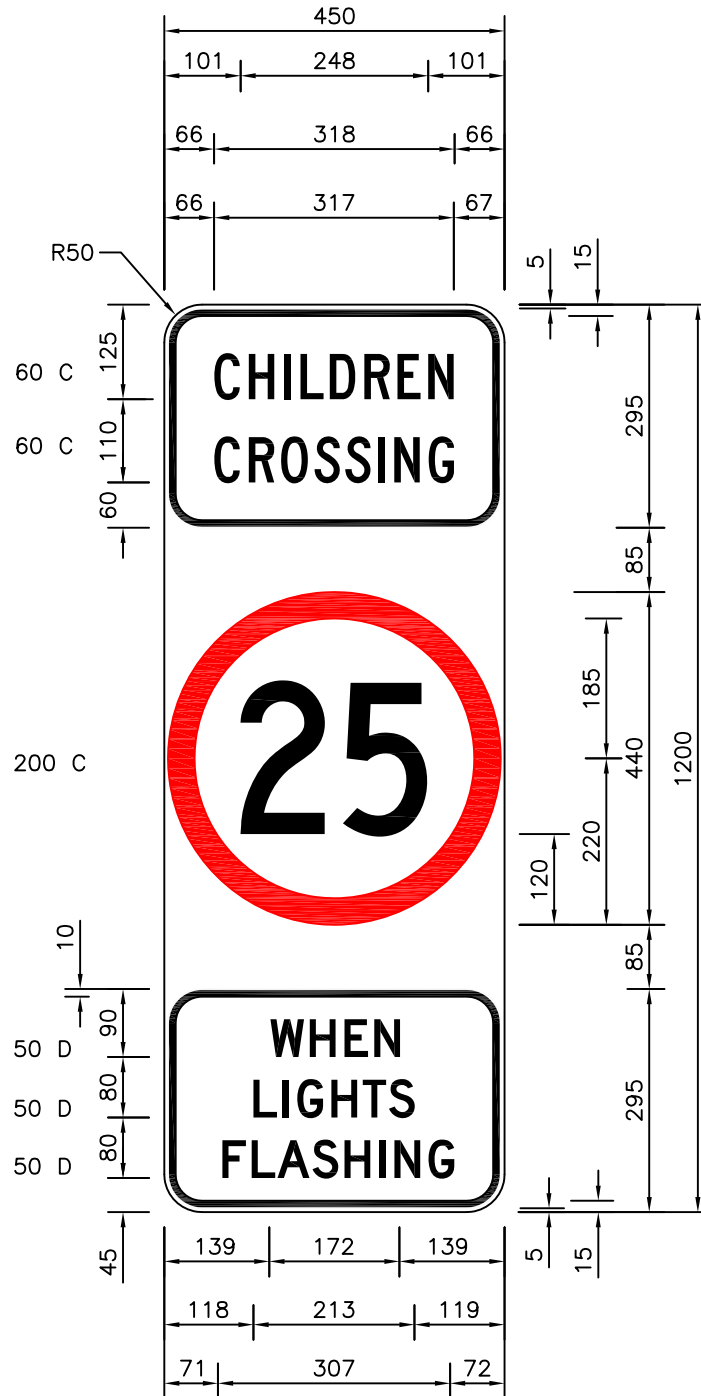

Red (retro-reflective)



White (retro-reflective)



Black

Formerly R4-SA56

Note: Letters & Numerals AS1744:2015.



Government of South Australia
Department of Planning,
Transport and Infrastructure

Technical Services
Safety and Service Division

Authorisation:

Date: 15 April, 2015

REGULATORY SIGN
"Koala" Pedestrian Crossing

R3-SA56

Drawn: A. Simister

Scale: 1:10