


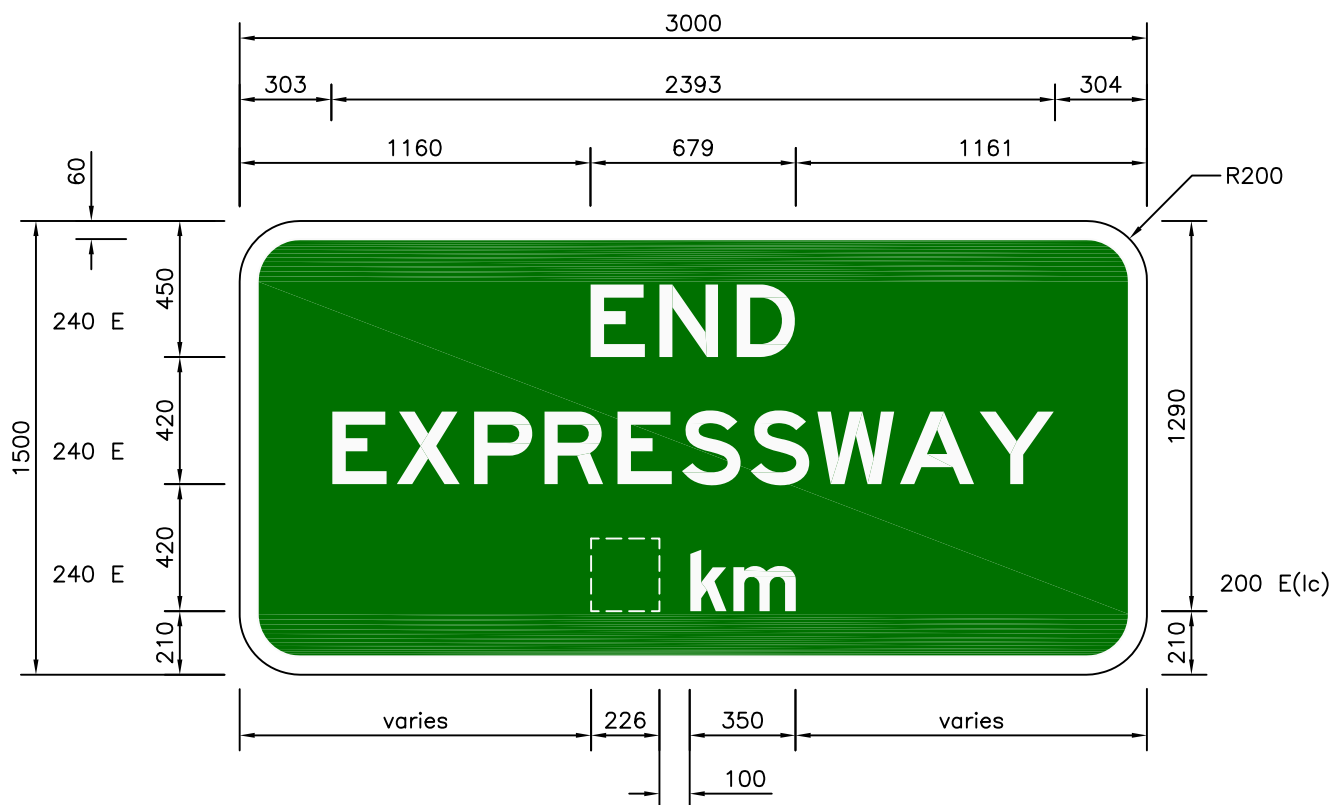

White (retro-reflective)



Green (retro-reflective)

Note: Letters & Numerals AS1744:2015.



Government of South Australia
Department of Planning,
Transport and Infrastructure

Technical Services
Safety and Service Division

Authorisation:

Date: 13 May, 2015

GUIDE SIGN

'End Expressway Xkm'

GE6-SA112

Drawn: A. Simister

Scale: 1:25