


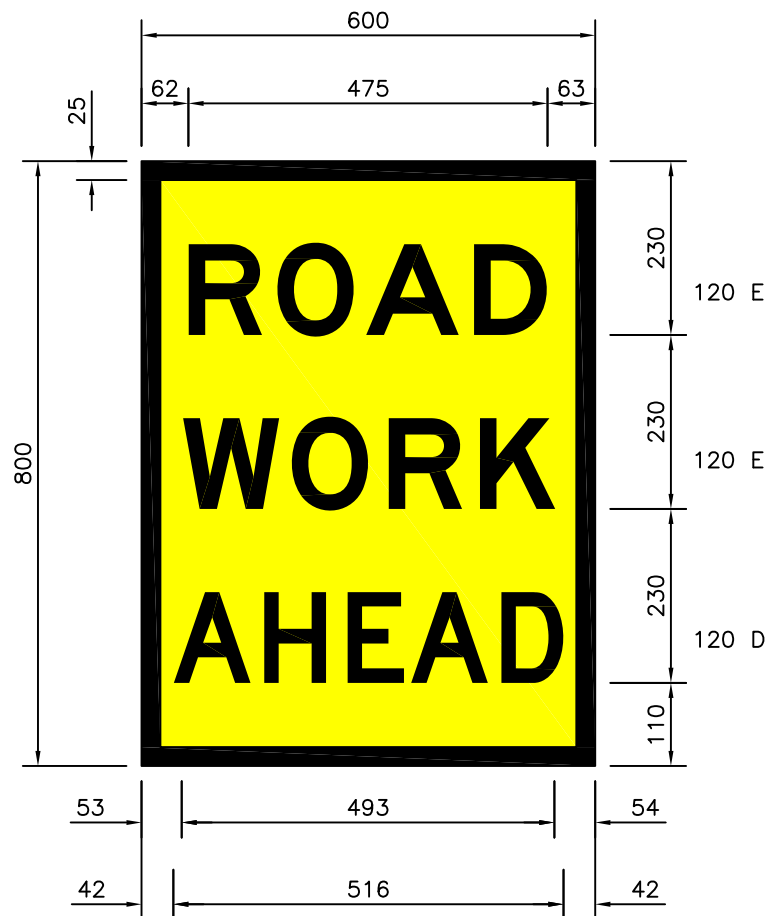

Note: For larger Standard size refer to AS 1743.
 *AA size shall only be used on local residential roads in 40km/h or 50km/h traffic areas.



Yellow (retro-reflective)



Black

Note: Letters & Numerals AS1744:2015.



Government of South Australia
 Department of Planning,
 Transport and Infrastructure

Technical Services
 Safety and Service Division

Drawn: A. Simister

Scale: 1:10

Authorisation:

Date: 23 April, 2015

TEMPORARY WARNING SIGN

'Road Work Ahead (3 Lines)'

T1-31AA