




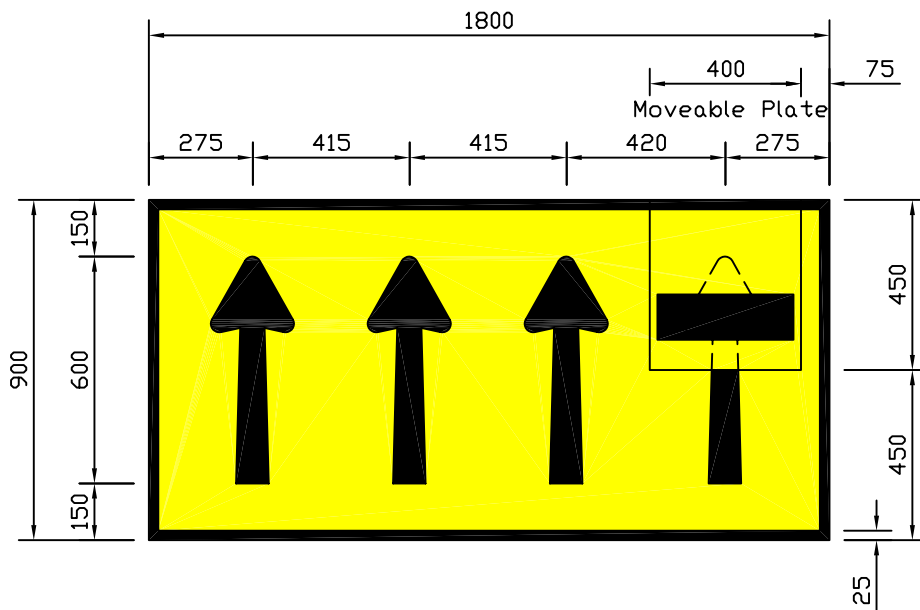

Arrow Details

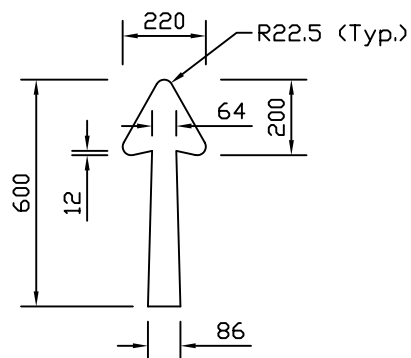

Moveable Plate

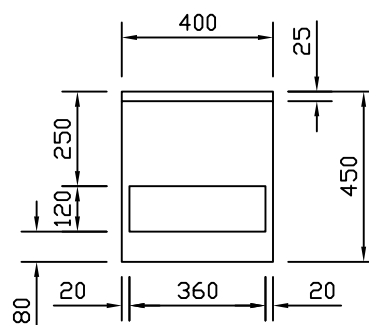

Yellow (retro-reflective)



Black

Note: Letters & Numerals AS1744.



TEMPORARY WARNING SIGN

'4 Lanes Status'

Statewide Operational Coordination Group
Traffic Management Unit

Authorisation:

A.B. Clark

Date: 24 April, 2002

Drawn: G.Roberts

Scale: 1:20

T2-6-SA3