



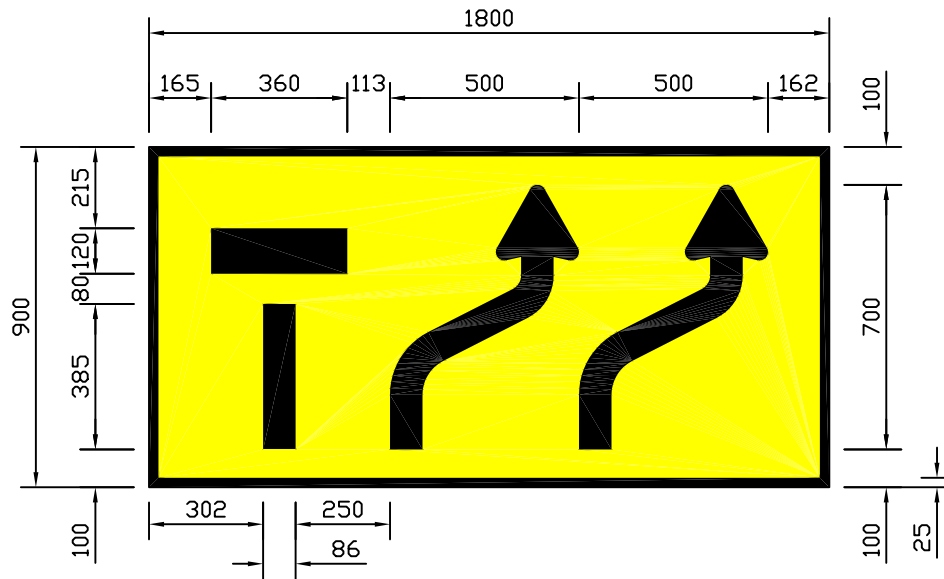

ARROW DETAILS

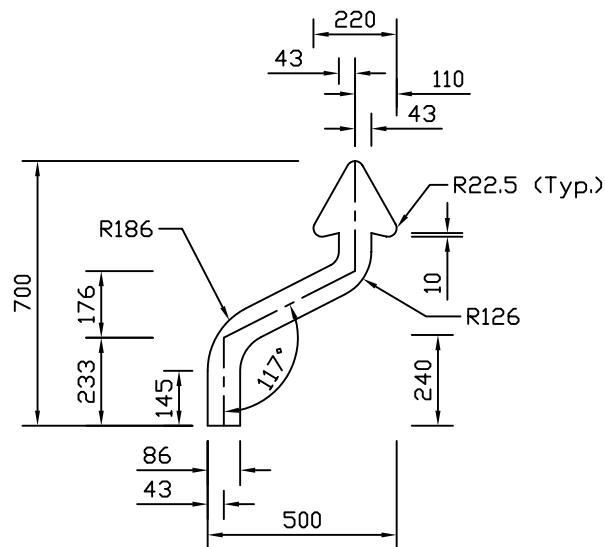

 Yellow (retro-reflective)

 Black

Note: Letters & Numerals AS1744.

 **TRANSPORT SA**

TEMPORARY WARNING SIGN

'3 Lanes Status (2 reverse curves)'

Statewide Operational Coordination Group
Traffic Management Unit

Authorisation:

A.B. Clark

Date: 11 March, 2003

Drawn: G.Roberts

Scale: 1:20

T2-6-SA102