


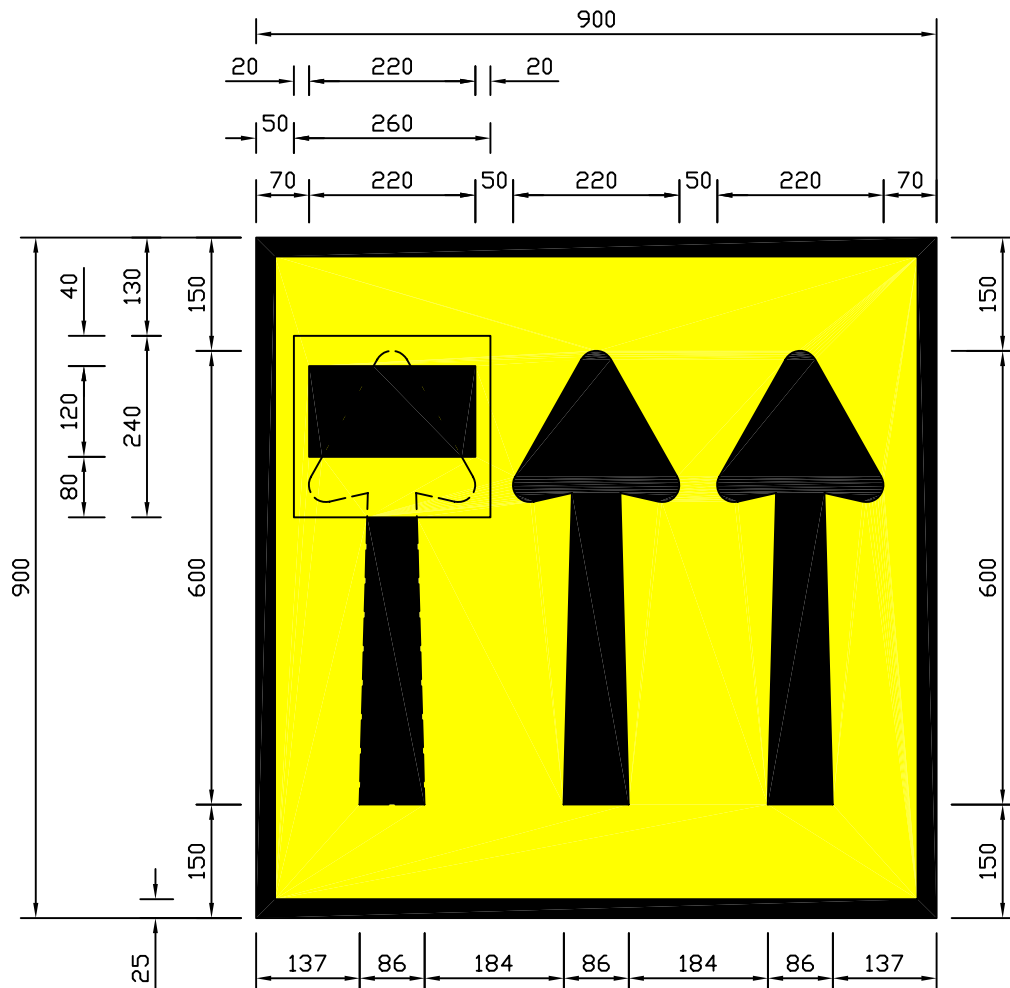


NOTE:
To be used as a substitute for
T2-6-2 for locations of restricted
widths, ie medians, narrow footpaths.

 Yellow (retro-reflective)

 Black

Note: Letters & Numerals AS1744.

Arrow Details

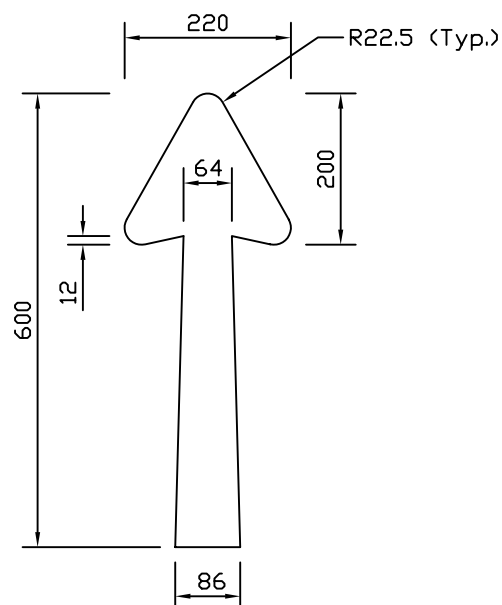

 **TRANSPORT SA**

TEMPORARY WARNING SIGN

'Narrow 3 Lane Status'

Statewide Operational Coordination Group
Traffic Management Unit

Authorisation:

Date: 24 April, 2002

Drawn: G. Roberts

Scale: 1:10

T2-6-SA108