


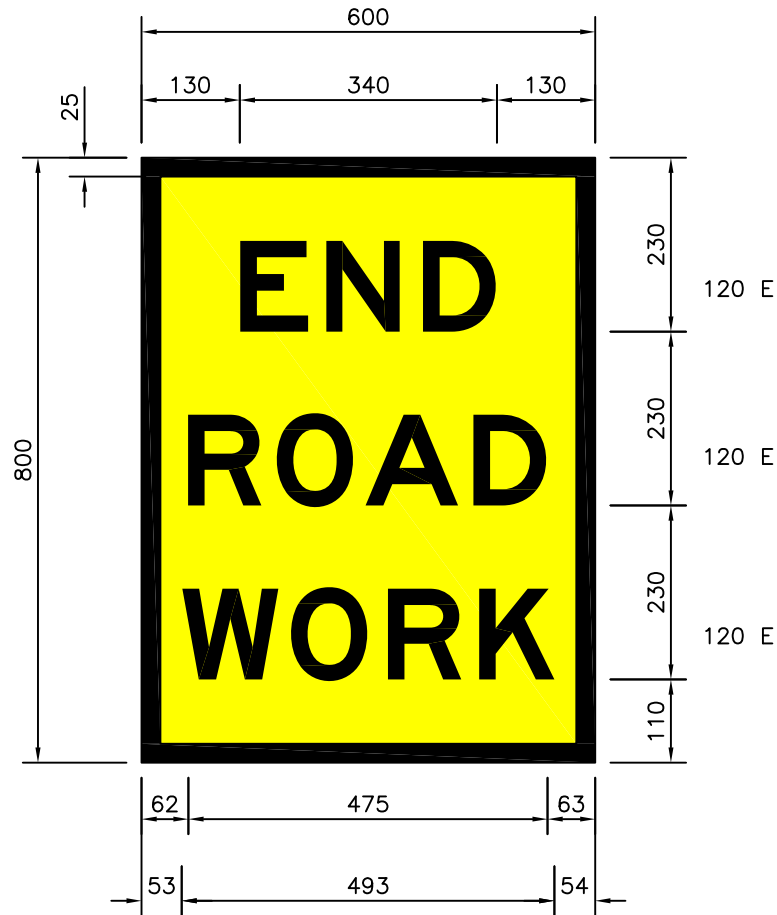

Note: For larger Standard size refer to AS 1743.
 *S size shall only be used on local residential roads in 40km/h or 50km/h traffic areas.

 Yellow (retro-reflective)

 Black

Note: Letters & Numerals AS1744:2015.

 Government of South Australia Department of Planning, Transport and Infrastructure	TEMPORARY WARNING SIGN 'End Road Work (3 Lines)	
Technical Services Safety and Service Division	Authorisation: 	T2-17AA
Drawn: A. Simister	Scale: 1:10	
Date: 30 April, 2015		