


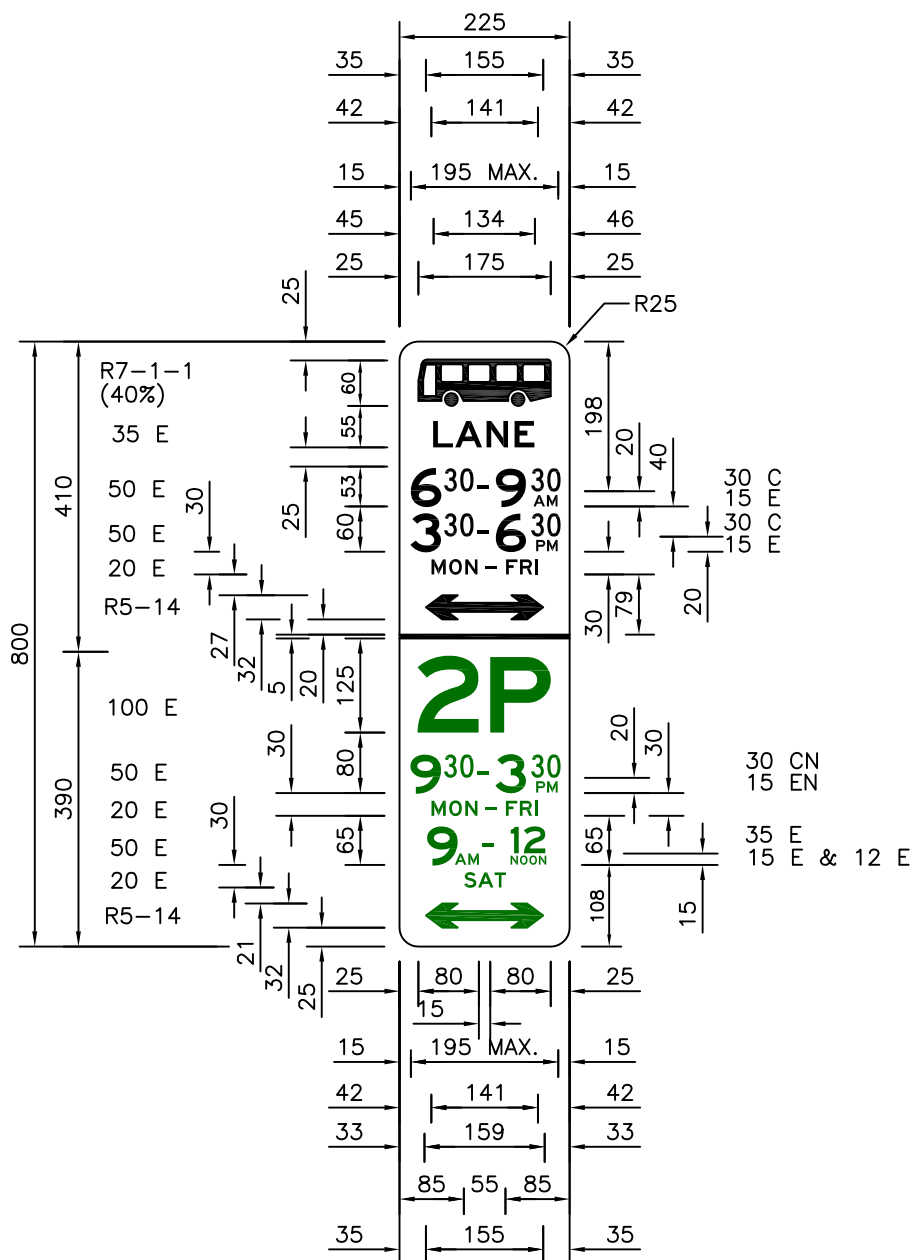

 Green (non-reflective)

 White (non-reflective)

 Black

Note: Letters & Numerals AS1744:2015.



Government of South Australia
Department of Planning,
Transport and Infrastructure

Technical Services
Safety and Service Division

Drawn: A. Simister

Scale: 1:10

Authorisation:

Date: 19 May, 2015

REGULATORY SIGN

'Part Time Bus Lane/Parking – Two Time Periods'

R5-SA100-2N