


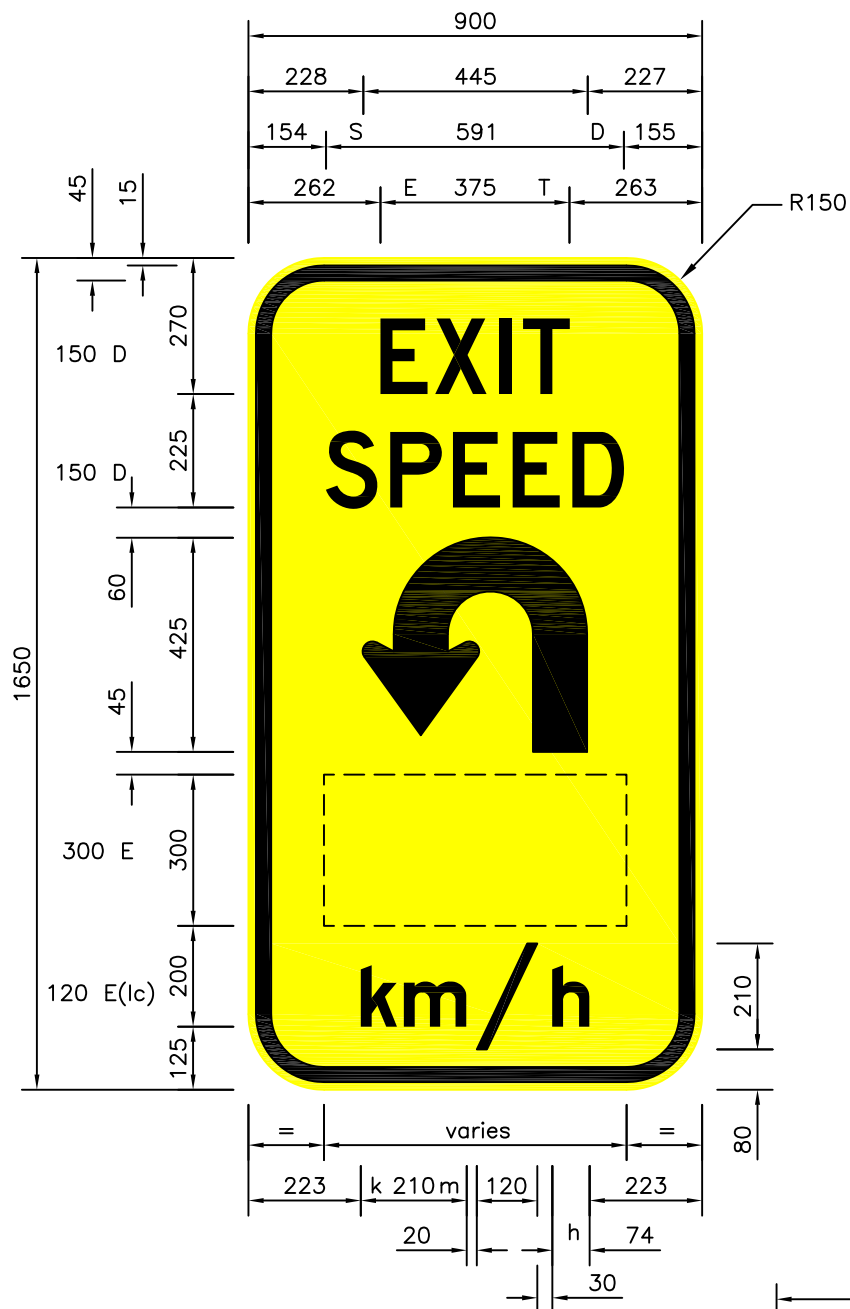

 Yellow (retro-reflective)

 Black

Note: Letters & Numerals AS1744:2015.

 Government of South Australia Department of Planning, Transport and Infrastructure	WARNING SIGN 'Exit Speed Hairpin Bend....km/h'		
Technical Services Safety and Service Division		Authorisation: 	W1-9-5AA (LorR)
Drawn: A. Simister	Scale: 1:15	Date: 19 May, 2015	