


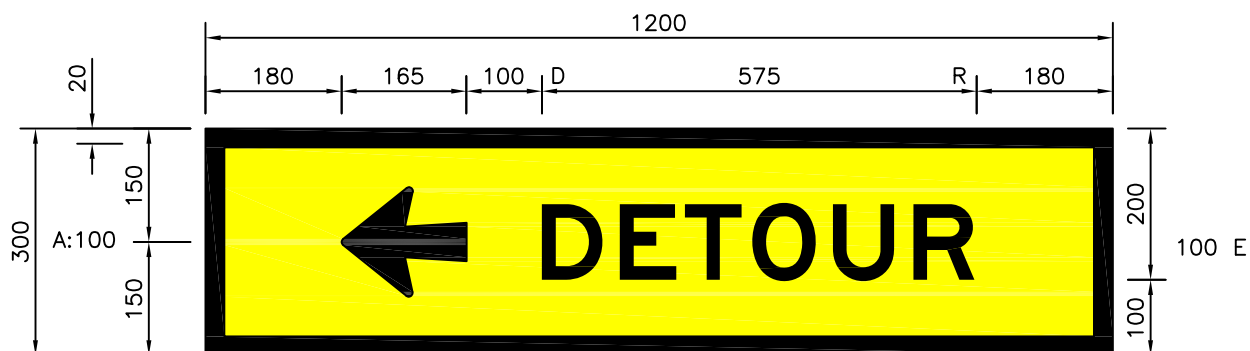

Dimensions apply to straight ahead,
left or right construction.

NOTE:

To be used in multi-message sign
frames only.



Black

Yellow class 1

Note: Letters & Numerals AS1744:2015.



Government of South Australia
Department of Planning,
Transport and Infrastructure

Road and Marine Services
Traffic Services, Traffic Solutions Unit

Drawn: A. Simister

Scale: 1:10

Authorisation:

Date: 10 January, 2020

TEMPORARY WARNING SIGN
'Detour'

TM5-1B
(SorLorR)