
| SIGN SIZE, mm |
|---|
| G9–SA111A(Illust.)<br>1000x1000 |
| G9–SA111B<br>1400x1400 |

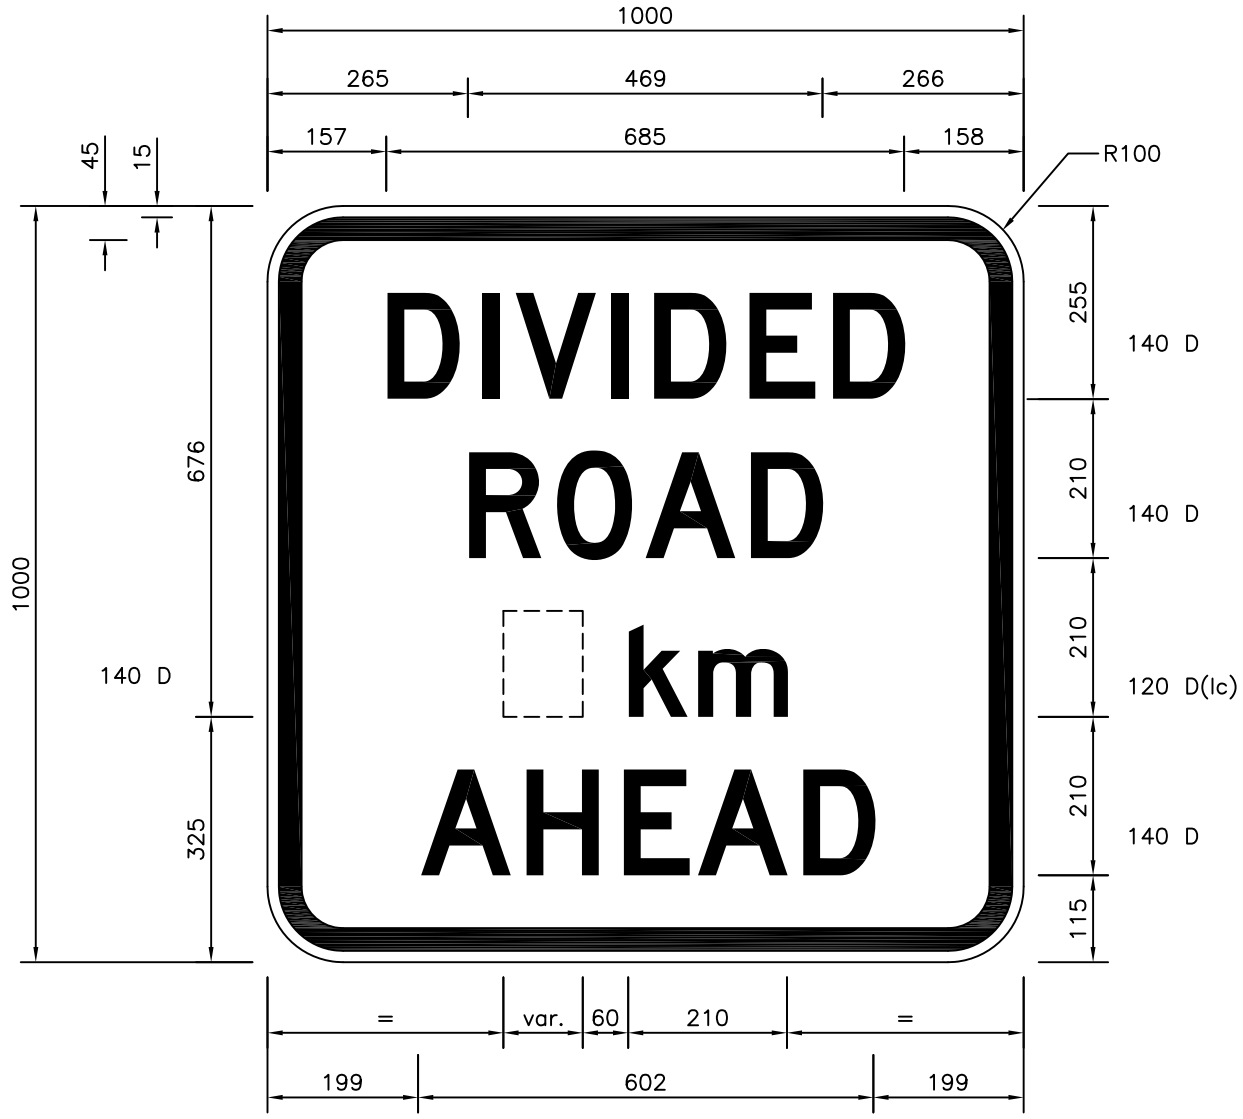


White (retro–reflective)

Black

Note: Letters & Numerals AS1744:2015.

Government of South Australia
Department of Planning, Transport and Infrastructure

GUIDE SIGN
'Divided Road Xkm Ahead'

Technical Services
Safety and Service Division

Authorisation:

Drawn: A. Simister

Scale: 1:10

Date: 13 May, 2015

**G9-SA111**