



CHAPTER 13

PROJECT SIGNS


DRAWING TITLE	DRAWING NO.	REVISION
PROJECT SIGN BOARD FOR LTA PROJECT - TIMBER SIGN BOARD	LTA/SDRE14/13/PSB1	A
PROJECT SIGN BOARD FOR LTA PROJECT - ALUMINIUM SIGN BOARD	LTA/SDRE14/13/PSB2	C
FLYOVER SIGNAGE & BRIDGE INFORMATION SIGN	LTA/SDRE14/13/PSB3	C
PROJECT SIGN BOARD	LTA/SDRE14/13/PSB4	B

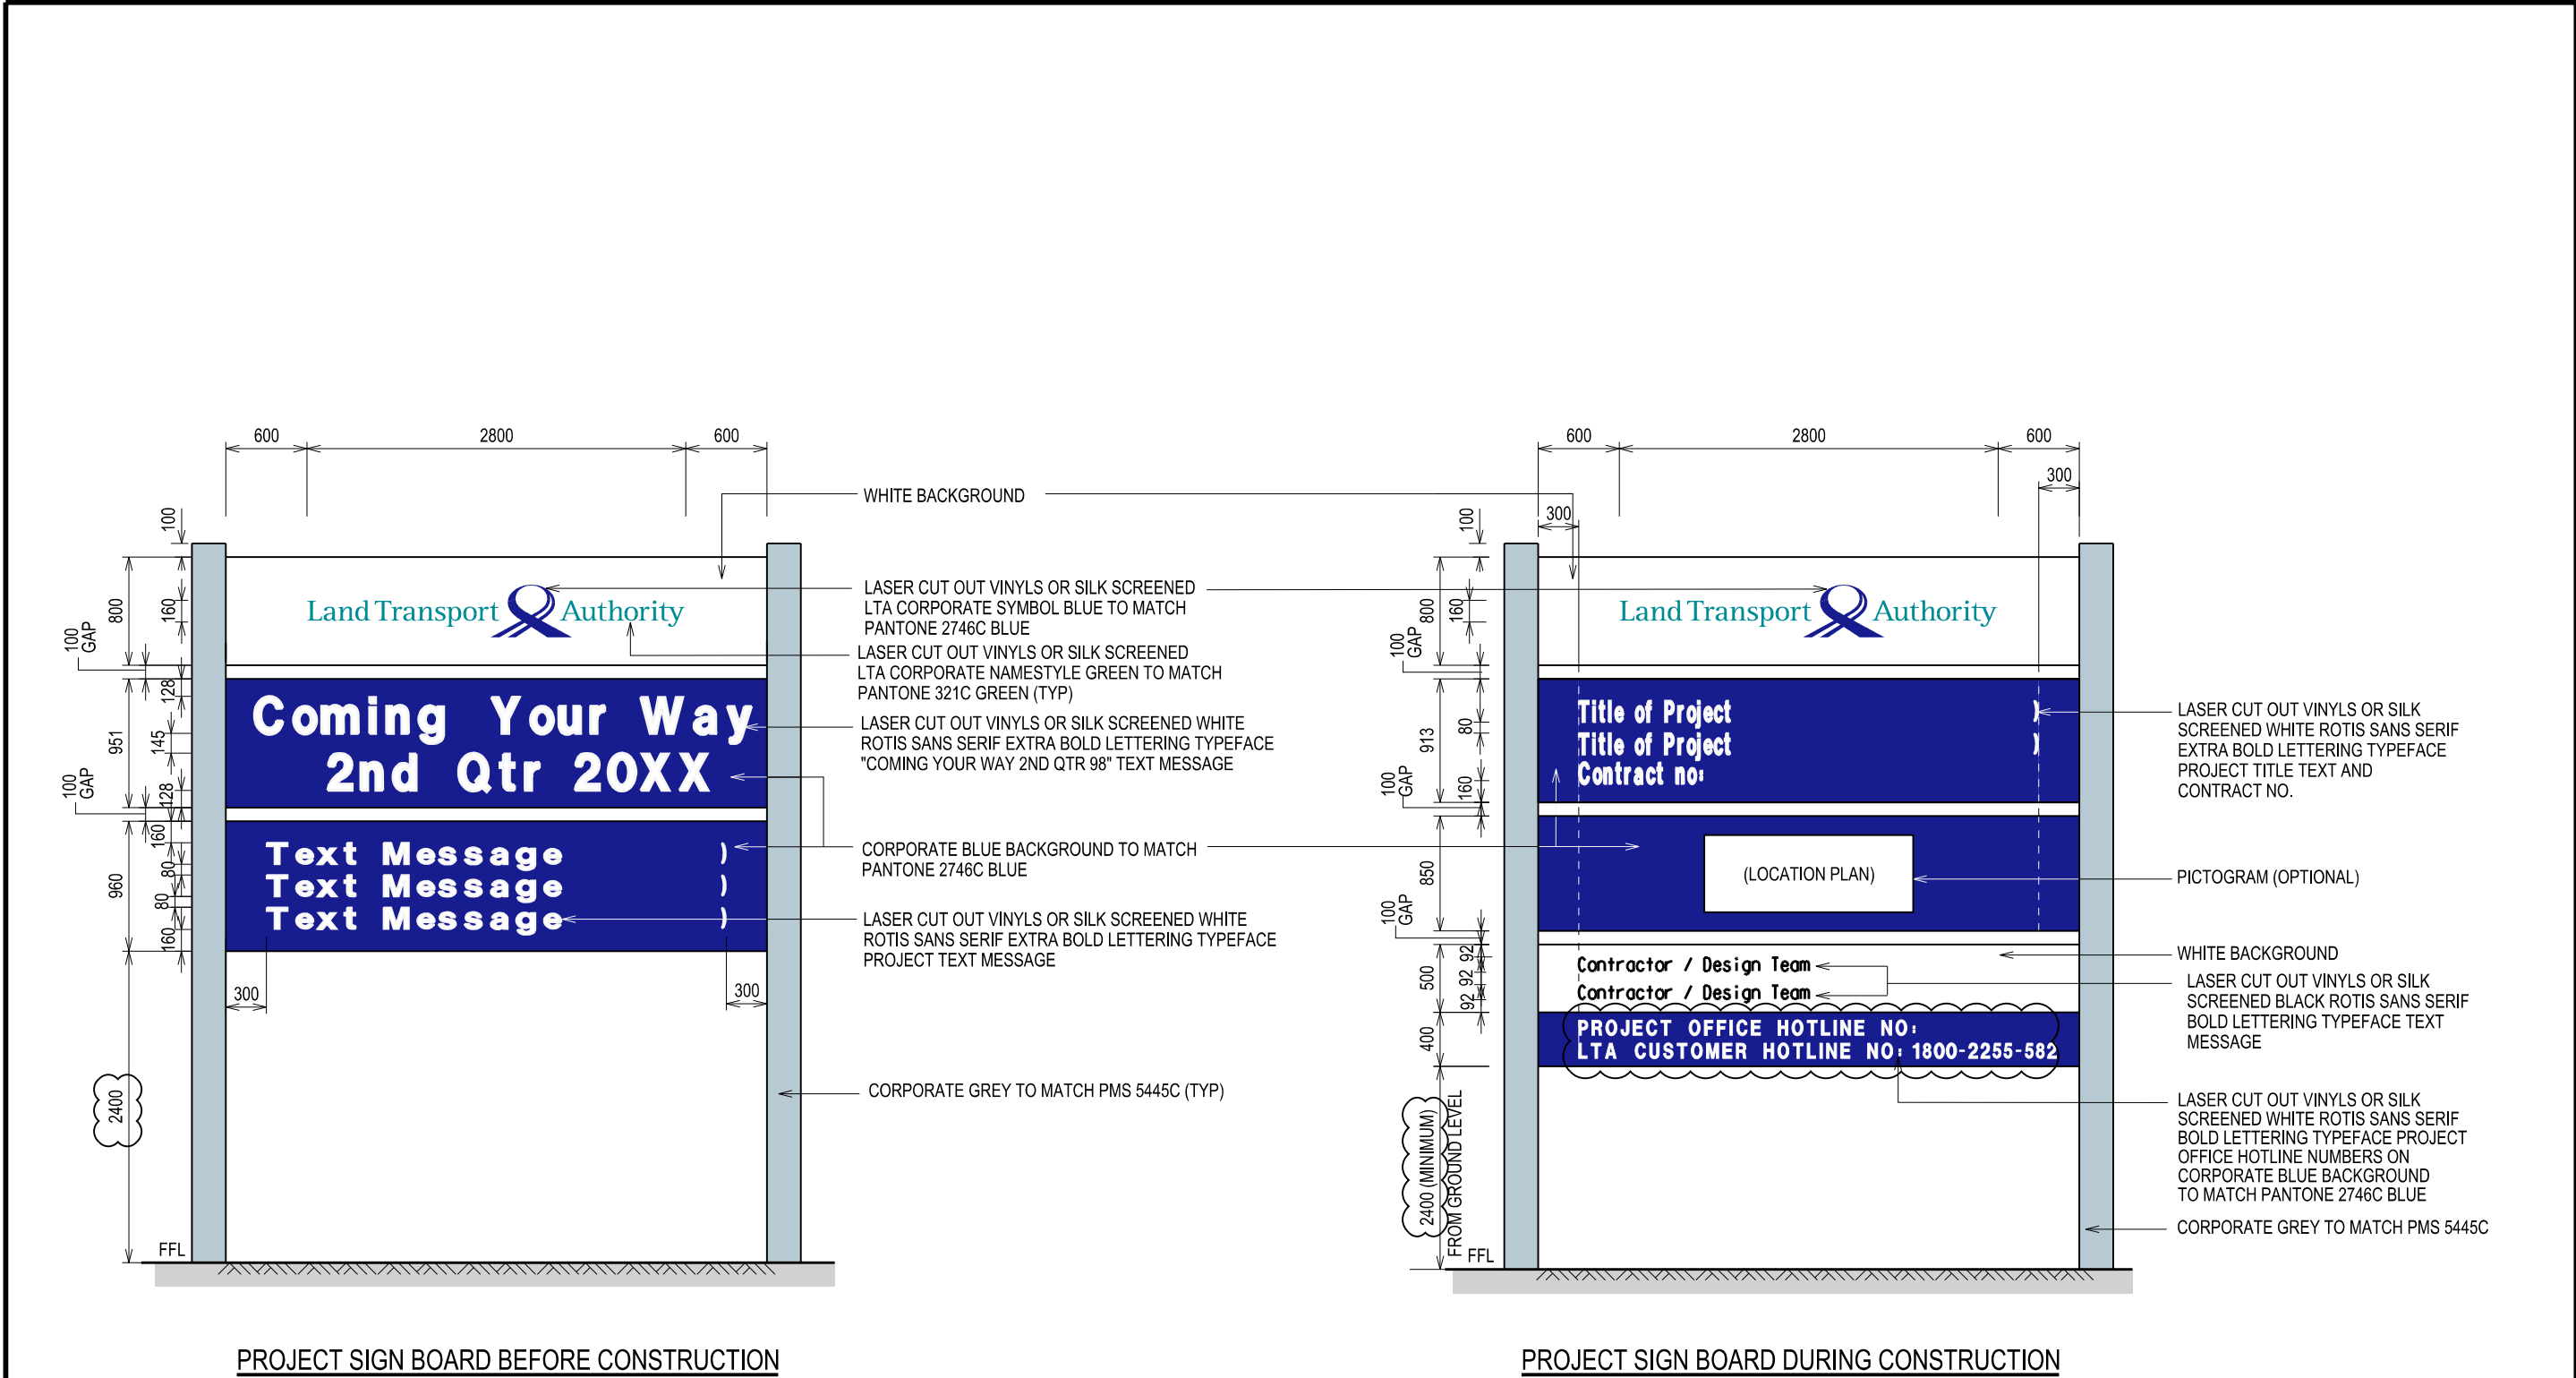


NOTES: 1. Timber sign board shall be used for project period not exceeding two years unless otherwise specified.				STANDARD	DETAIL	Land Transport Authority		
						PROJECT SIGN BOARD FOR LTA PROJECT - TIMBER SIGN BOARD		
A	APR 2019	DRAWING NO.		LTA/SDRE14/13/PSB1		REV.	A	
REV.	DATE	DATE OF ISSUE	SCALE	SHEET NO.				
		1st APR 2014	1:50	1 OF 1				

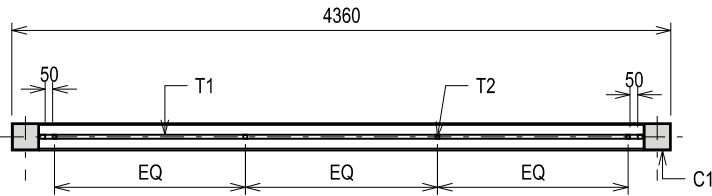


SECTION B-B
SCALE 1:50

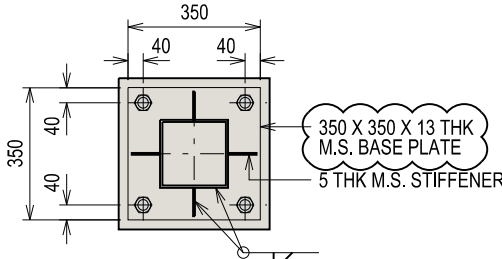


SECTION C-C
SCALE 1:20

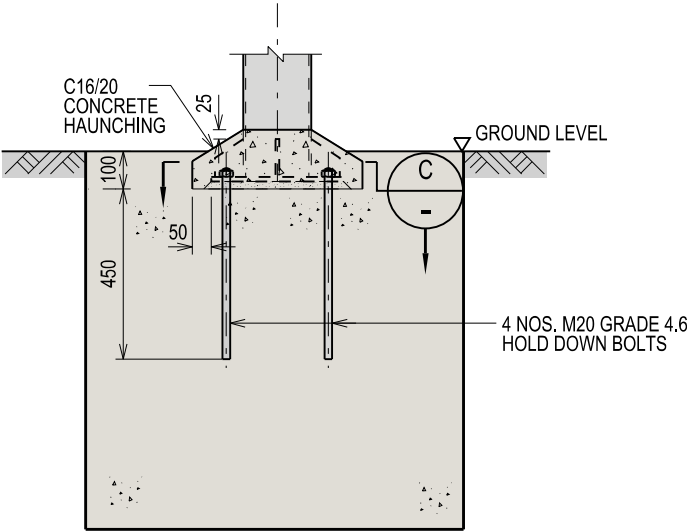


DETAIL 1
TYPICAL BASE PLATE CONNECTION DETAILS
SCALE 1:20

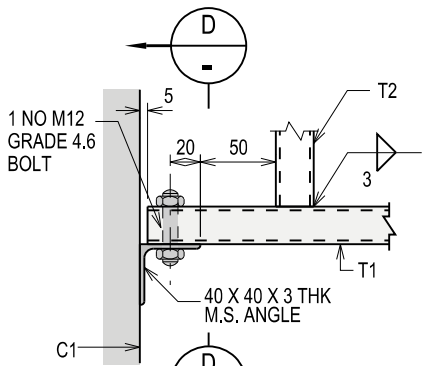


DETAIL 2
SCALE 1:5

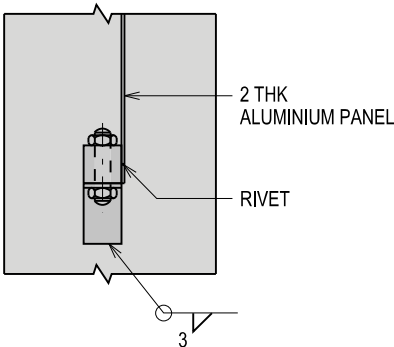


SECTION D-D
SCALE 1:5

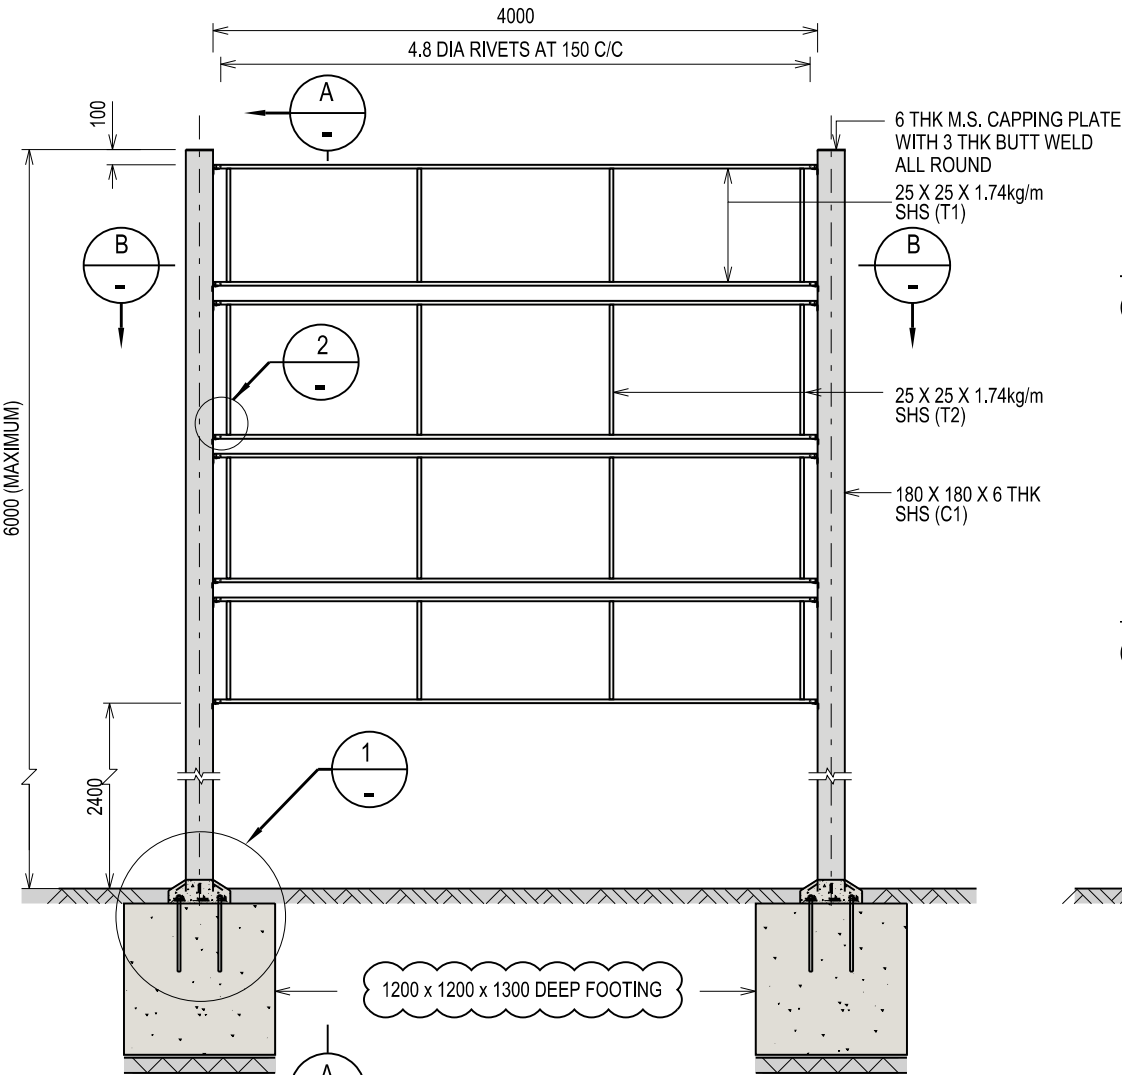


REAR ELEVATION OF PROJECT SIGN BOARD
SCALE 1:50

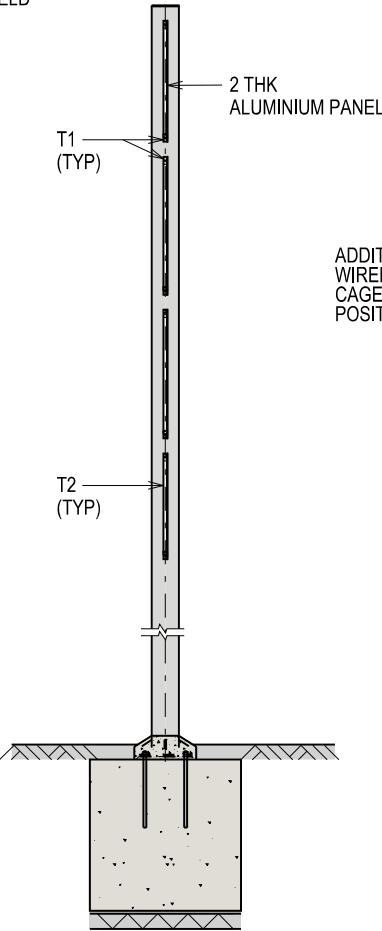

SECTION A-A
SCALE 1:50

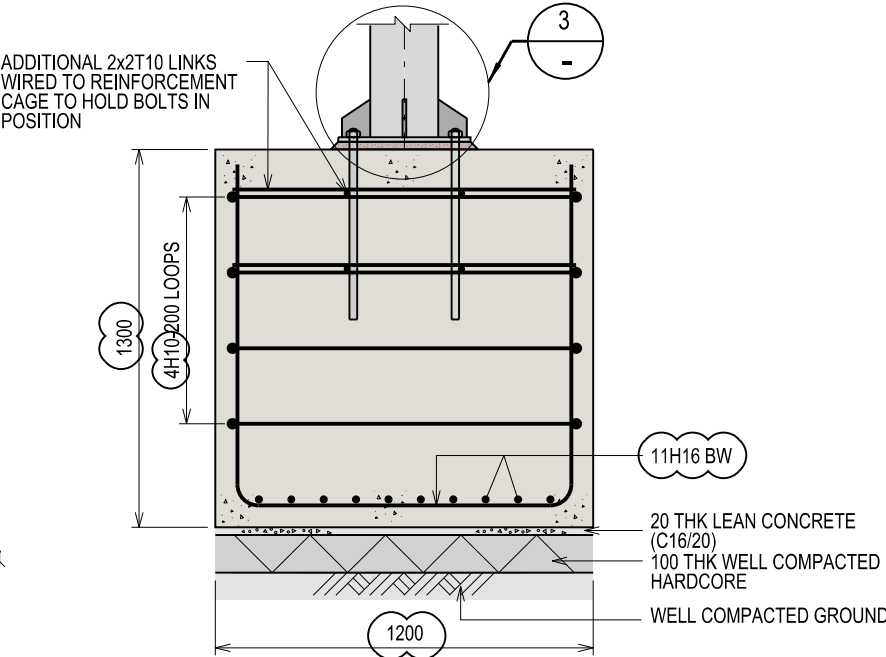

TYPICAL FOOTING DETAILS
SCALE 1:20
(CLEAR COVER TO REINFORCEMENT SHALL BE 50mm)

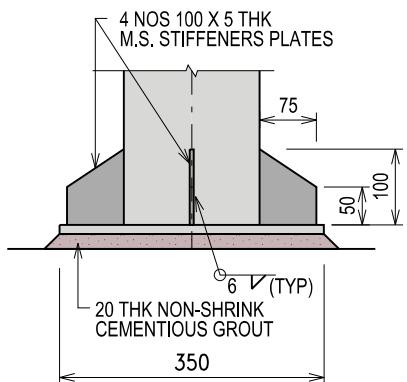

DETAIL 3
5mm THK M.S. STIFFENER DETAILS
SCALE 1:10

ALL STRUCTURAL AND GEOTECHNICAL DETAILS ARE TO BE CHECKED AND ENDORSED BY PROFESSIONAL ENGINEER

- NOTES:
- 1. Minimum soil bearing capacity shall be 75KPa.
 - 2. Soil around footing shall be compacted after backfilling.
 - 3. The concrete shall be C28/35.



C	JUL 2020
B	APR 2019
A	OCT 2015
REV.	DATE

STANDARD DETAIL


PROJECT SIGN BOARD
FOR LTA PROJECT -
ALUMINIUM SIGN BOARD




DRAWING NO. LTA/SDRE14/13/PSB2		REV. C
DATE OF ISSUE 1st APR 2014	SCALE AS SHOWN	SHEET NO. 1 OF 1

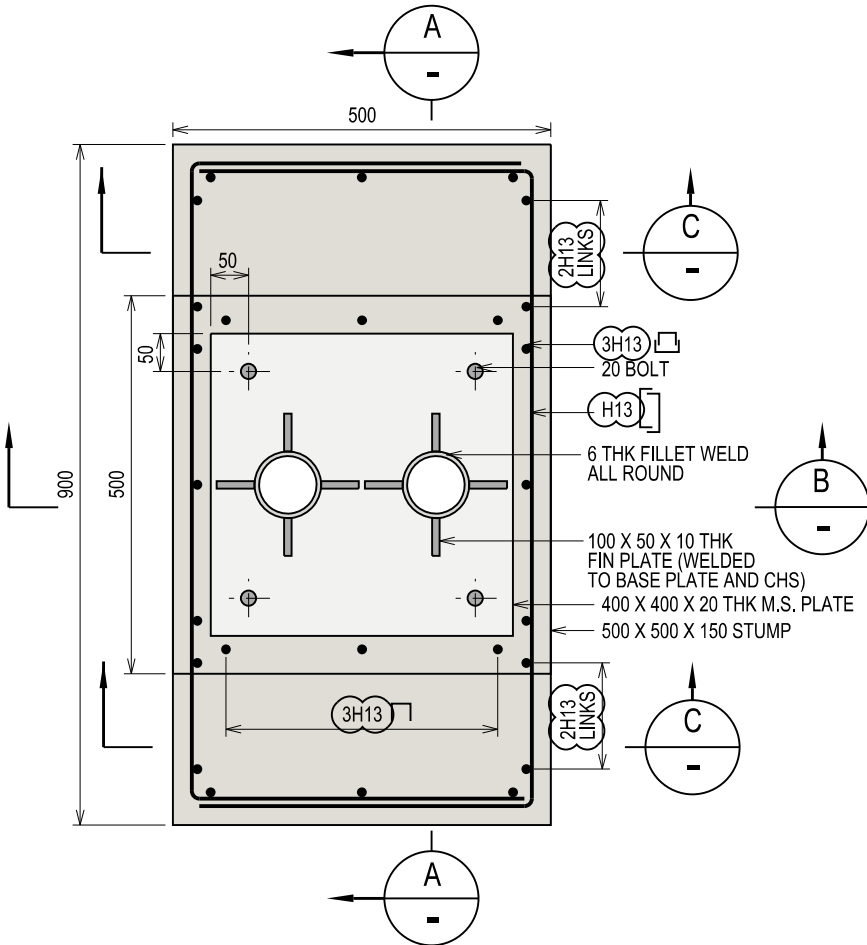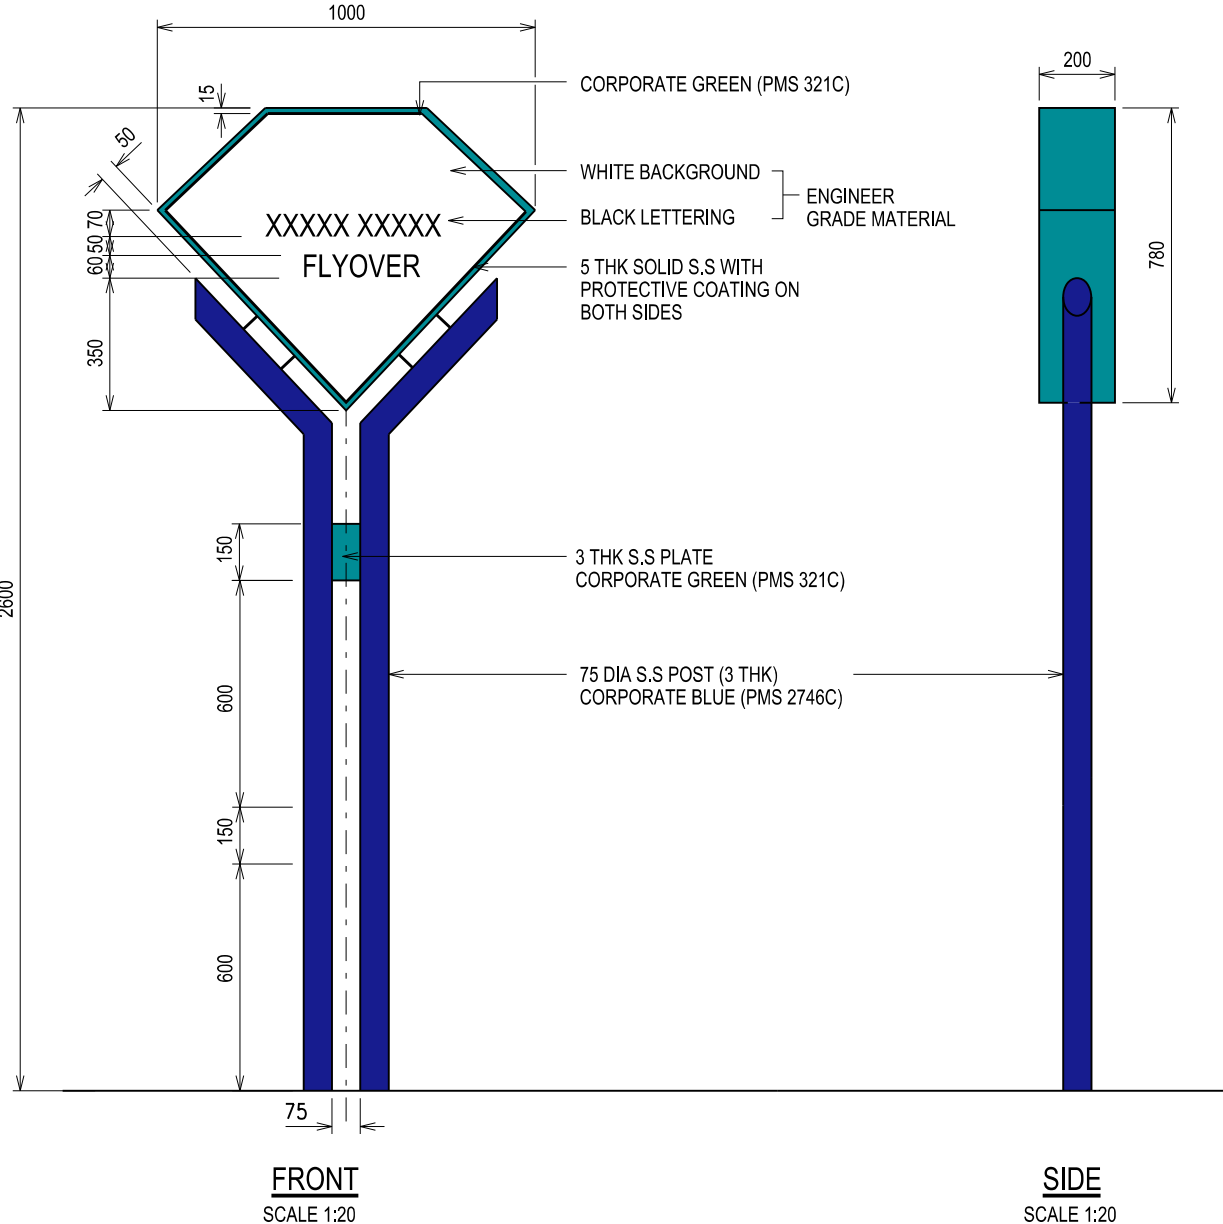


PLAN OF FOUNDATION
(FOOTING SIZE = 900mm(L) x 500mm(B) x 500mm(D))
SCALE 1:10

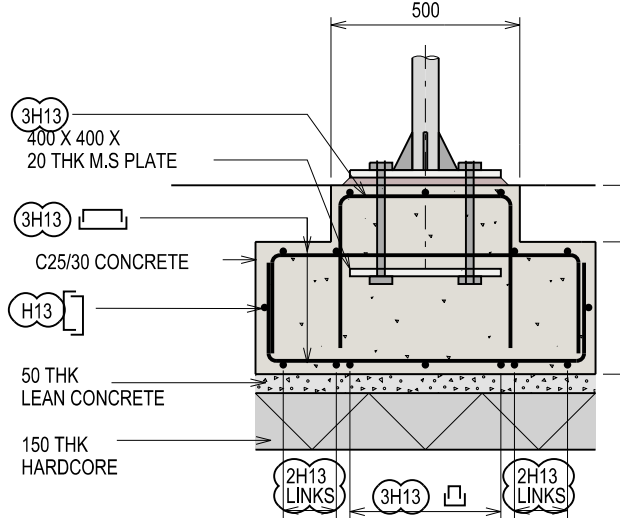


SECTION A-A
SCALE 1:20

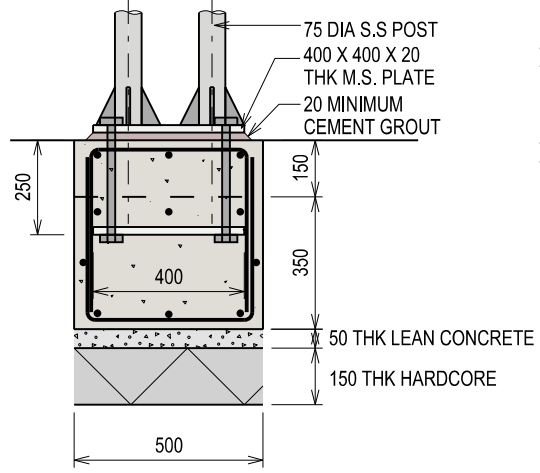

SECTION B-B
SCALE 1:20

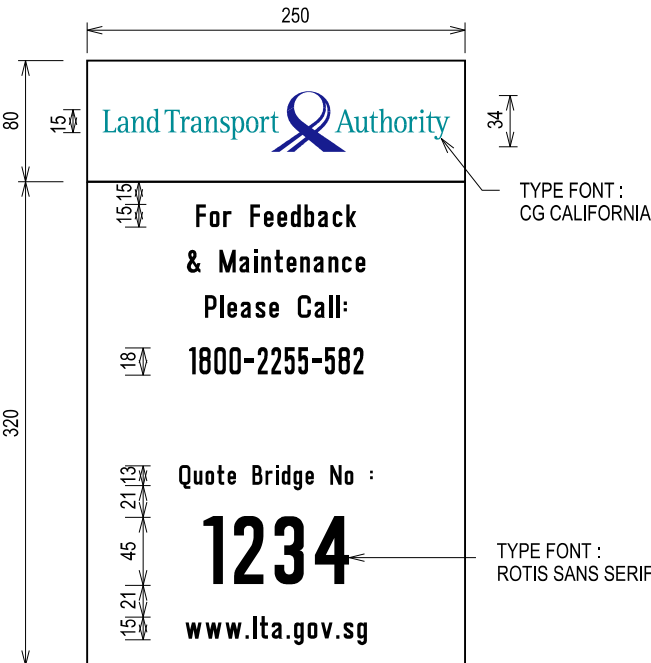


BRIDGE INFORMATION SIGN
SCALE 1:5

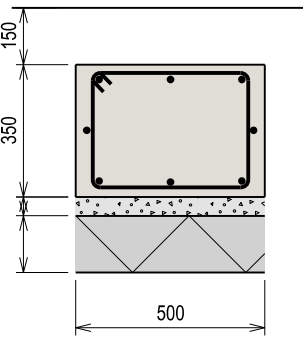

SECTION C-C
SCALE 1:20

STANDARD		DETAIL		Land Transport Authority	
C		JUL 2020		DRAWING NO. LTA/SDRE14/13/PSB3	
B		APR 2019		REV. C	
A		OCT 2015		DATE OF ISSUE 1st APR 2014	
REV.		DATE		SCALE AS SHOWN	
				SHEET NO. 1 OF 1	

FLYOVER SIGNAGE & BRIDGE INFORMATION SIGN

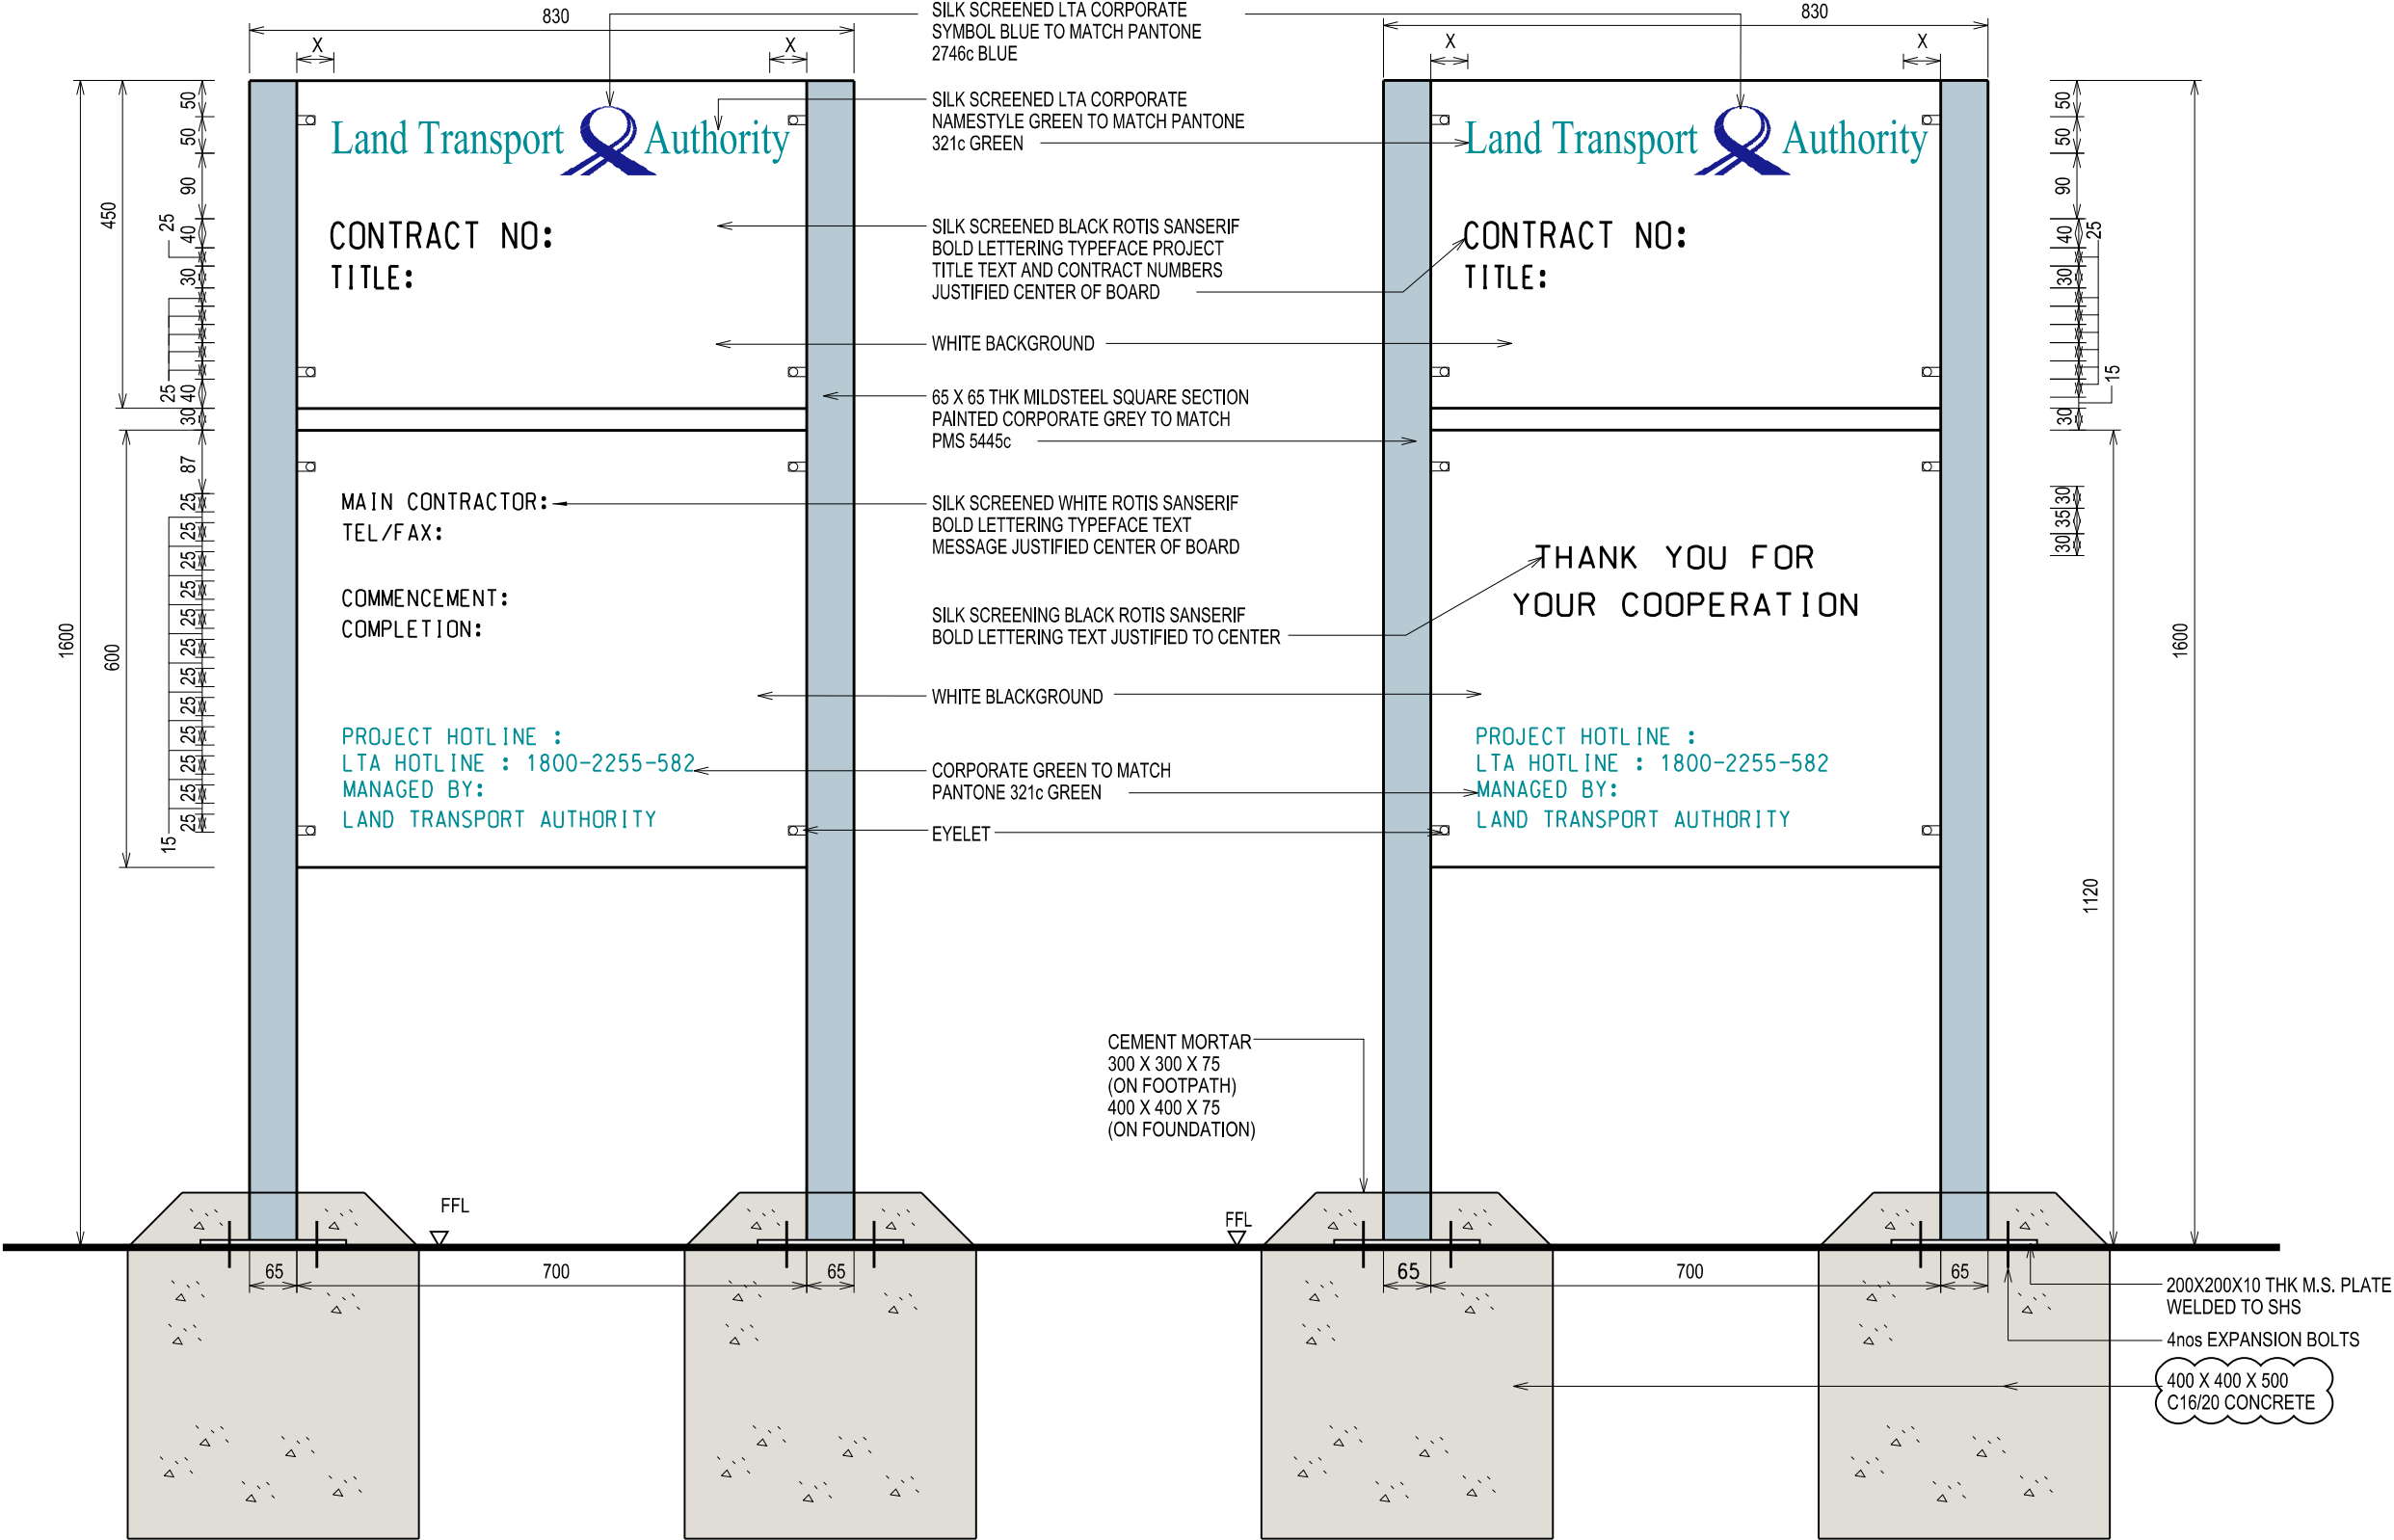

FRONT ELEVATION OF PROJECT SIGNBOARD
SCALE 1:10

REAR ELEVATION OF PROJECT SIGNBOARD
SCALE 1:10

	</
--	--	----