


CHAPTER 16


TRAFFIC PROHIBITORY SIGNS

| DRAWING TITLE                            | DRAWING NO.        | REVISION |
|------------------------------------------|--------------------|----------|
| TRAFFIC PROHIBITORY SIGNS (SHEET 1 OF 6) | LTA/SDRE14/16/TFP1 | -        |
| TRAFFIC PROHIBITORY SIGNS (SHEET 2 OF 6) | LTA/SDRE14/16/TFP2 | -        |
| TRAFFIC PROHIBITORY SIGNS (SHEET 3 OF 6) | LTA/SDRE14/16/TFP3 | A        |
| TRAFFIC PROHIBITORY SIGNS (SHEET 4 OF 6) | LTA/SDRE14/16/TFP4 | -        |
| TRAFFIC PROHIBITORY SIGNS (SHEET 5 OF 6) | LTA/SDRE14/16/TFP5 | -        |
| TRAFFIC PROHIBITORY SIGNS (SHEET 6 OF 6) | LTA/SDRE14/16/TFP6 | -        |

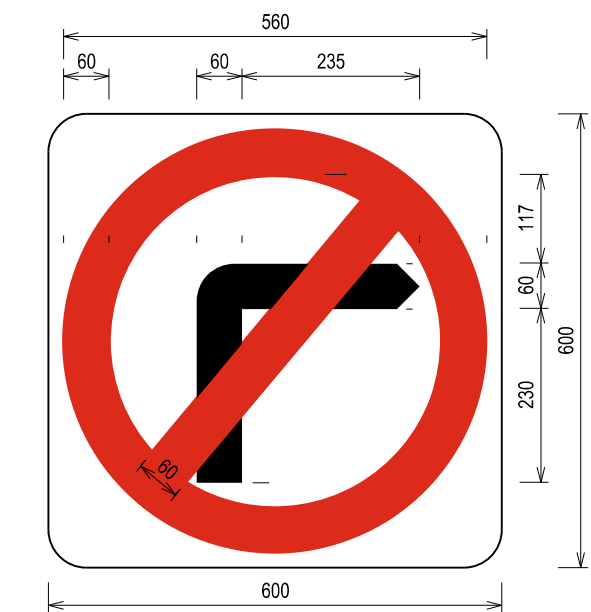


**NO RIGHT TURN**

THIS SIGN PROHIBITS VEHICLES FROM TURNING RIGHT. THIS SIGN MAY BE USED WITH TRAFFIC SIGNALS AND THE PROHIBITION MAY BE QUALIFIED WITH A SUPPLEMENTARY PLATE.

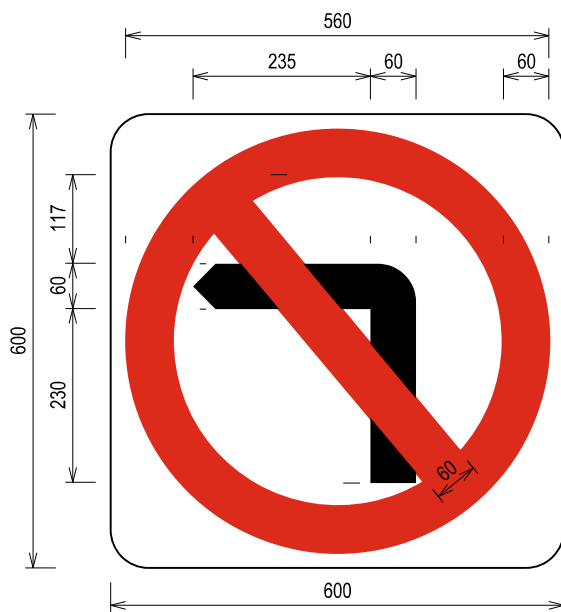


**NO LEFT TURN**

THIS SIGN PROHIBITS VEHICLES FROM TURNING LEFT. THIS SIGN MAY BE USED WITH TRAFFIC SIGNALS AND THE PROHIBITION MAY BE QUALIFIED WITH A SUPPLEMENTARY PLATE.

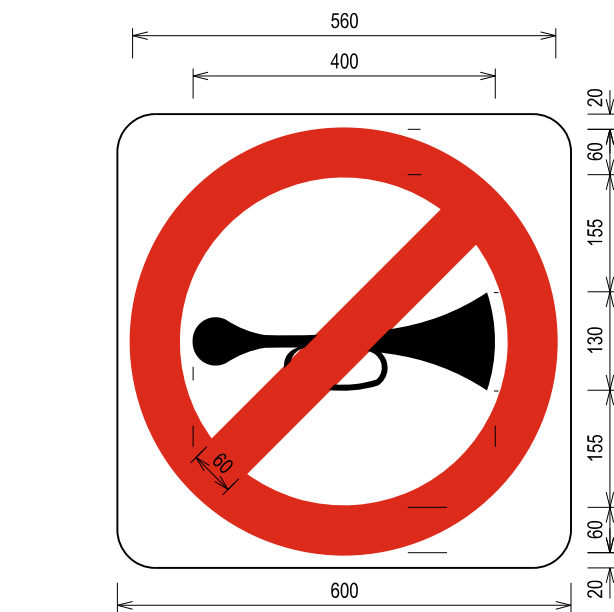


**NO HORNING**

THIS SIGN PROHIBITS THE USE OF AUDIBLE DEVICES EXCEPT TO AVOID ACCIDENTS.

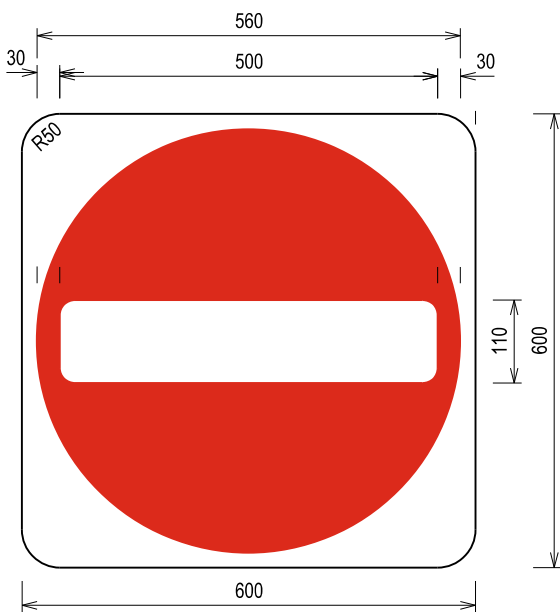


**NO ENTRY**

THE SIGN INDICATES THAT VEHICLES ARE NOT PERMITTED TO ENTER UNLESS INDICATED OTHERWISE BY A SUPPLEMENTARY PLATE.

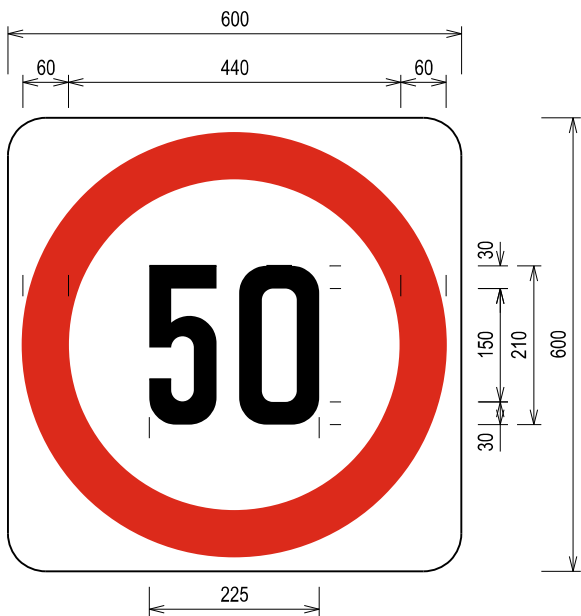


**MAXIMUM SPEED LIMIT**

THIS SIGN INDICATES THAT A SPEED LIMIT OF 50 km/h IS IMPOSED ON THE RESTRICTED SECTION OF THE ROAD. THE NUMERALS IN THIS SIGN MAY BE ALTERED TO CATER FOR DIFFERENT SPEED LIMITATIONS.

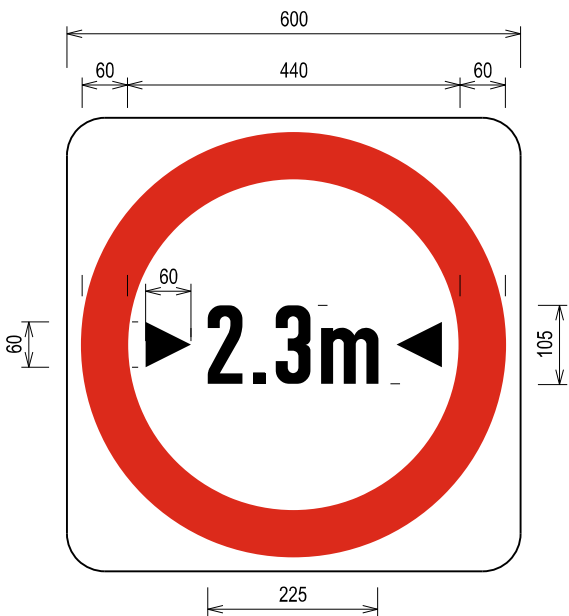

**WIDTH LIMIT**


THIS SIGN INDICATES THAT VEHICLES WIDER THAN 2.3m ARE PROHIBITED TO PROCEED. THE NUMERALS IN THIS SIGN MAY BE ALTERED TO CATER FOR DIFFERENT WIDTH RESTRICTIONS.

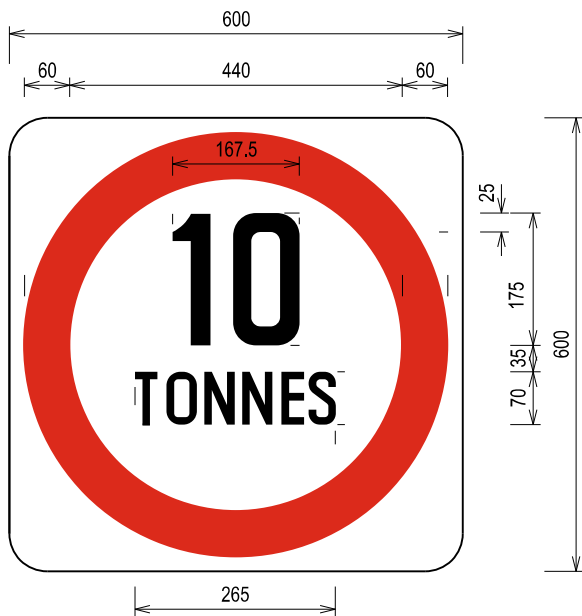

**WEIGHT LIMIT**


THIS SIGN INDICATES THAT VEHICLES WITH A LADEN OR UNLADEN WEIGHT IN EXCESS OF 10 TONNES ARE PROHIBITED TO PROCEED. THE NUMERALS IN THIS SIGN MAY BE ALTERED TO CATER FOR DIFFERENT WEIGHT RESTRICTIONS.

| |
|---|
| |</ |
|---|

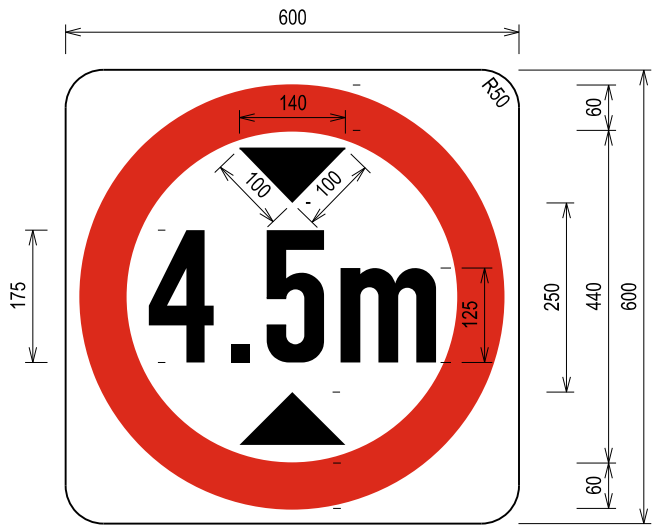


HEIGHT LIMIT

THIS SIGN INDICATES THAT VEHICLES HAVING AN OVERALL HEIGHT GREATER THAN 4.5m SHALL BE PROHIBITED FROM PROCEEDING.

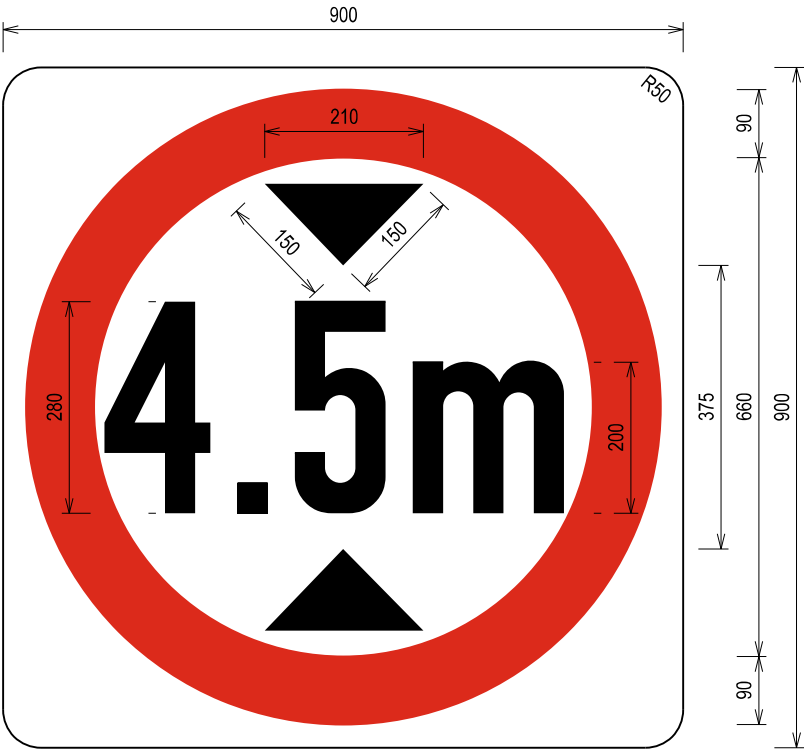


HEIGHT LIMIT  
(FOR EXPRESSWAY ONLY)

THIS SIGN INDICATES THAT VEHICLES HAVING AN OVERALL HEIGHT GREATER THAN 4.5 METRES SHALL BE PROHIBITED FROM PROCEEDING.

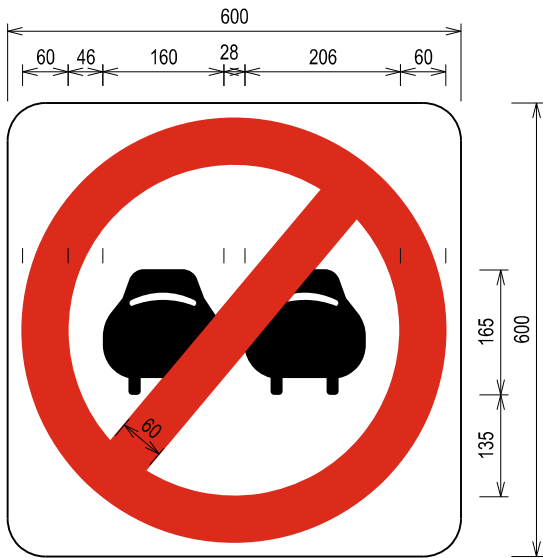

NO OVERTAKING



THIS SIGN PROHIBITS THE OVERTAKING OF VEHICLES. IT MAY BE USED WITH A SUPPLEMENTARY PLATE TO INDICATE THE END OF THE "NO OVERTAKING" ZONE OR TO INDICATE THE LENGTH OF ROAD OVER WHICH THE PROHIBITION APPLIES.

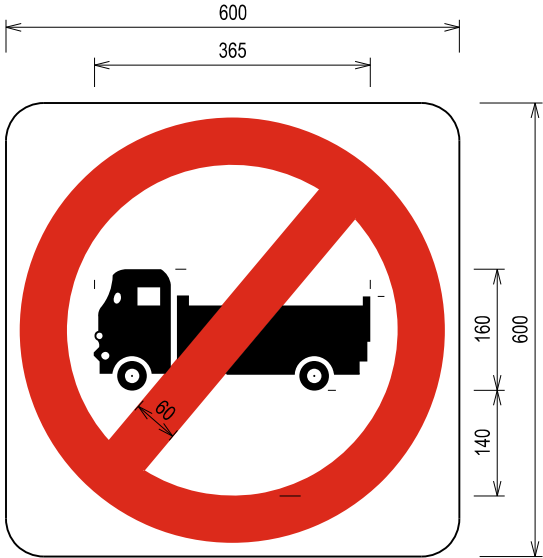


LORRY RESTRICTION

THIS SIGN PROHIBITS THE ENTRY OF ALL GOODS VEHICLES. THIS SIGN MAY BE USED WITH SUPPLEMENTARY PLATES FOR EXAMPLE, "EXCEEDING 2500 KILOGRAMS IN UNLADEN WEIGHT".

| |
|---|
| |</ |
|---|

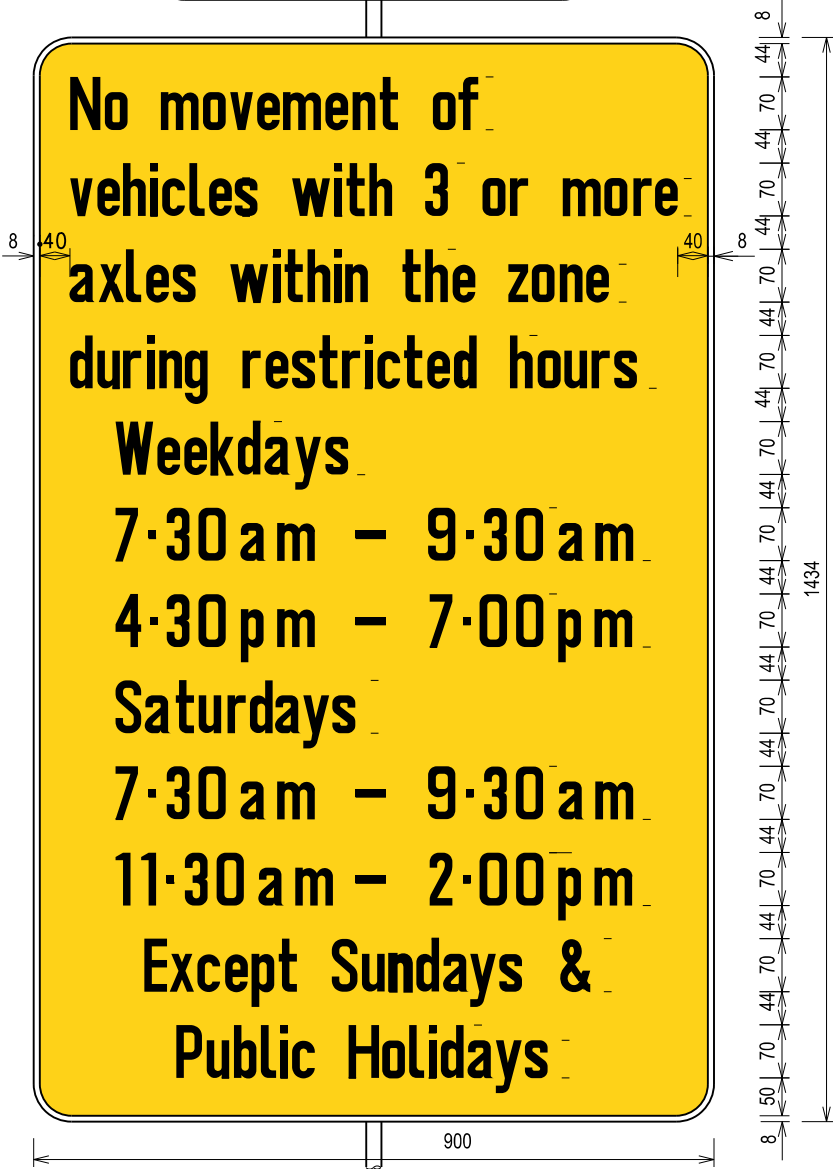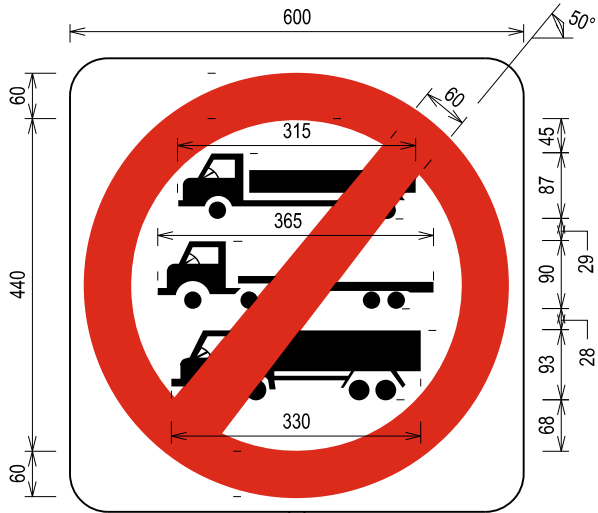


RESTRICTION OF MOVEMENT OF VEHICLES WITH 3 OR MORE AXLES.

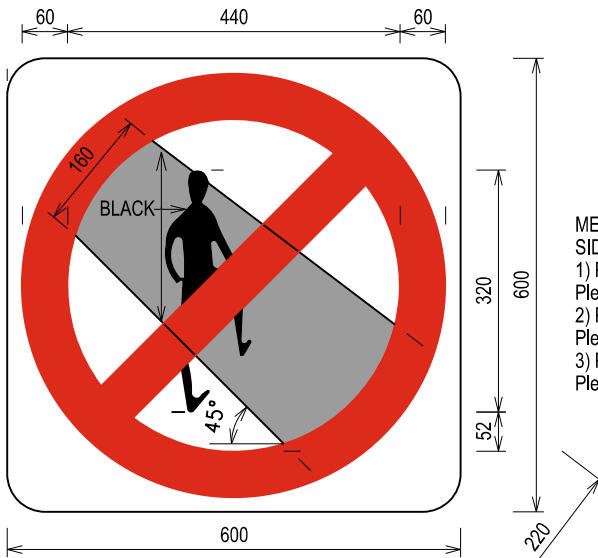

MESSAGE (BLACK) ON REVERSED SIDE (WHITE) :  
1) PEDESTRIANS  
Please Use Crossing  
2) PEDESTRIANS  
Please Use Underpass  
3) PEDESTRIANS  
Please Use Overpass


PEDESTRIAN CROSSING PROHIBITION

THIS SIGN INDICATES THAT PEDESTRIANS SHALL NOT CROSS THE ROAD EXCEPT AT THE PROVIDED PEDESTRIAN CROSSING(S). IT MAY BE USED WITH SUPPLEMENTARY PLATES TO INDICATE THE DIRECTION OR DIRECTIONS IN WHICH THE PROHIBITION APPLIES.

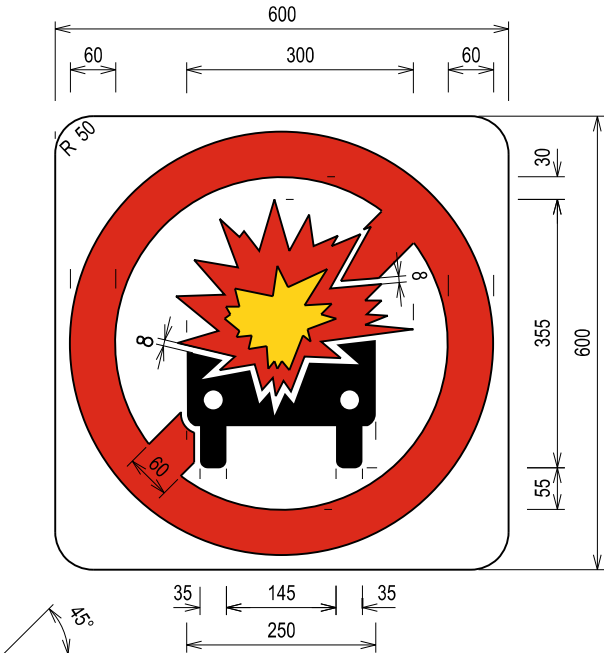


HAZARDOUS LOADS PROHIBITION

THIS SIGN PROHIBITS THE ENTRY OF VEHICLES TRANSPORTING HAZARDOUS LOADS.

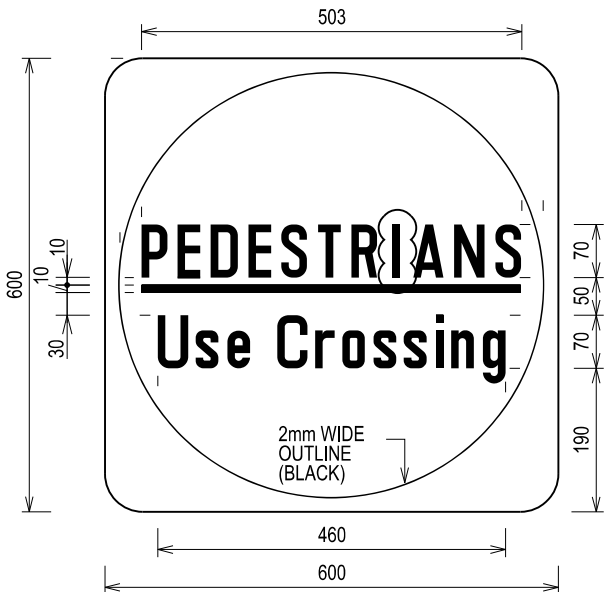


PEDESTRIAN CROSSING PROHIBITION (MESSAGE ON REVERSED SIDE)


| |
|---|
| |</ |
|---|

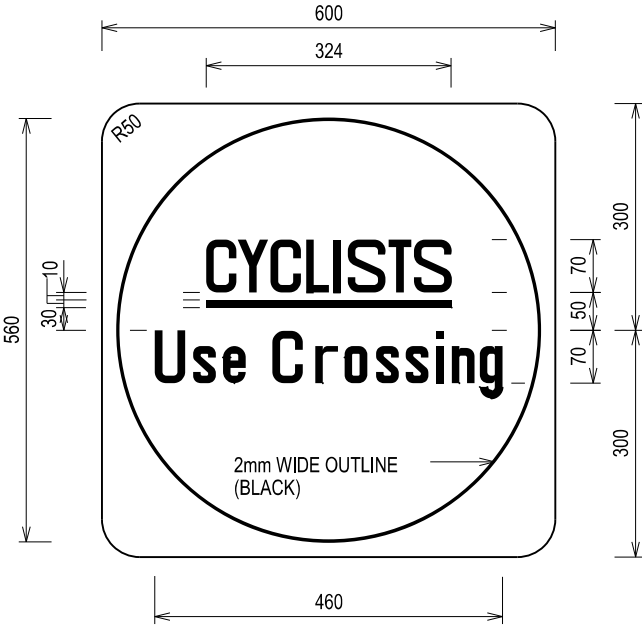


CYCLIST CROSSING PROHIBITION  
(MESSAGE ON REVERSED SIDE)

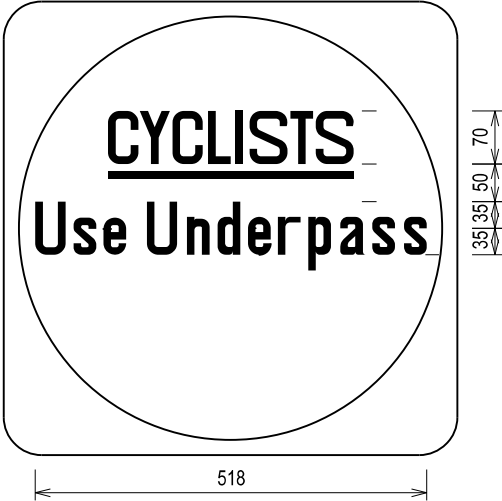


CYCLIST CROSSING PROHIBITION  
(MESSAGE ON REVERSED SIDE)

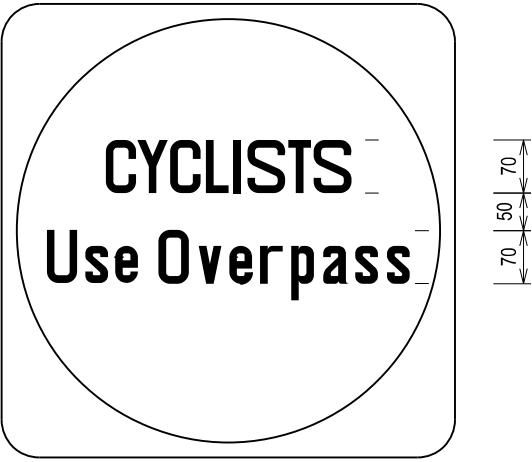

CYCLIST CROSSING PROHIBITION  
(MESSAGE ON REVERSED SIDE)

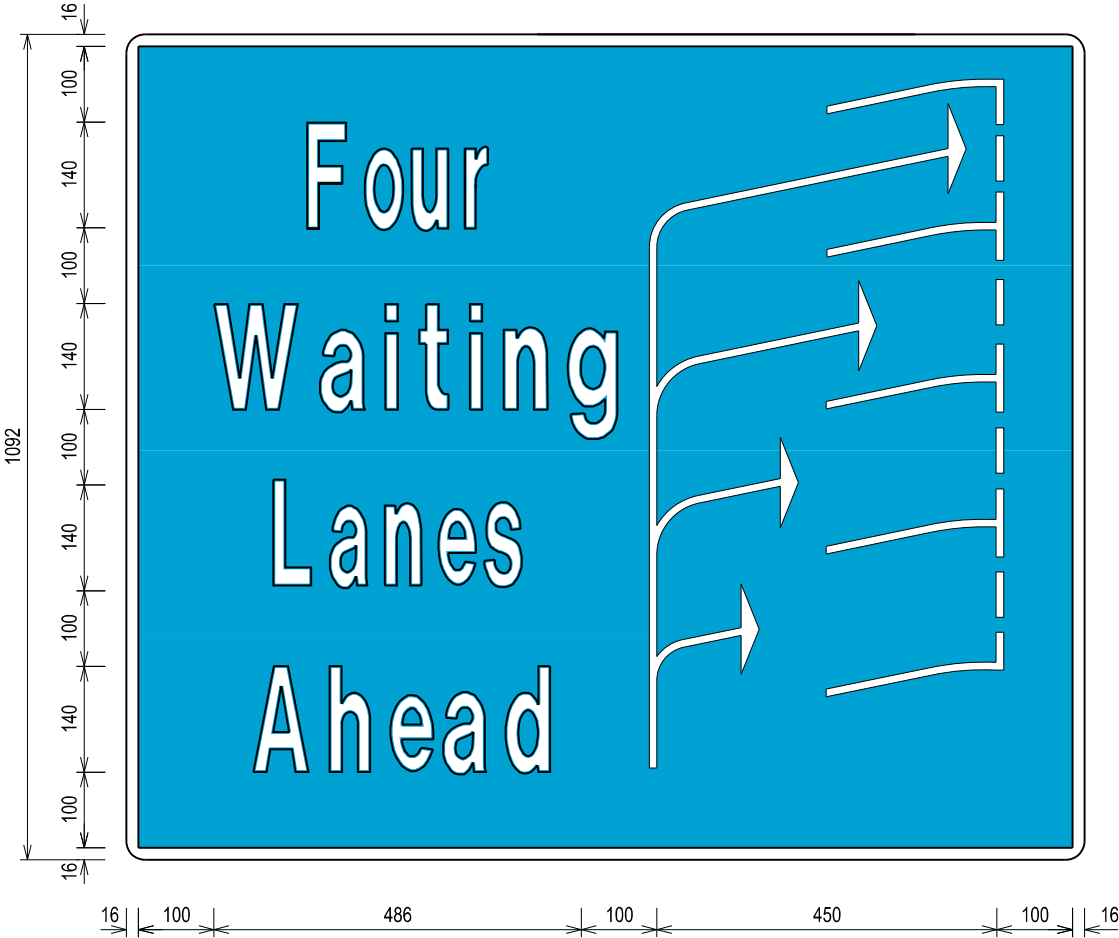


|      |      |                                             |        |                                |            |                  |
|------|------|---------------------------------------------|--------|--------------------------------|------------|------------------|
| REV. | DATE | STANDARD                                    | DETAIL | Land Transport Authority       |            |                  |
|      |      | TRAFFIC PROHIBITORY SIGNS<br>(SHEET 4 OF 6) |        | DRAWING NO. LTA/SDRE14/16/TFP4 |            | REV. -           |
|      |      |                                             |        | DATE OF ISSUE 1st APR 2014     | SCALE 1:10 | SHEET NO. 4 OF 6 |
|      |      |                                             |        |                                |            |                  |

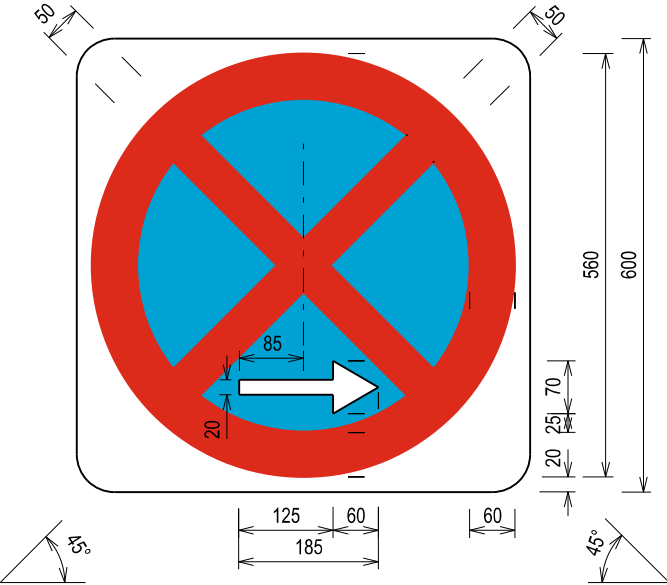


NO STOPPING

THIS SIGN PROHIBITS STOPPING BY VEHICLES UNLESS THE VEHICLES IS PREVENTED FROM PROCEEDING DUE TO TRAFFIC CONDITIONS. THIS SIGN SHALL BE SO PLACED THAT THEIR DISTANCE IS AT 60° TO THE KERB LINE. IT MAY BE USED IN CONJUNCTION WITH SUPPLEMENTARY PLATES TO INDICATE TIME DURATION AND THE CATEGORY OF VEHICLES BEING PROHIBITED.

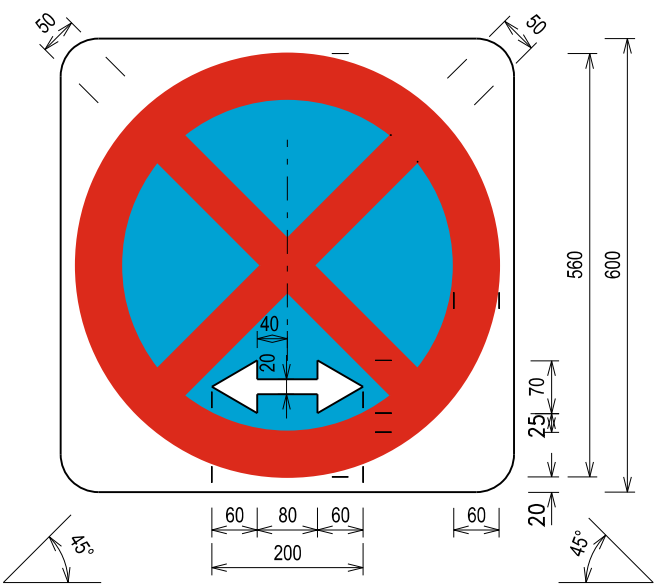


NO STOPPING

THIS SIGN PROHIBITS STOPPING BY VEHICLES WITH DIRECTIONS IN WHICH THE PROHIBITION APPLIES.

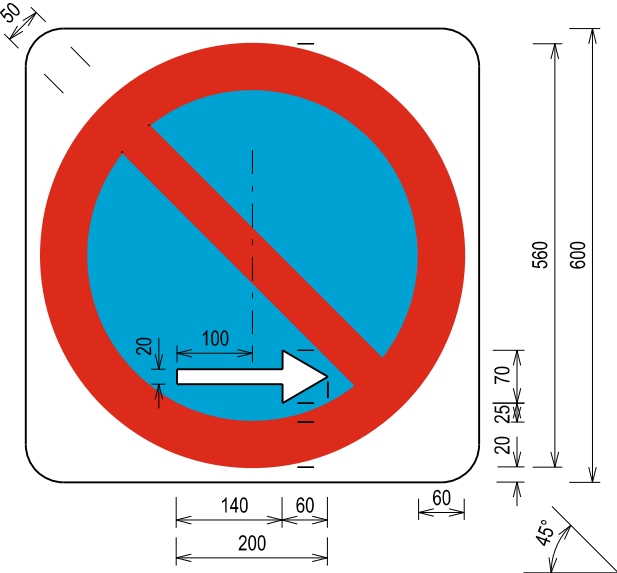

NO WAITING

THIS SIGN PROHIBITS WAITING BY VEHICLES. THIS SIGN SHALL BE PLACED SUCH THAT THEIR DISTANCE IS 60° TO THE KERB LINE. TO INDICATE TIME DURATION AND THE CATEGORY OF VEHICLES PROHIBITED.

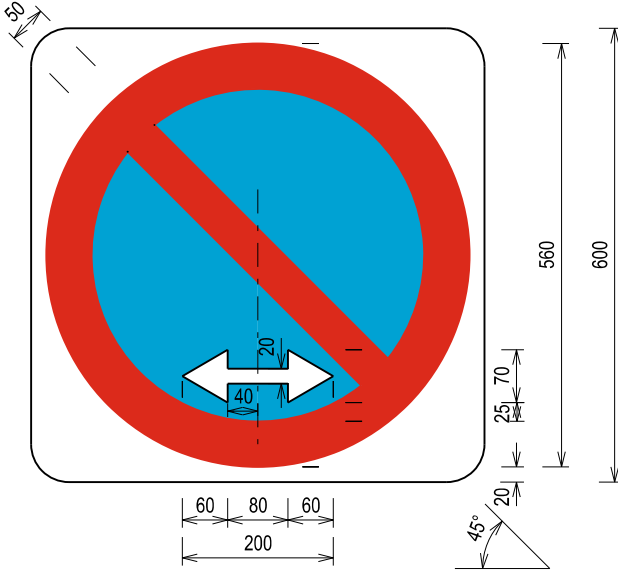


NO WAITING


THIS SIGN PROHIBITS WAITING BY VEHICLES. THIS SIGN SHALL BE PLACED SUCH THAT THEIR PLATE IS PERPENDICULAR OR NEARLY PERPENDICULAR TO THE ROAD.

| |
|---|
| |</ |
|---|



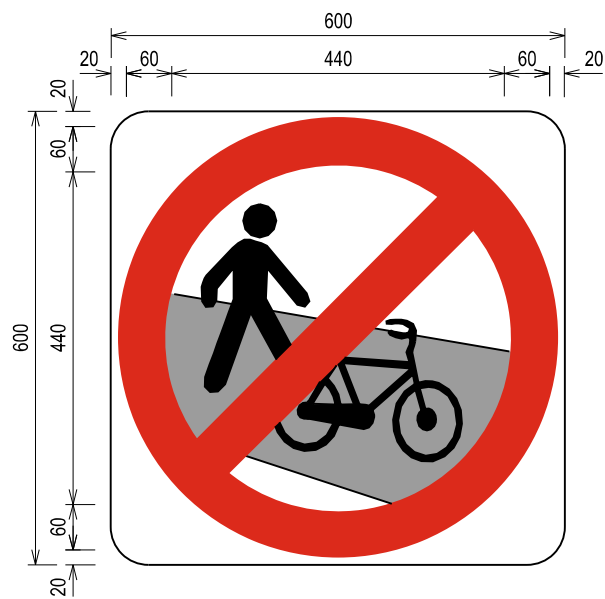


**PEDESTRIAN & CYCLISTS CROSSING PROHIBITION SIGN**  
BLACK PICTOGRAMS, RED CIRCLE & BAR AND GREY ROAD ON WHITE BACKGROUND

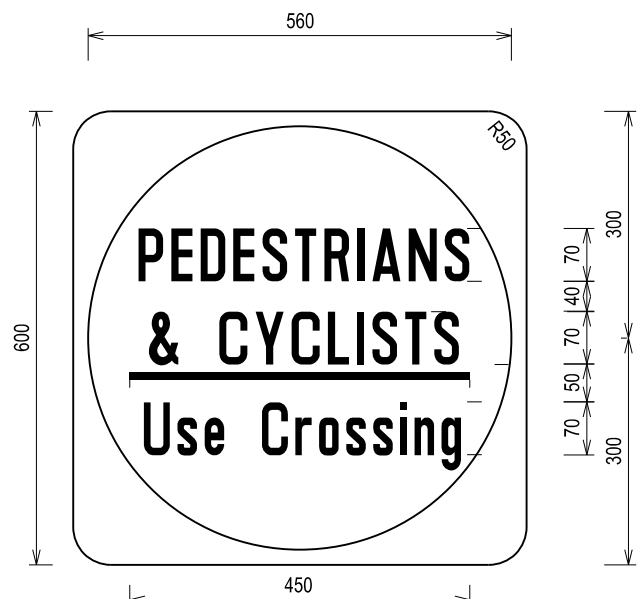


**CYCLIST CROSSING PROHIBITION**  
(MESSAGE ON REVERSED SIDE)



**SIGN INDICATING FIFTY METRES (50m) LIMIT OF A BICYCLE CROSSING**  
BLACK PICTOGRAMS, RED CIRCLE & BAR AND GREY ROAD ON WHITE BACKGROUND

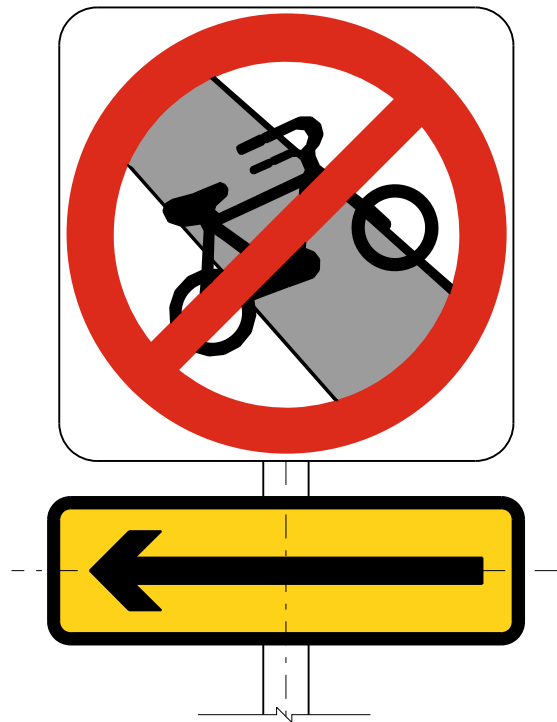

**CYCLIST CROSSING PROHIBITION**  
SIGN INDICATING FIFTY METRES (50m)

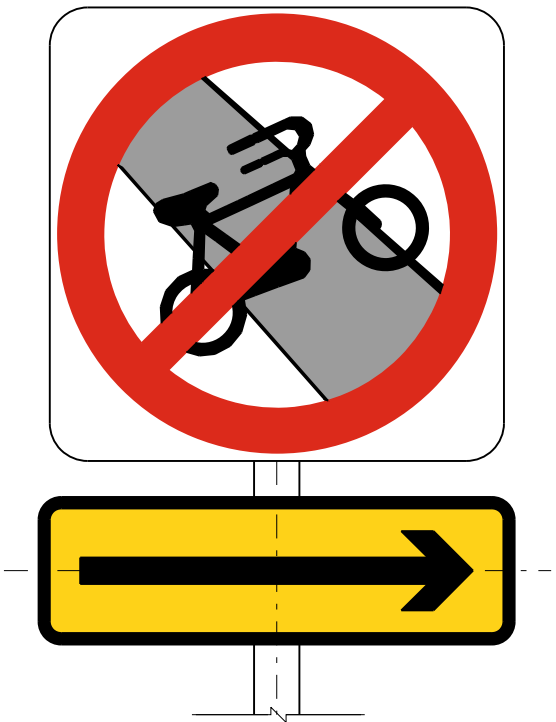

**CYCLIST CROSSING PROHIBITION**  
SIGN INDICATING FIFTY METRES (50m)

|                           |      |                |  |                          |           |
|---------------------------|------|----------------|--|--------------------------|-----------|
| STANDARD                  |      | DETAIL         |  | Land Transport Authority |           |
| TRAFFIC PROHIBITORY SIGNS |      | (SHEET 6 OF 6) |  | DRAWING NO.              | REV.      |
|                           |      |                |  | LTA/SDRE14/16/TFP6       | -         |
|                           |      |                |  | DATE OF ISSUE            | SHEET NO. |
|                           |      |                |  | 1st APR 2014             | 6 OF 6    |
|                           |      |                |  | SCALE                    |           |
|                           |      |                |  | 1:10                     |           |
| REV.                      | DATE |                |  |                          |           |