


CHAPTER 17


TRAFFIC WARNING SIGNS

DRAWING TITLE	DRAWING NO.	REVISION
TRAFFIC WARNING SIGNS (SHEET 1 OF 9)	LTA/SDRE14/17/TFW1	-
TRAFFIC WARNING SIGNS (SHEET 2 OF 9)	LTA/SDRE14/17/TFW2	-
TRAFFIC WARNING SIGNS (SHEET 3 OF 9)	LTA/SDRE14/17/TFW3	-
TRAFFIC WARNING SIGNS (SHEET 4 OF 9)	LTA/SDRE14/17/TFW4	-
TRAFFIC WARNING SIGNS (SHEET 5 OF 9)	LTA/SDRE14/17/TFW5	-
TRAFFIC WARNING SIGNS (SHEET 6 OF 9)	LTA/SDRE14/17/TFW6	A
TRAFFIC WARNING SIGNS (SHEET 7 OF 9)	LTA/SDRE14/17/TFW7	-
TRAFFIC WARNING SIGNS (SHEET 8 OF 9)	LTA/SDRE14/17/TFW8	-
TRAFFIC WARNING SIGNS (SHEET 9 OF 9)	LTA/SDRE14/17/TFW9	-

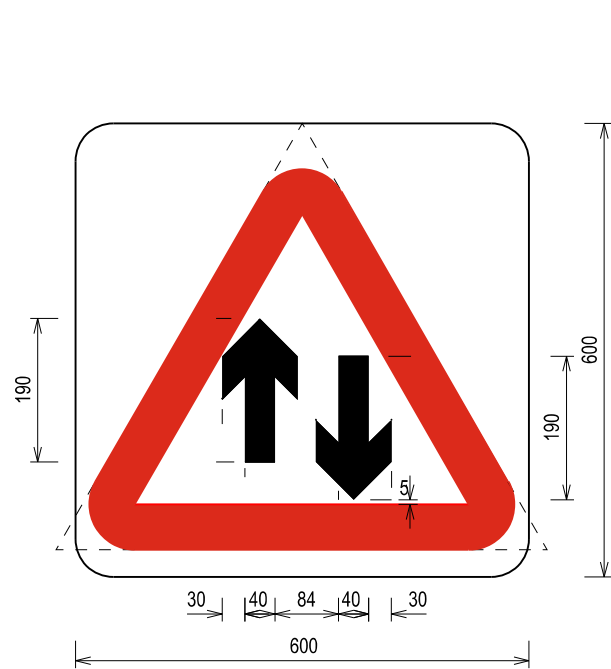


TWO WAY TRAFFIC AHEAD

THIS SIGN INDICATES THAT MOTORISTS ARE APPROACHING A SECTION OF THE ROAD WHICH IS TWO-WAY IN CONTRAST TO THE CURRENT SECTION WHICH IS ONE-WAY. IT MAY BE USED WITH A SUPPLEMENTARY PLATE.

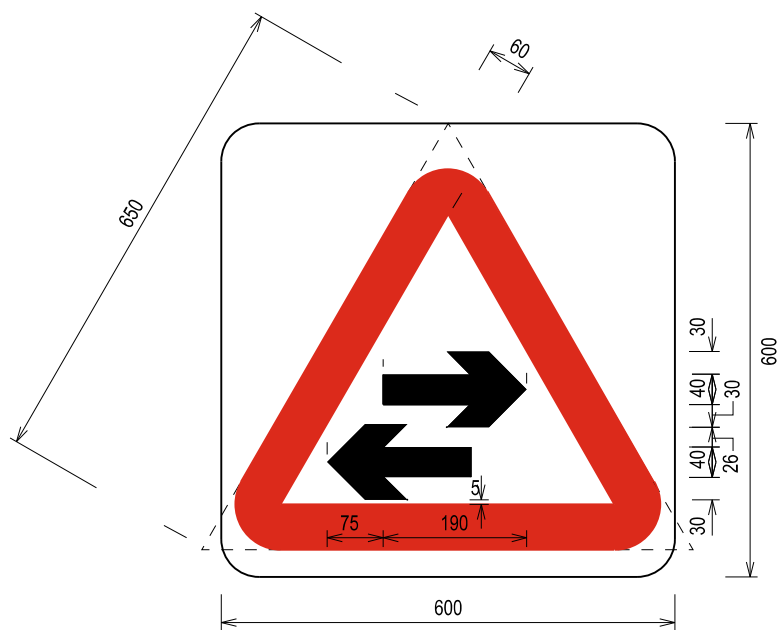


TWO WAY TRAFFIC ACROSS A ONE WAY CARRIAGEWAY AHEAD

THIS SIGN INDICATES THAT MOTORISTS ARE APPROACHING A CONTROLLED OR UNCONTROLLED JUNCTION WHERE THE ROAD PERPENDICULAR TO THE APPROACH IS TWO-WAY. IT MAY BE USED WITH A SUPPLEMENTARY PLATE.

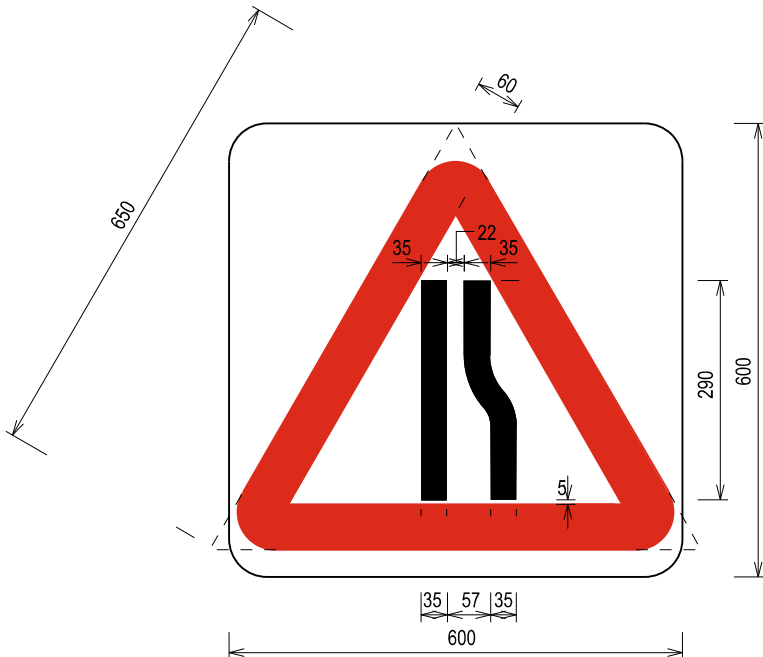


ROAD NARROWS ON RIGHT AHEAD

THIS SIGN INDICATES A ROAD NARROWING AHEAD ON THE RIGHT SIDE. IT MAY BE USED WITH A SUPPLEMENTARY PLATE.

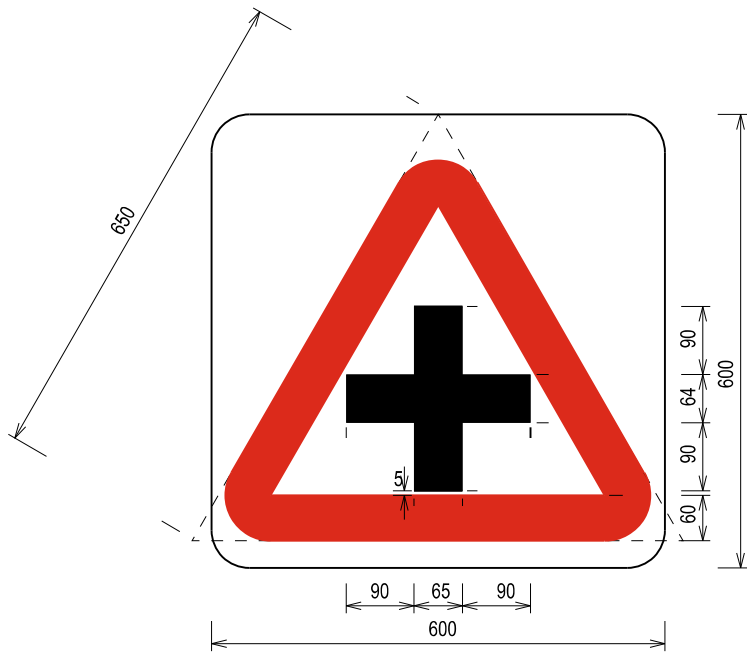


CROSS ROADS AHEAD

THIS SIGN INDICATES THAT MOTORISTS ARE APPROACHING A CONTROLLED OR UNCONTROLLED CROSS ROADS. THIS MAY BE USED WITH A SUPPLEMENTARY PLATE.

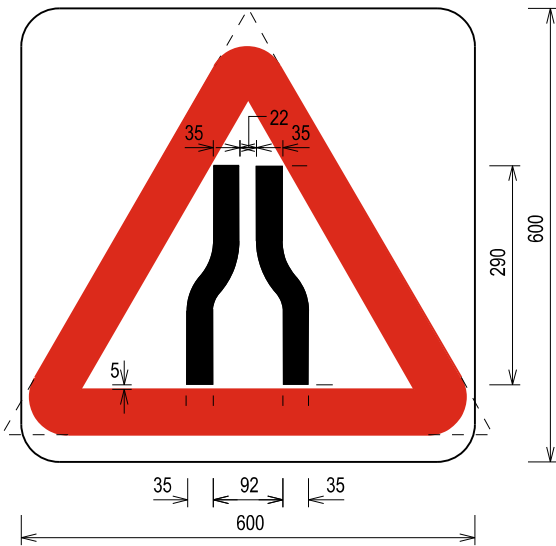

ROAD NARROWS ON BOTH SIDES AHEAD


THIS SIGN INDICATES THAT THE ROAD AHEAD BECOMES NARROWER ON BOTH SIDES. IT MAY BE USED WITH A SUPPLEMENTARY PLATE.

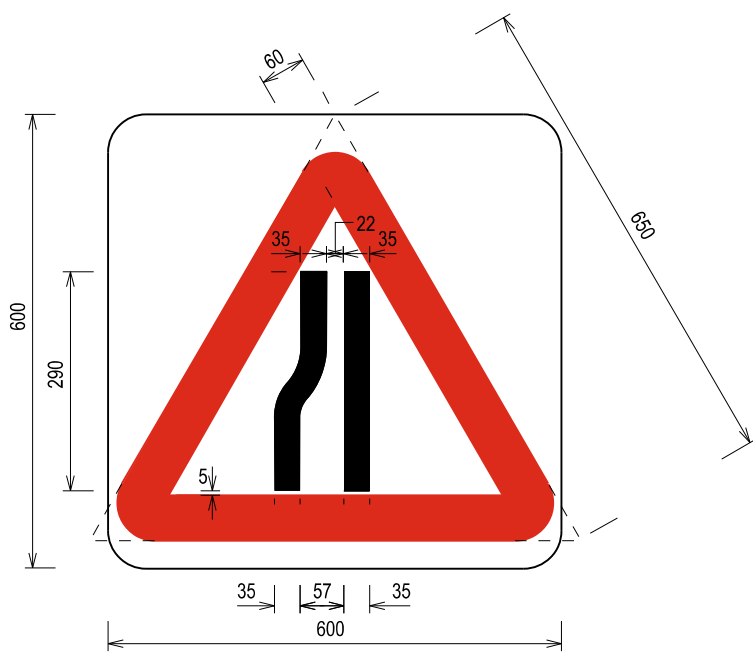

ROAD NARROWS ON LEFT AHEAD


THIS SIGN INDICATES A ROAD NARROWING AHEAD ON THE LEFT SIDE. IT MAY BE USED WITH A SUPPLEMENTARY PLATE.

STANDARD DETAIL		Land Transport Authority	
TRAFFIC WARNING SIGNS (SHEET 1 OF 9)		DRAWING NO. LTA/SDRE14/17/TFW1	
		DATE OF ISSUE 1st APR 2014	REV. -
REV. DATE		SCALE 1:10	SHEET NO. 1 OF 9

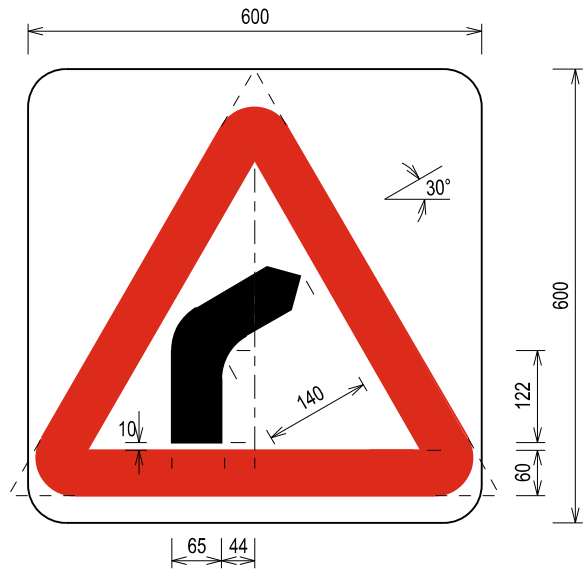


BEND TO THE RIGHT AHEAD

THIS SIGN INDICATES THAT THE ROAD AHEAD BENDS TO THE RIGHT. IT MAY BE USED WITH A SUPPLEMENTARY PLATE.

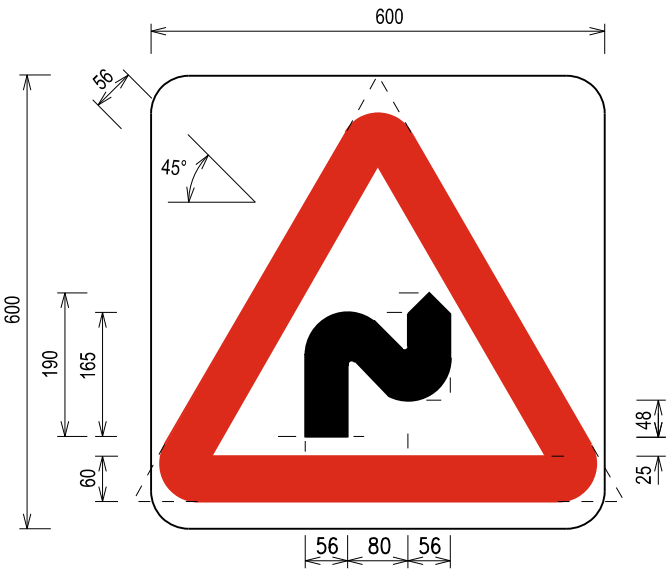


DOUBLE BEND AHEAD, FIRST TO THE RIGHT

THIS SIGN INDICATES THAT THE ROAD AHEAD HAS A DOUBLE BEND, WITH THE FIRST BEND TO THE RIGHT. IT MAY BE USED WITH A SUPPLEMENTARY PLATE.

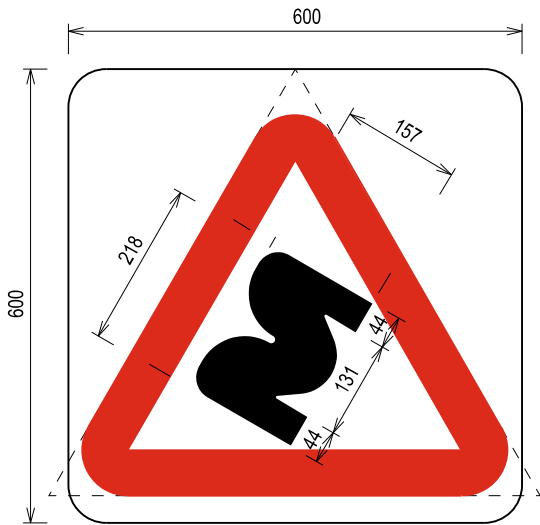


SERIES OF BENDS FIRST, TO THE RIGHT AHEAD

THIS SIGN INDICATES THAT THE ROAD AHEAD HAS A SERIES OF BENDS, WITH THE FIRST BEND TO THE RIGHT. IT MAY BE USED WITH A SUPPLEMENTARY PLATE.

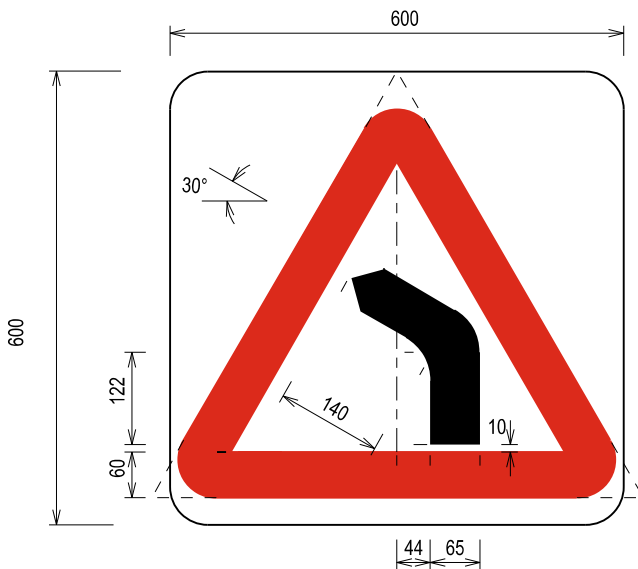


BEND TO THE LEFT AHEAD

THIS SIGN INDICATES THAT THE ROAD AHEAD BENDS TO THE LEFT. IT MAY BE USED WITH A SUPPLEMENTARY PLATE.

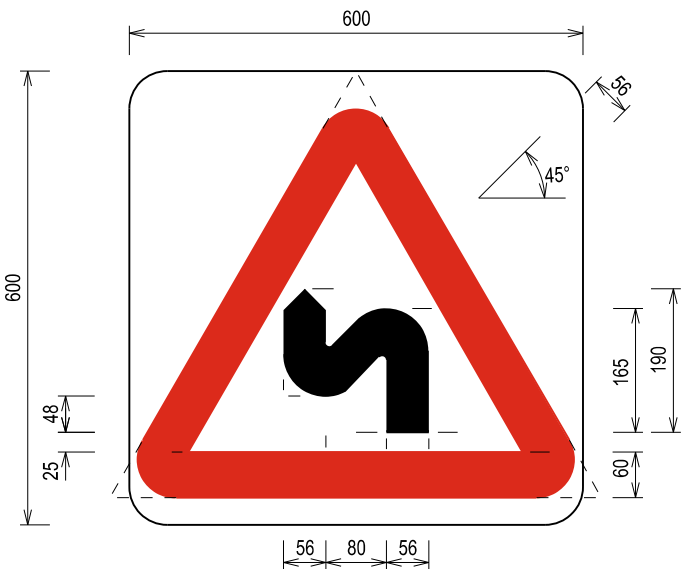

DOUBLE BEND AHEAD, FIRST TO THE LEFT

THIS SIGN INDICATES THAT THE ROAD AHEAD HAS A DOUBLE BEND, WITH THE FIRST BEND TO THE LEFT. IT MAY BE USED WITH A SUPPLEMENTARY PLATE.

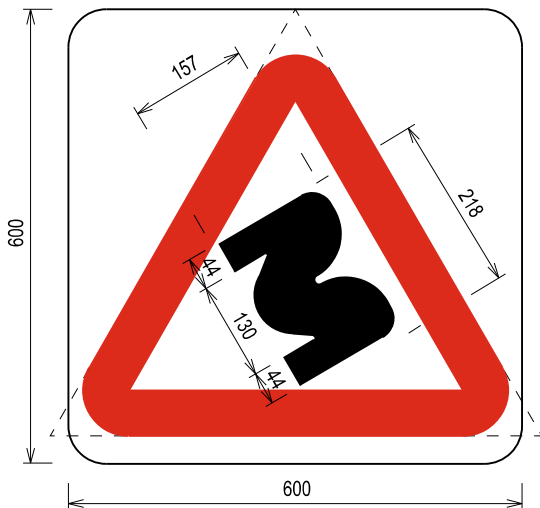


SERIES OF BENDS FIRST, TO THE LEFT AHEAD

THIS SIGN INDICATES THAT THE ROAD AHEAD HAS A SERIES OF BENDS WITH THE FIRST BEND TO THE LEFT. IT MAY BE USED WITH A SUPPLEMENTARY PLATE.


REV.	DATE	STANDARD DETAIL	Land Transport Authority		
			DRAWING NO. LTA/SDRE14/17/TFW2		
			REV. -		
			DATE OF ISSUE 1st APR 2014	SCALE 1:10	SHEET NO. 2 OF 9

TRAFFIC WARNING SIGNS
(SHEET 2 OF 9)

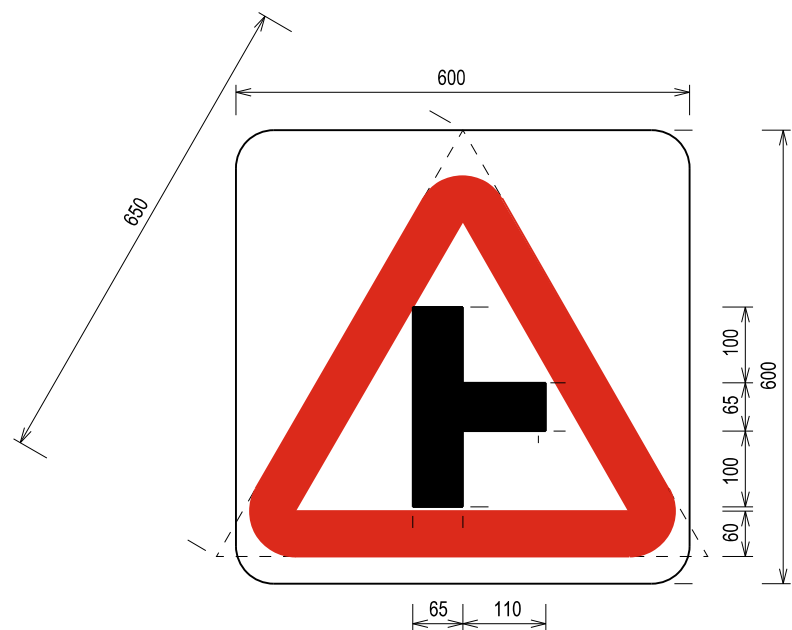


SIDE ROAD TO THE RIGHT AHEAD

THIS SIGN INDICATES THE APPROACH TO A SIDE ROAD JUNCTION. IT MAY BE USED WITH A SUPPLEMENTARY PLATE.

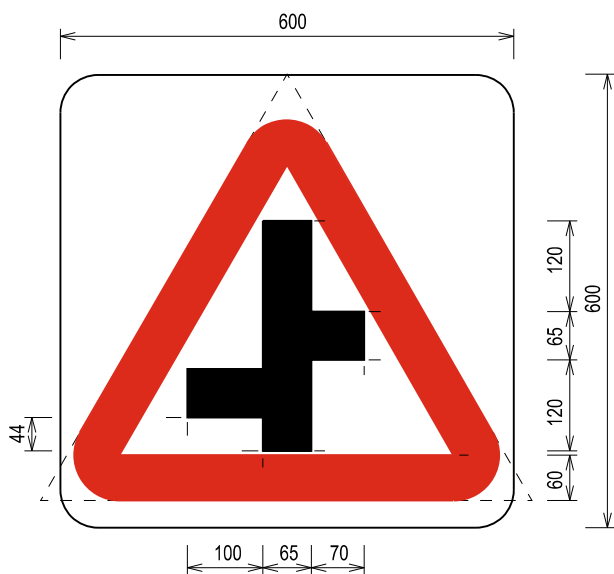


STAGGERED JUNCTION, LEFT TURN FIRST AHEAD

THIS SIGN INDICATES THE APPROACH TO A STAGGERED JUNCTION. IT MAY BE USED WITH A SUPPLEMENTARY PLATE.

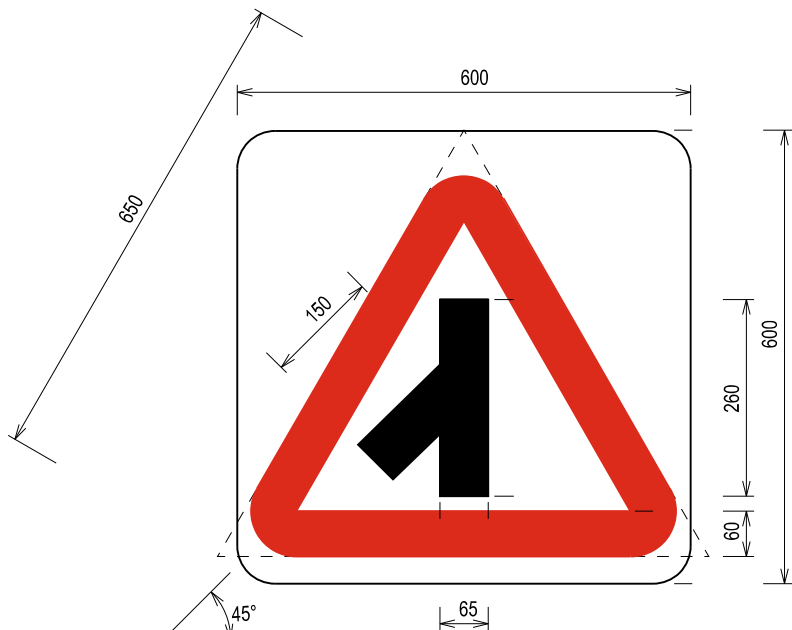


TRAFFIC MERGES FROM LEFT AHEAD

THIS SIGN INDICATES THE APPROACH TO A POINT WHERE TRAFFIC WILL BE MERGING FROM THE LEFT ONTO THEIR ROUTE. IT MAY BE USED WITH A SUPPLEMENTARY PLATE.

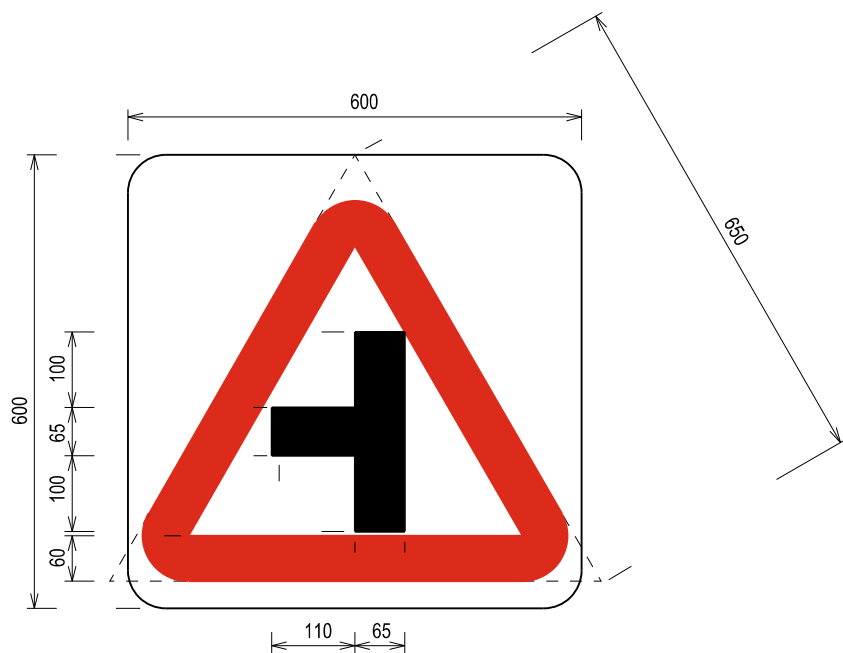


SIDE ROAD TO THE LEFT AHEAD

THIS SIGN INDICATES THE APPROACH TO A SIDE ROAD JUNCTION. IT MAY BE USED WITH A SUPPLEMENTARY PLATE.

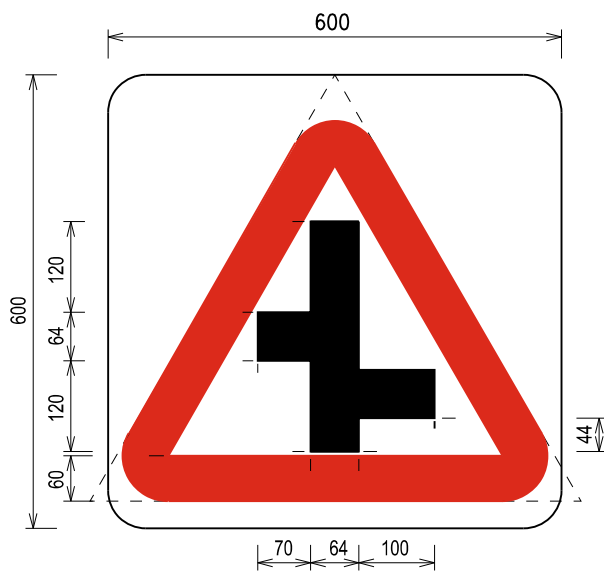

STAGGERED JUNCTION,
RIGHT TURN FIRST AHEAD


THIS SIGN INDICATES THE APPROACH TO A STAGGERED JUNCTION. IT MAY BE USED WITH A SUPPLEMENTARY PLATE.

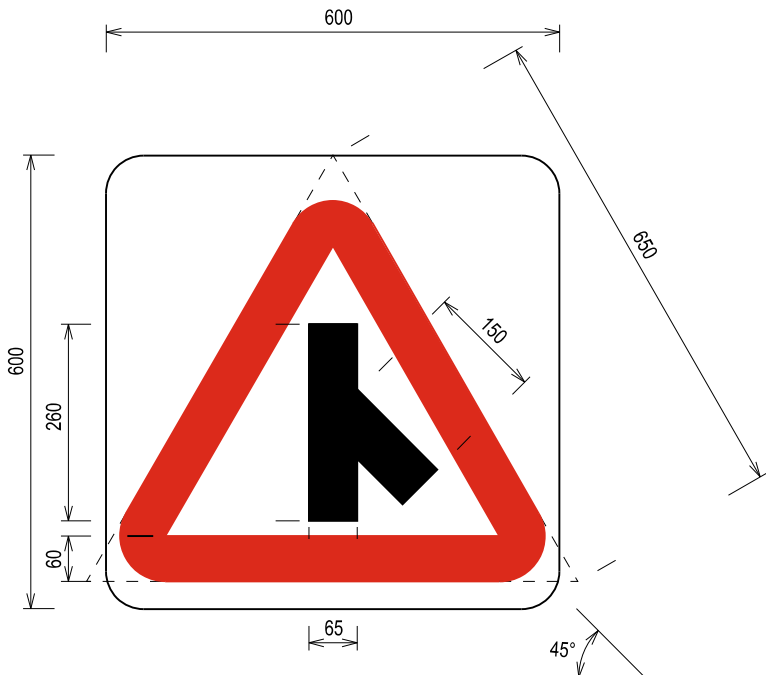

TRAFFIC MERGES FROM RIGHT AHEAD


THIS SIGN INDICATES THE APPROACH OF A POINT WHERE TRAFFIC WILL BE MERGING FROM THE RIGHT ONTO THEIR ROUTE. IT MAY BE USED WITH A SUPPLEMENTARY PLATE.

STANDARD DETAIL		Land Transport Authority	
TRAFFIC WARNING SIGNS (SHEET 3 OF 9)		DRAWING NO. LTA/SDRE14/17/TFW3	REV. -
REV.	DATE	DATE OF ISSUE 1st APR 2014	SHEET NO. 3 OF 9

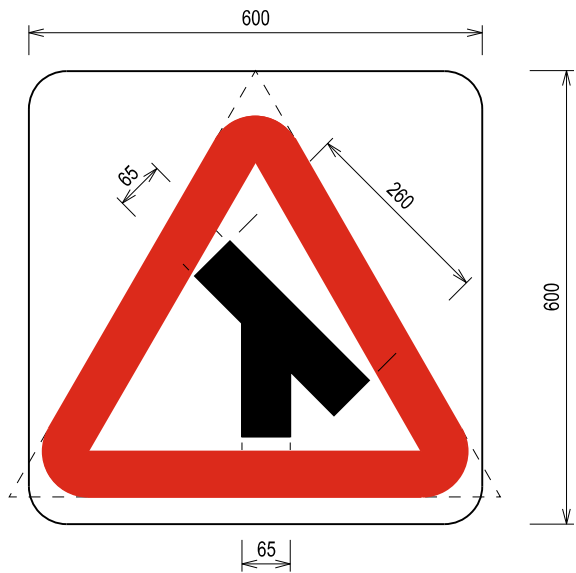


MERGING INTO TRAFFIC ON RIGHT AHEAD

THIS SIGN INDICATES THE APPROACH TO A MAJOR ROUTE AND MOTORISTS WILL BE EXPECTED TO MERGE WITH TRAFFIC ON THE MAJOR ROUTE. IT MAY BE USED WITH A SUPPLEMENTARY PLATE.

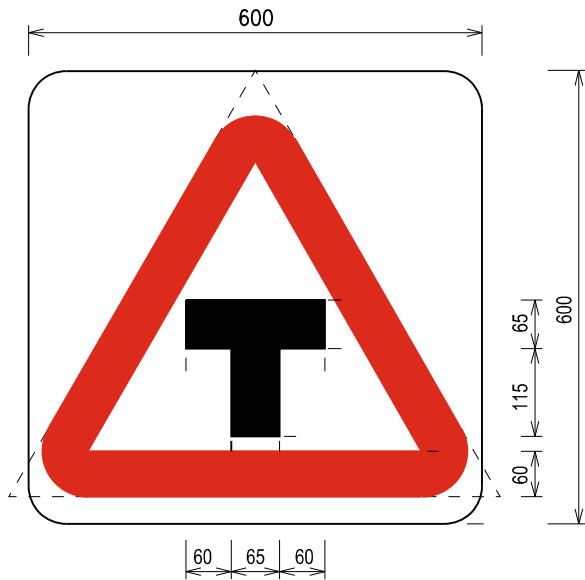


T-JUNCTION AHEAD

THIS SIGN INDICATES THE APPROACH TO A CONTROLLED OR UNCONTROLLED T-JUNCTION. IT MAY BE USED WITH A SUPPLEMENTARY PLATE.

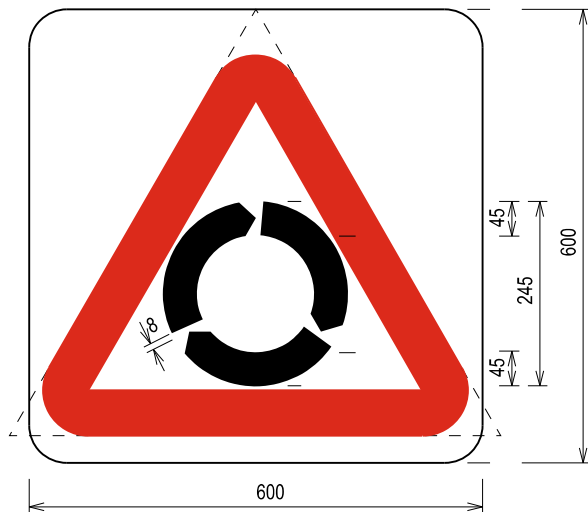


ROUNDABOUT AHEAD

THIS SIGN INDICATES THE APPROACH TO A ROUNDABOUT. THIS SIGN MAY BE USED WITH A SUPPLEMENTARY PLATE.

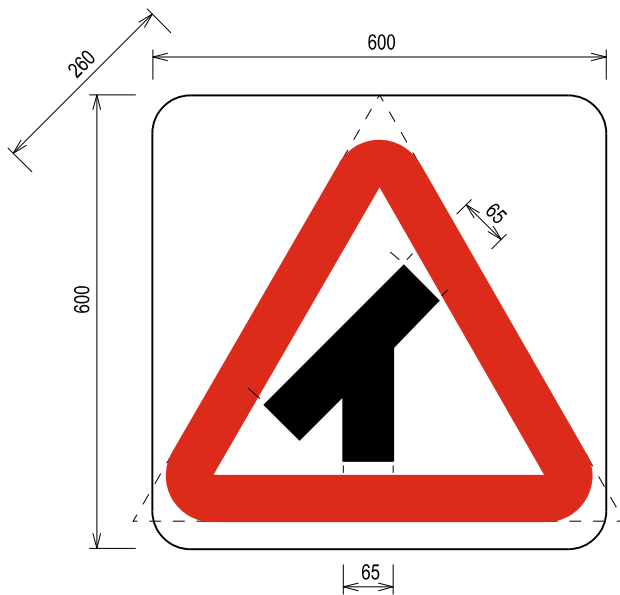


MERGING INTO TRAFFIC ON LEFT AHEAD

THIS SIGN INDICATES THE APPROACH TO A MAJOR ROUTE AND MOTORISTS WILL BE EXPECTED TO MERGE WITH TRAFFIC ON THE MAJOR ROUTE. IT MAY BE USED WITH A SUPPLEMENTARY PLATE.

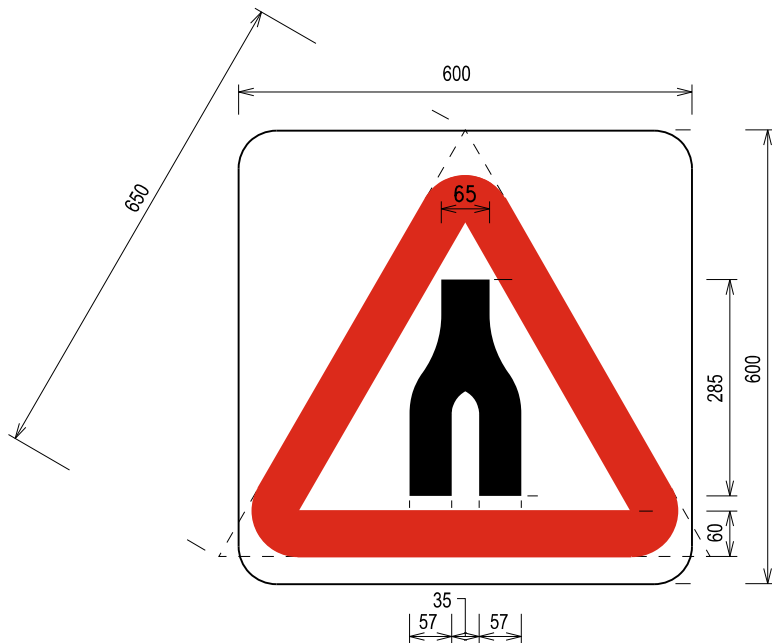

DUAL CARRIAGEWAY ENDS AHEAD


THIS SIGN INDICATES THAT THE DUAL CARRIAGEWAY WILL BECOME A SINGLE CARRIAGEWAY AHEAD. THIS SIGN MAY BE USED WITH A SUPPLEMENTARY PLATE.

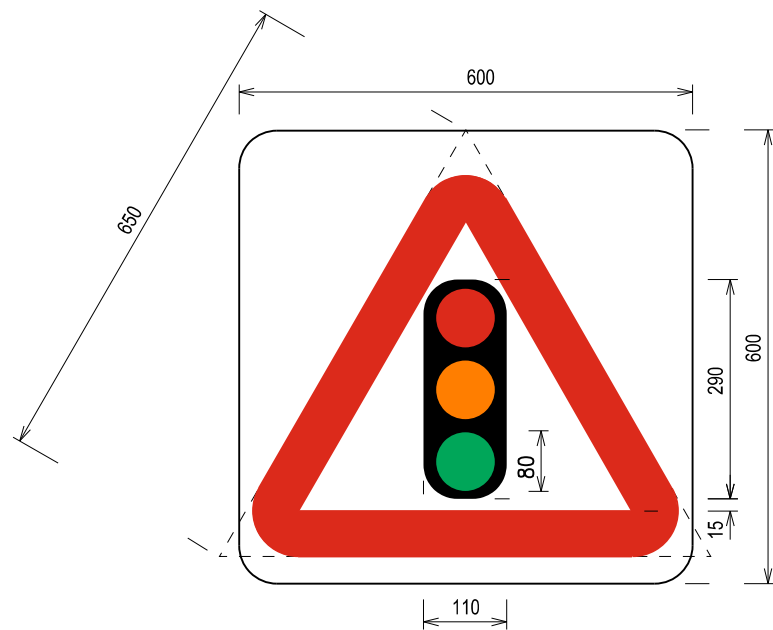

TRAFFIC SIGNALS AHEAD


THIS SIGN INDICATES THE APPROACH TO A SET OF TRAFFIC SIGNAL. IT MAY BE USED WITH A SUPPLEMENTARY PLATE.

STANDARD DETAIL		Land Transport Authority	
TRAFFIC WARNING SIGNS (SHEET 4 OF 9)		DRAWING NO. LTA/SDRE14/17/TFW4	REV. -
REV.	DATE	DATE OF ISSUE 1st APR 2014	SHEET NO. 4 OF 9

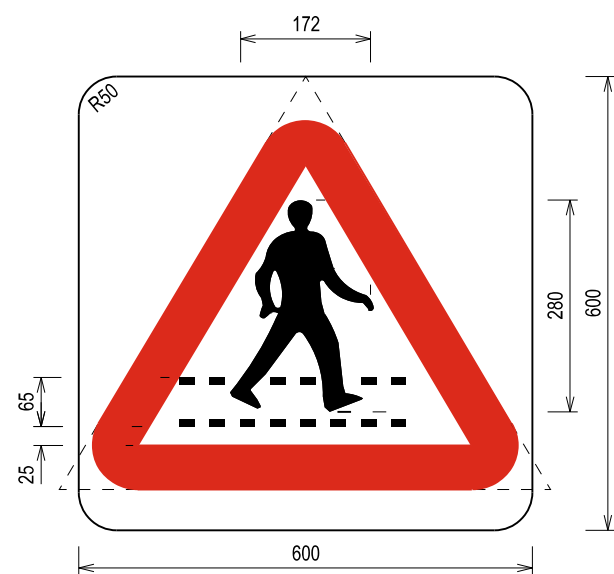


PEDESTRIAN CROSSING AHEAD

THIS SIGN INDICATES THE APPROACH TO A PEDESTRIAN CROSSING. IT MAY BE USED IN CONJUNCTION WITH A SUPPLEMENTARY PLATE.

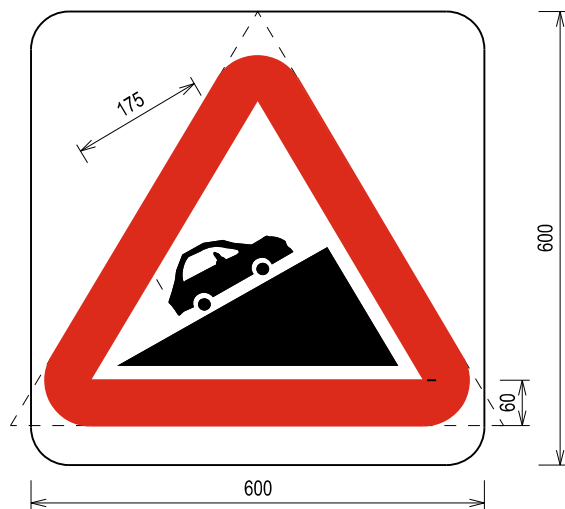


STEEP HILL UPWARDS AHEAD

THIS SIGN INDICATES A STEEP HILL UPWARDS AND SHOULD BE USED AT THE FOOT OF ALL HILLS LIKELY TO GIVE TROUBLE TO THE MOTORISTS. IT MAY BE USED WITH A SUPPLEMENTARY PLATE.

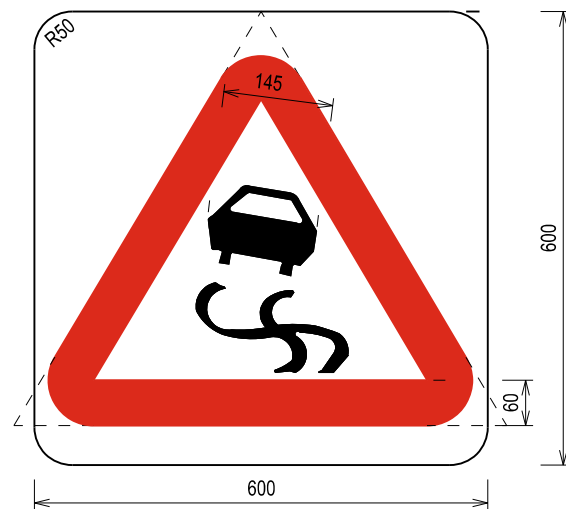


SLIPPERY ROAD AHEAD

THIS SIGN WARNS OF THE POSSIBLE SLIPPERY CONDITION OF THE ROAD SURFACE AHEAD. IT MAY BE USED WITH A SUPPLEMENTARY PLATE.

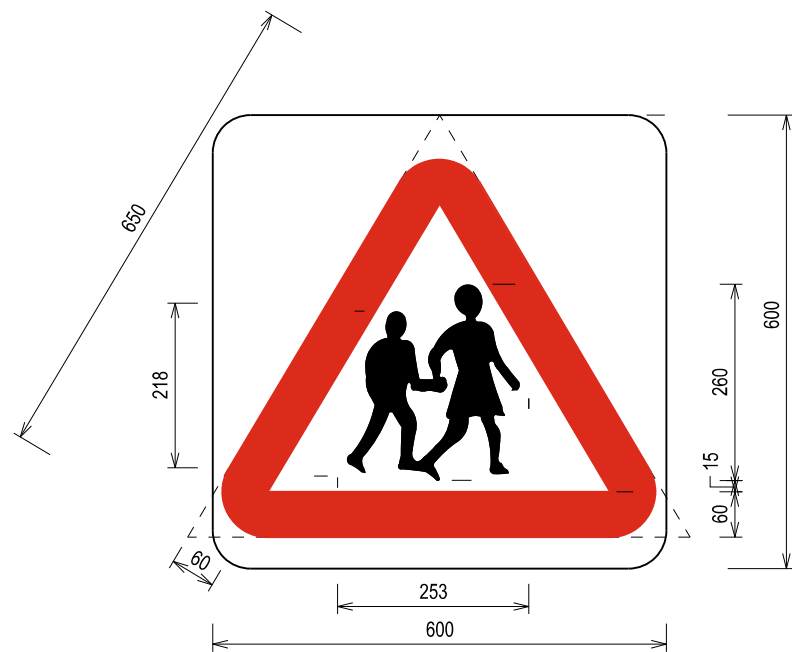


CHILDREN AHEAD

THIS SIGN INDICATES THE APPROACH TO AN AREA WHERE CHILDREN ARE LIKELY TO BE PLAYING NEARBY OR CROSSING THE ROAD. IT MAY BE USED TO INDICATE THE APPROACH TO A SCHOOL OR PLAYGROUND EXIT. IT MAY ALSO BE USED WITH A SUPPLEMENTARY PLATE.

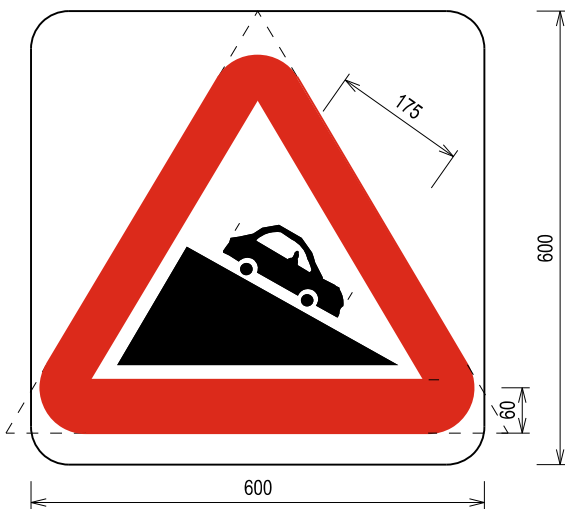

STEEP HILL DOWNWARDS AHEAD


THIS SIGN INDICATES A STEEP HILL DOWNWARDS AND SHOULD BE USED AT THE TOP OF HILLS WHEN THE GRADIENT OF THE HILL IS 1:10 OR STEEPER. IT MAY BE USED WITH A SUPPLEMENTARY PLATE.

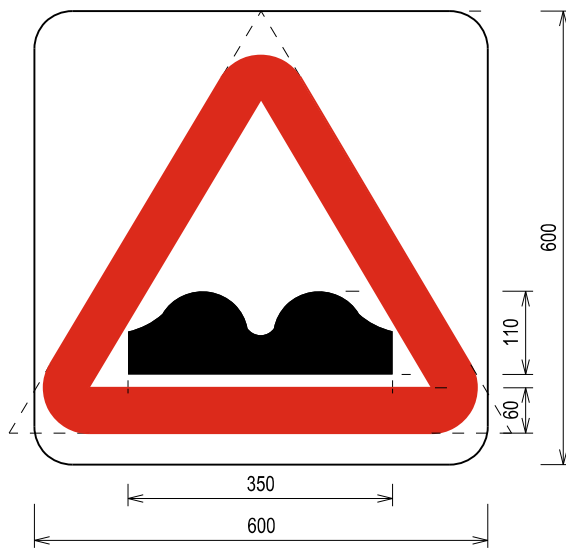

UNEVEN ROAD AHEAD


THIS SIGN WARNS OF THE UNEVEN ROAD SURFACE AHEAD. IT MAY BE USED WITH A SUPPLEMENTARY PLATE.

STANDARD DETAIL		Land Transport Authority	
TRAFFIC WARNING SIGNS (SHEET 5 OF 9)		DRAWING NO. LTA/SDRE14/17/TFW5	
		DATE OF ISSUE 1st APR 2014	REV. -
		SCALE 1:10	SHEET NO. 5 OF 9

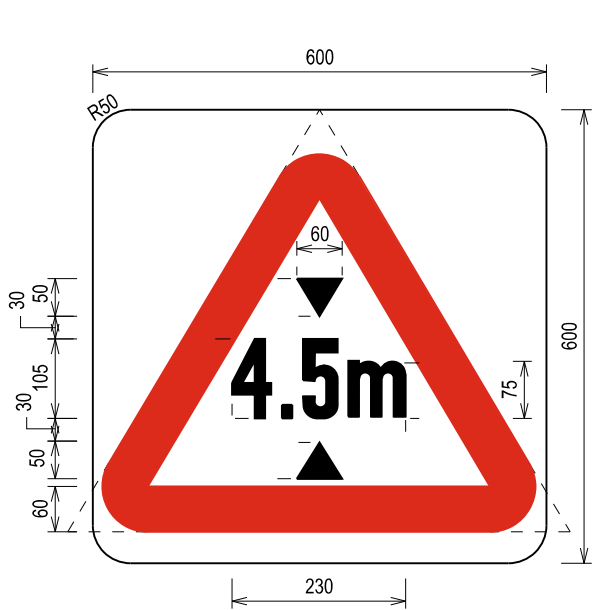


HEIGHT LIMIT AHEAD

THIS SIGN WARNS OF A 4.5m HEIGHT RESTRICTION AHEAD. IT MAY BE QUALIFIED BY A SUPPLEMENTARY PLATE. THE NUMERALS IN THE ABOVE SIGN MAY BE ALTERED TO CATER FOR DIFFERENT HEIGHT RESTRICTIONS.

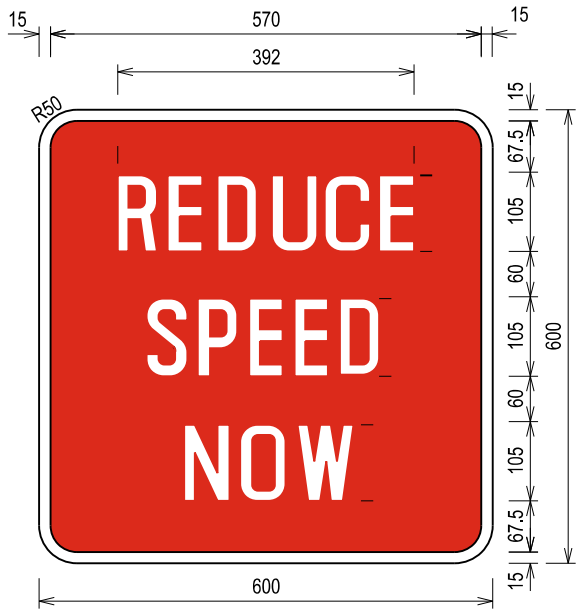


REDUCE SPEED NOW

THIS PLATE MAY BE USED WITH OTHER SIGNS.

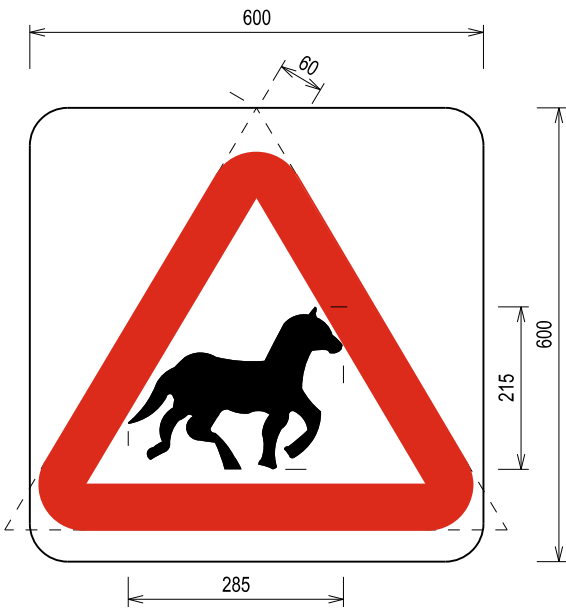

HORSES OR PONIES AHEAD

THIS SIGN INDICATES THAT MOTORISTS ARE APPROACHING A LENGTH OF ROAD ON WHICH THEY ARE LIKELY TO ENCOUNTER HORSES. IT MAY BE USED WITH A SUPPLEMENTARY PLATE.

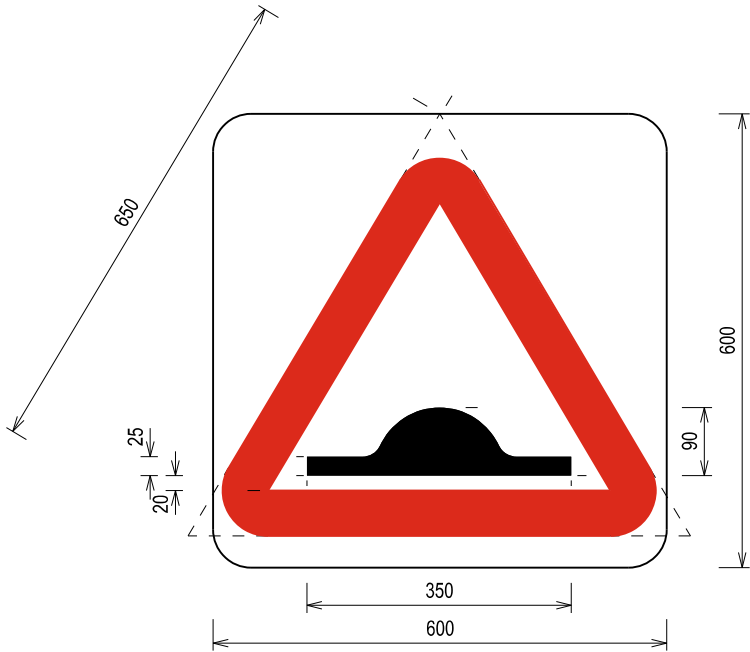

ROAD HUMP AHEAD


THIS SIGN WARNS OF A ROAD HUMP OR HUMPS AHEAD. IT MAY BE ACCOMPANIED BY A 'SLOW' PLATE TO ADVISE MOTORISTS TO SLOW DOWN.



RAISED ZEBRA CROSSING


THIS SIGN INDICATES THE APPROACH TO A RAISED ZEBRA CROSSING. IT MAY BE USED IN CONJUNCTION WITH A SUPPLEMENTARY PLATE.

--	--	

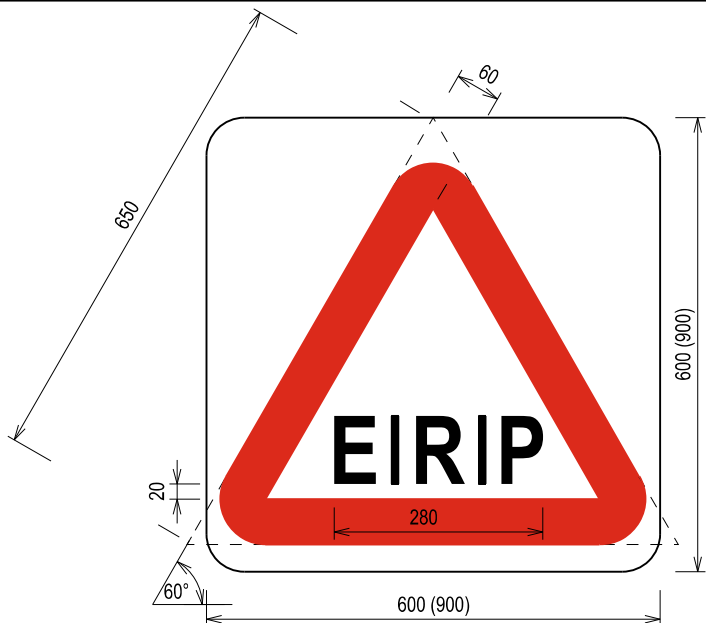


ELECTRONIC ROAD PRICING ZONE AHEAD

THIS SIGN INDICATES THERE IS AN ELECTRONIC ROAD PRICING ZONE AHEAD AND MOTORISTS SHOULD INSERT CASHCARD INTO THE IU TO PAY FOR ENTERING THE ZONE DURING RESTRICTED HOURS.

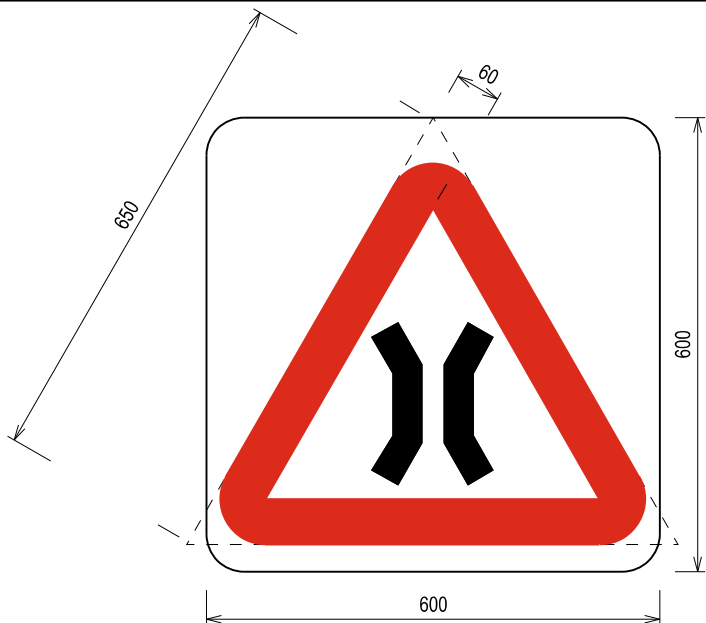


NARROW BRIDGE AHEAD

THIS SIGN INDICATES THE APPROACH TO A NARROW BRIDGE. IT MAY BE USED WITH A SUPPLEMENTARY PLATE.

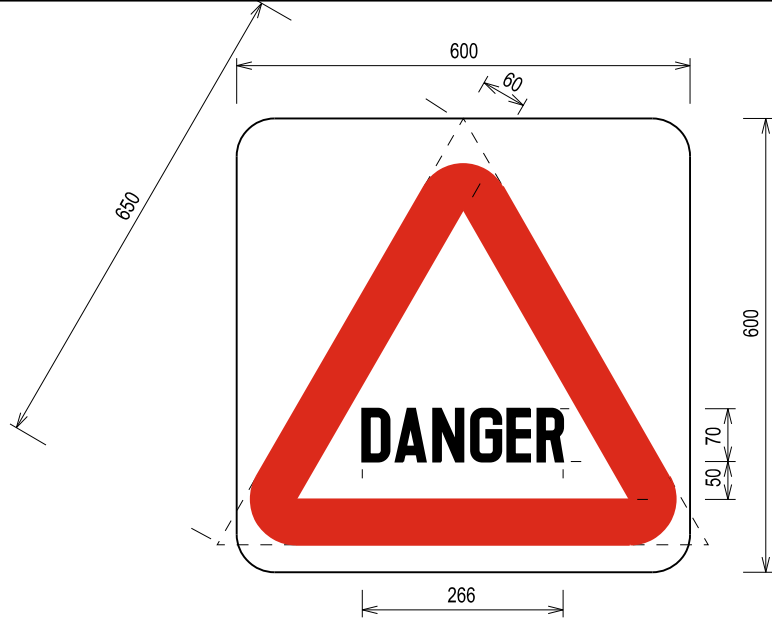

DANGER AHEAD

THIS SIGN IS THE FIRST WARNING TO MOTORISTS OF AN OBSTRUCTION AHEAD AND SHOULD BE EXHIBITED ON ALL APPROACHES TO THE WORK SITE. ON EXPRESSWAYS THE SIGN MUST BE SUPPLEMENTED BY A DISTANCE PLATE.

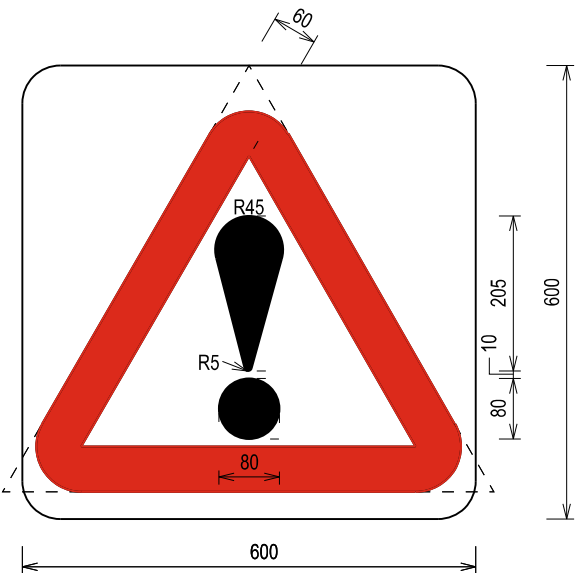

OTHER DANGER AHEAD

THIS SIGN WARNS OF POTENTIAL DANGER AHEAD WHICH IS NOT COVERED BY ANY OTHER WARNING SIGN. THE SIGN WILL ALWAYS BE QUALIFIED BY A SUPPLEMENTARY PLATE GIVING THE NATURE OF OTHER DANGER.



QUAYSIDE OR RIVER BANK AHEAD


THIS SIGN WARNS MOTORISTS THAT THE ROAD IS ABOUT TO LEAD ONTO A QUAYSIDE OR RIVER BANK.



ACCIDENT AREA AHEAD


THIS SIGN WARNS MOTORISTS THAT THE SECTION OF ROAD AHEAD IS PRONE TO ACCIDENTS.

--	--	

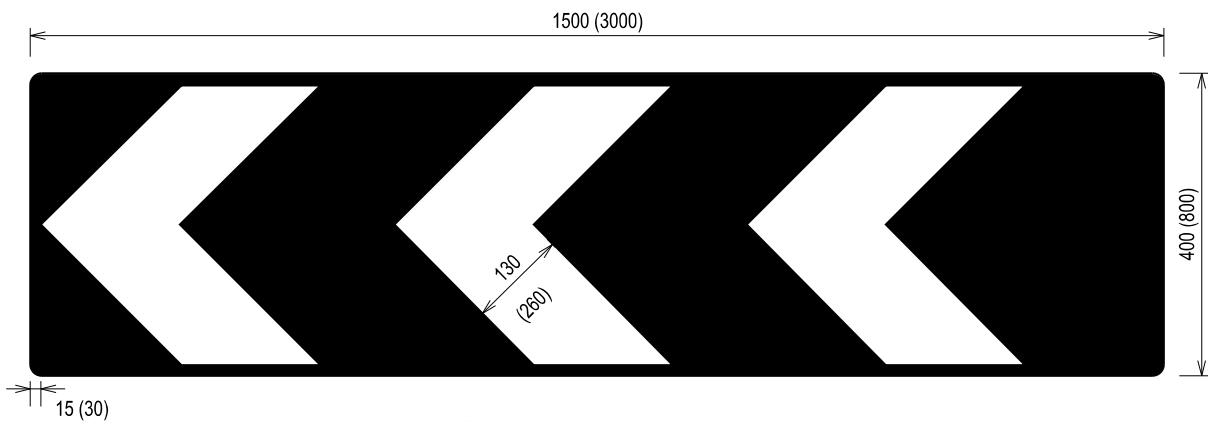


SHARP DEVIATION

THIS SIGN IS USED WHERE THERE IS A SHARP DEVIATION ON THE ROAD TO RIGHT OR LEFT. IT IS TO BE PLACED ON THE BEND OR DEVIATION FACING THE APPROACHING TRAFFIC. IT MAY BE USED SINGLY OR ON LONG BENDS MULTIPLE DEVIATION SIGNS MAY BE PLACED END TO END. THE SIGN MAY ALSO BE USED ON ROUNDABOUTS OR ON T-JUNCTIONS TO MARK THE END OF THE APPROACHING ROUTE.

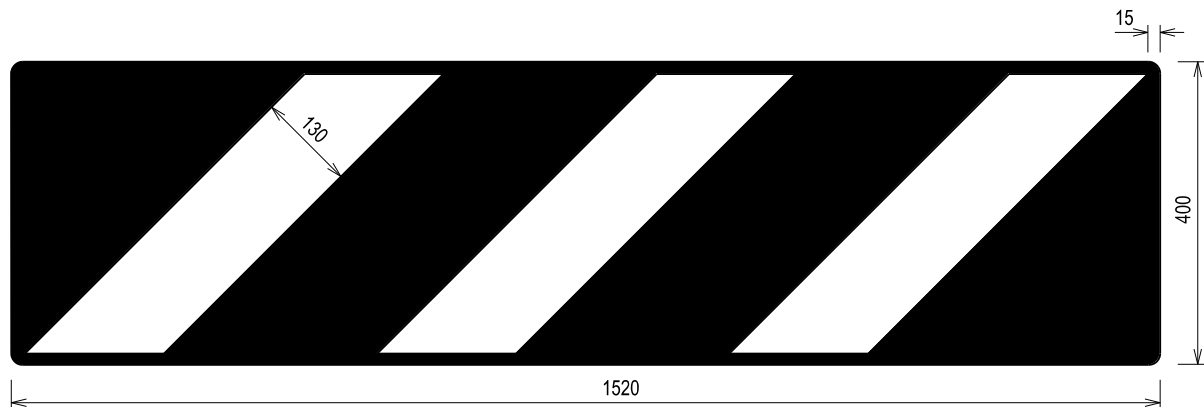


BARRIER

THIS SIGN IS FOR TEMPORARY USE AROUND OBSTRUCTIONS OR EXCAVATIONS. IT MAY BE EXTENDED TO ANY LENGTH REQUIRED.

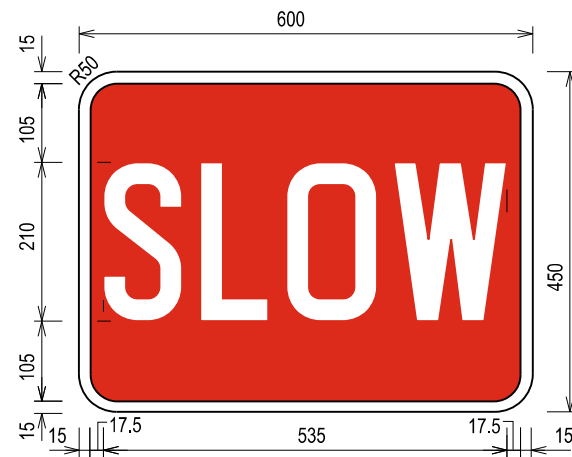


SLOW

THIS SIGN IS TO INFORM MOTORISTS TO REDUCE THEIR SPEED DUE TO THE PROXIMITY OF SOME DANGER AHEAD.

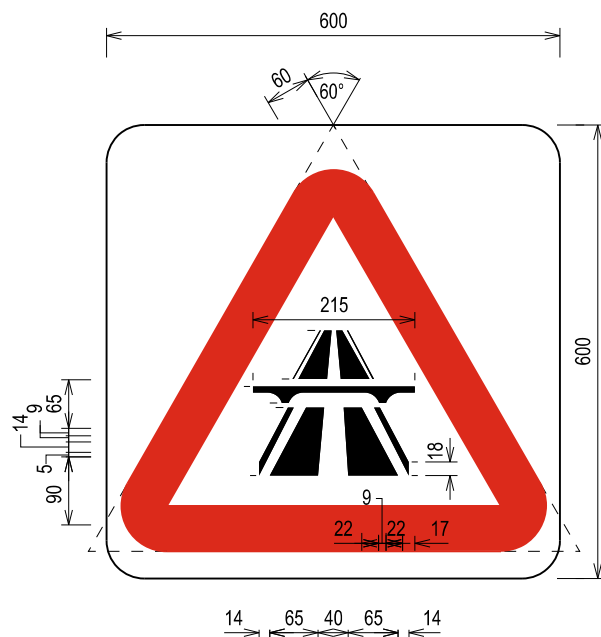


EXPRESSWAY AHEAD

THIS SIGN INDICATES THAT THE STRETCH OF ROAD AHEAD IS ON EXPRESSWAY. THE SPEED LIMIT ON EXPRESSWAYS IS 80 KM/HR

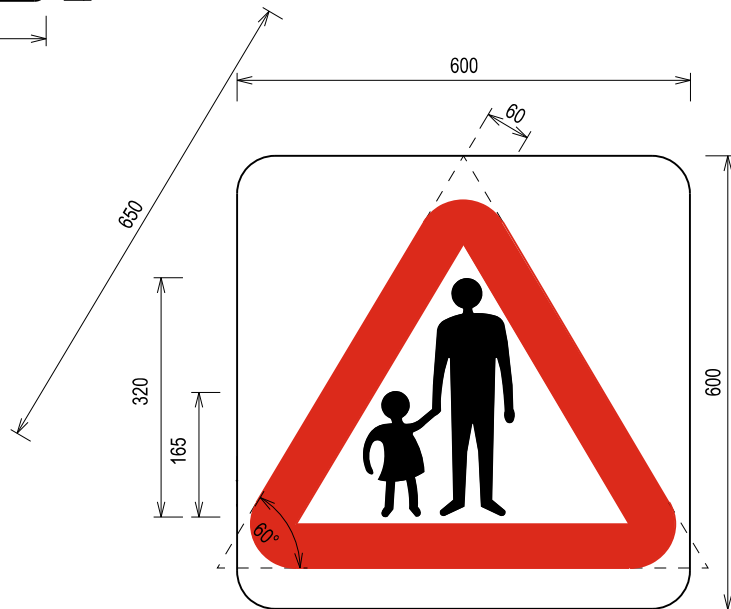

PEDESTRIAN IN ROAD AHEAD

THIS SIGN INDICATES THE APPROACH TO AN AREA WHERE PEDESTRIAN ARE LIKELY TO CROSS THE ROAD. IT MAY BE USED IN CONJUNCTION WITH A SUPPLEMENTARY PLATE.

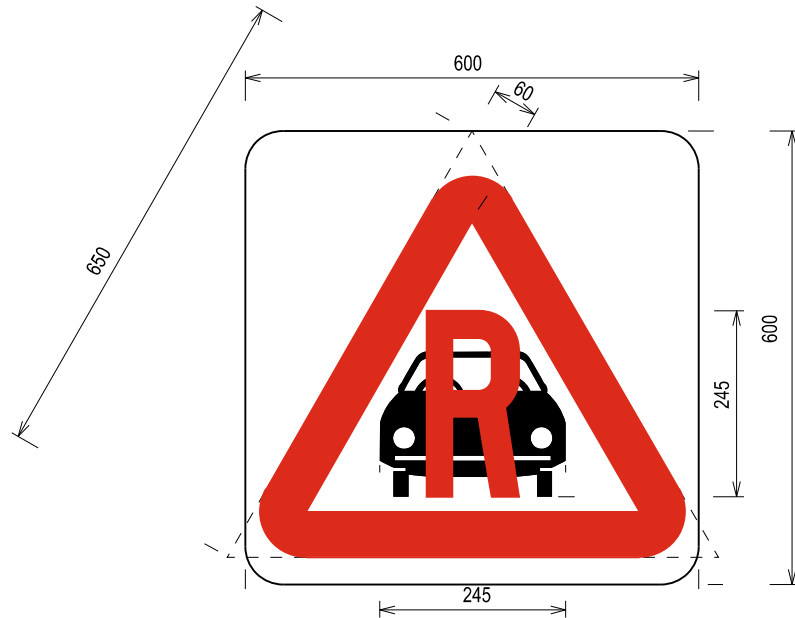

RESTRICTED ZONE AHEAD

THIS SIGN WARNS MOTORISTS THAT THE SECTION OF ROAD AHEAD IS WITHIN THE RESTRICTED ZONE. IT MAY BE USED WITH A SUPPLEMENTARY PLATE.



ELDERLY OR HANDICAPPED
PEDESTRIANS AHEAD

REV.	DATE	STANDARD	DETAIL	Land Transport Authority		
				DRAWING NO. LTA/SDRE14/17/TFW8		
				REV. -		
				DATE OF ISSUE 1st APR 2014	SCALE 1:10	SHEET NO. 8 OF 9

STANDARD

DETAIL

TRAFFIC WARNING SIGNS
(SHEET 8 OF 9)

Land Transport Authority

DRAWING NO. LTA/SDRE14/17/TFW8

REV. -

DATE OF ISSUE
1st APR 2014


SCALE
1:10

SHEET NO.
8 OF 9




LOW FLYING AIRCRAFT AHEAD

THIS SIGN CAUTIONS MOTORISTS OF THE POSSIBILITY OF LOW FLYING AIRCRAFTS CROSSING THEIR PATH IN THE STRETCH OF ROAD AHEAD.

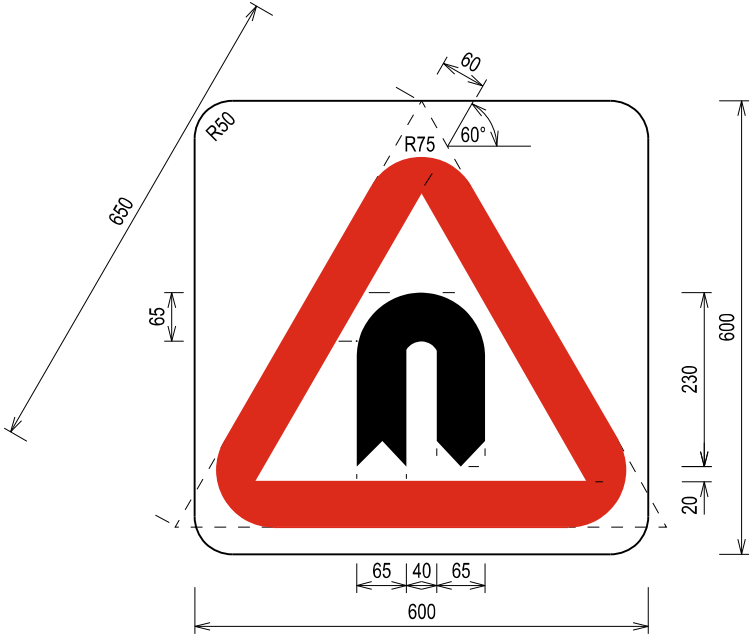


U-TURN AHEAD

THIS SIGN INDICATES THAT VEHICLES MAY BE MAKING A U-TURN AHEAD. (TO BE USED ONLY IN SPECIAL CIRCUMSTANCES)

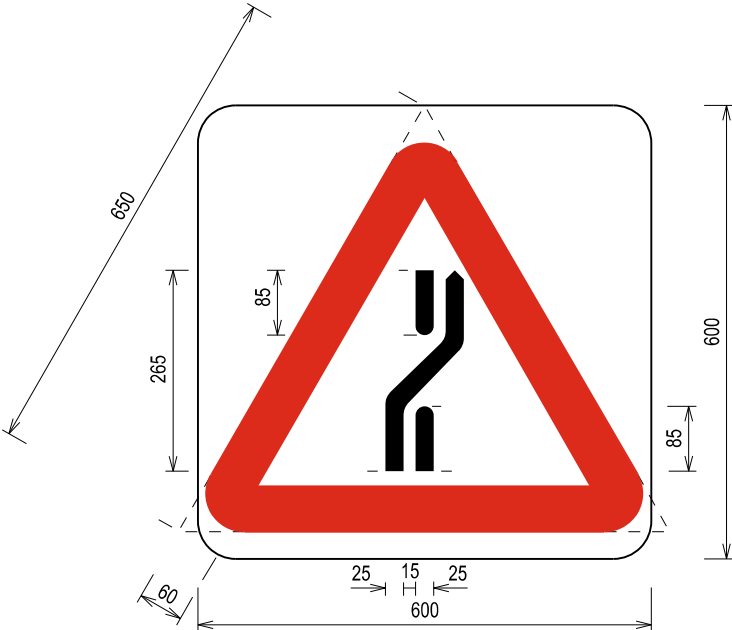


DIVERSION TO ANOTHER CARRIAGEWAY TO THE RIGHT AHEAD

THIS SIGN WILL BE USED TO DIVERT TRAFFIC FROM ONE CARRIAGEWAY OF A DUAL OR MULTI-CARRIAGEWAY ROAD TO ANOTHER AT AND AROUND WORKS OR OBSTRUCTION.

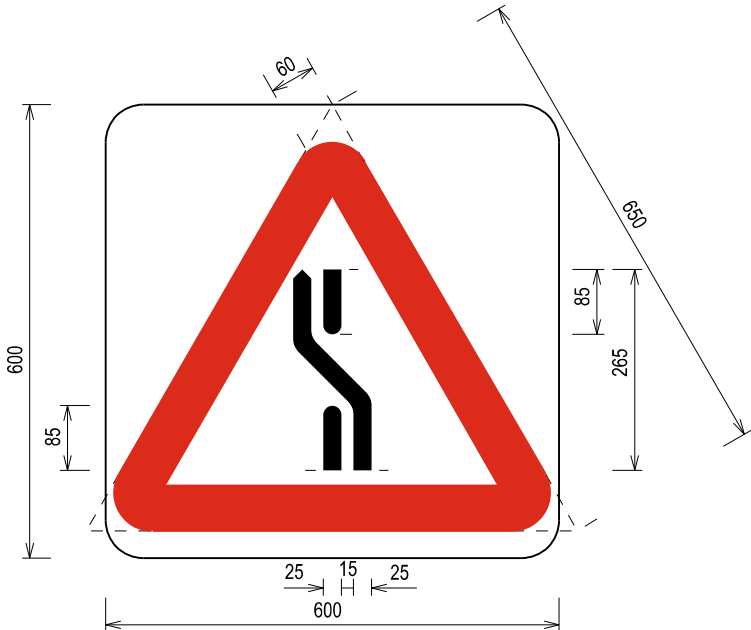


DIVERSION TO ANOTHER CARRIAGEWAY TO THE LEFT AHEAD

THIS SIGN WILL BE USED TO DIVERT TRAFFIC FROM ONE CARRIAGEWAY OF A DUAL OR MULTI-CARRIAGEWAY ROAD TO ANOTHER AT AND AROUND WORKS OR OBSTRUCTION.

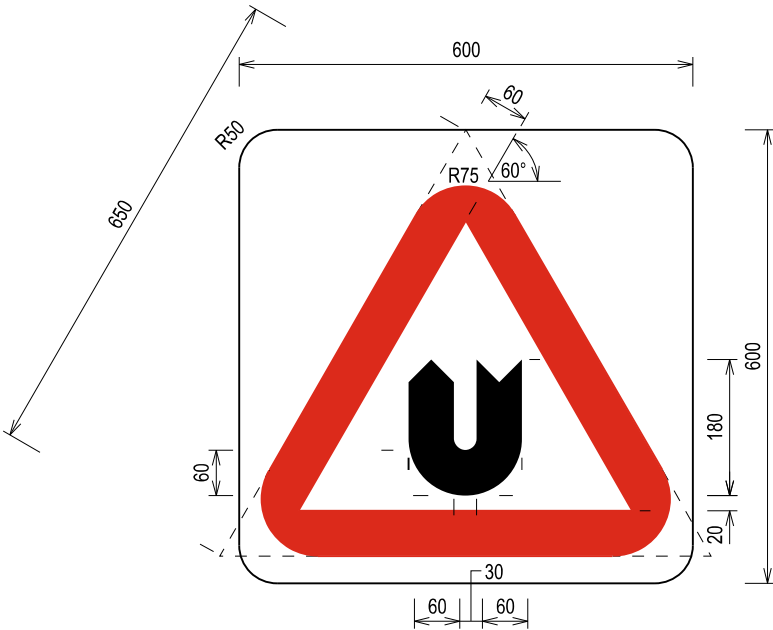

U-TURN AHEAD (FROM OPPOSITE DIRECTION)

THIS SIGN WARNS MOTORISTS THAT VEHICLES FROM THE OPPOSITE DIRECTION MAY BE MAKING A U-TURN AHEAD. (TO BE USED ONLY IN SPECIAL CIRCUMSTANCES)

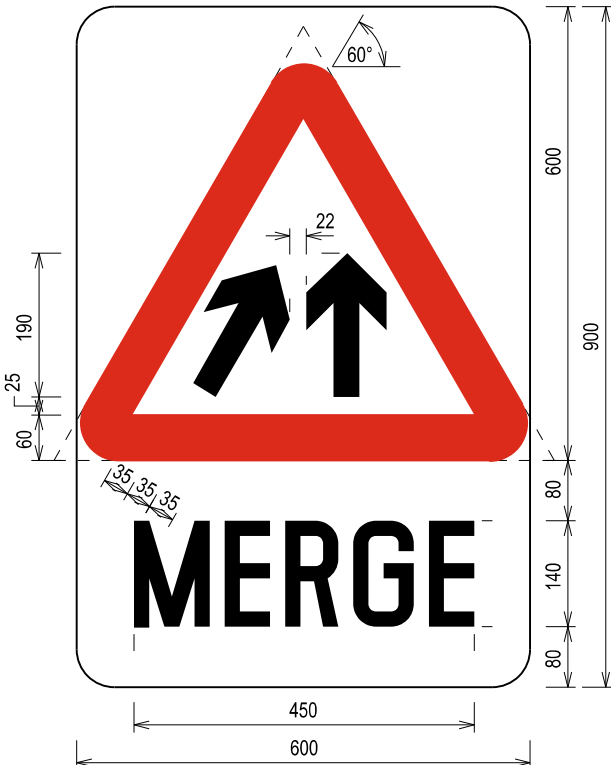

MERGE AHEAD

THIS SIGN INDICATES THAT THE TWO TRAFFIC LANES WILL BE MERGED INTO ONE TRAFFIC LANE AHEAD. IT MAY BE USED WITH A SUPPLEMENTARY SIGN.

REV.	DATE	STANDARD DETAIL	Land Transport Authority		
			DRAWING NO. LTA/SDRE14/17/TFW9		
			REV. -		
			DATE OF ISSUE 1st APR 2014	SCALE 1:10	SHEET NO. 9 OF 9

TRAFFIC WARNING SIGNS (SHEET 9 OF 9)