

CHAPTER 18


TRAFFIC INFORMATORY SIGNS

DRAWING TITLE	DRAWING NO.	REVISION
TRAFFIC INFORMATORY SIGNS (SHEET 1 OF 19)	LTA/SDRE14/18/TFI1	A
TRAFFIC INFORMATORY SIGNS (SHEET 2 OF 19)	LTA/SDRE14/18/TFI2	B
TRAFFIC INFORMATORY SIGNS (SHEET 3 OF 19)	LTA/SDRE14/18/TFI3	A
TRAFFIC INFORMATORY SIGNS (SHEET 4 OF 19)	LTA/SDRE14/18/TFI4	A
TRAFFIC INFORMATORY SIGNS (SHEET 5 OF 19)	LTA/SDRE14/18/TFI5	A
TRAFFIC INFORMATORY SIGNS (SHEET 6 OF 19)	LTA/SDRE14/18/TFI6	A
TRAFFIC INFORMATORY SIGNS (SHEET 7 OF 19)	LTA/SDRE14/18/TFI7	A
TRAFFIC INFORMATORY SIGNS (SHEET 8 OF 19)	LTA/SDRE14/18/TFI8	A
TRAFFIC INFORMATORY SIGNS (SHEET 9 OF 19)	LTA/SDRE14/18/TFI9	A
TRAFFIC INFORMATORY SIGNS (SHEET 10 OF 19)	LTA/SDRE14/18/TFI10	A
TRAFFIC INFORMATORY SIGNS (SHEET 11 OF 19)	LTA/SDRE14/18/TFI11	A
TRAFFIC INFORMATORY SIGNS (SHEET 12 OF 19)	LTA/SDRE14/18/TFI12	A
TRAFFIC INFORMATORY SIGNS (SHEET 13 OF 19)	LTA/SDRE14/18/TFI13	A
TRAFFIC INFORMATORY SIGNS (SHEET 14 OF 19)	LTA/SDRE14/18/TFI14	A
TRAFFIC INFORMATORY SIGNS (SHEET 15 OF 19)	LTA/SDRE14/18/TFI15	B
TRAFFIC INFORMATORY SIGNS (SHEET 16 OF 19)	LTA/SDRE14/18/TFI16	A
TRAFFIC INFORMATORY SIGNS (SHEET 17 OF 19)	LTA/SDRE14/18/TFI17	A


CHAPTER 18

TRAFFIC INFORMATORY SIGNS

DRAWING TITLE	DRAWING NO.	REVISION
TRAFFIC INFORMATORY SIGNS (SHEET 18 OF 19)	LTA/SDRE14/18/TFI18	A
TRAFFIC INFORMATORY SIGNS (SHEET 19 OF 19)	LTA/SDRE14/18/TFI19	A

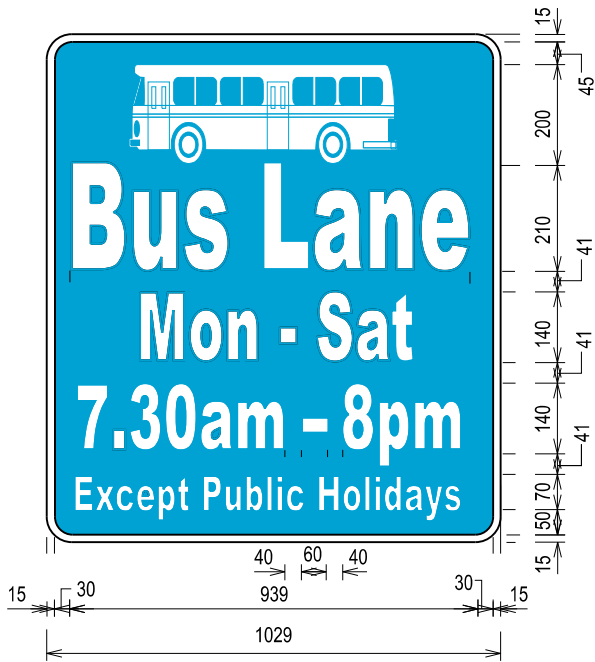

BUS LANE (FULL DAY)
SCALE 1:15

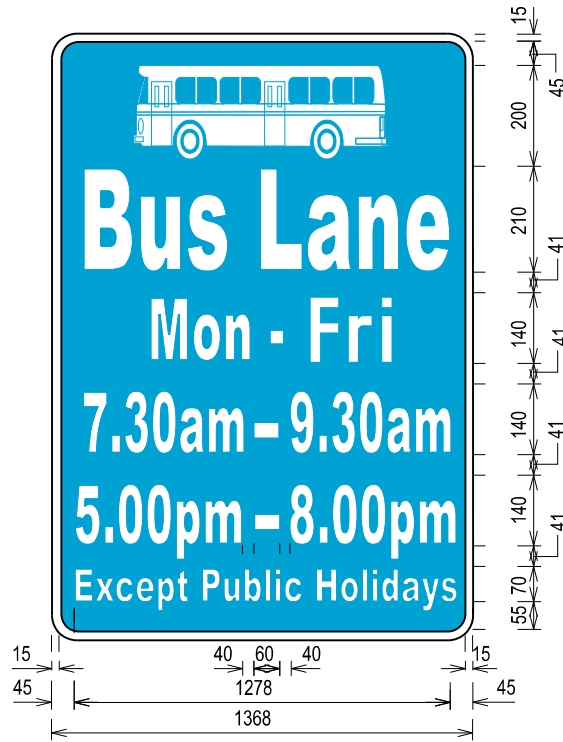


BUS LANE (NORMAL)
SCALE 1:15




ONE WAY STREET TO LEFT
SCALE 1:10

THIS SIGN INFORMS MOTORISTS OF THE ONE WAY MOVEMENT TO THE LEFT ALONG THE ROAD AHEAD. THIS SIGN MAY BE USED AT A T-JUNCTION WHERE THE FLOW ALONG THE STRAIGHT-THROUGH ROUTE IS ONE WAY.

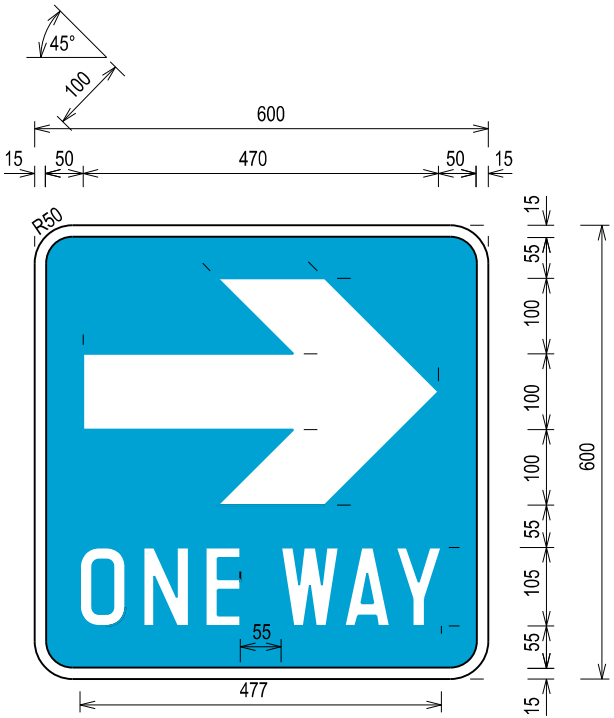


ONE WAY STREET TO RIGHT
SCALE 1:10

THIS SIGN INFORMS MOTORISTS OF THE ONE WAY TRAFFIC MOVEMENT TO THE RIGHT ALONG THE ROAD AHEAD. THIS SIGN MAY BE USED AT A T-JUNCTION WHERE THE FLOW ALONG THE STRAIGHT-THROUGH ROUTE IS ONE WAY.

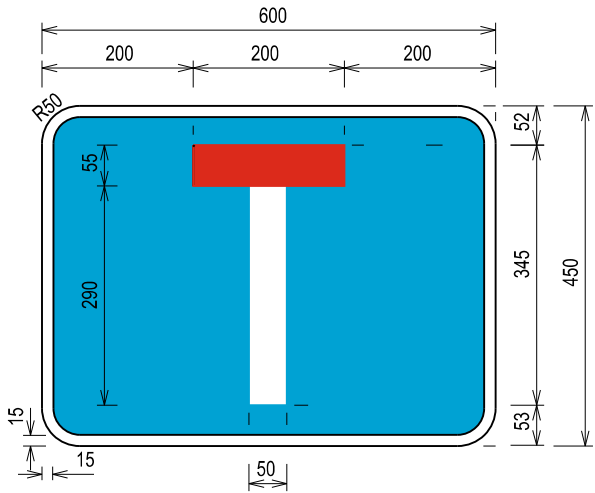


NO THROUGH ROAD
SCALE 1:10

THIS SIGN IS PLACED AT THE ENTRY TO A ROAD AND INFORMS MOTORISTS THAT THIS IS NO THROUGH ROAD.

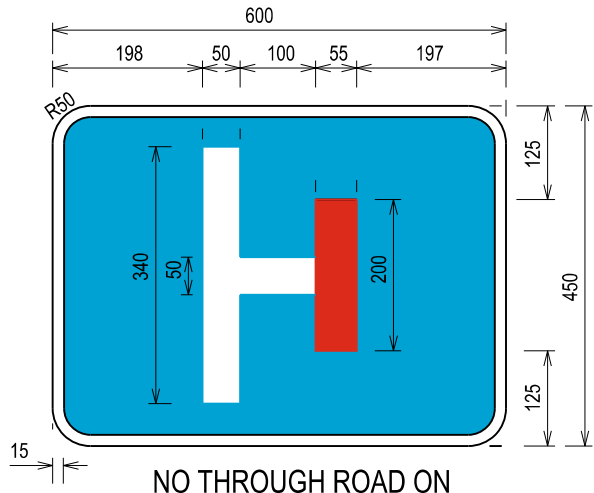

**NO THROUGH ROAD ON
SIDE ROAD TO RIGHT**
SCALE 1:10


THIS SIGN GIVES ADVANCE INFORMATION OF A NO THROUGH ROAD ON SIDE ROAD TO THE RIGHT.

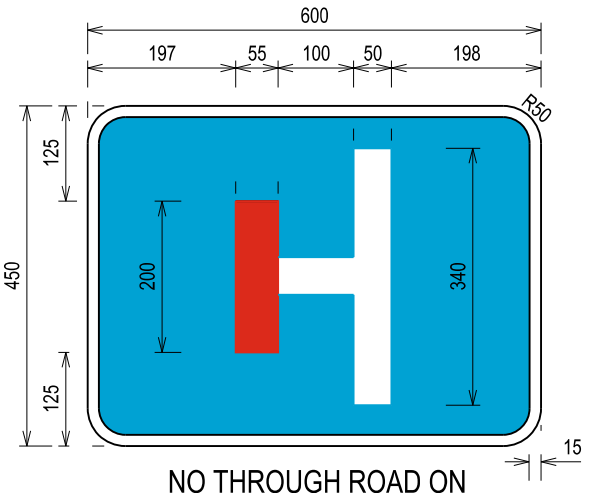

**NO THROUGH ROAD ON
SIDE ROAD TO LEFT**
SCALE 1:10


THIS SIGN GIVES ADVANCE INFORMATION OF A NO THROUGH ROAD ON SIDE ROAD TO THE LEFT.

--	--	

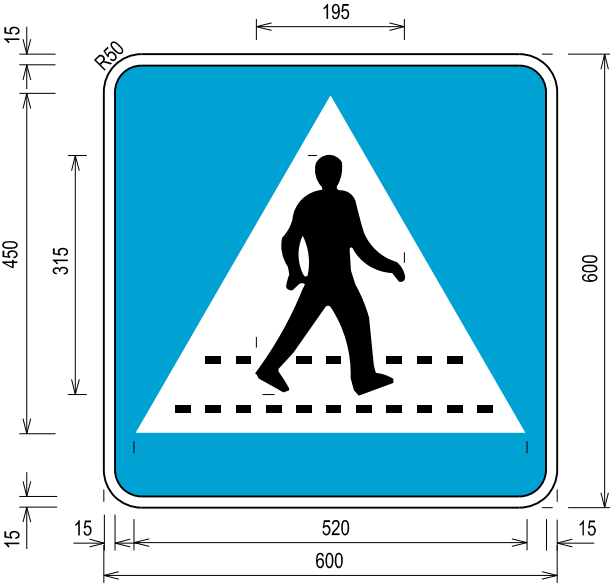


PEDESTRIAN CROSSING

THIS SIGN INDICATES TO PEDESTRIANS AND MOTORISTS THE POSITION OF A DESIGNATED PEDESTRIAN CROSSING.

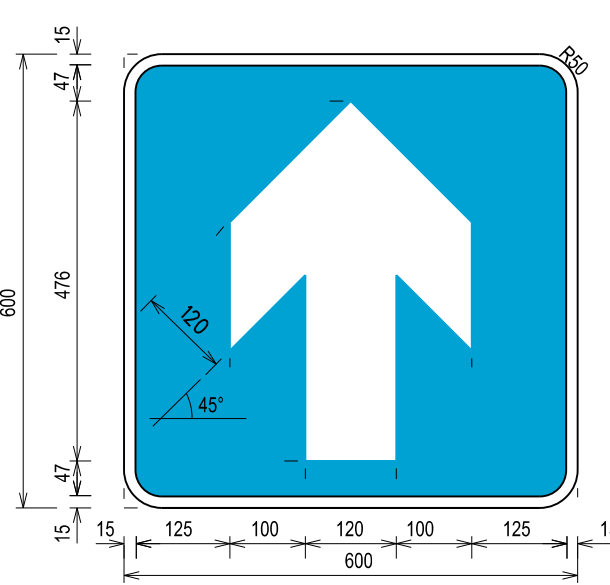


ONE WAY TRAFFIC

THIS SIGN INFORMS MOTORISTS OF THE DIRECTION OF PERMITTED TRAFFIC FLOW ON A ONE WAY STREET. IT MAY BE PLACED AT THE ENTRY TO A ONE WAY STREET OR AT APPROPRIATE LOCATIONS ALONG A ONE WAY STREET.

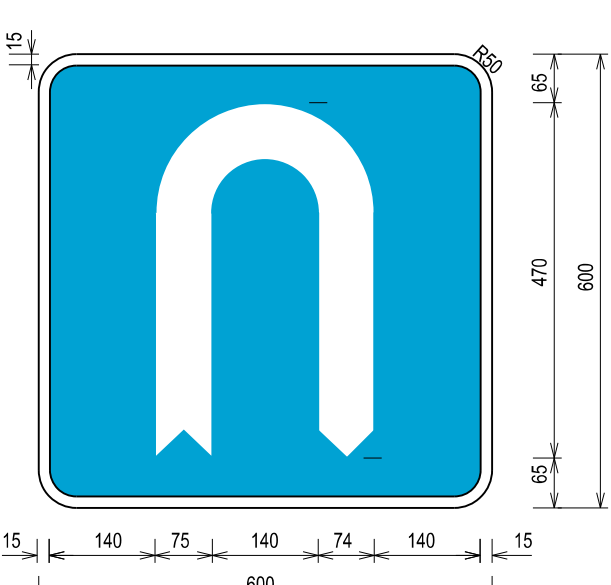

U-TURN


THIS SIGN INFORMS MOTORISTS OF A U TURN FACILITY AHEAD. MOTORISTS ARE PROHIBITED FROM EXECUTING U-TURNS AT ALL ROAD INTERSECTIONS AND ARE PERMITTED ONLY BY THE DISPLAY OF THIS SIGN.

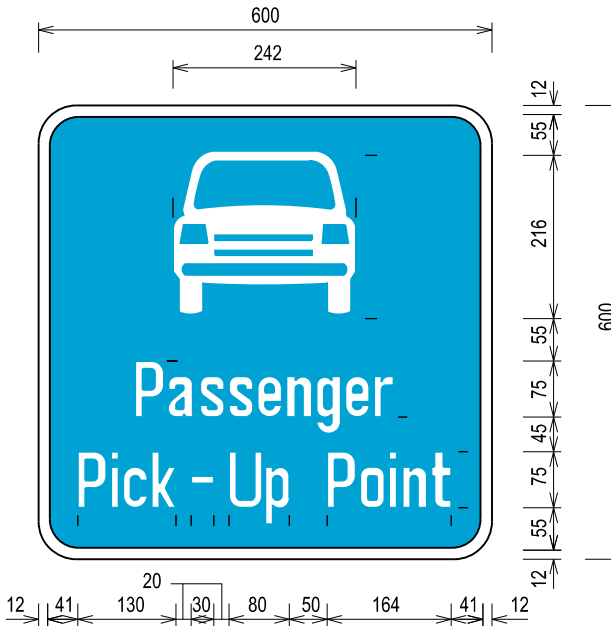

PASSENGER PICK-UP POINT


THIS SIGN INDICATES A DESIGNATED PICK-UP / DROP OFF POINT FOR PASSENGERS OF VEHICLES.

STANDARD DETAIL		Land Transport Authority	
TRAFFIC INFORMATORY SIGNS (SHEET 2 OF 19)	DRAWING NO. LTA/SDRE14/18/TFI2		REV. B
	DATE OF ISSUE 1st APR 2014	SCALE 1:10	SHEET NO. 2 OF 19
B	APR 2024		
A	OCT 2015		
REV.	DATE		

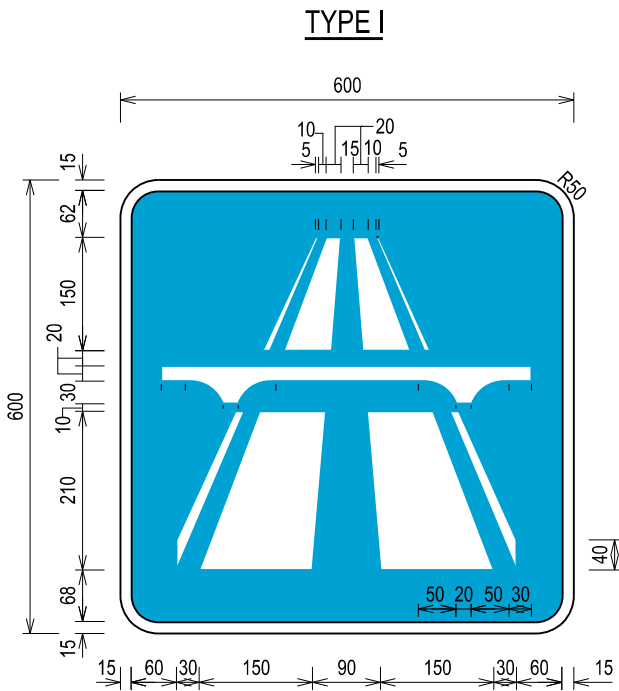

START OF EXPRESSWAY

THIS SIGN INDICATES THE START OF AN EXPRESSWAY. MOTORISTS HAVE TO OBEY THE TRAFFIC RULES THAT APPLY TO EXPRESSWAY BEYOND THIS POINT. THIS SIGN IS NORMALLY PLACED AT ENTRANCE TO EXPRESSWAY.

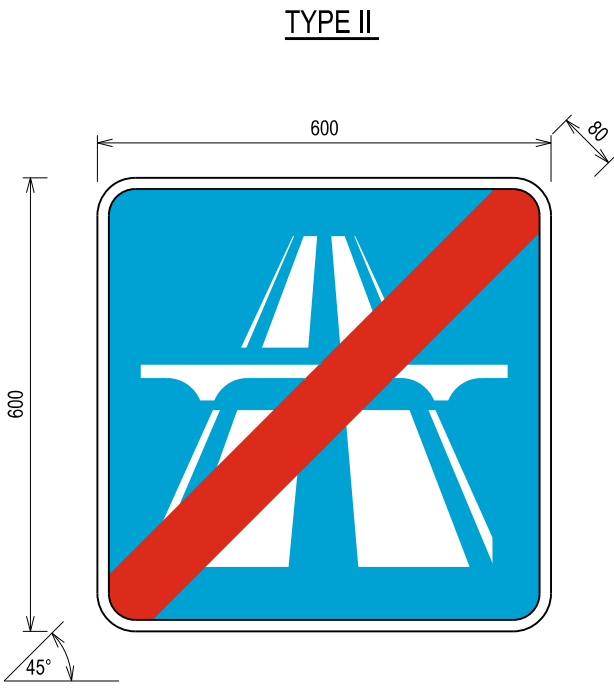


END OF EXPRESSWAY


THIS SIGN IS PLACED AT THE EXIT OF EXPRESSWAY. MOTORISTS ARE EXPECTED TO REDUCE THEIR SPEED ACCORDINGLY.

	</
--	--	----


TYPE I

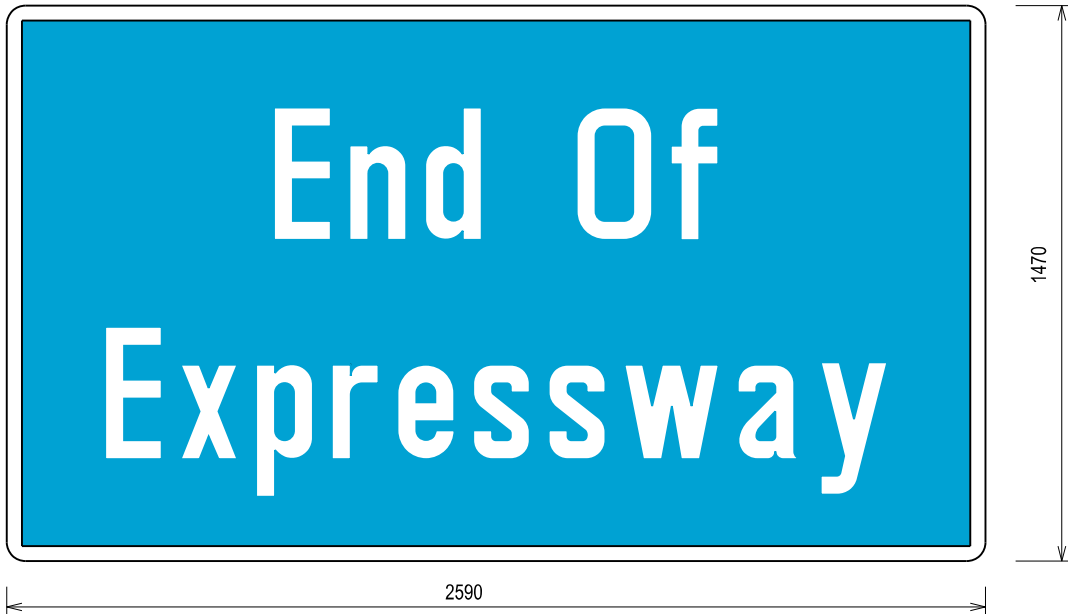


THIS SIGN IS PLACED AT THE END OF EXPRESSWAY.

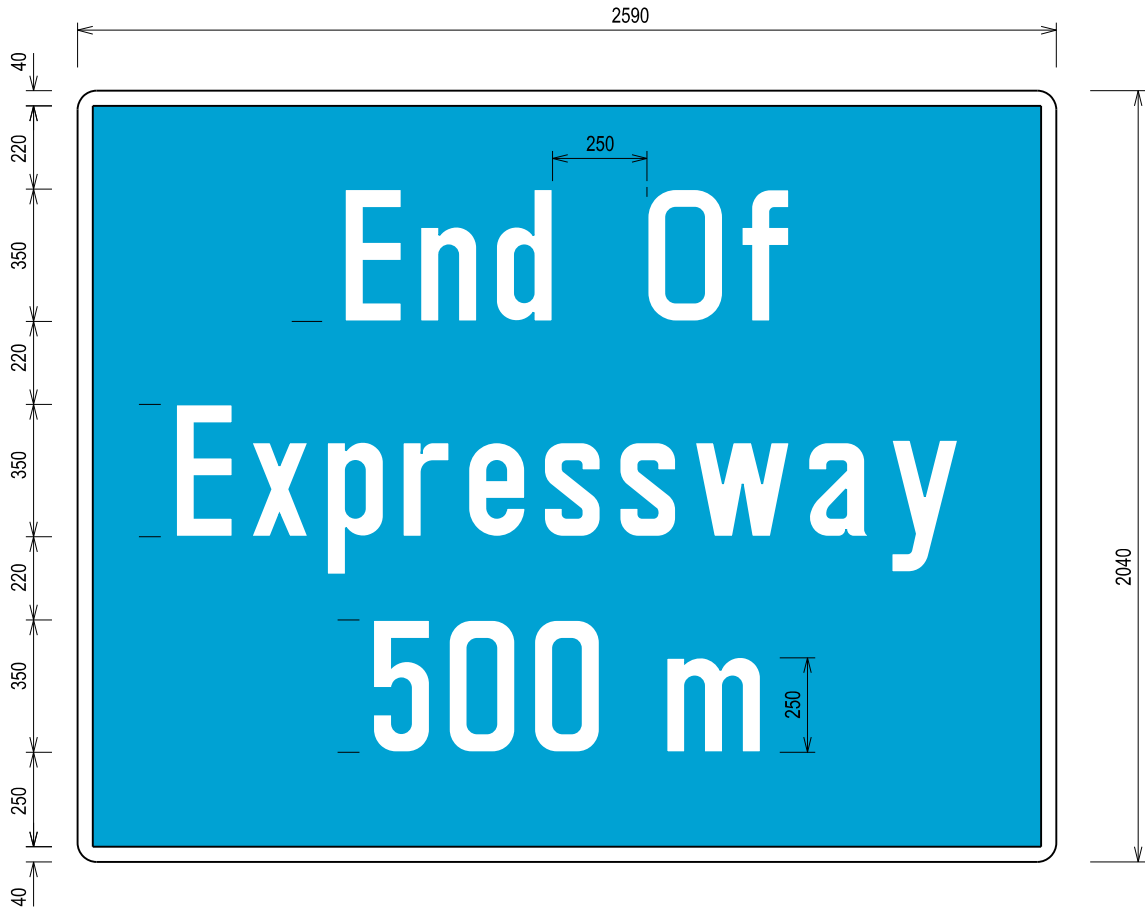

THIS SIGN GIVES ADVANCE INFORMATION OF THE END OF EXPRESSWAY AHEAD.

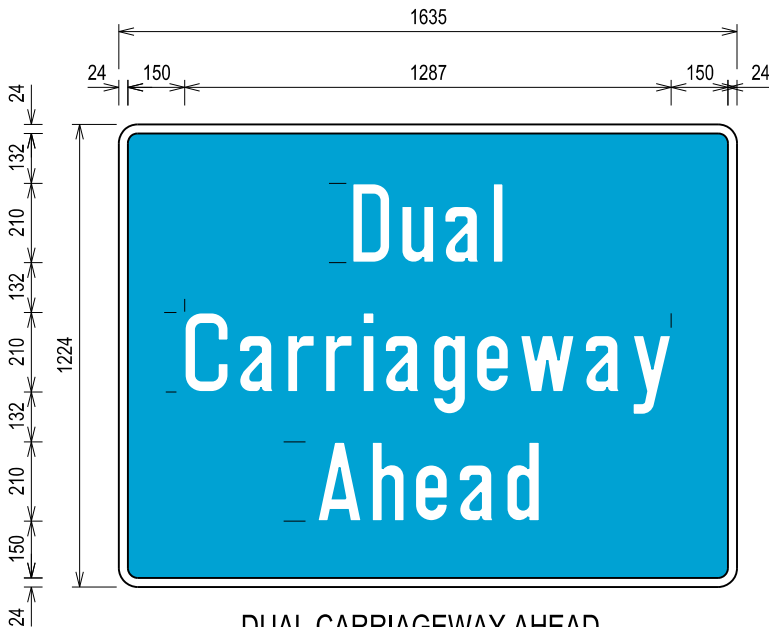

DUAL CARRIAGEWAY AHEAD

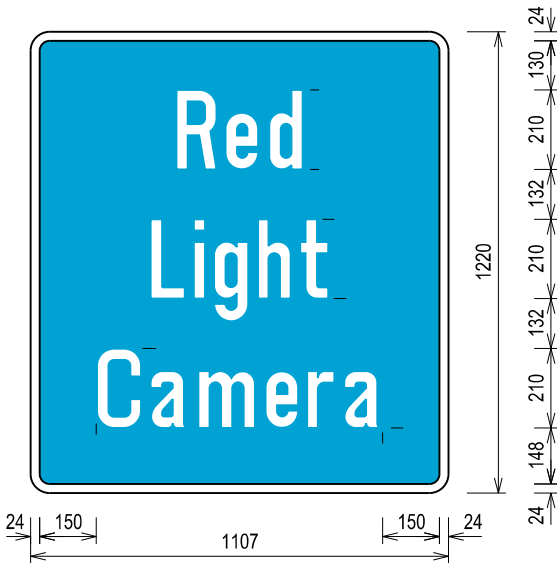


RED LIGHT CAMERA SIGN

THIS SIGN INFORMS MOTORISTS OF THE PRESENCE OF A RED LIGHT CAMERA SYSTEM AT THE SET OF TRAFFIC SIGNALS AHEAD. THE RED LIGHT CAMERA SYSTEM IS ACTIVATED WHEN A VEHICLE BEATS THE RED LIGHT. A PHOTOGRAPH OF THE OFFENDING VEHICLE IS THEN RECORDED.




KEEP LEFT UNLESS OVERTAKING

STANDARD		DETAIL		Land Transport Authority	
TRAFFIC INFORMATORY		SIGNALS		DRAWING NO.	REV.
(SHEET 4 OF 19)				LTA/SDRE14/18/TFI4	A
A		APR 2024		DATE OF ISSUE	SHEET NO.
REV.		DATE		1st APR 2014	4 OF 19
				SCALE	
				1:20	

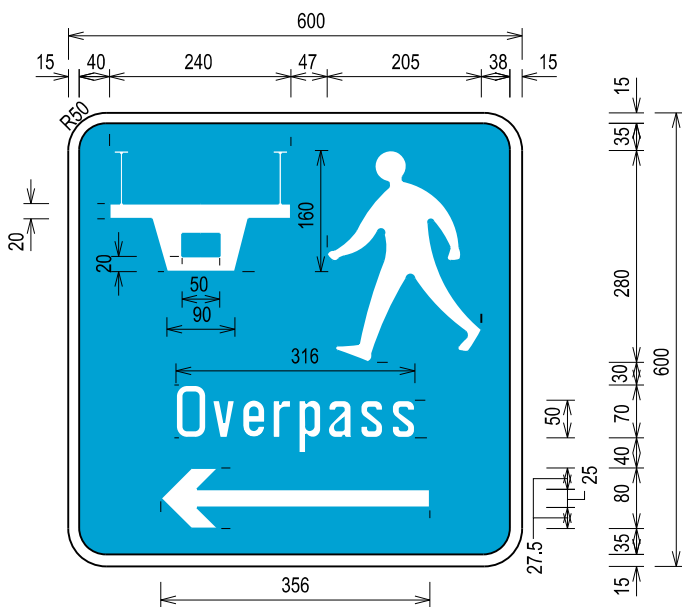


OVERPASS

THIS SIGN INFORMS PEDESTRIAN ON THE LOCATION OF AN OVERPASS.

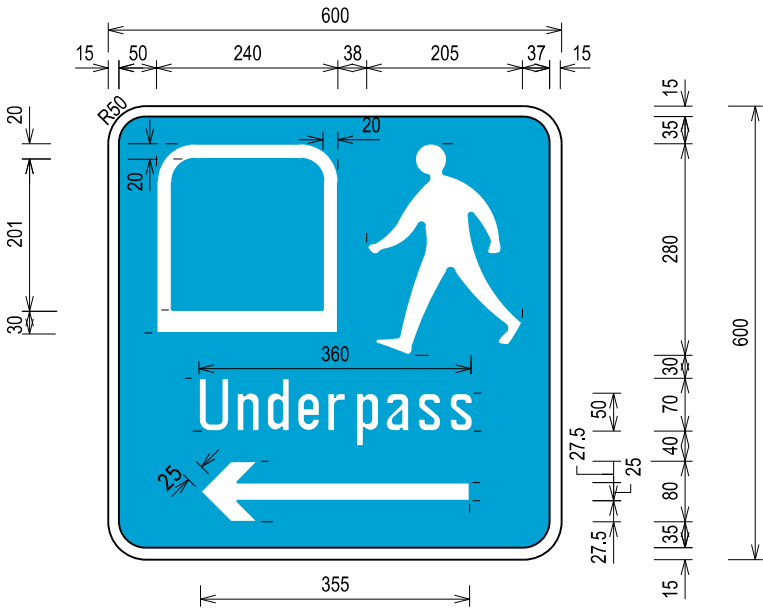


UNDERPASS

THIS SIGN INFORMS PEDESTRIAN ON THE LOCATION OF AN UNDERPASS.

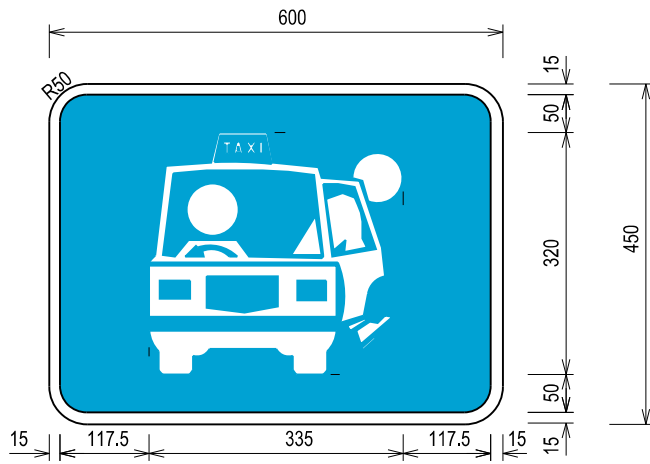

TAXI DROP-OFF POINT


THIS SIGN INDICATES A DESIGNATED DROP-OFF POINT FOR TAXIS. NO PASSENGERS ARE PERMITTED TO BOARD TAXIS HERE.

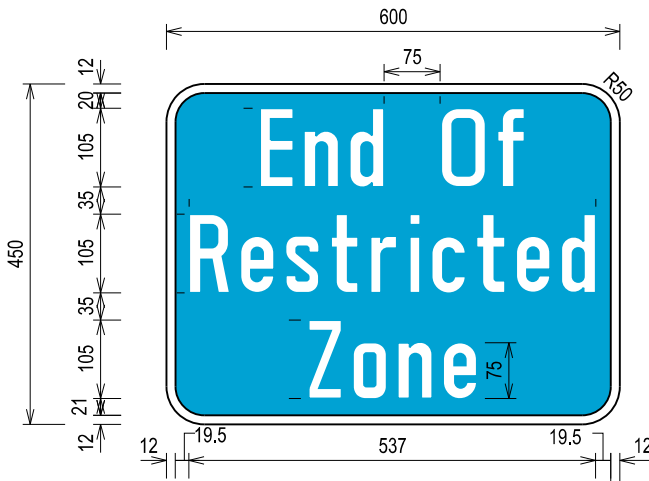


END OF RESTRICTED ZONE

THIS SIGN INFORMS MOTORISTS THAT THEY ARE MOVING OUT OF THE RESTRICTED ZONE.


--	--	

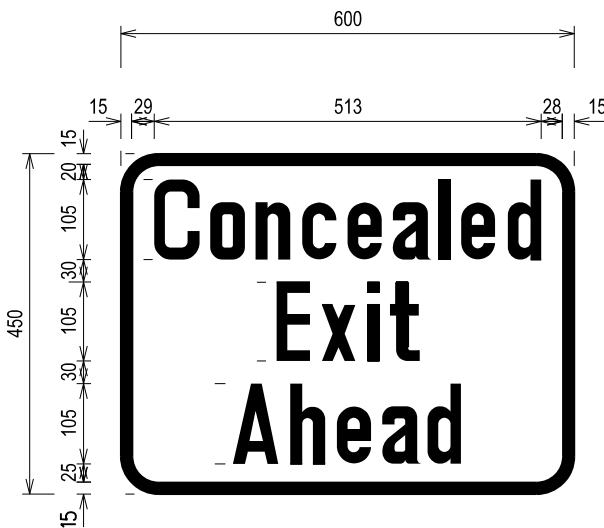


CONCEALED EXIT AHEAD
THIS SIGN ADVISES MOTORISTS OF A CONCEALED EXIT AHEAD.

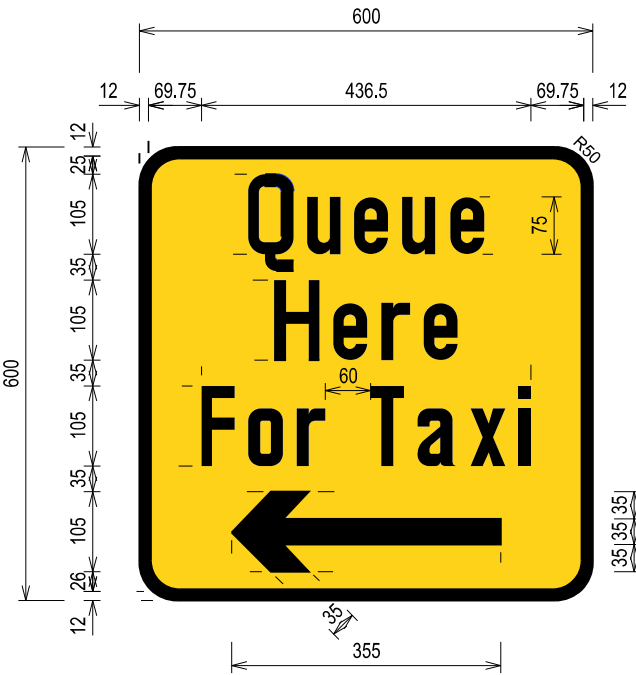


QUEUE HERE FOR TAXI
THIS SIGN INFORMS TAXI COMMUTERS TO QUEUE AT THIS LOCATION TO BOARD TAXIS.

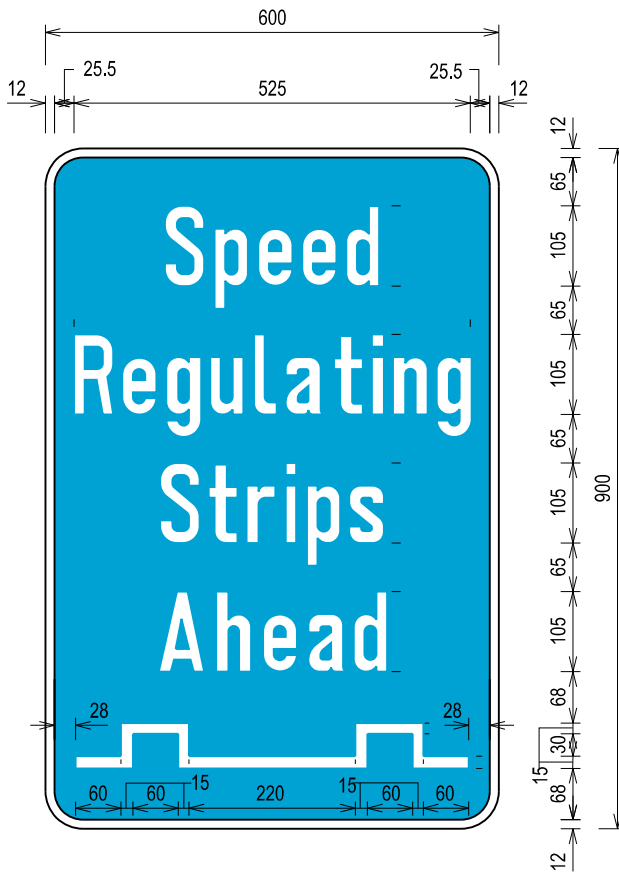

SPEED REGULATING STRIPS AHEAD
THIS SIGN ADVISES MOTORISTS OF THE PRESENCE OF SPEED REGULATING STRIPS AHEAD. SPEED REGULATING STRIPS ARE USED TO SLOW DOWN VEHICLES AT LOCATIONS WHERE IT IS INADVISABLE TO TRAVEL AT A HIGH SPEED.

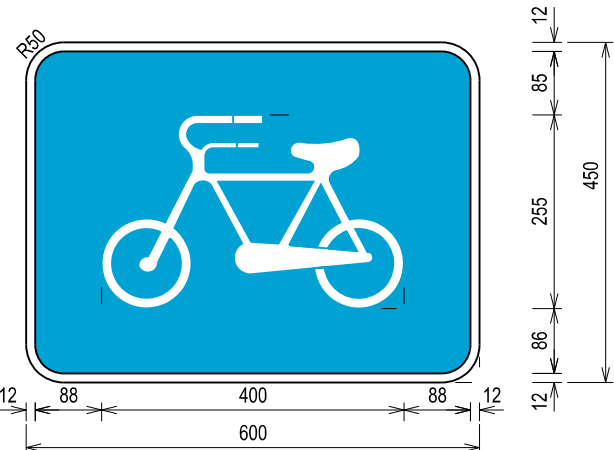

BICYCLES STAND
THIS SIGN INDICATES A BICYCLE STAND.

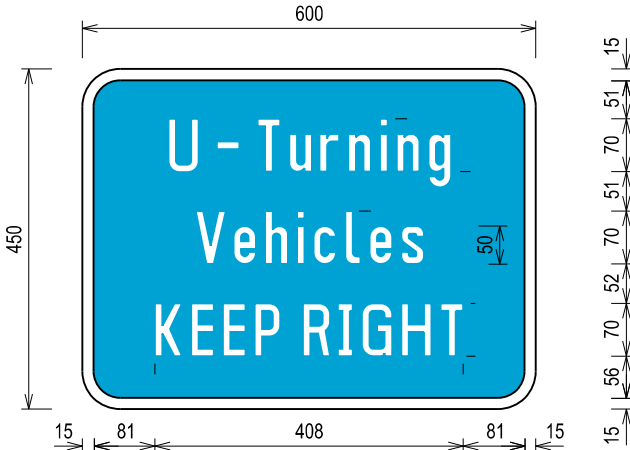

U-TURNING VEHICLES KEEP RIGHT
THIS SIGN ADVISES U-TURNING VEHICLES TO KEEP TO THE RIGHT LANE SO THAT THE U-TURNING MANOEUVRE MAY BE SAFELY MADE.


STANDARD DETAIL		Land Transport Authority	
TRAFFIC INFORMATORY SIGNS (SHEET 6 OF 19)		DRAWING NO. LTA/SDRE14/18/TFI6	REV. A
REV.	DATE	DATE OF ISSUE 1st APR 2014	SCALE 1:10
		SHEET NO. 6 OF 19	



NO PARKING OF BICYCLES

SCALE 1:10


THIS SIGN INFORMS CYCLISTS OF THE PROHIBITION OF PARKING BICYCLES AT PLACES DISPLAYING THIS SIGN.

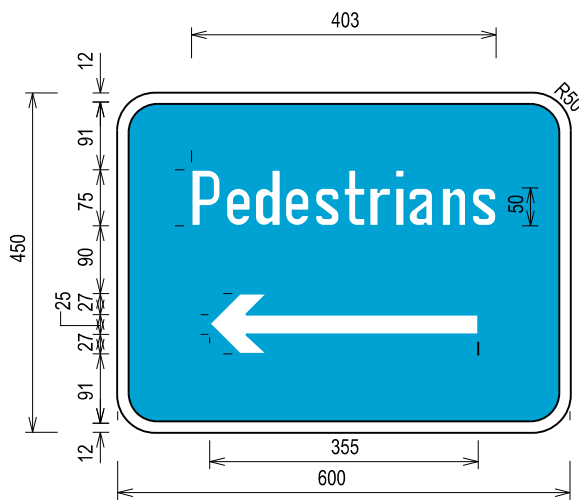

DIRECTION OF TEMPORARY PEDESTRIAN ROUTE


SCALE 1:10

THIS SIGN ADVISES PEDESTRIANS THAT THE TEMPORARY FOOTWAYS IS TO THE LEFT. THE ARROW MAY BE REVERSED OR A DOUBLE HEADED ARROW MAY BE USED TO ADVISE OF A TEMPORARY FOOTWAY TO THE RIGHT OR TO THE LEFT AND RIGHT RESPECTIVELY.

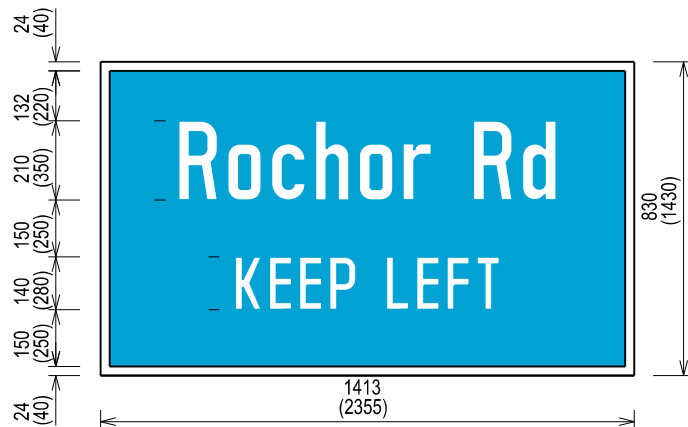

ROCHOR RD, KEEP LEFT


SCALE 1:20

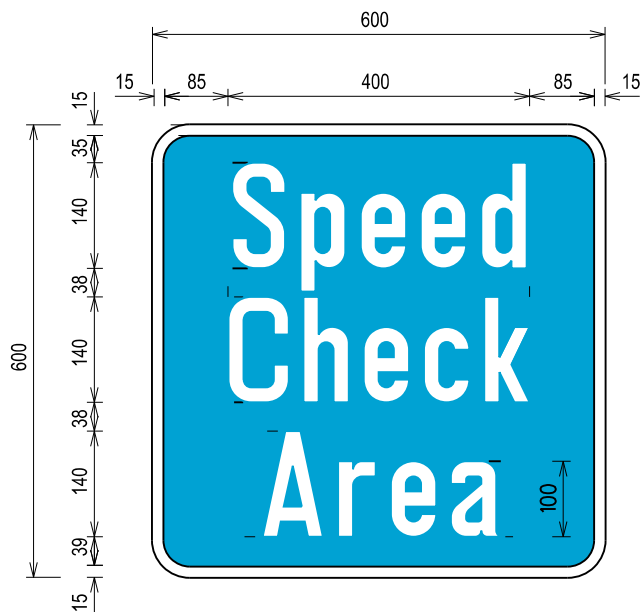

SPEED CHECK AREA

SCALE 1:10


THIS SIGN INFORMS MOTORISTS OF THE POSSIBILITY OF A SPEED CHECK AHEAD.

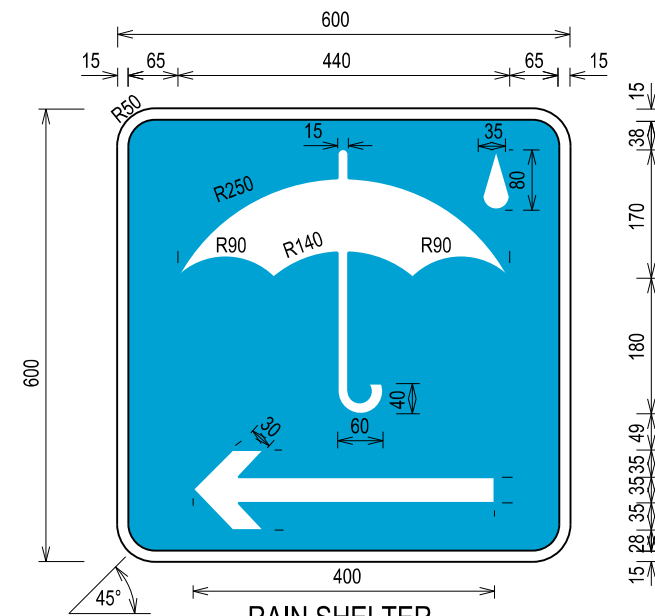

RAIN SHELTER


SCALE 1:10

THIS SIGN INFORMS MOTOR CYCLISTS / CYCLISTS ON THE LOCATION OF A RAIN SHELTER.

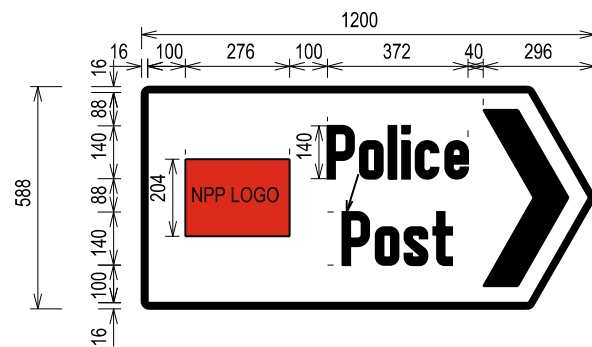

POLICE POST


SCALE 1:20

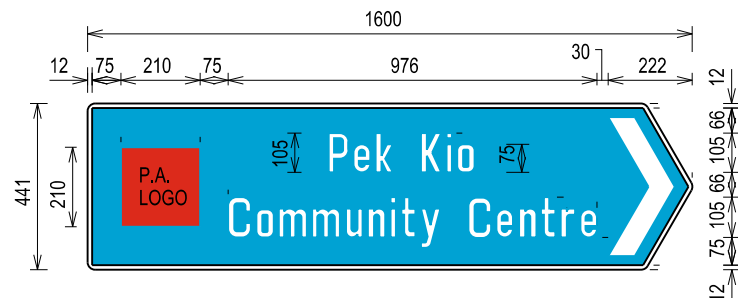


COMMUNITY CENTRE


SCALE 1:20

--	--	

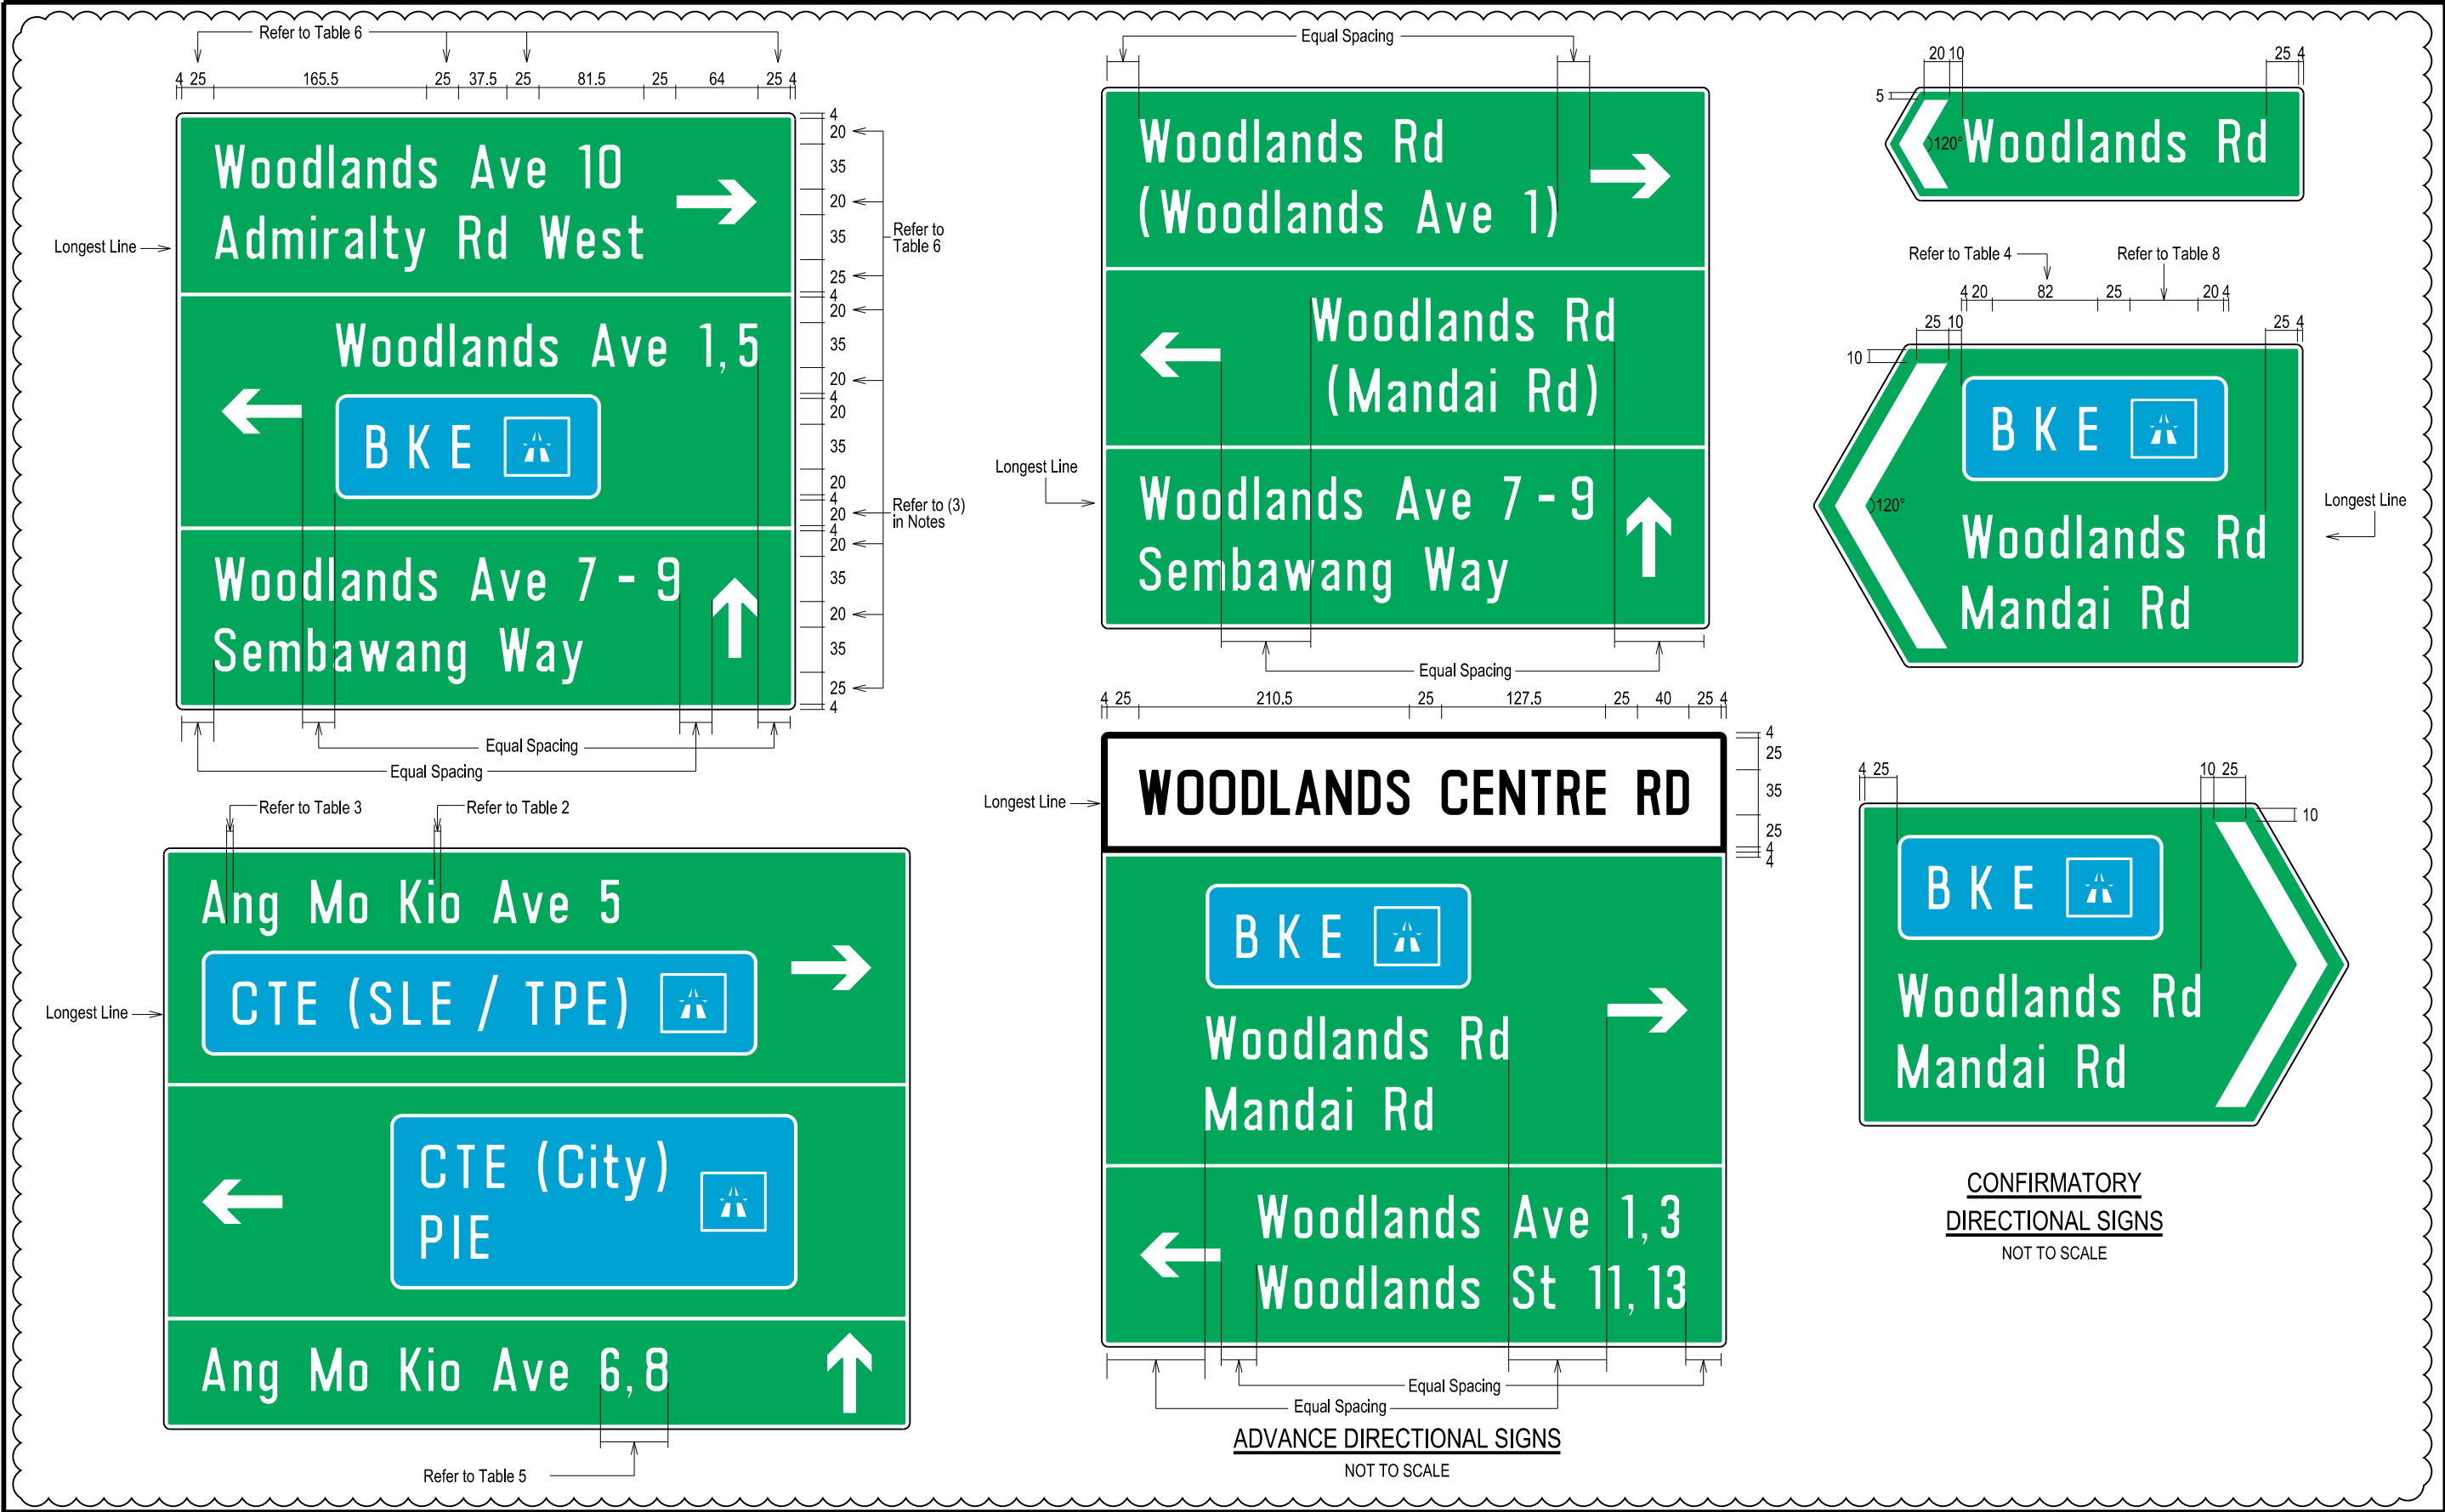

NOTES: 1. Logo of expressway shall always be on the right of the sign regardless of the arrow direction. Refer to SDRE Chapter 7 Table 8 for the absolute size of the logo. Multiplication factor should not be applied to them. 2. All dimensions are in Factor 1 unless otherwise stated. 3. If the expressway legend blue box is at the bottom line, the space between the blue box and the bottom border is 20mm multiply by Factor. 4. The longest line (including arrow) in the sign will determine the overall width of the sign.		5. Arrow placement for different direction should be placed in an alternate manner. 6. For confirmatory sign, arrow width and spacing between arrow and border is narrower for one liner only sign. 7. For confirmatory sign, legends are always left aligned regardless of the sign direction. 8. All references are made to SDRE Chapter 7 Directional Signs.		STANDARD DETAIL TRAFFIC INFORMATORY SIGNS (SHEET 8 OF 19)		Land Transport Authority DRAWING NO. LTA/SDRE14/18/TFI8 DATE OF ISSUE 1st APR 2014 SCALE AS SHOWN SHEET NO. 8 OF 19	
A		APR 2024		REV.		REV. A	
REV.		DATE					

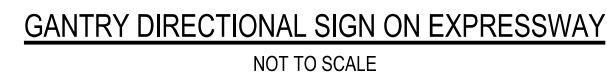

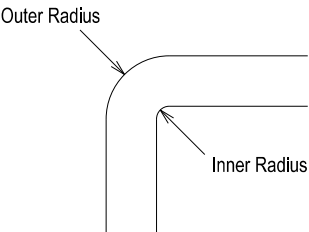

Corner Radii of the 'A' and 'B'

Font Factor	Outer Radius (mm)	Inner Radius (mm)
4	50	34
6	50	26
10	50	10
12	50	2

Note: 'B' is applicable only in factor 6 for signs in factor 10 and 12



Sample in font factor 6



Sample in font factor 10



Sample in font factor 12

Corner Radii 'C' of the Blue Box for Expressway Legend

Font Factor	Outer Radius (mm)	Inner Radius (mm)
6	60	36
10	100	60
12	120	72

Note: Legend / content shown on the sign is just for illustration purposes only

NOTES:

1. Logo of expressway shall always be on the right of the sign regardless of the arrow direction. Refer to SDRE Chapter 7 Table 8 for the absolute size of the logo. Multiplication factor should not be applied to them.
2. All dimensions are in Factor 1 unless otherwise stated.
3. If the expressway legend blue box is at the bottom line, the space between the blue box and the bottom border is 20mm multiply by Factor.
4. The longest line (including arrow) in the sign will determine the overall width of the sign.




5. Numbers in brackets are alternative dimensions to be used if necessary, such as space constraint etc.
6. For confirmatory sign, arrow width and spacing between arrow and border is narrower for one liner only sign.
7. For confirmatory sign, legends are always left aligned regardless of the sign direction.
8. All references are made to SDRE Chapter 7 Directional Signs.

STANDARD DETAIL

TRAFFIC INFORMATORY
SIGNS
(SHEET 10 OF 19)

Land Transport Authority

DRAWING NO. LTA/SDRE14/18/TFI10		REV. A
DATE OF ISSUE 1st APR 2014	SCALE AS SHOWN	SHEET NO. 10 OF 19

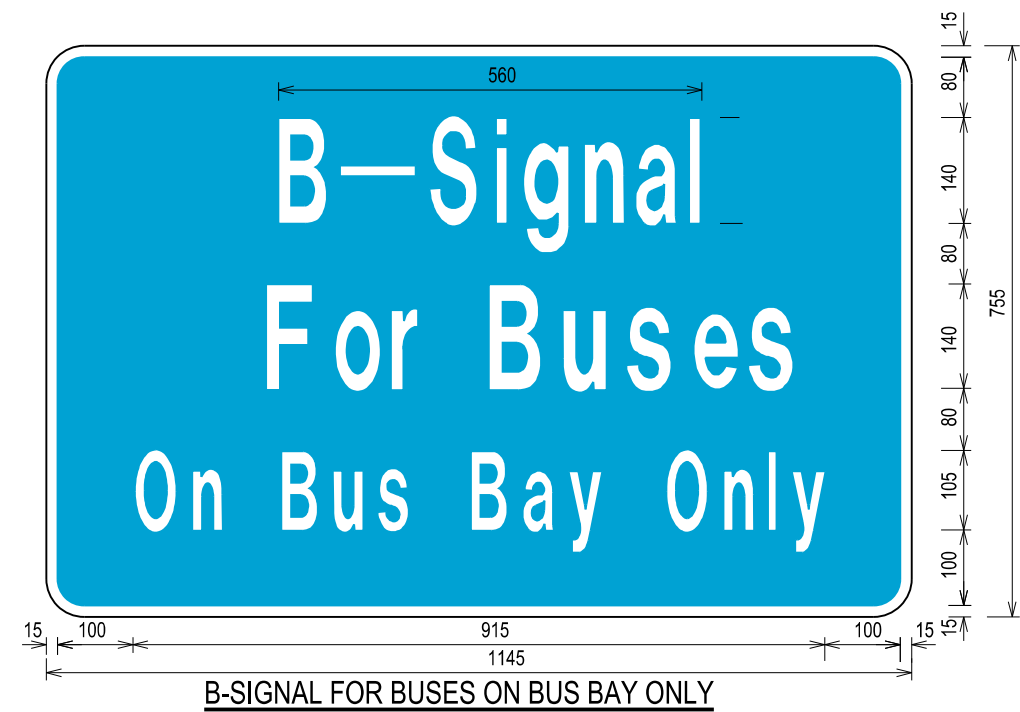
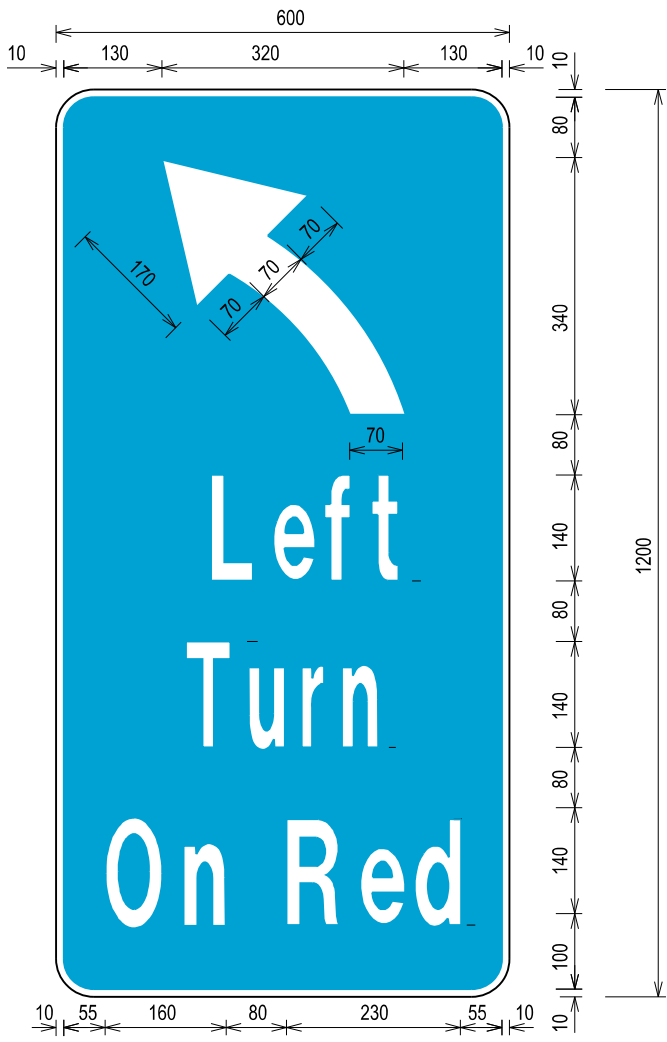
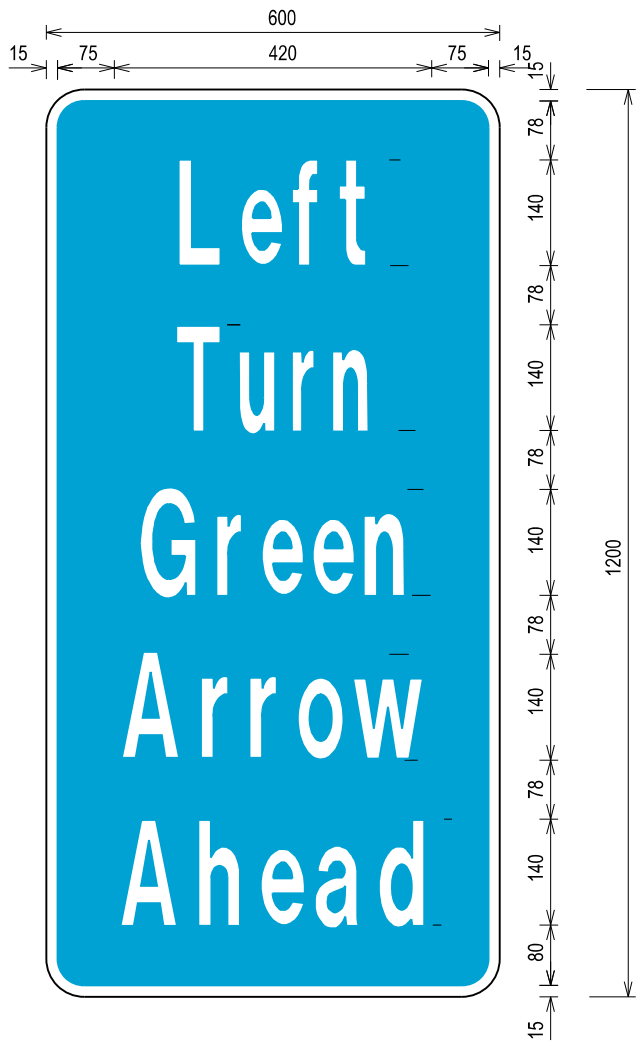


B-SIGNAL FOR BUSES ON BUS BAY ONLY




B-SIGNAL FOR BUSES ON LEFT MOST LANE ONLY

STANDARD DETAIL		Land Transport Authority	
TRAFFIC INFORMATORY SIGNS (SHEET 11 OF 19)	DRAWING NO. LTA/SDRE 14/18/TF11		REV. A
	DATE OF ISSUE 1st APR 2014	SCALE 1:10	SHEET NO. 11 OF 19
	REV. DATE		

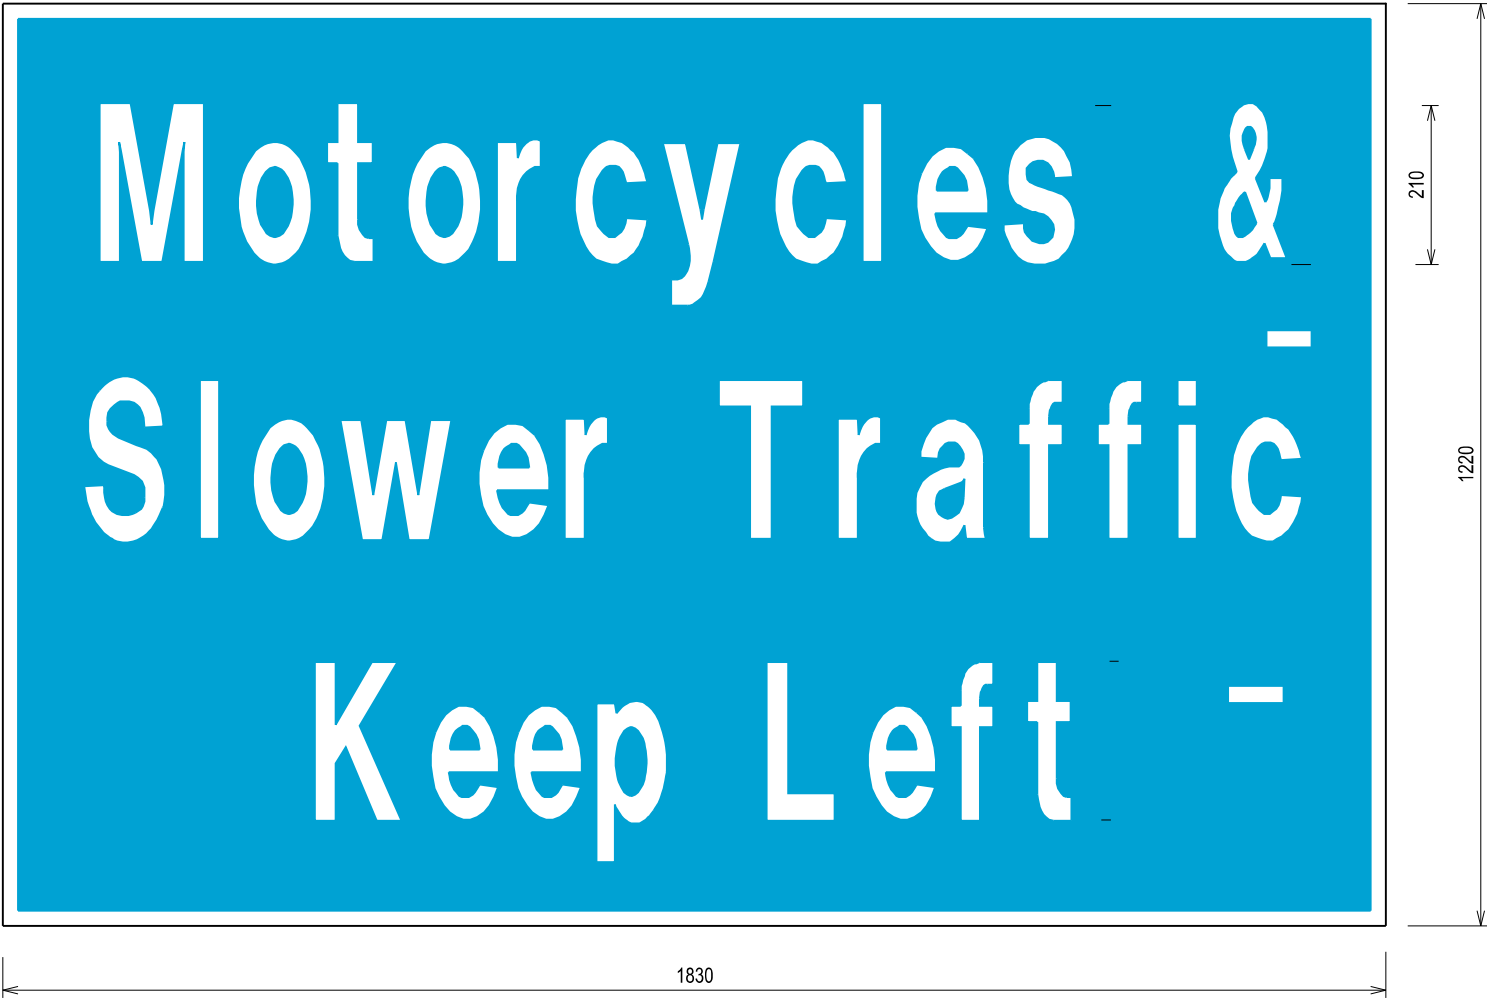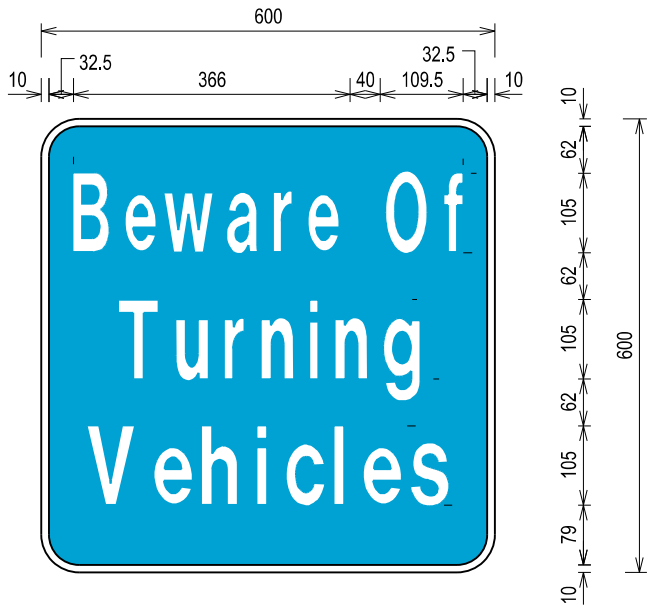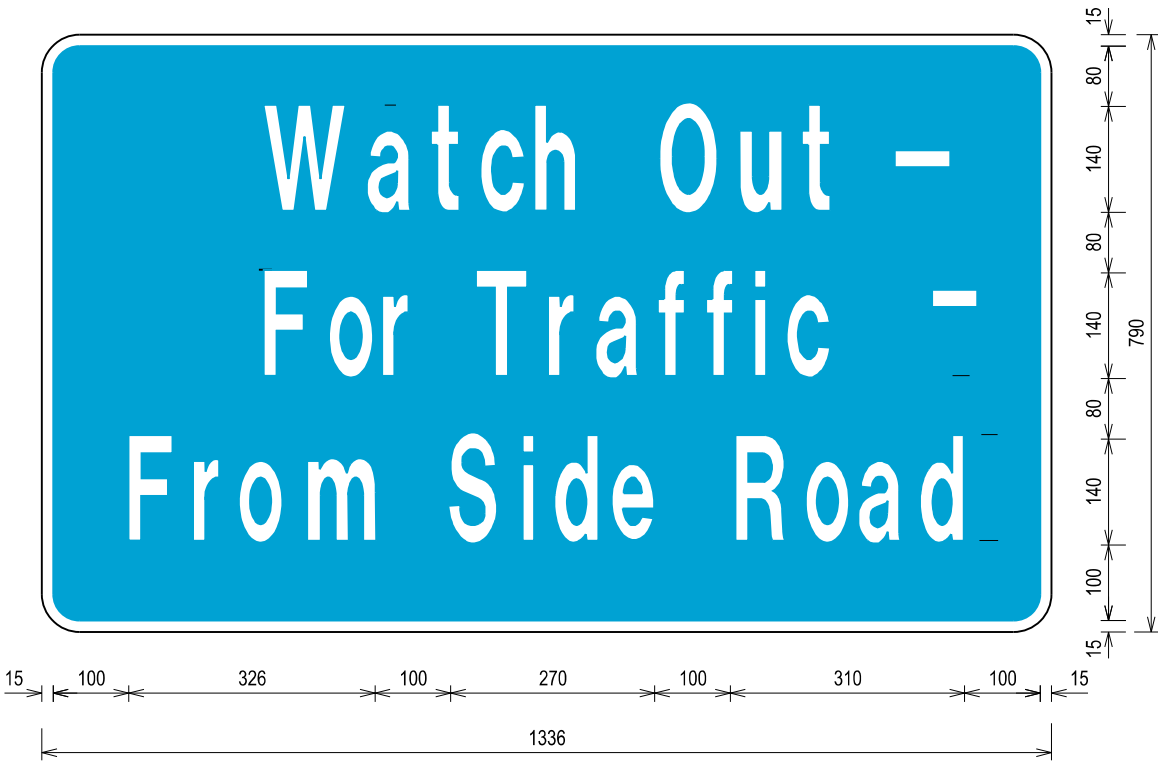


--	--	

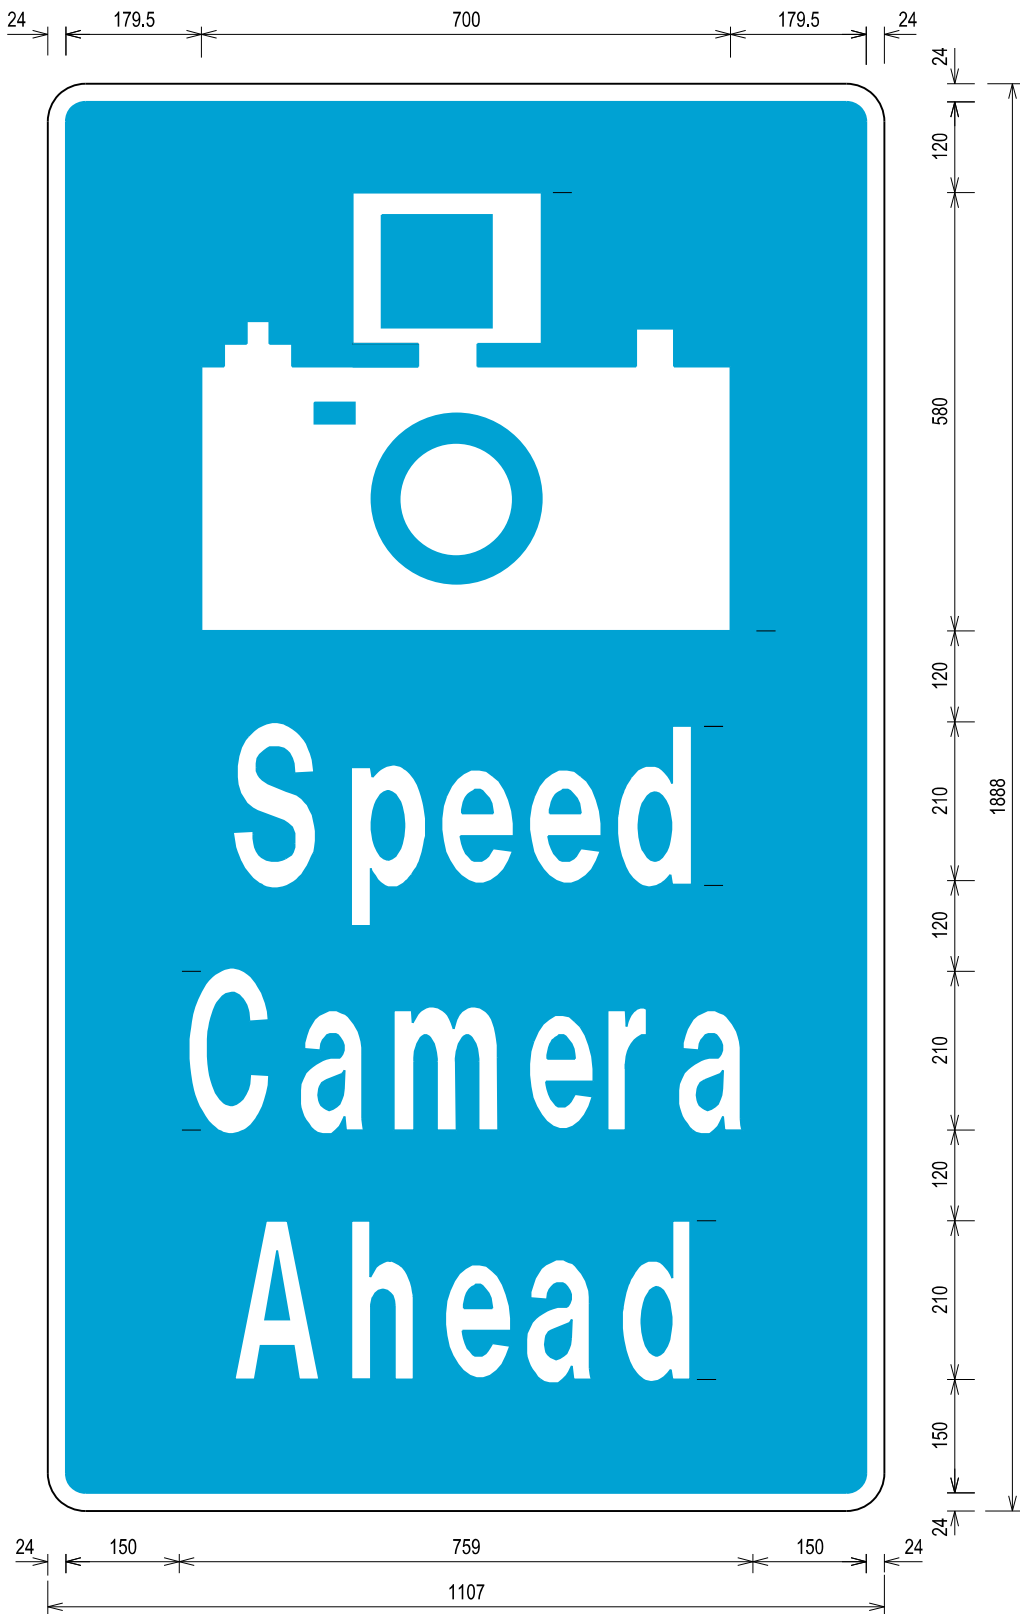


STANDARD DETAIL		Land Transport Authority	
TRAFFIC INFORMATORY SIGNS (SHEET 13 OF 19)		DRAWING NO. LTA/SDRE14/18/TFI13	REV. A
REV. A	APR 2024	DATE OF ISSUE 1st APR 2014	SCALE 1:100
SHEET NO. 13 OF 19			




8-14

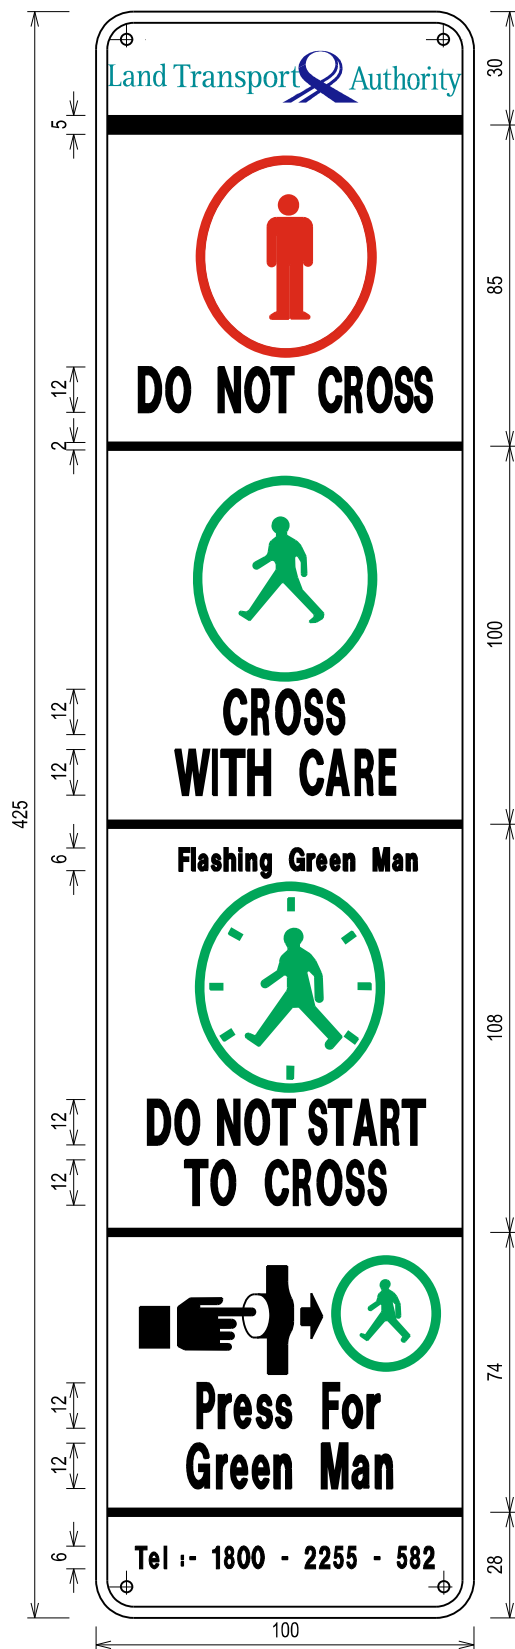

NOTE: - POSITION OF RIVETS
425mm X 100mm
SCALE 1:20

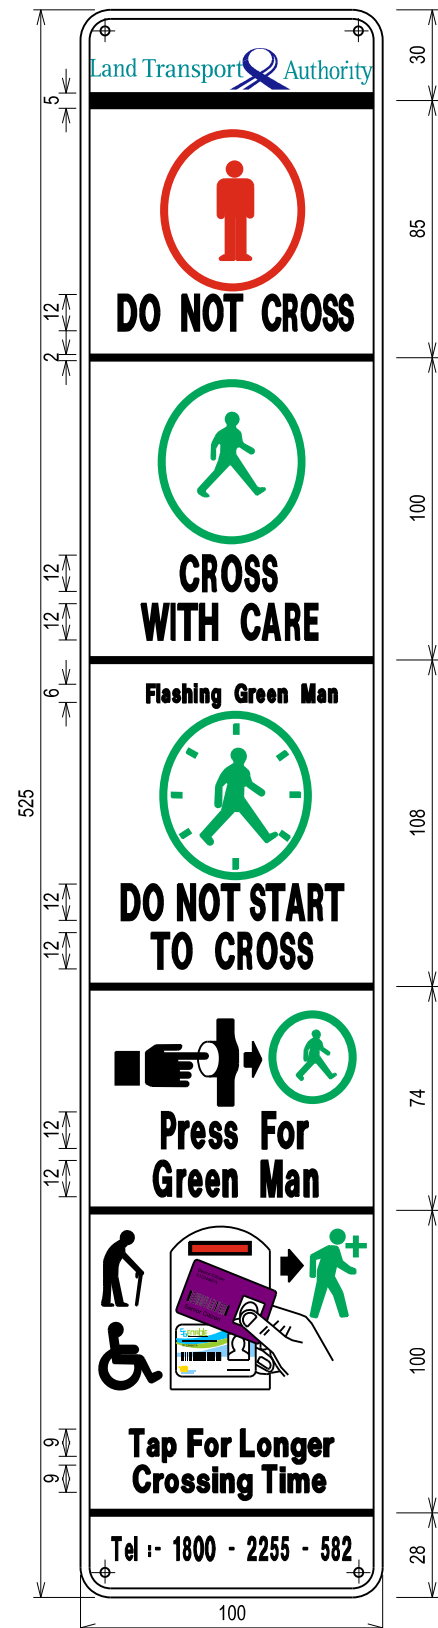


NOTE: - POSITION OF RIVETS
525mm X 100mm
SCALE 1:25

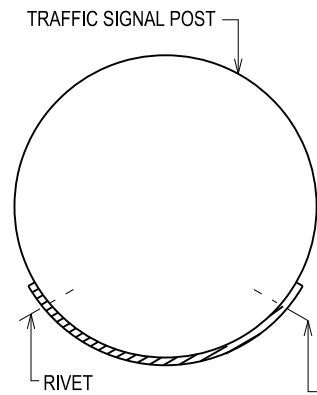


SECTION
SCALE 1:1

"WALK WITH CARE" SIGN SLIGHTY BEND
TO HUG THE POST AND RIVETED
(418 X 100)

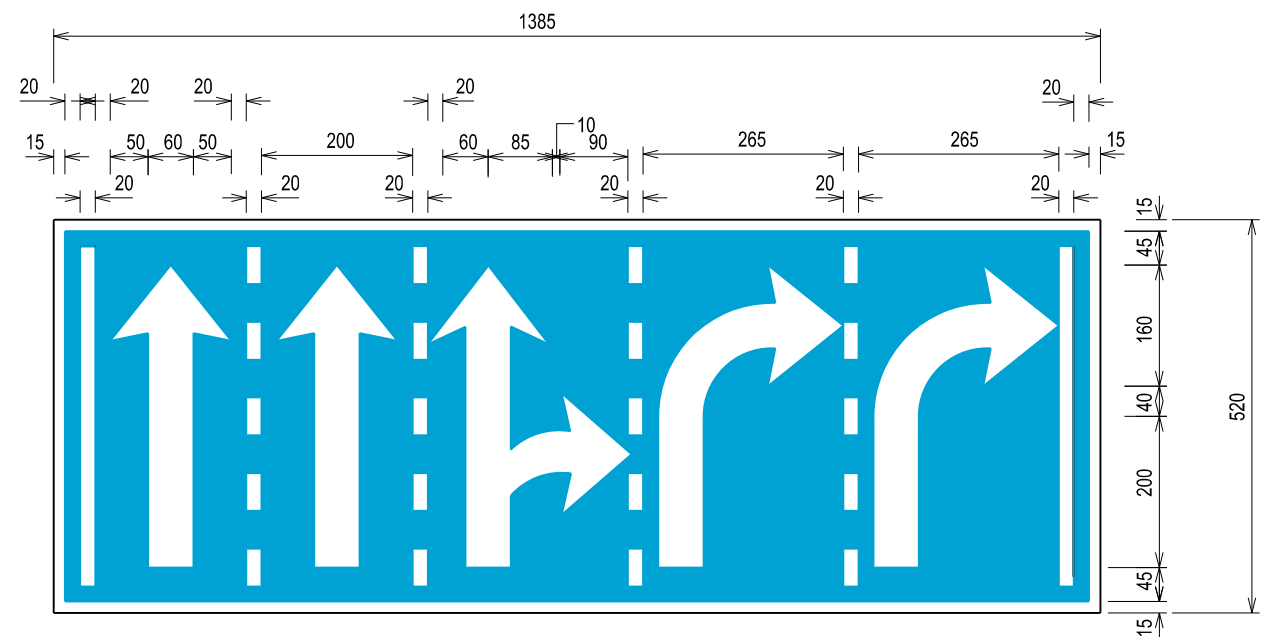

LANE INDICATION SIGN
SCALE 1:10

COLOUR CODE:
WHITE ARROW, BORDER & LANE MARKINGS ON BLUE BACKGROUND

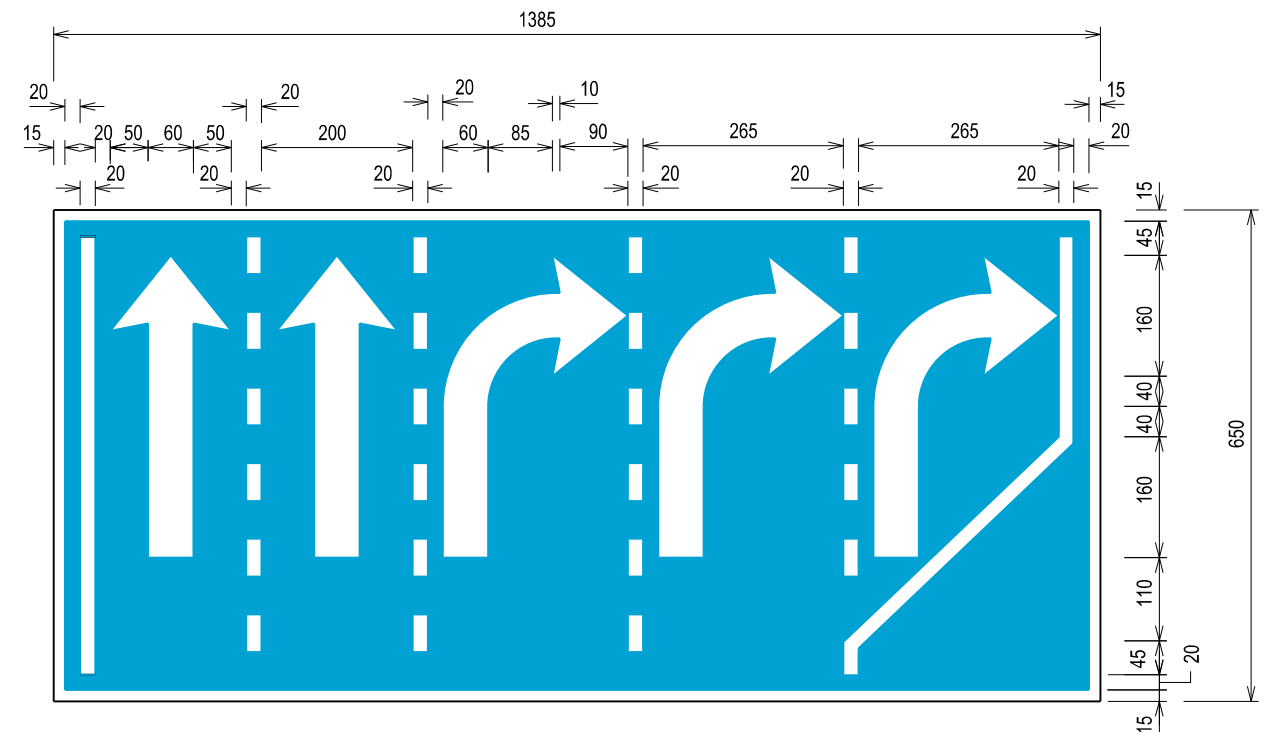

LANE INDICATION SIGN
SCALE 1:10


COLOUR CODE:
WHITE ARROW, BORDER & LANE MARKINGS ON BLUE BACKGROUND

STANDARD DETAIL

TRAFFIC INFORMATORY
SIGNS
(SHEET 15 OF 19)


Land Transport Authority

DRAWING NO.	LTA/SDRE14/18/TFI15	REV.	B
DATE OF ISSUE	1st APR 2014	SCALE	AS SHOWN
SHEET NO.	15 OF 19		

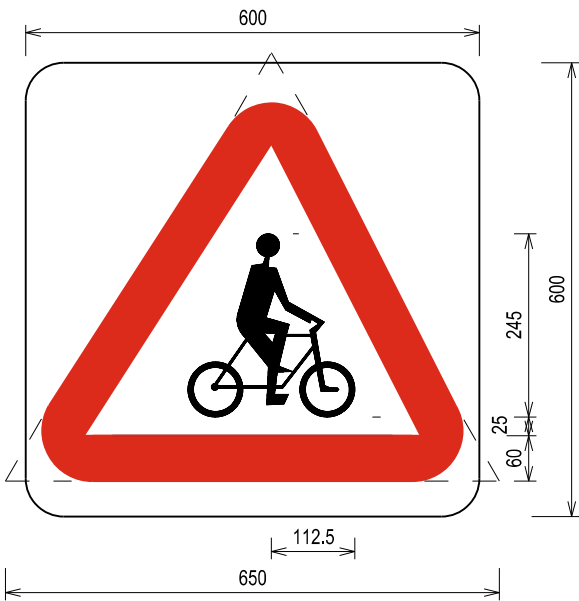


CYCLIST CROSSING AHEAD

THIS SIGN INDICATES THE APPROACH TO A CYCLIST CROSSING

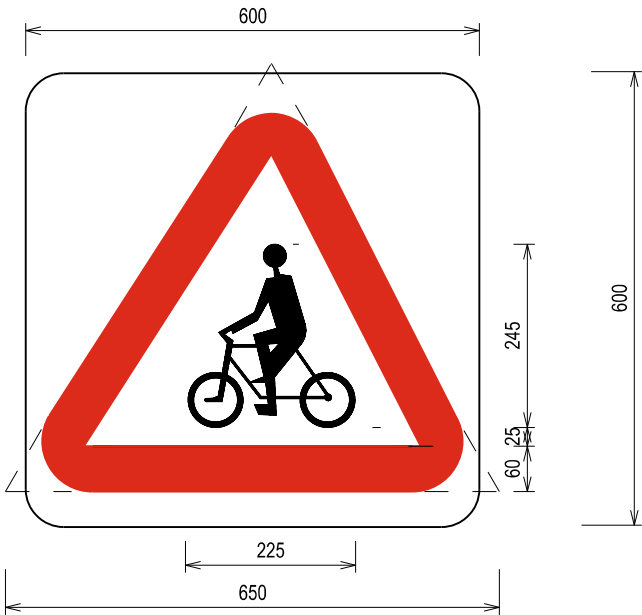


CYCLIST CROSSING AHEAD


THIS SIGN INDICATES THE APPROACH TO A CYCLIST CROSSING

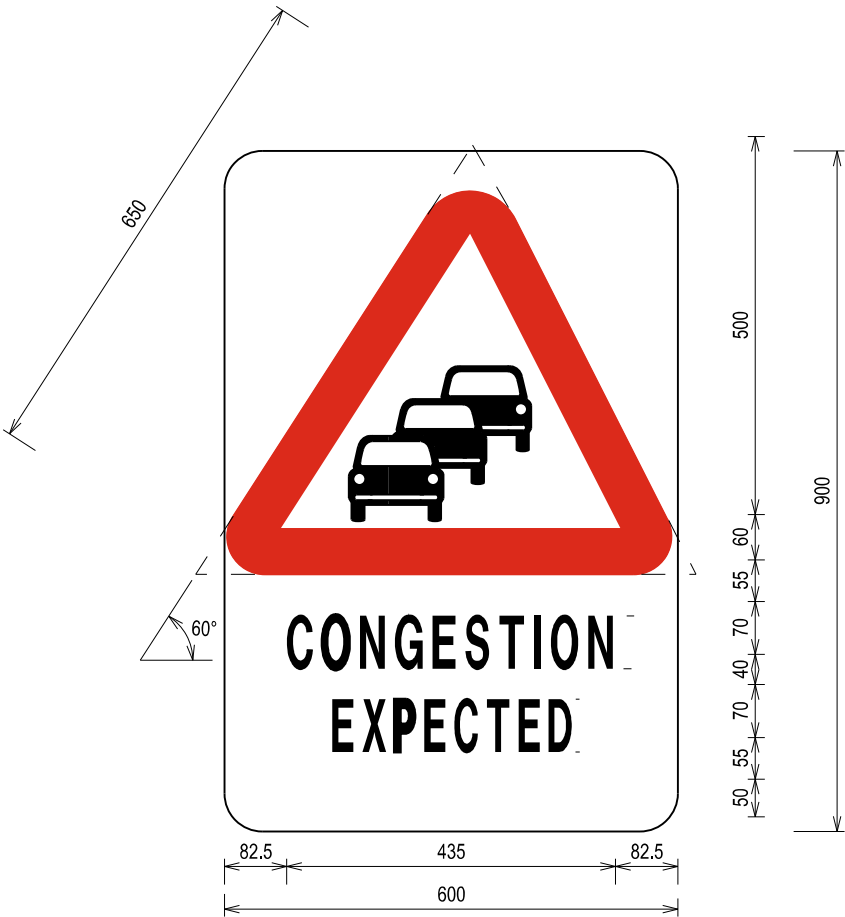

CONGESTION EXPECTED AHEAD


STANDARD		DETAIL		Land Transport Authority	
TRAFFIC INFORMATORY		SIGNS		DRAWING NO.	REV.
(SHEET 16 OF 19)		(SHEET 16 OF 19)		LTA/SDRE14/18/TFI16	A
A		APR 2024		DATE OF ISSUE	SHEET NO.
REV.		DATE		1st APR 2014	16 OF 19
				SCALE	
				1:10	

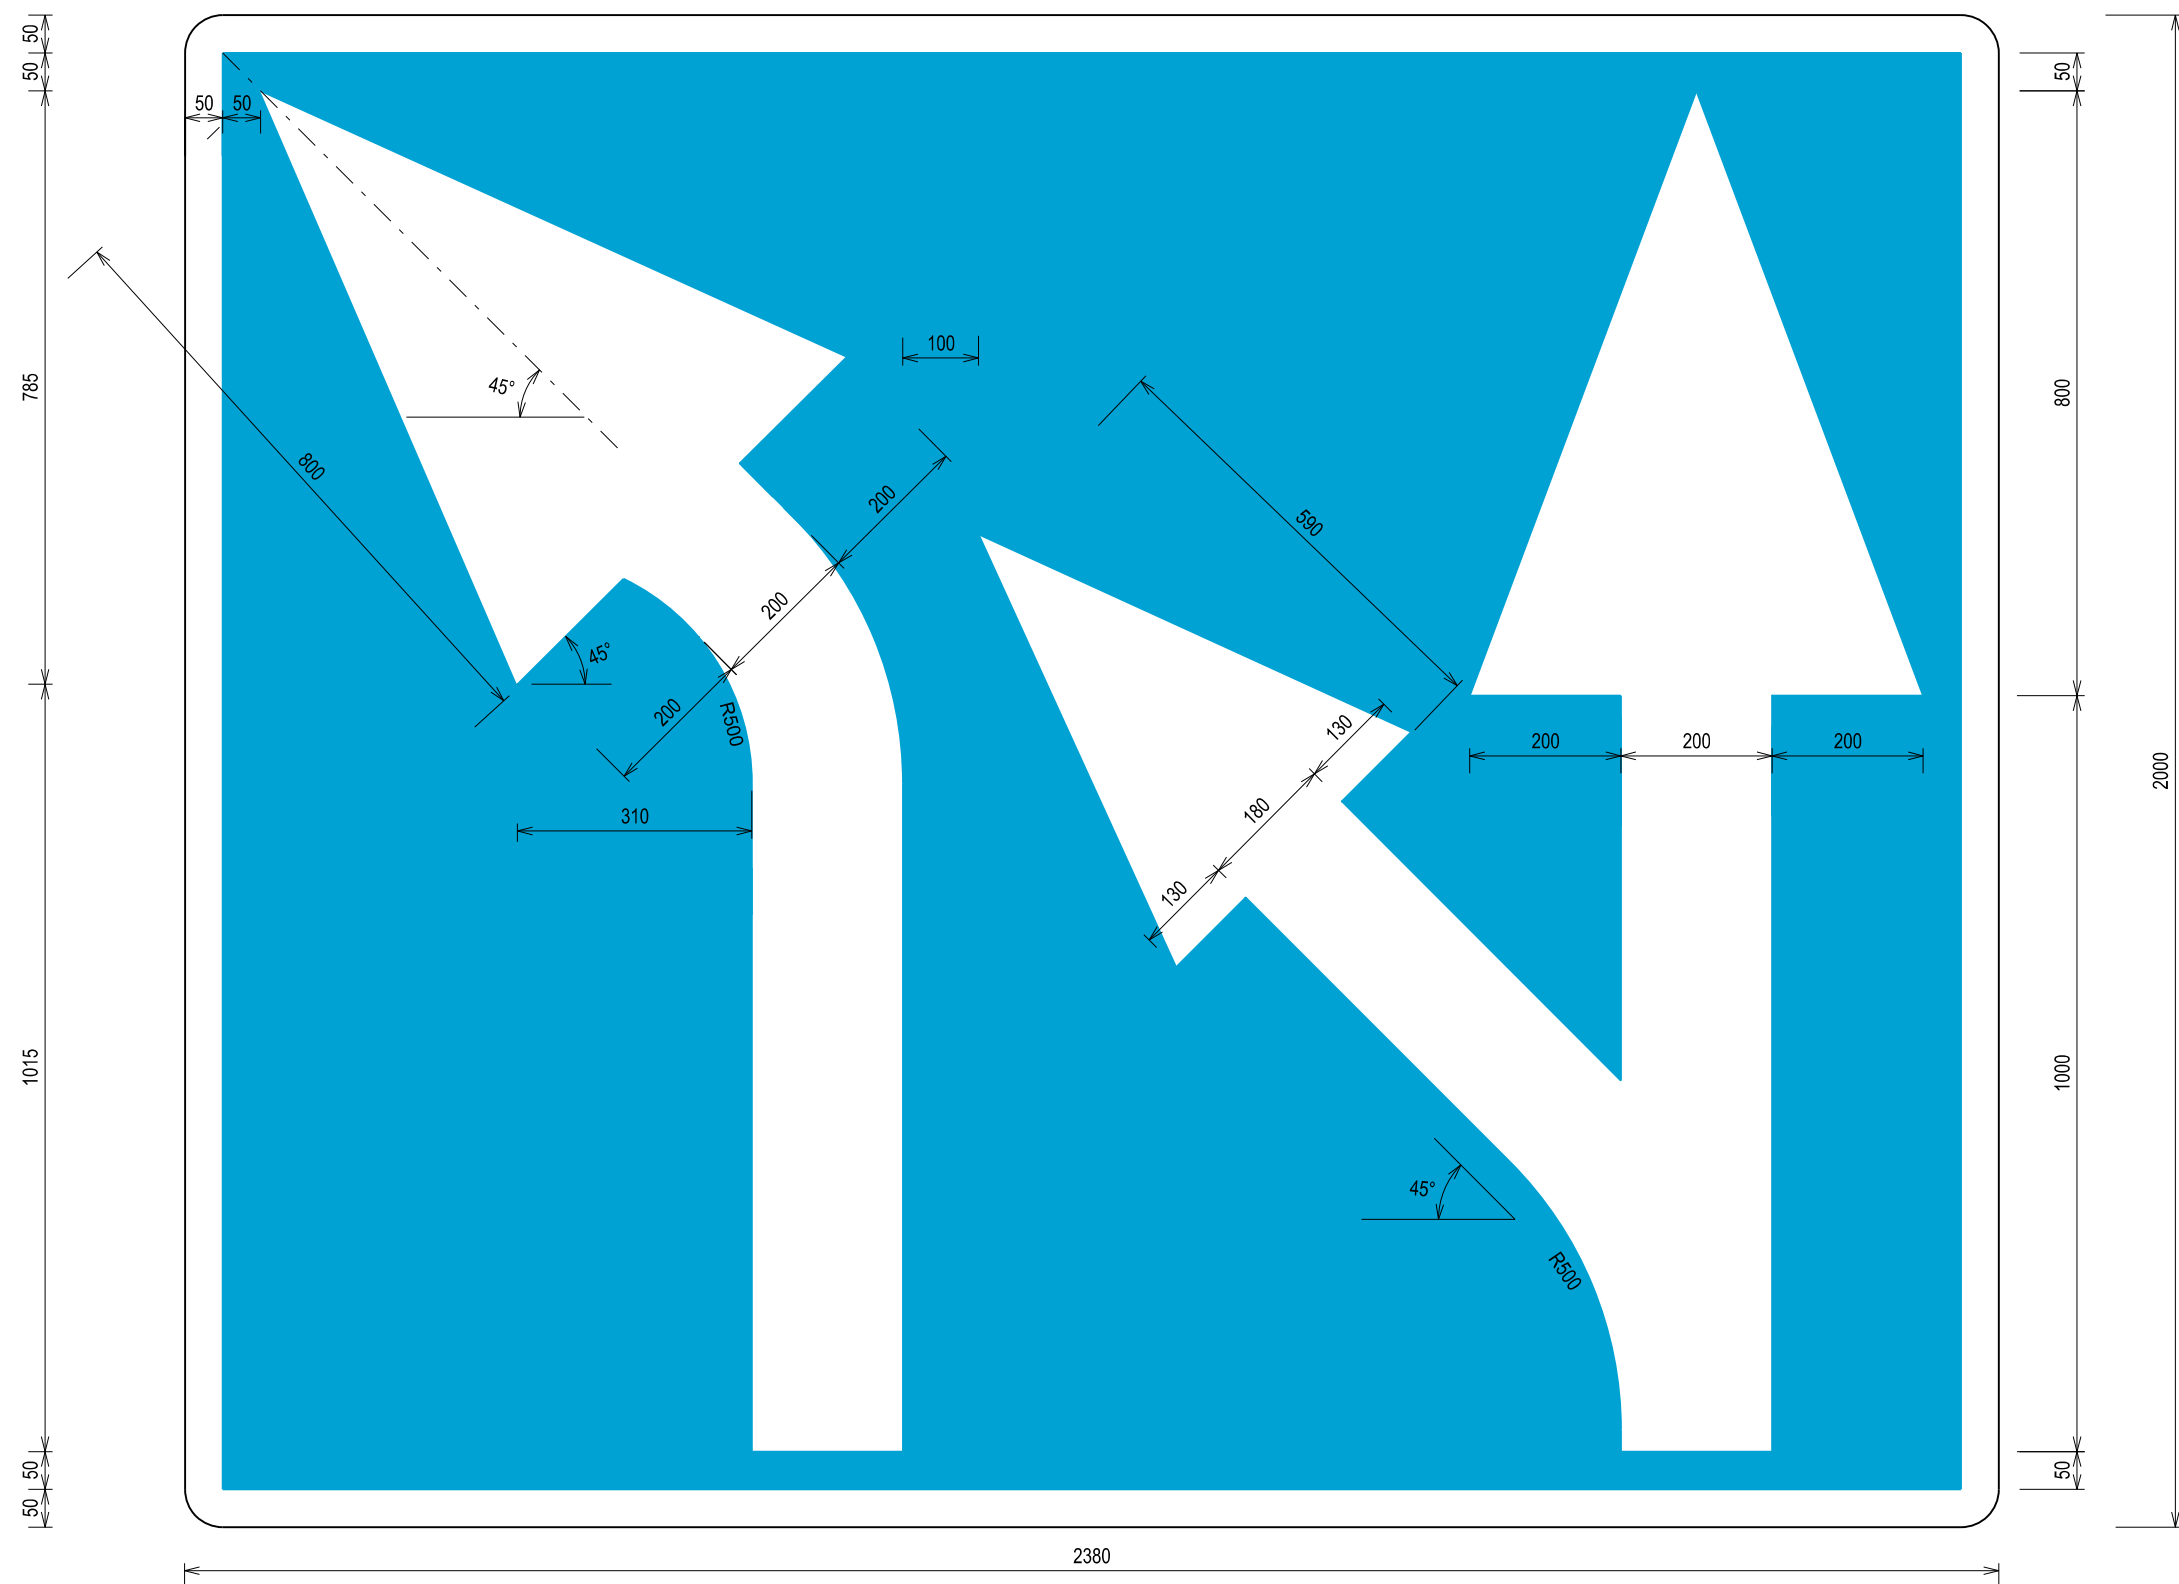[illegible]

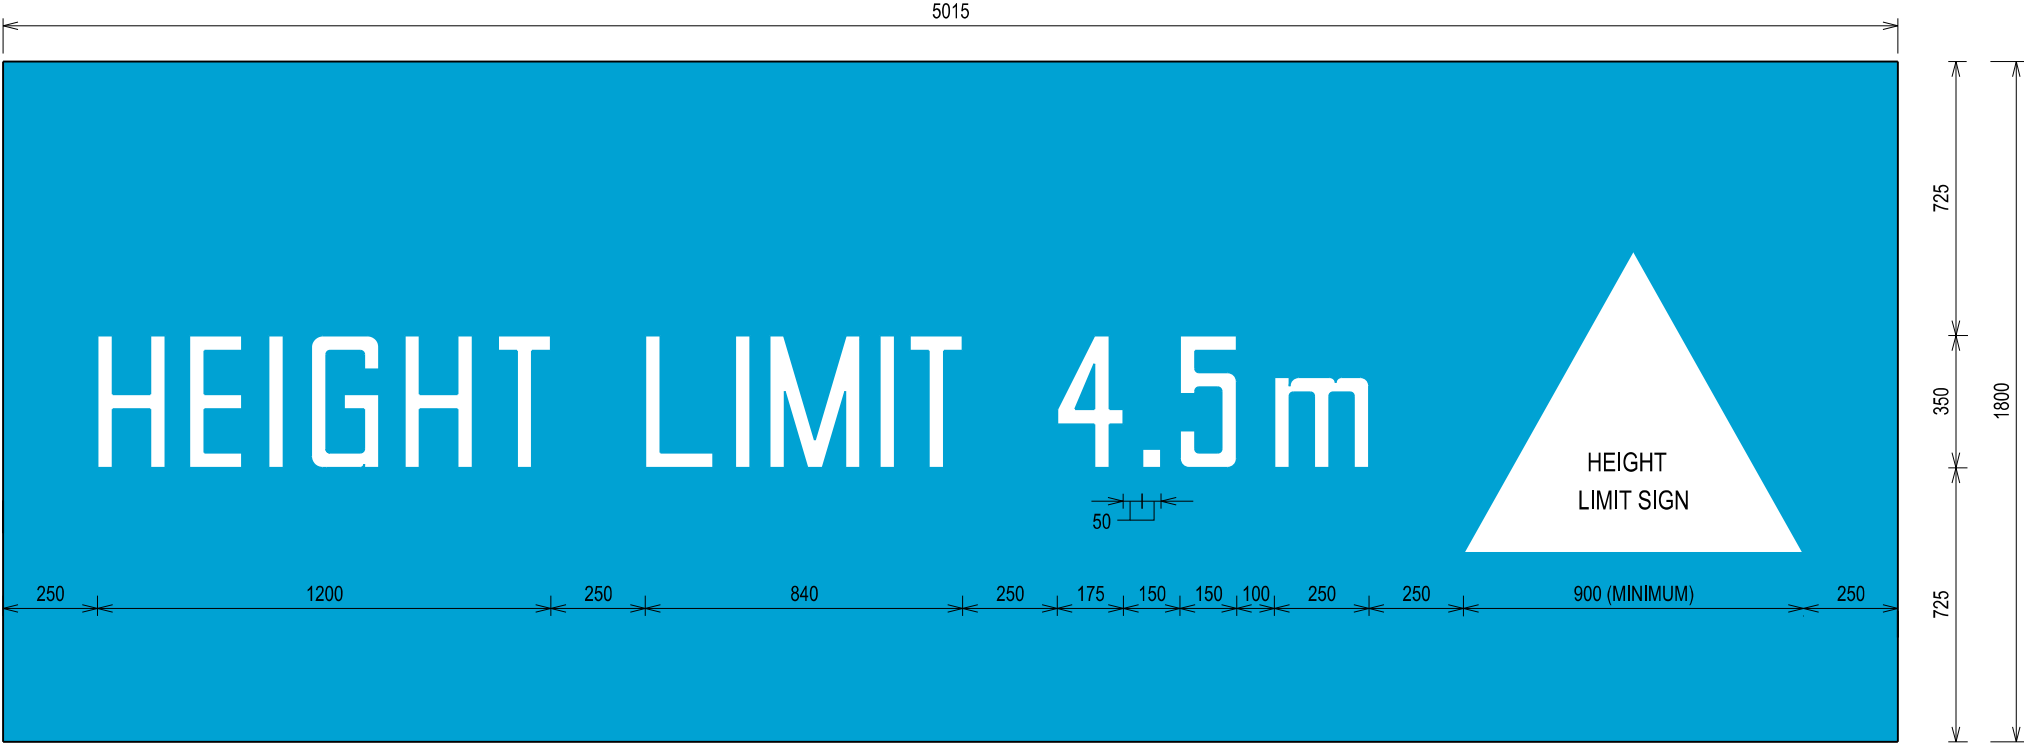


NO. OF LANES	(MINIMUM)		c (mm)
	a (mm)	b (mm)	
2 LANES ($\approx$ 7.4m)	290.5	290.5	300
3 LANES ($\approx$ 11.1m)	1115.5	1115.5	400
4 LANES ($\approx$ 14.8m)	1790.5	1790.5	800
5 LANES ($\approx$ 17.5m)	2565.5	2565.5	1000

FOR 1 LANE

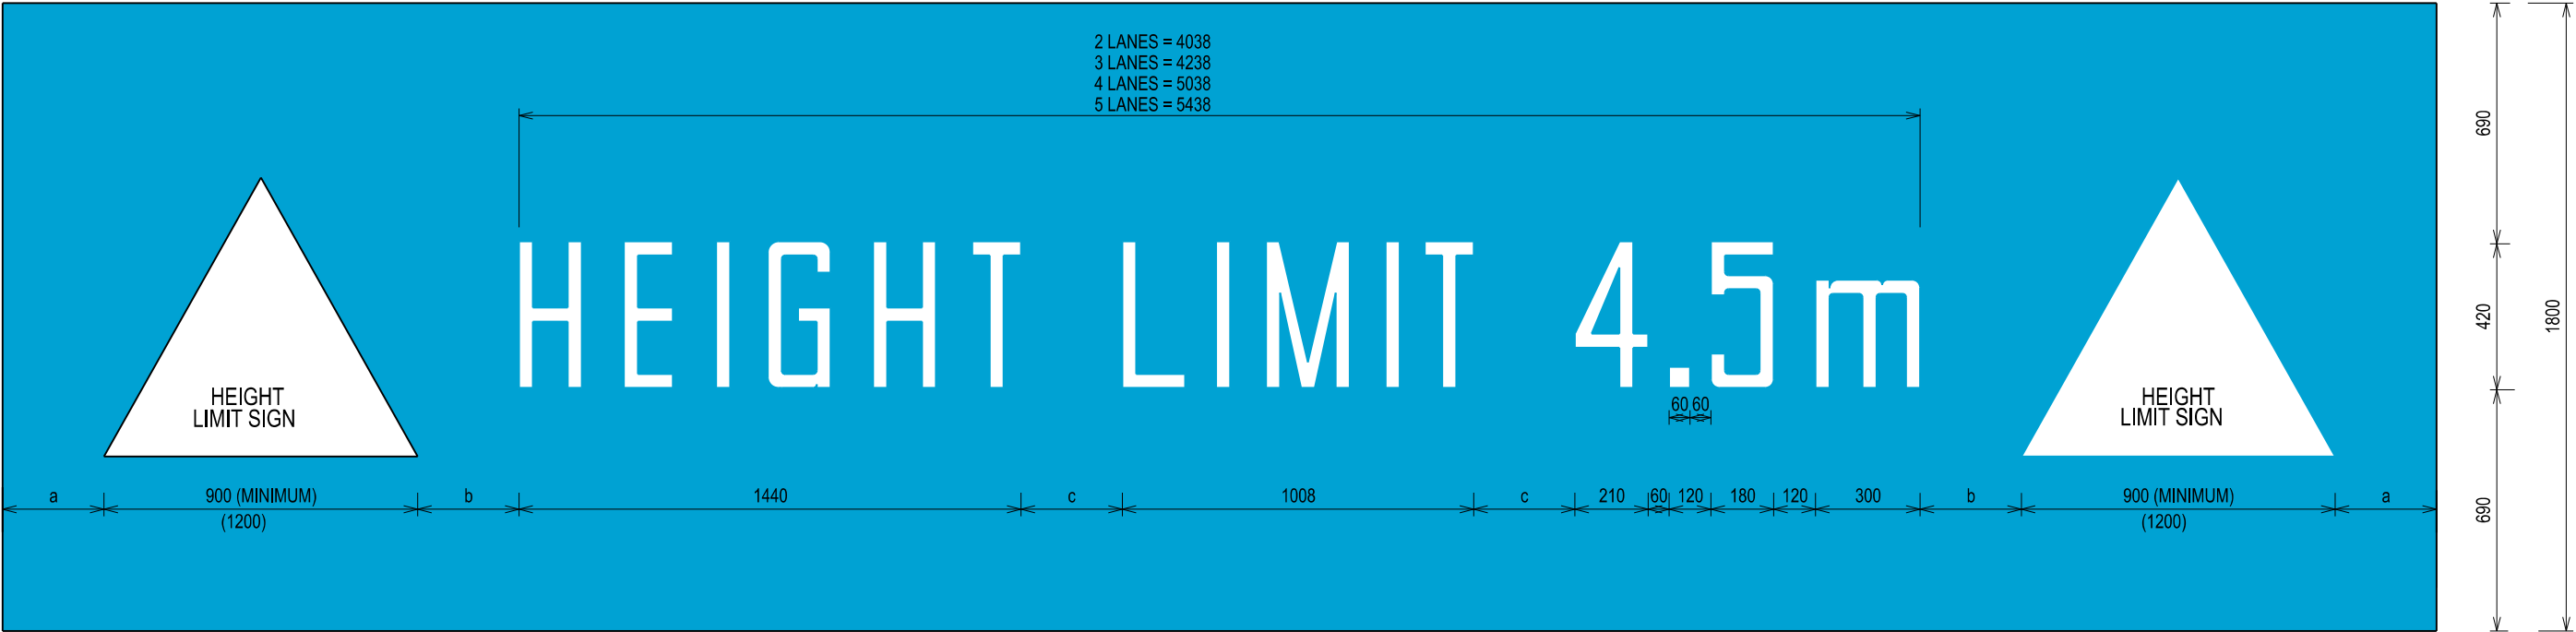


FOR 2 LANES OR MORE

A	APR 2024	DATE	STANDARD DETAIL	Land Transport Authority		
			TRAFFIC INFORMATORY SIGNS (SHEET 18 OF 19)	DRAWING NO.	REV.	
				LTA/SDRE14/18/TFI18	A	
REV.		DATE	DATE OF ISSUE	SCALE	SHEET NO.	
			1st APR 2014	1:20	18 OF 19	

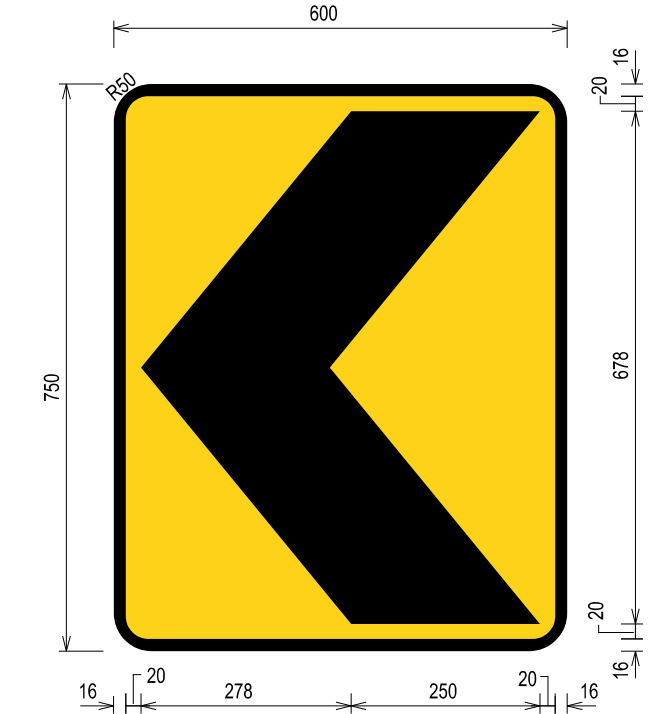


CURVE ALIGNMENT MARKER (FOR ARTERIAL ROAD)
SCALE 1:10

BLACK ARROW : VINYL CUT FILM
YELLOW BACKGROUND : FLOURESCENT YELLOW WIDE ANGLE
PRISMATIC REFLECTIVE SHEETING OR EQUIVALENT
BACKING : 2.03mm ALUMINIUM PLATE
SIZE : 600mm X 750mm
BORDER : 16mm BLACK ALL ROUND

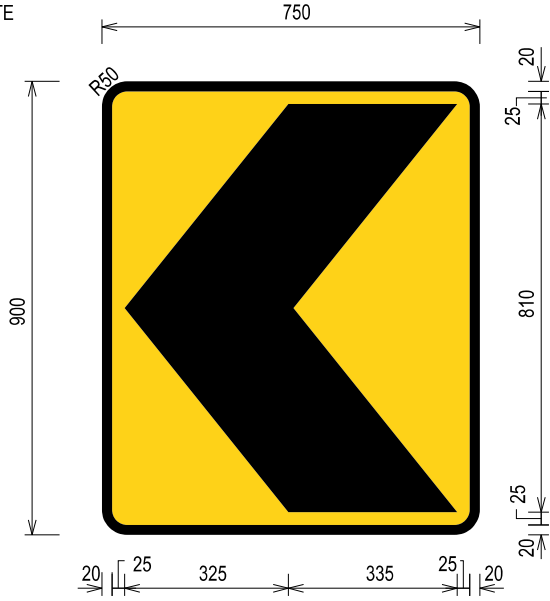


CURVE ALIGNMENT MARKER (FOR EXPRESSWAY)
SCALE 1:15

BLACK ARROW : VINYL CUT FILM
YELLOW BACKGROUND : FLOURESCENT YELLOW WIDE ANGLE
PRISMATIC REFLECTIVE SHEETING OR EQUIVALENT
BACKING : 2.03mm ALUMINIUM PLATE
SIZE : 750mm X 900mm
BORDER : 20mm BLACK ALL ROUND

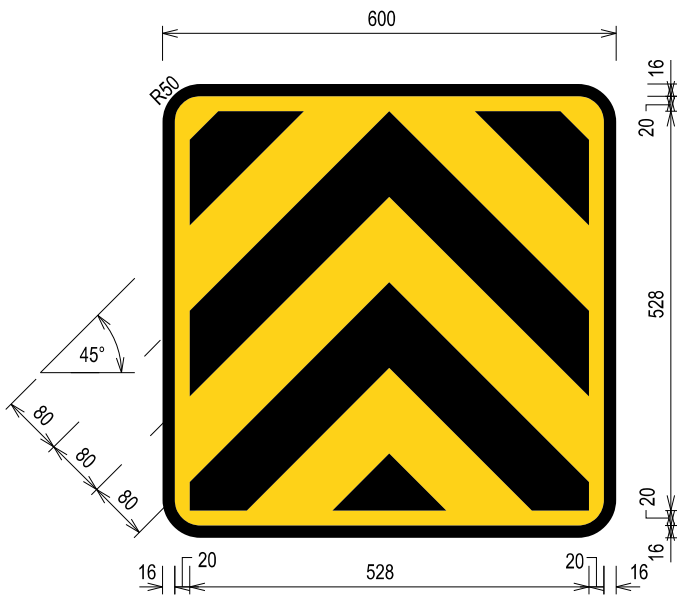


600mm X 600mm OBJECT MARKER
SCALE 1:10

BLACK ARROW : VINYL CUT FILM
YELLOW BACKGROUND : FLOURESCENT YELLOW WIDE ANGLE
PRISMATIC REFLECTIVE SHEETING OR EQUIVALENT
BACKING : 2.03mm ALUMINIUM PLATE
SIZE : 600mm X 600mm
BORDER : 16mm BLACK ALL ROUND

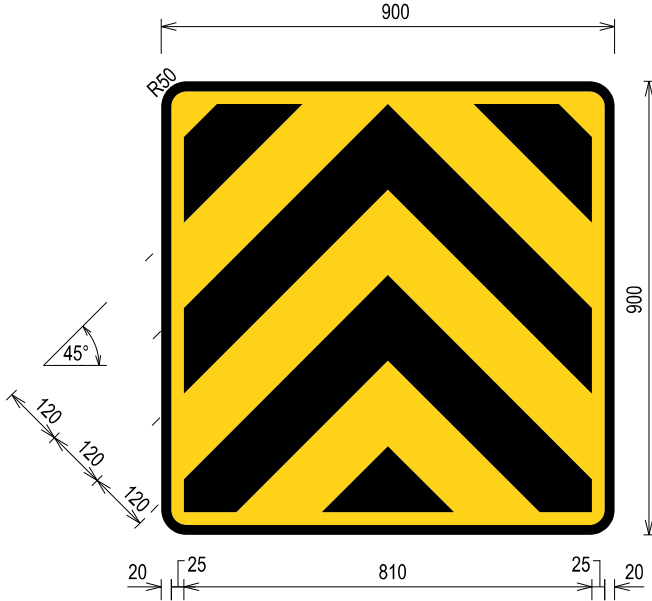


900mm X 900mm OBJECT MARKER
SCALE 1:15

BLACK ARROW : VINYL CUT FILM
YELLOW BACKGROUND : FLOURESCENT YELLOW WIDE ANGLE
PRISMATIC REFLECTIVE SHEETING OR EQUIVALENT
BACKING : 2.03mm ALUMINIUM PLATE
SIZE : 900mm X 900mm
BORDER : 20mm BLACK ALL ROUND

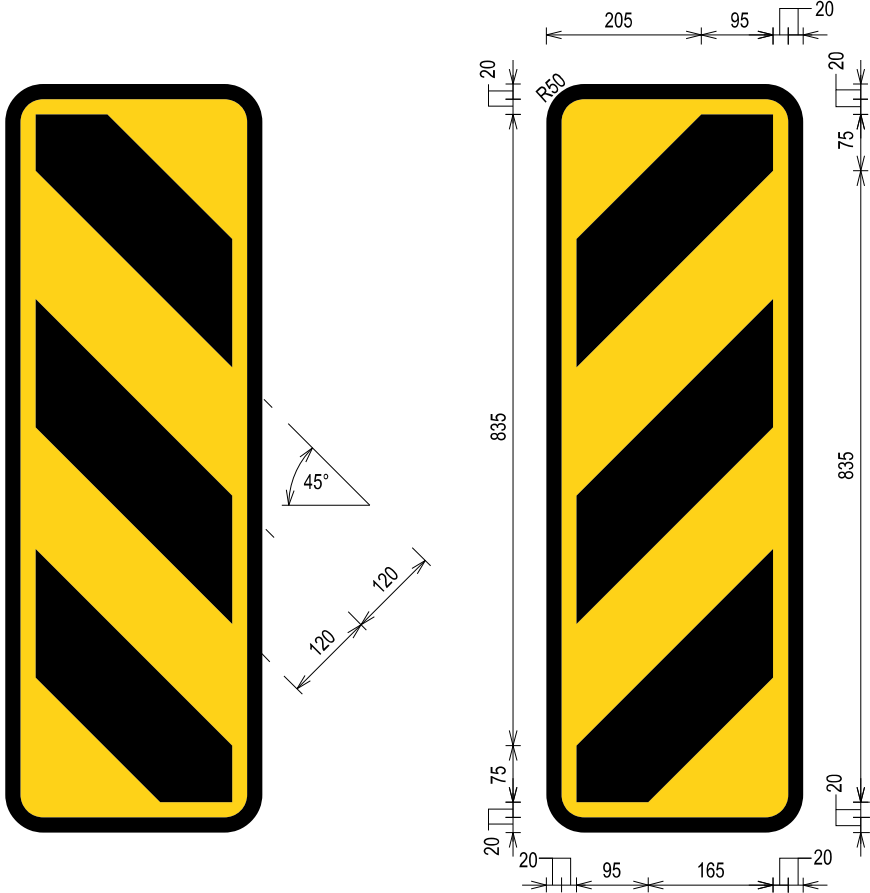

340mm X 990mm OBJECT MARKER
SCALE 1:10

BLACK STRIP : VINYL CUT FILM
YELLOW BACKGROUND : FLOURESCENT YELLOW WIDE ANGLE
PRISMATIC REFLECTIVE SHEETING OR EQUIVALENT
BACKING : 2.03mm ALUMINIUM PLATE
SIZE : 340mm X 990mm
BORDER : 20mm BLACK ALL ROUND

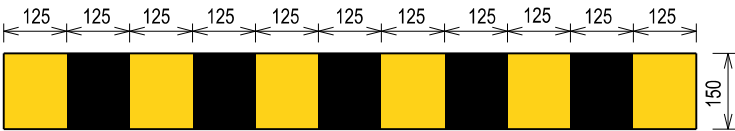

KERB STRIP MARKER
SCALE 1:15

BLACK STRIP : VINYL CUT FILM
YELLOW BACKGROUND : FLOURESCENT YELLOW WIDE ANGLE
PRISMATIC REFLECTIVE SHEETING OR EQUIVALENT
BACKING : 2.03mm ALUMINIUM PLATE
HEIGHT : 150mm
LENGTH : VARIES WITH SIZE OF KERB NOSING

STANDARD DETAIL		Land Transport Authority	
TRAFFIC INFORMATORY SIGNS (SHEET 19 OF 19)	DRAWING NO. LTA/SDRE14/18/TFI19		REV. A
	DATE OF ISSUE 1st APR 2014	SCALE AS SHOWN	SHEET NO. 19 OF 19
	REV. A	APR 2024	DATE