
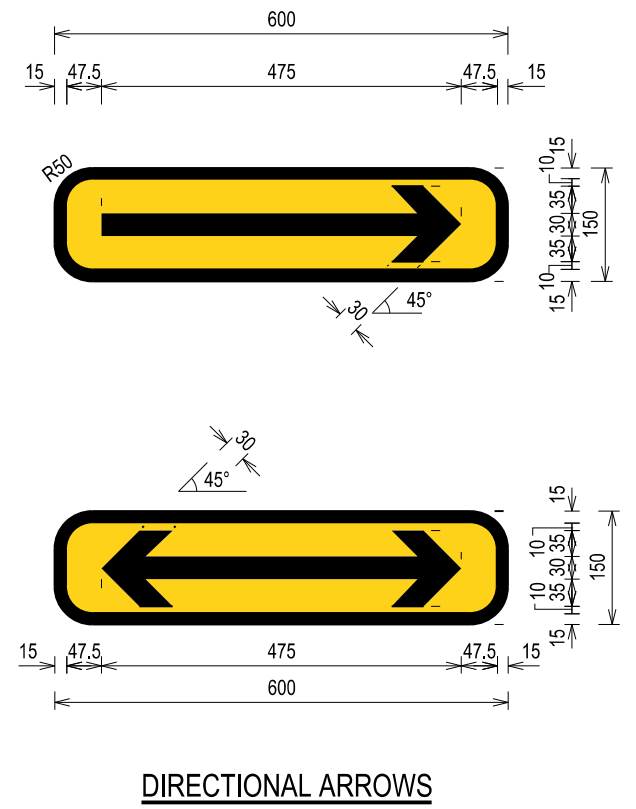
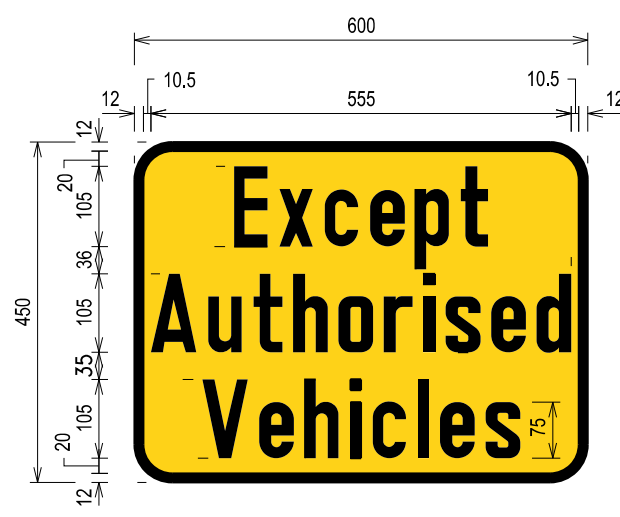
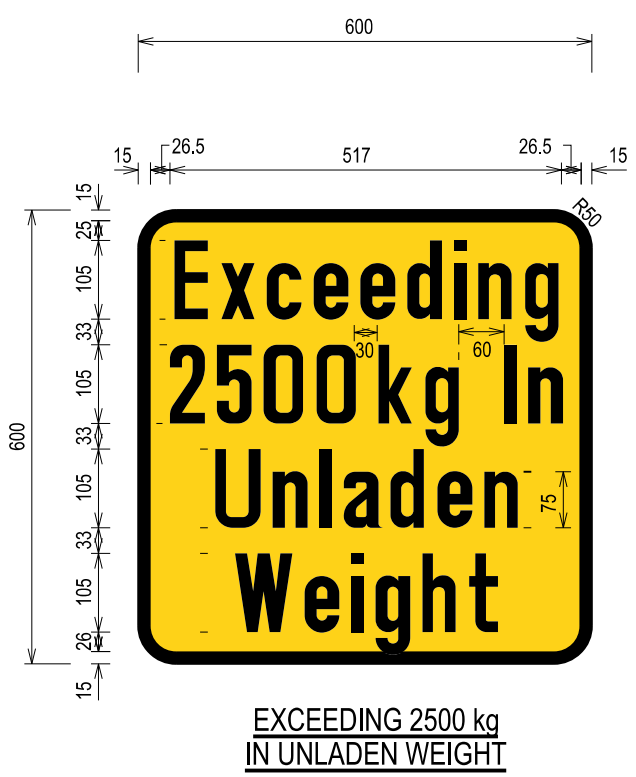
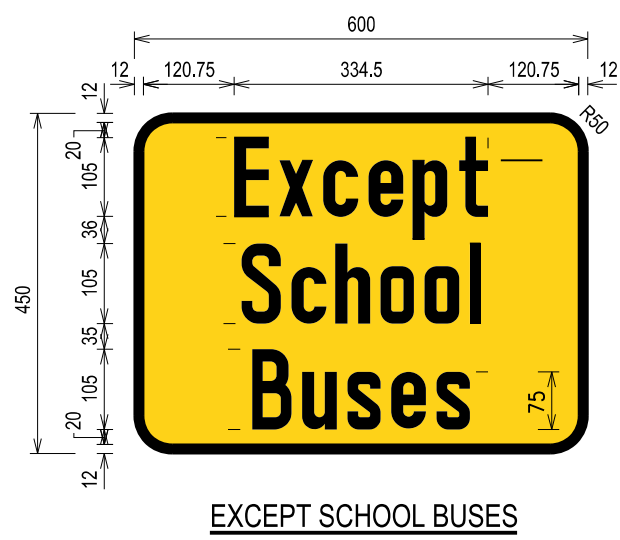


CHAPTER 19




TRAFFIC INFORMATORY SIGNS

DRAWING TITLE	DRAWING NO.	REVISION
TRAFFIC INFORMATORY SIGNS (SHEET 1 OF 2)	LTA/SDRE14/19/TFS1	-
TRAFFIC INFORMATORY SIGNS (SHEET 2 OF 2)	LTA/SDRE14/19/TFS2	-

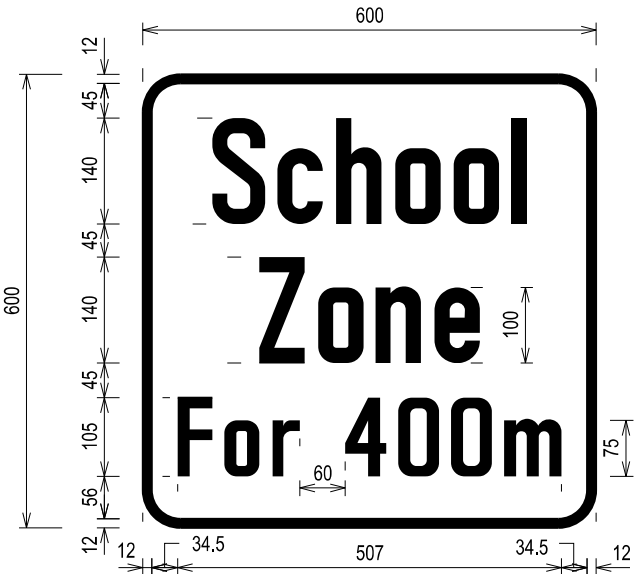

THESE SIGNS ARE TO BE USED WITH OTHER SIGNS TO SIGNIFY THE EXTENT THE RESTRICTIONS ETC. CONVEYED BY THESE OTHER SIGNS ARE TO APPLY.

STANDARD		DETAIL	
REV.		DATE	
		TRAFFIC INFORMATORY SIGNS (SHEET 1 OF 2)	
		Land Transport Authority	
		DRAWING NO. LTA/SDRE14/19/TFS1	
		REV. -	
		DATE OF ISSUE 1st APR 2014	
		SCALE 1:10	
		SHEET NO. 1 OF 2	

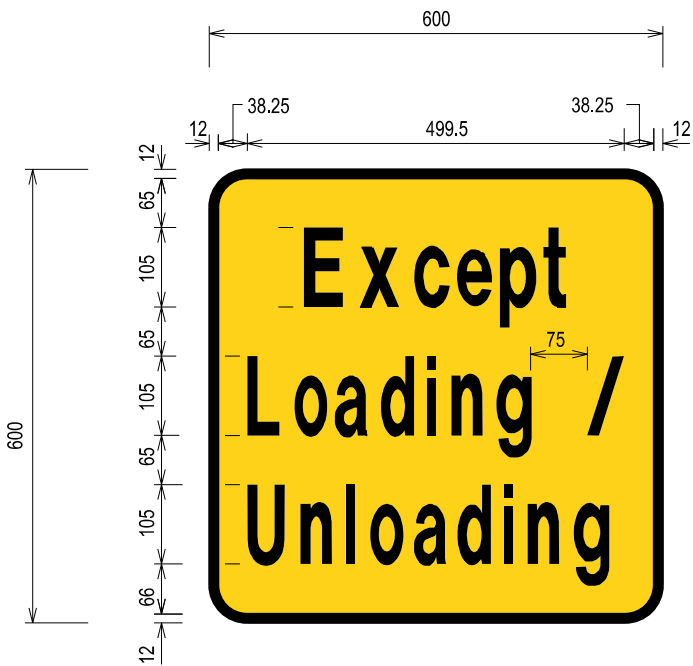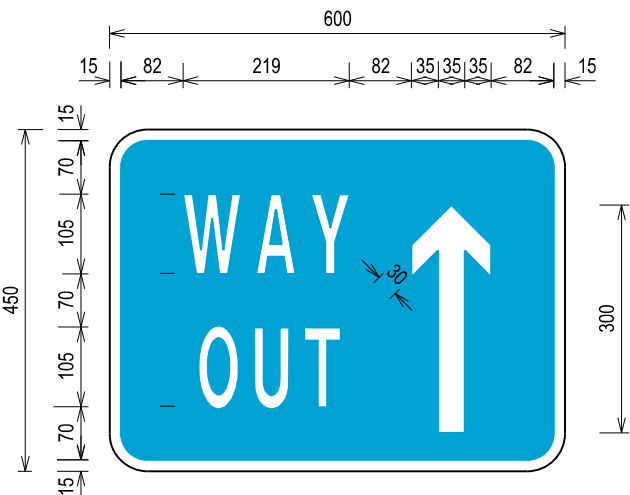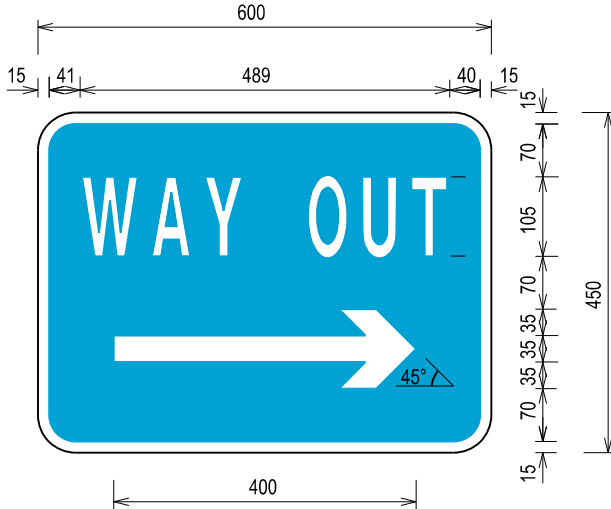

--	--	