


CHAPTER 20

STREET NAME BOARD

DRAWING TITLE	DRAWING NO.	REVISION
STREET NAME SIGN - GENERAL CONFIGURATION LAYOUT (SHEET 1 OF 3)	LTA/SDRE14/20/SNB1	A
STREET NAME SIGN - GENERAL CONFIGURATION LAYOUT (SHEET 2 OF 3)	LTA/SDRE14/20/SNB2	-
STREET NAME SIGN - GENERAL CONFIGURATION LAYOUT (SHEET 3 OF 3)	LTA/SDRE14/20/SNB3	A
STREET NAME SIGN - STREET NAME SIGN ON SINGLE SUPPORT POST	LTA/SDRE14/20/SNB4	A
STREET NAME SIGN - STREET NAME SIGN ON DOUBLE SUPPORT POST	LTA/SDRE14/20/SNB5	A
STREET NAME SIGN - CANTILEVER STREET NAME SIGN ON VERTICAL SUPPORT POST	LTA/SDRE14/20/SNB6	A
STREET NAME SIGN - CANTILEVER STREET NAME SIGN ON EXISTING LAMP POST	LTA/SDRE14/20/SNB7	A
STREET NAME SIGN SINGLE SIDE STREET NAME SIGN ON EXISTING LAMP POST	LTA/SDRE14/20/SNB8	A
STREET NAME SIGN ON TRAFFIC POST	LTA/SDRE14/20/SNB9	A
STREET NAME SIGN - EXTRUSION	LTA/SDRE14/20/SNB10	A
STREET NAME SIGN - CASTING PARTS	LTA/SDRE14/20/SNB11	A
STREET NAME SIGN - TRAFFIC SIGN ON SUPPORT POST	LTA/SDRE14/20/SNB12	-

TEXTS - USE AUTOMATIC KERNING

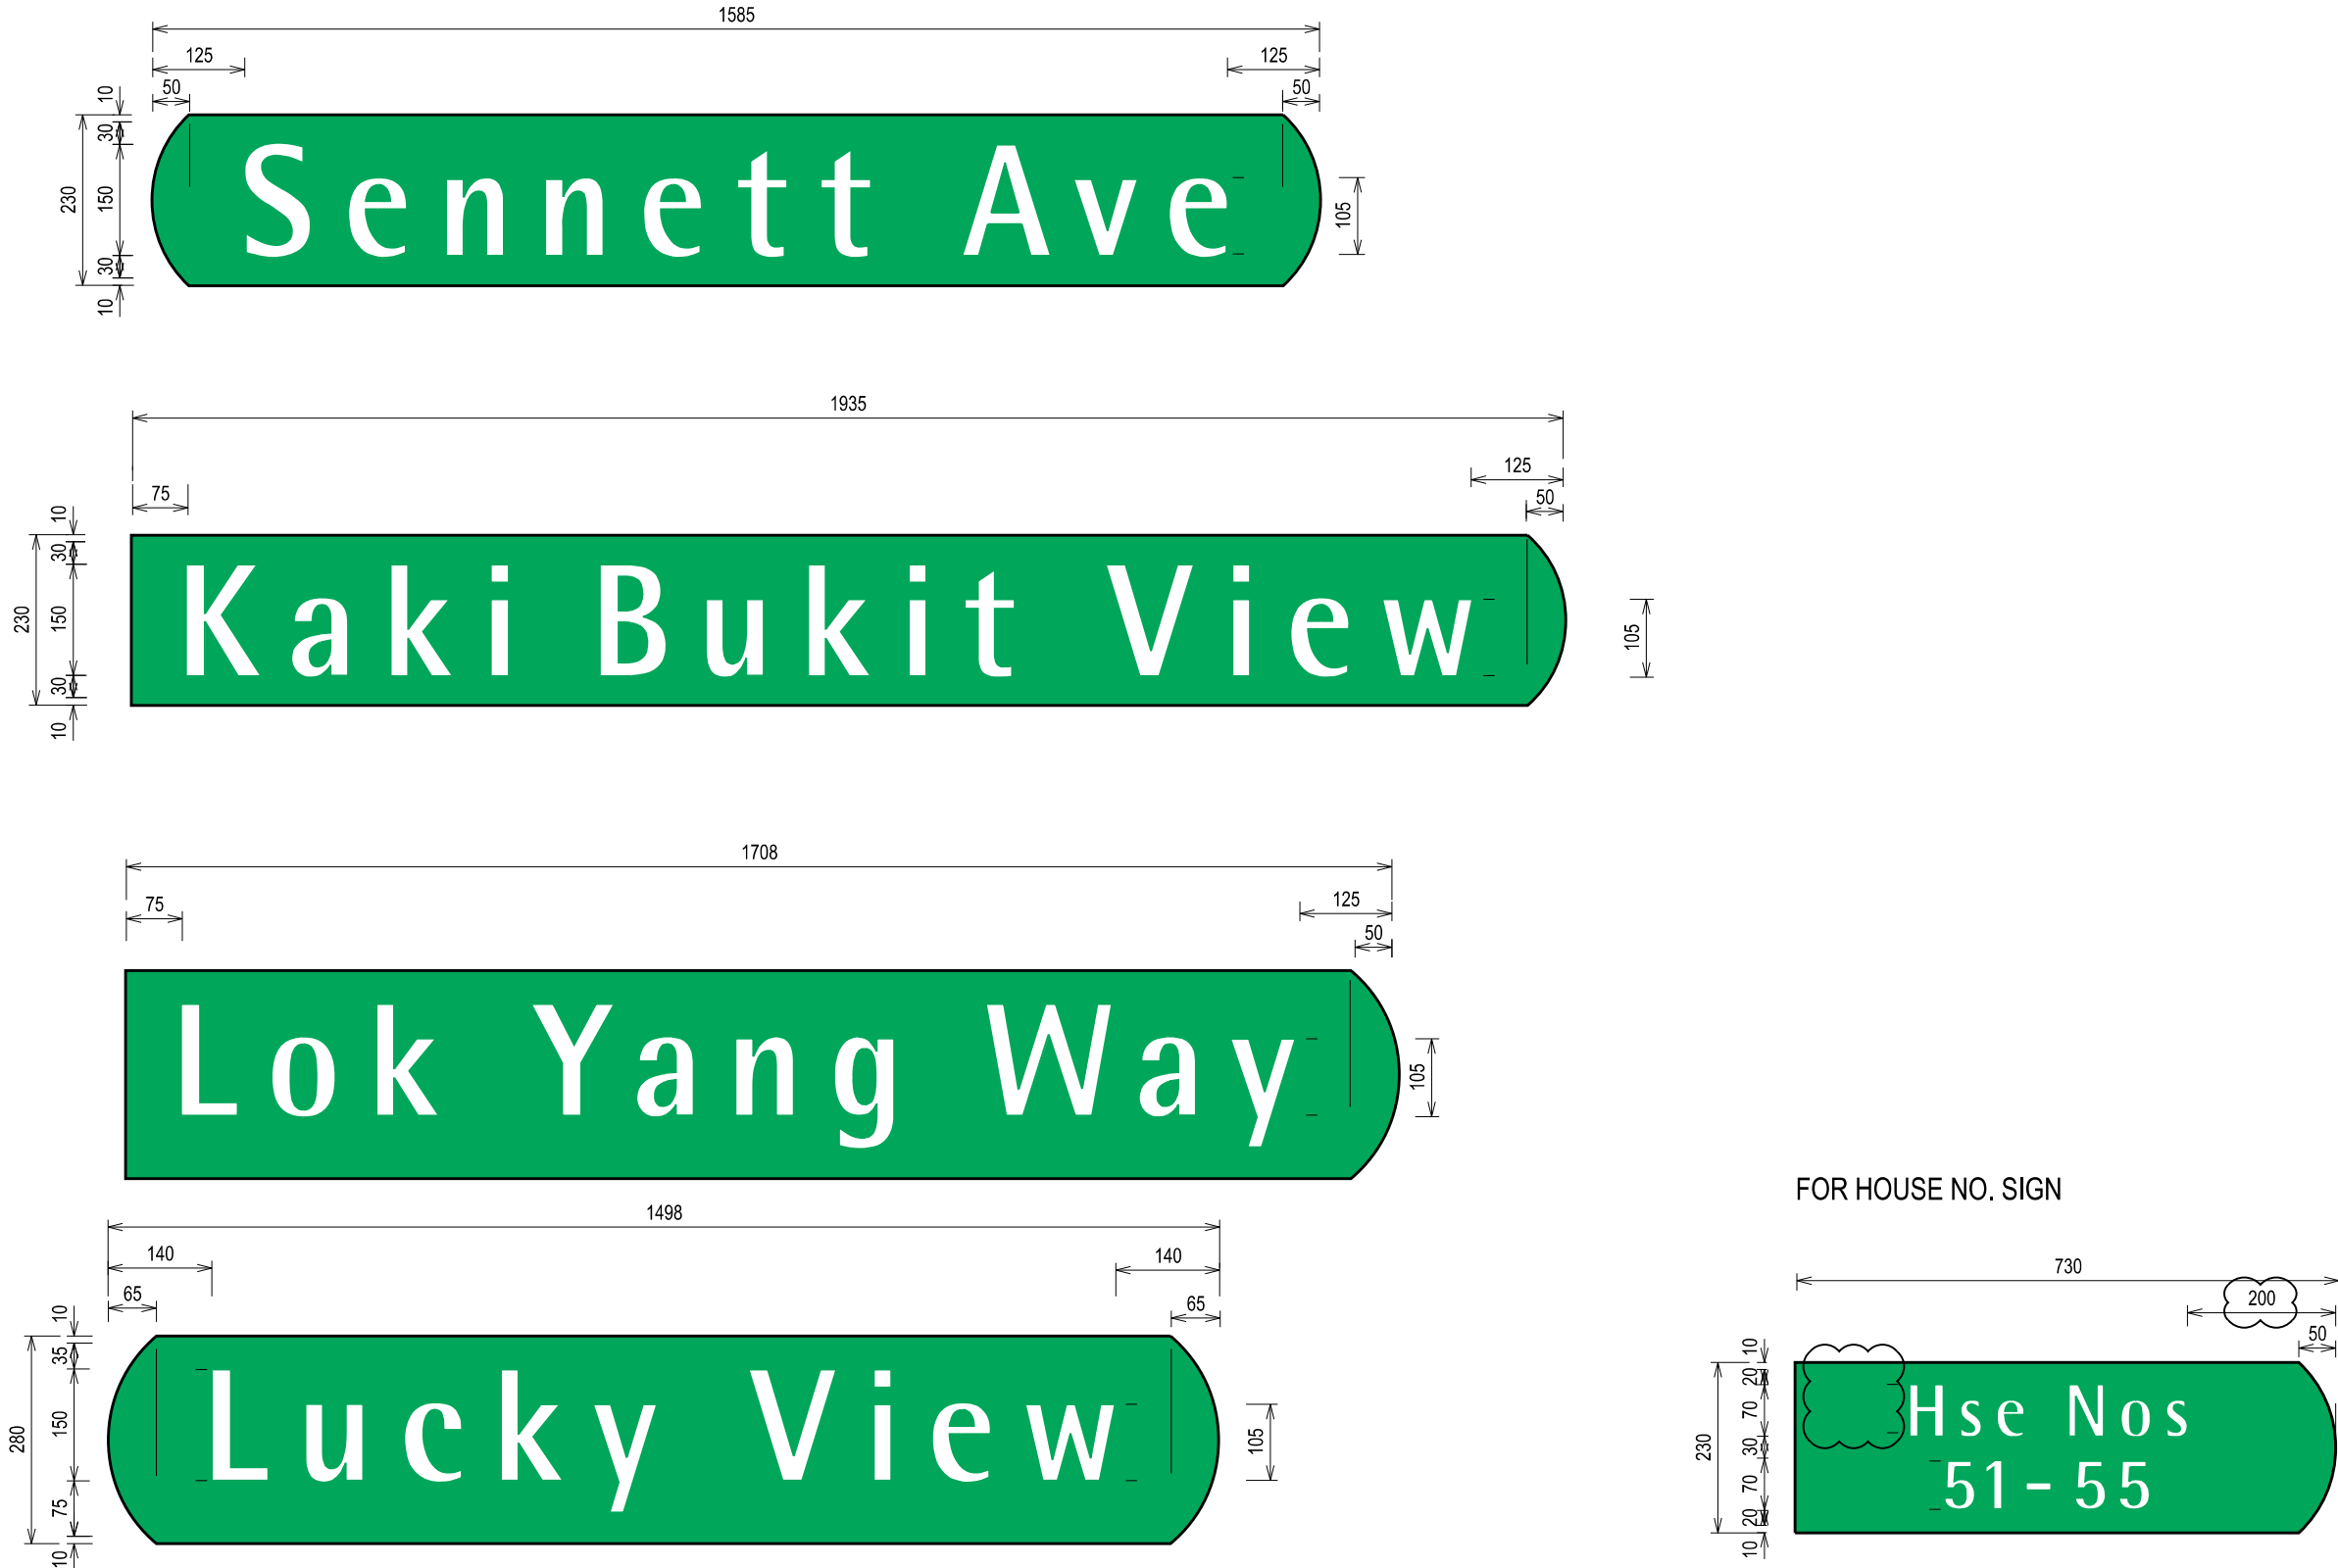

NOTES:

1. All measurements indicated in the drawings are approximate and shall be taken as a guide only.
2. Font used for the street name sign shall be rotis semi-san in extra bold.
3. Wide angle prismatic retroreflective sheet shall be used.
4. White letterings on green background, reflective sheetings complying with ASTM D4956-2001 Type IX.

STANDARD		DETAIL		Land Transport Authority	
A		APR 2019		DRAWING NO. LTA/SDRE14/20/SNB1	
REV.		DATE		DATE OF ISSUE 1st APR 2014	
				SCALE 1:10	
				SHEET NO. 1 OF 3	

LTA Rotis Font

A B C D E F G H I J K L M


N O P Q R S T U V W X Y Z

a b c d e f g h i j k l m

n o p q r s t u v w x y z

0 1 2 3 4 5 6 7 8 9 (# & , . /)

NOTES: 1. All measurements indicated in the drawings are approximate and shall be taken as a guide only.				STANDARD	DETAIL	Land Transport Authority					
								STREET NAME SIGN - GENERAL CONFIGURATION LAYOUT (SHEET 2 OF 3)	DRAWING NO.		REV.
									LTA/SDRE14/20/SNB2		-
									DATE OF ISSUE	SCALE	SHEET NO.
									1st APR 2014	NTS	2 OF 3
		REV.	DATE								

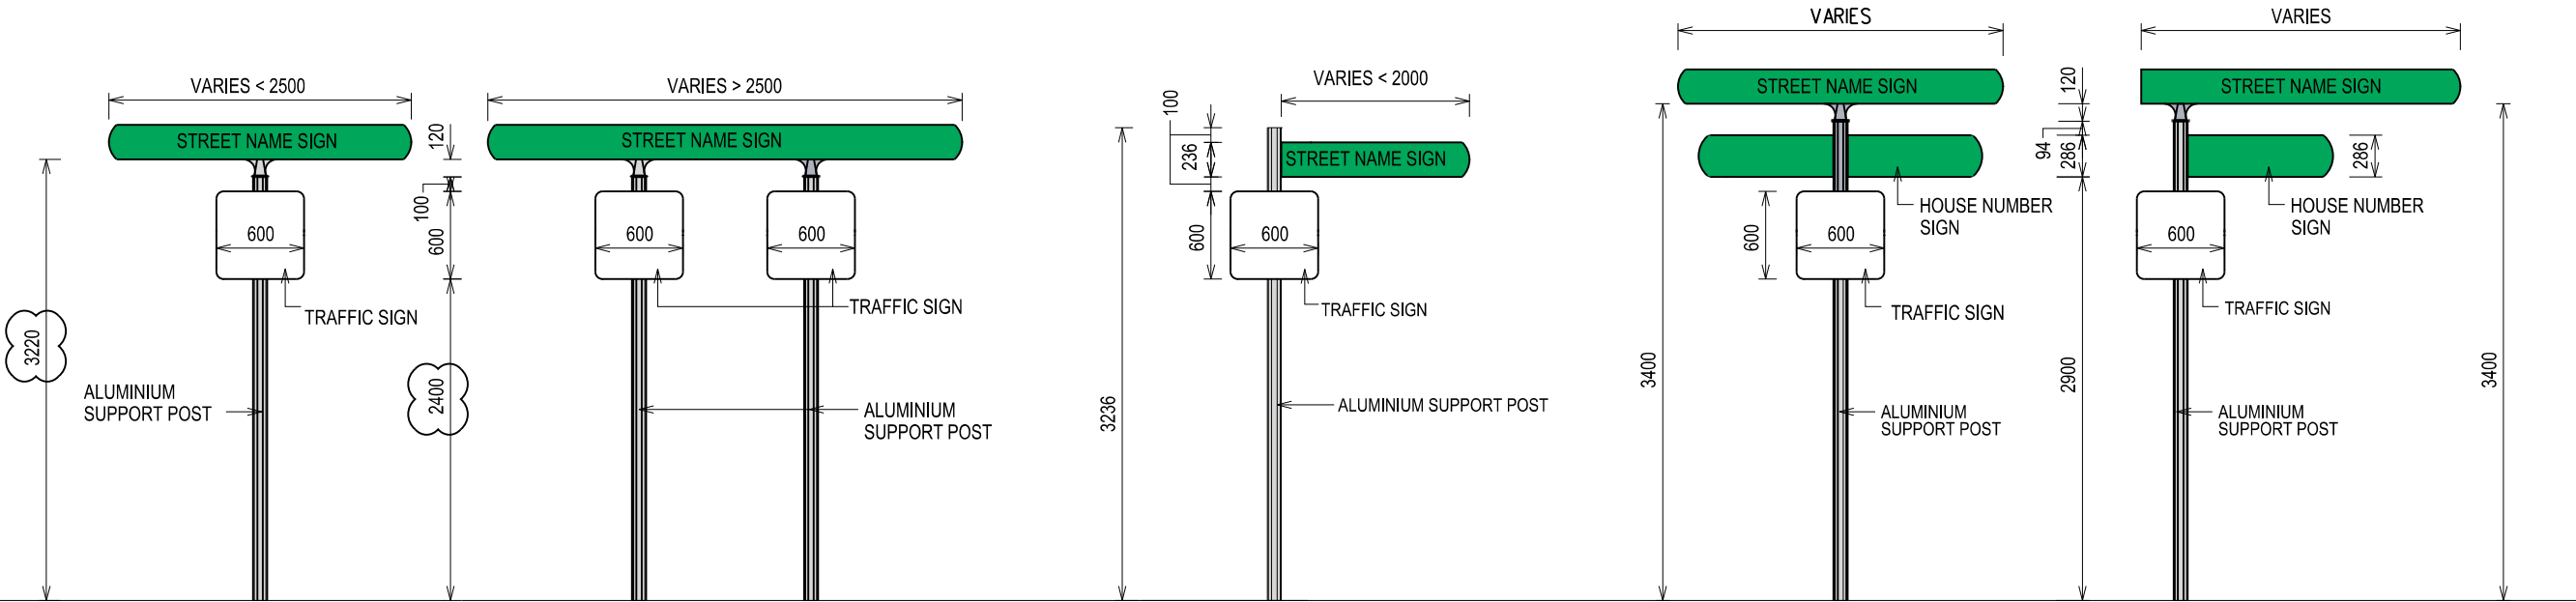


SNS-S1
SCALE 1:50

SNS-S2
SCALE 1:50

SNS-S3
SCALE 1:50

SNS-S4
SCALE 1:50


SNS-S5
SCALE 1:50

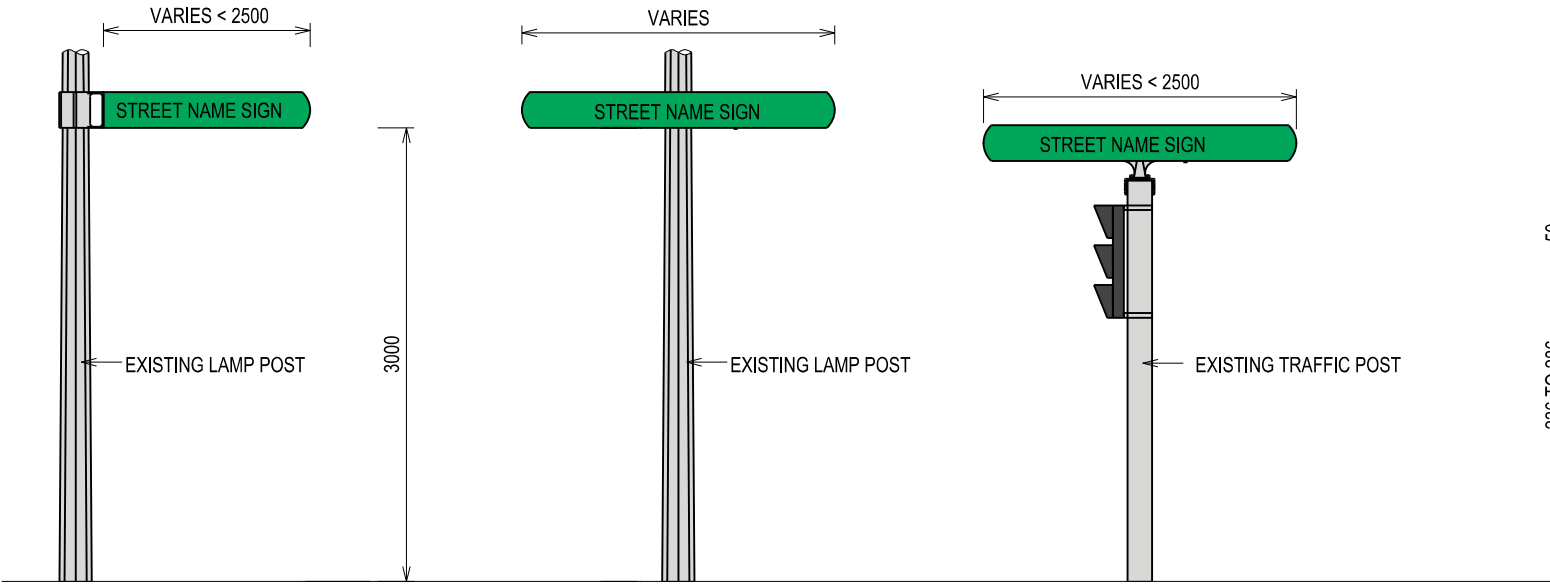

SNS-L1
SCALE 1:50

SNS-L2
SCALE 1:50

SNS-T1
SCALE 1:50



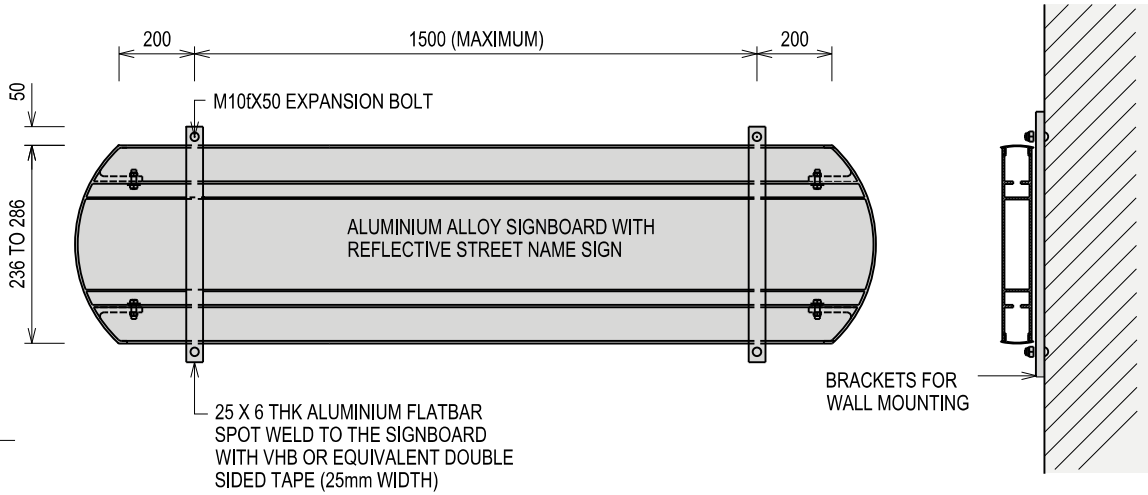


SNS-W1
SCALE 1:20

NOTES:

1. All measurements indicated in the drawings are approximate and shall be taken as a guide only.
2. The design must be compactible and interchangeable.

STANDARD DETAIL		Land Transport Authority	
STREET NAME SIGN - GENERAL CONFIGURATION LAYOUT (SHEET 3 OF 3)		DRAWING NO. LTA/SDRE14/20/SNB3	
		REV. A	
		DATE OF ISSUE 1st APR 2014	SHEET NO. 3 OF 3

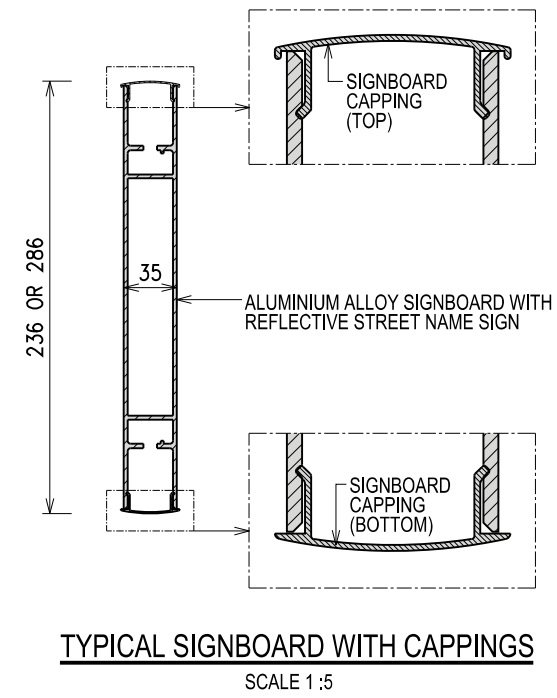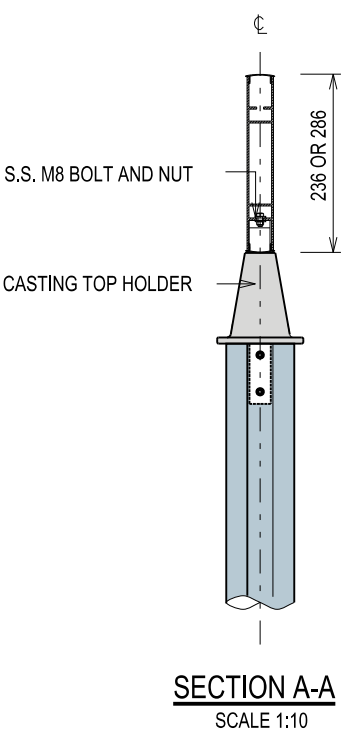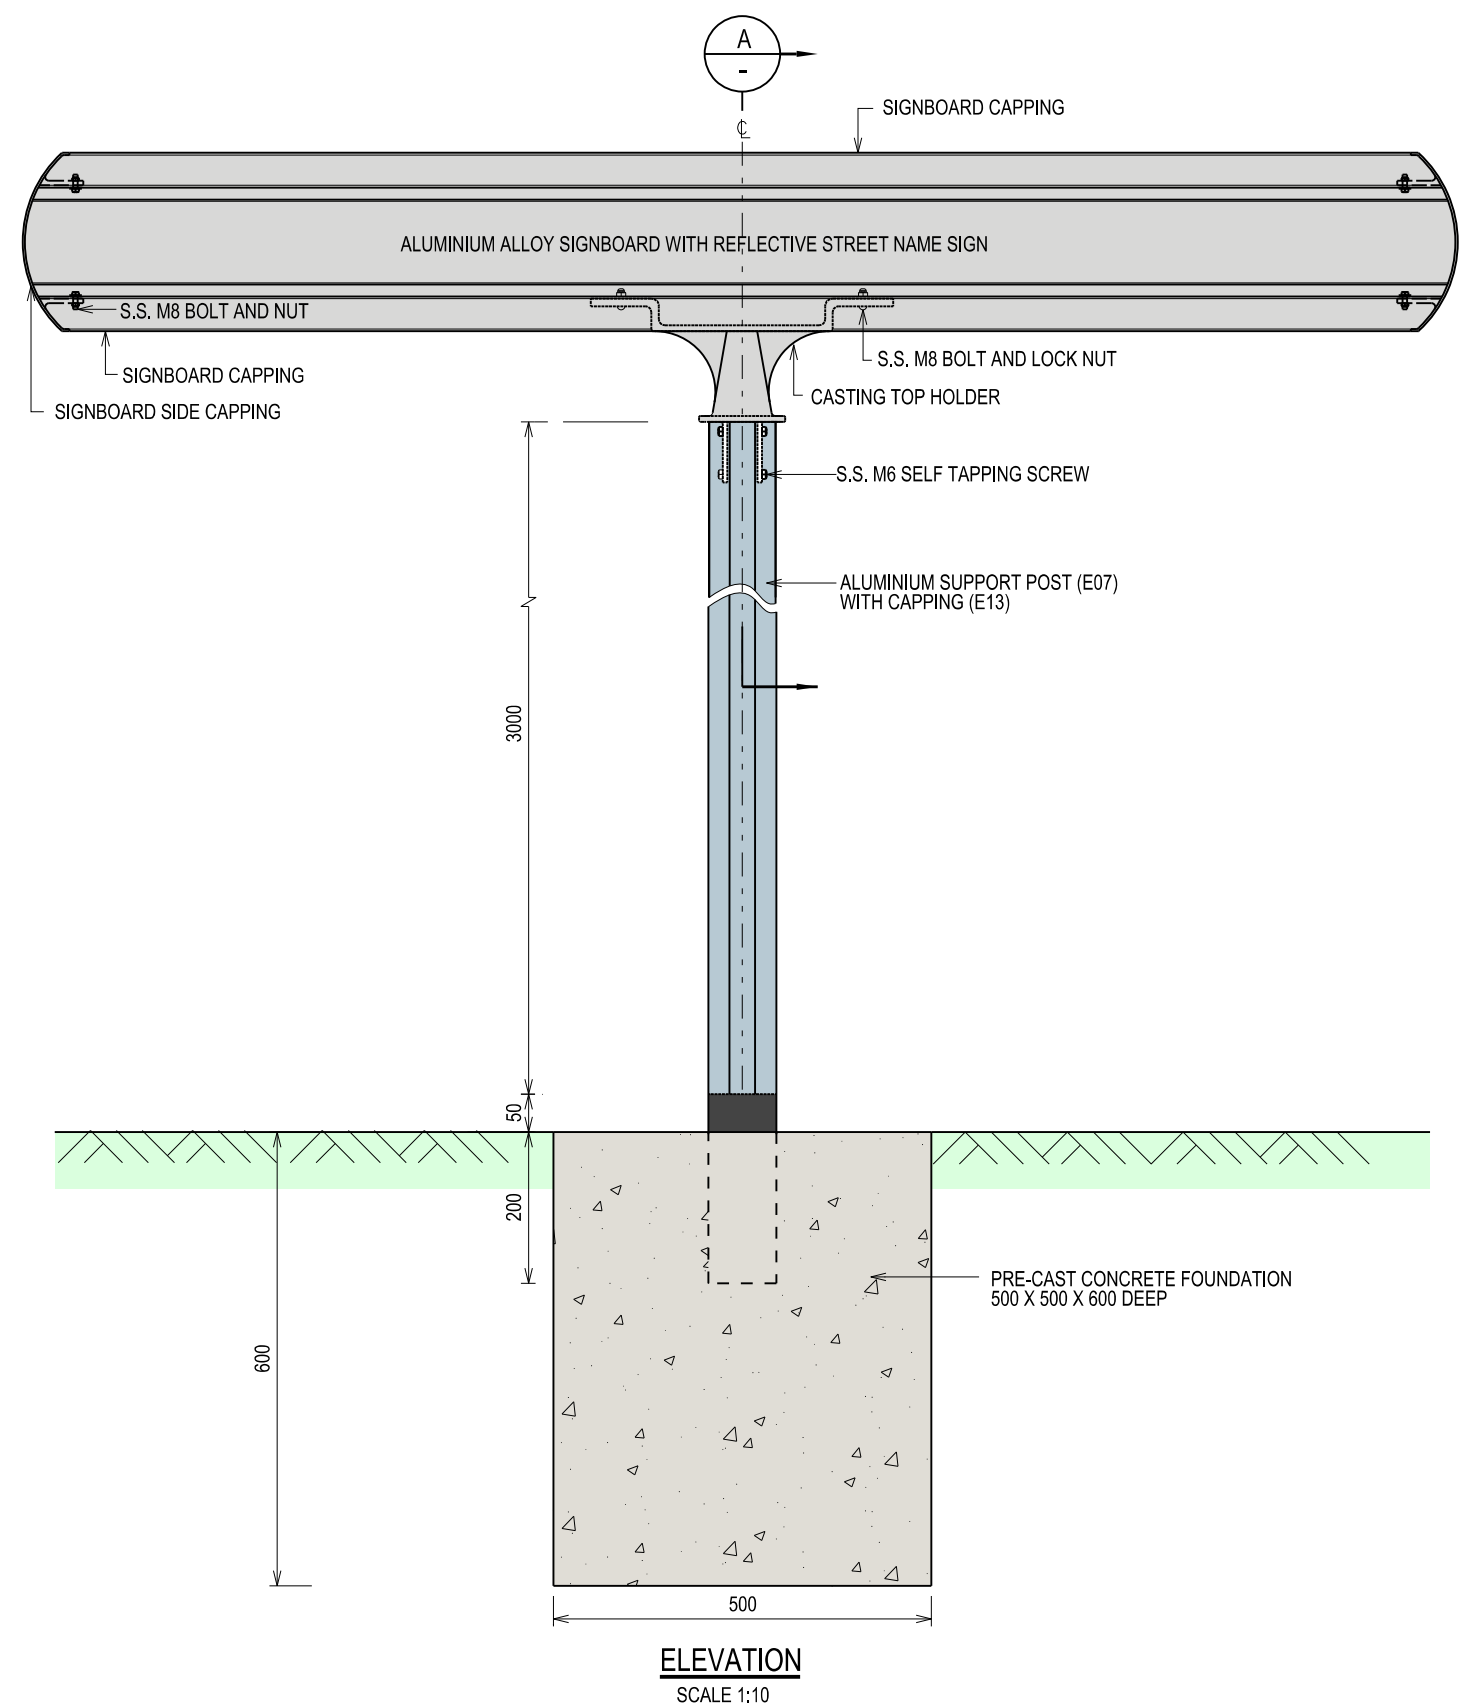

- NOTES:
- 1. ALL EXTRUDED SECTIONS SHALL BE FABRICATED FROM HIGH STRENGTH, MARINE GRADE ALUMINIUM ALLOYS OF DURABILITY RATING B TO BS EN 1999;
 - 2. ALL CASTING PARTS SHALL BE PRODUCED VIA PRESSURE DIE CAST METHOD. ALL STRUCTURAL CAST COMPONENTS SHALL BE FROM HIGH STRENGTH, MARINE GRADE ALUMINIUM ALLOYS OF DURABILITY RATING B TO BS EN 1999;
 - 3. ALL FASTENERS SHALL BE STAINLESS STEEL, AND ALL EXPOSED FASTENERS SHALL BE OF TAMPER-PROOF TYPE TO BS EN ISO 3506;
 - 4. ALL EXPOSED SURFACES SHALL BE POWDER COATED.

NOTES:
1. All measurements indicated in the drawings are approximate and shall be taken as guide only.

	</
--	--	----




- NOTES:**
1. ALL EXTRUDED SECTIONS SHALL BE FABRICATED FROM HIGH STRENGTH, MARINE GRADE ALUMINIUM ALLOYS OF DURABILITY RATING B TO BS EN 1999;
 2. ALL CASTING PARTS SHALL BE PRODUCED VIA PRESSURE DIE CAST METHOD. ALL STRUCTURAL CAST COMPONENTS SHALL BE FROM HIGH STRENGTH, MARINE GRADE ALUMINIUM ALLOYS OF DURABILITY RATING B TO BS EN 1999;
 3. ALL FASTENERS SHALL BE STAINLESS STEEL, AND ALL EXPOSED FASTENERS SHALL BE OF TAMPER-PROOF TYPE TO BS EN ISO 3506;
 4. ALL EXPOSED SURFACES SHALL BE POWDER COATED.

NOTES:


1. All Measurements indicated in the drawings are approximate and shall be taken as guide only.

[illegible]

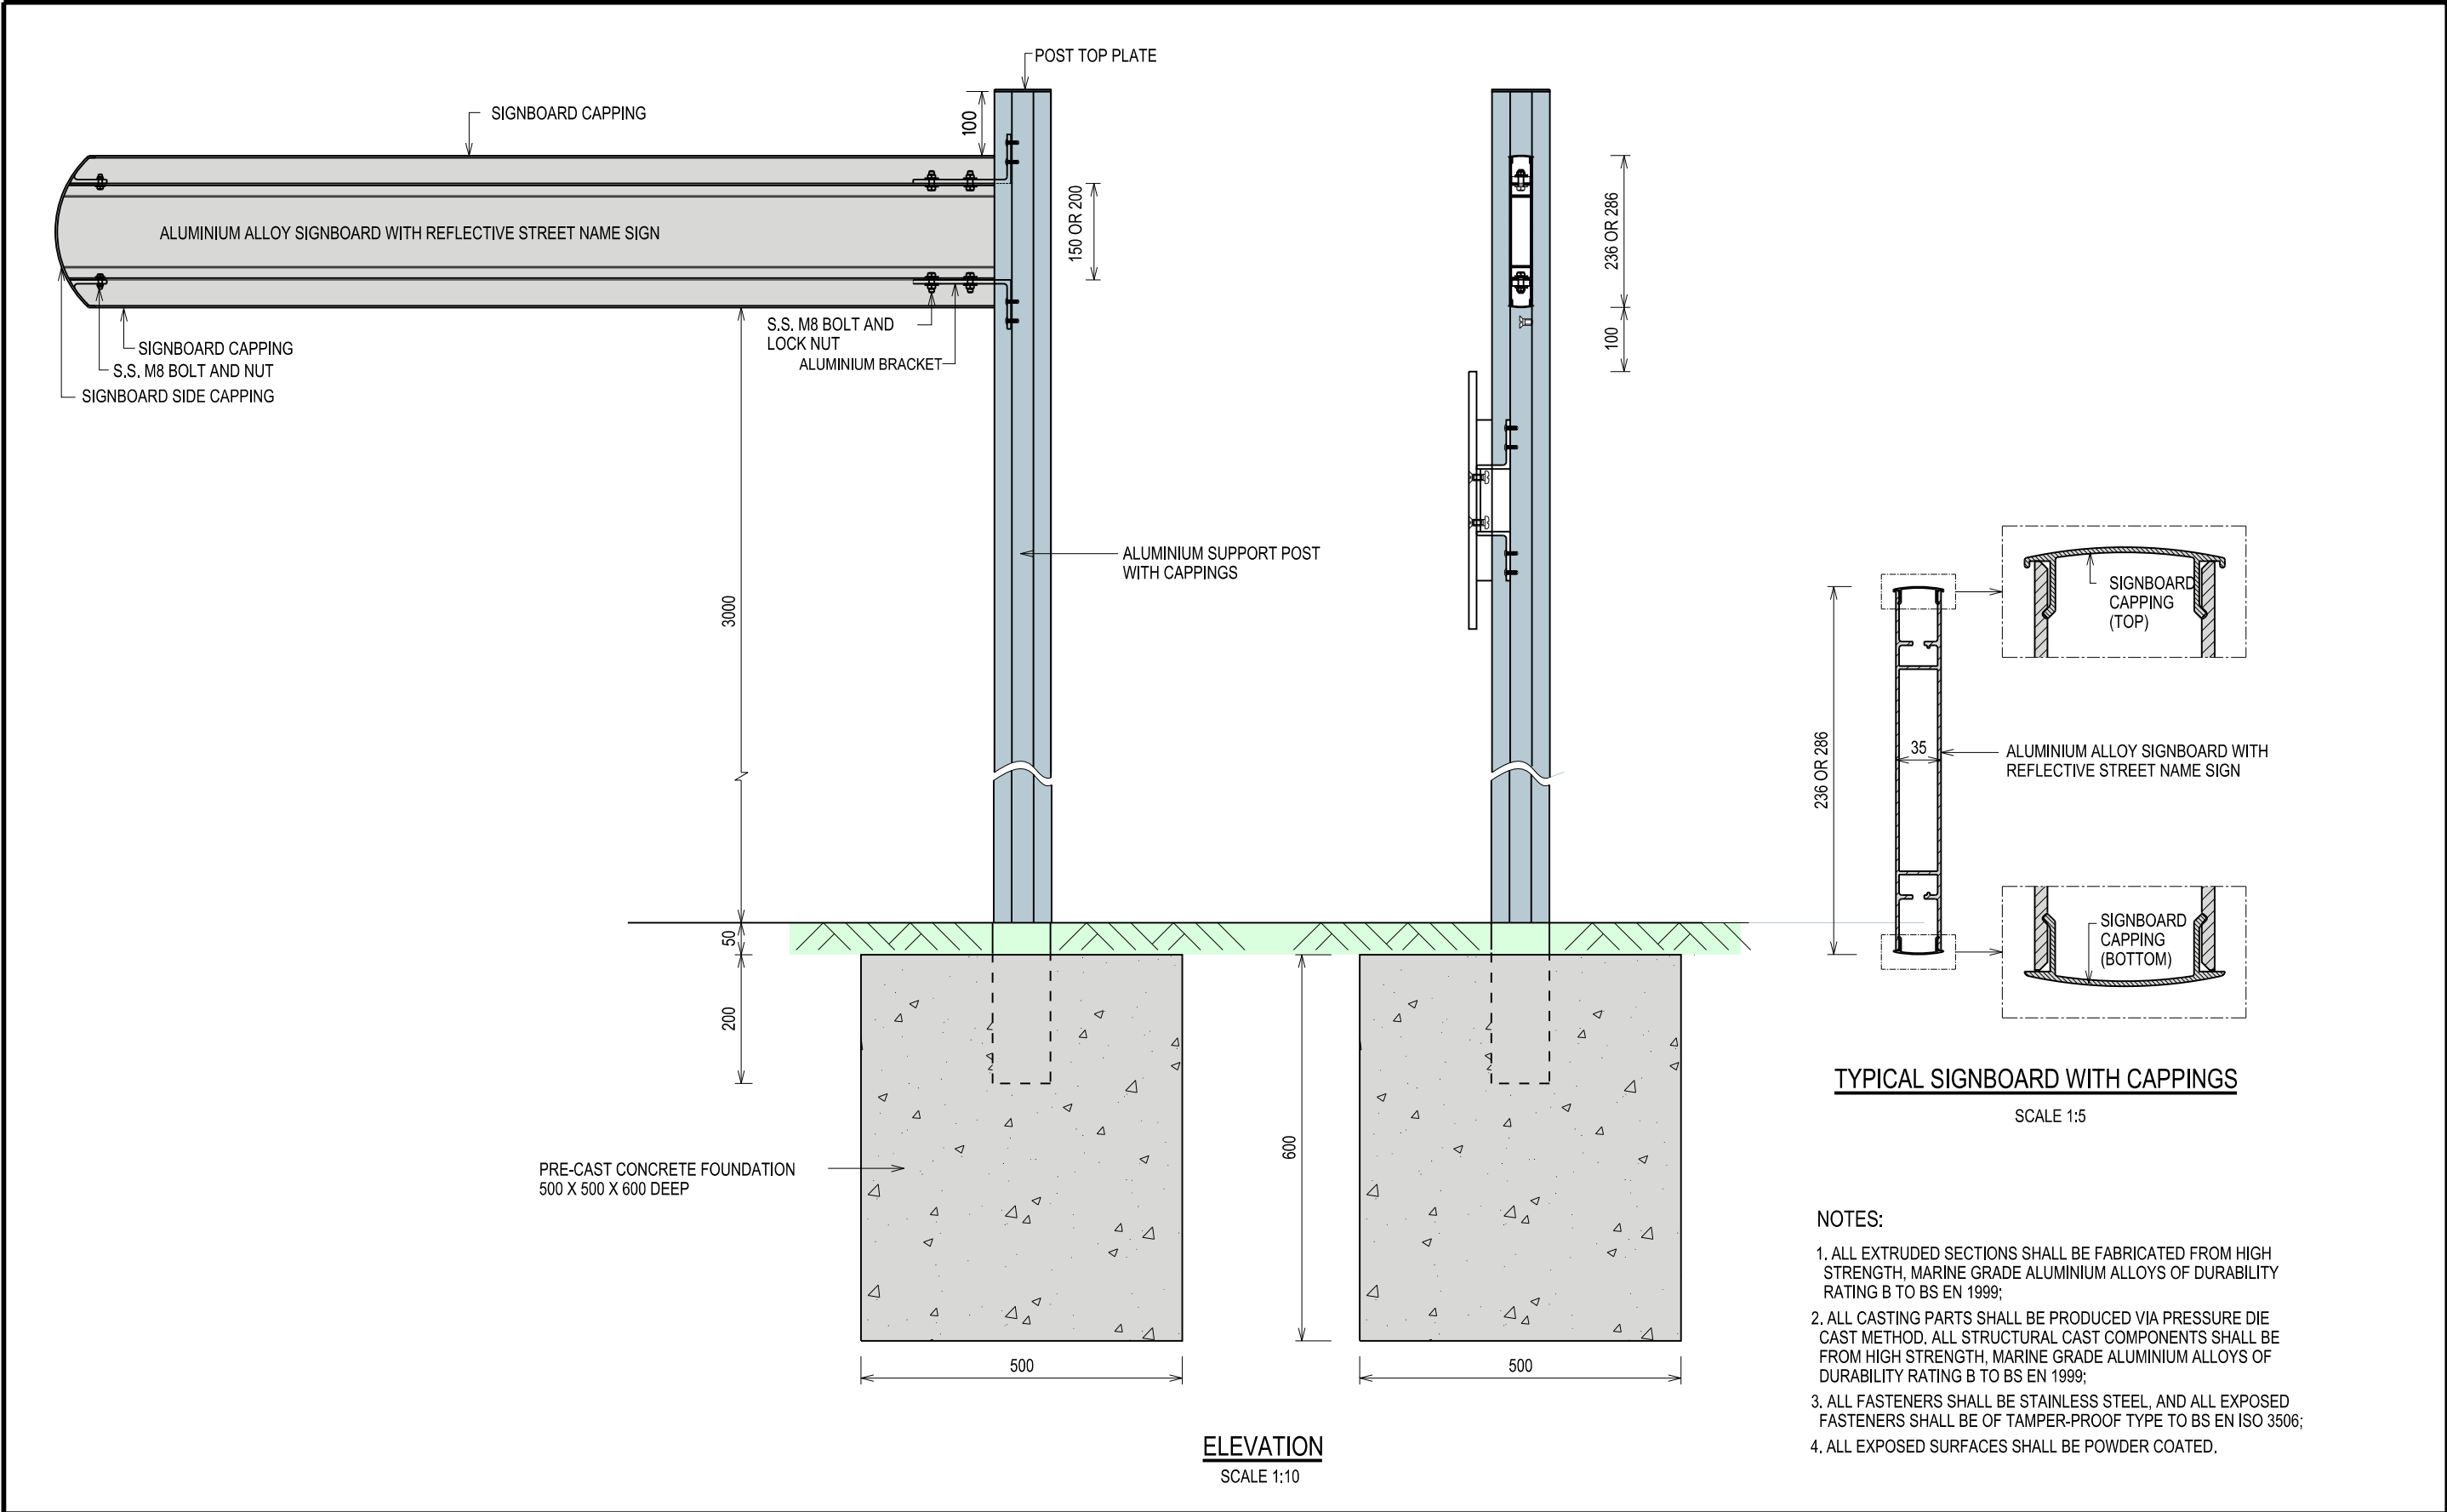


NOTES: 1. All Measurements indicated in the drawings are approximate and shall be taken as guide only.			STANDARD DETAIL	Land Transport Authority		
				DRAWING NO. LTA/SDRE14/20/SNB6		
				DATE OF ISSUE	SCALE	SHEET NO.
				1st APR 2014	AS SHOWN	1 OF 1


STREET NAME SIGN - CANTILEVER STREET NAME SIGN ON VERTICAL SUPPORT POST	
REV. A	OCT 2015
REV.	DATE

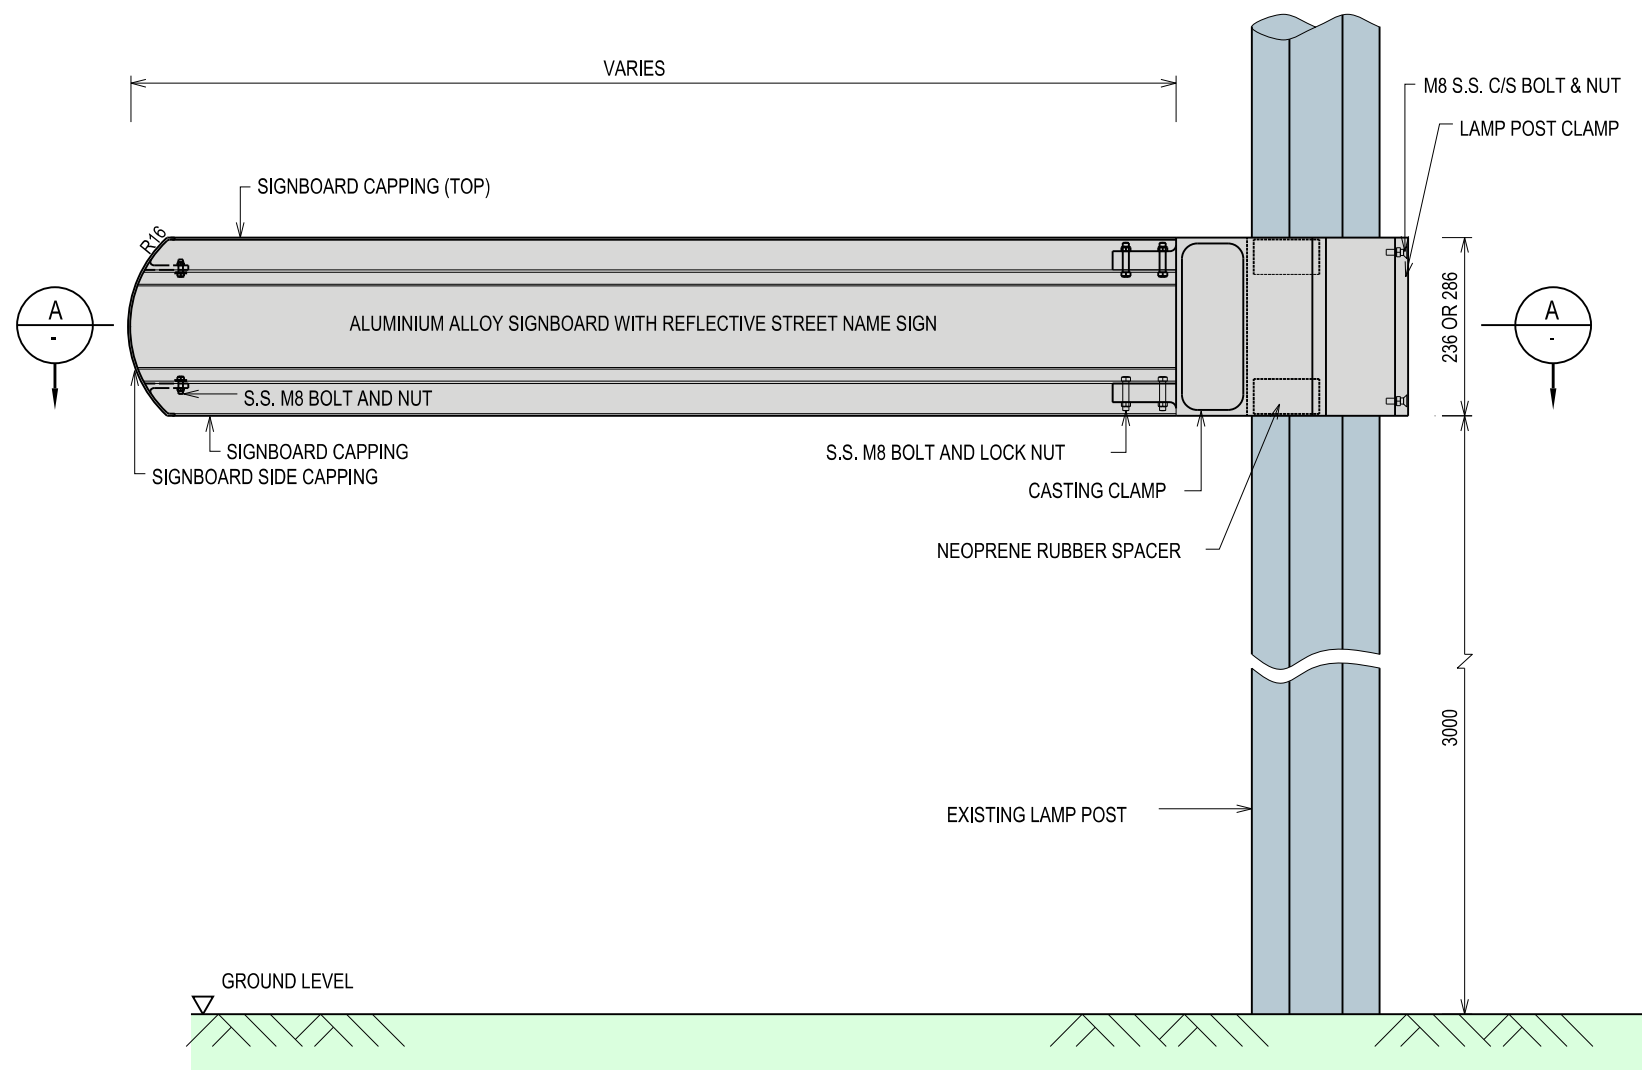

ELEVATION
SCALE 1:10

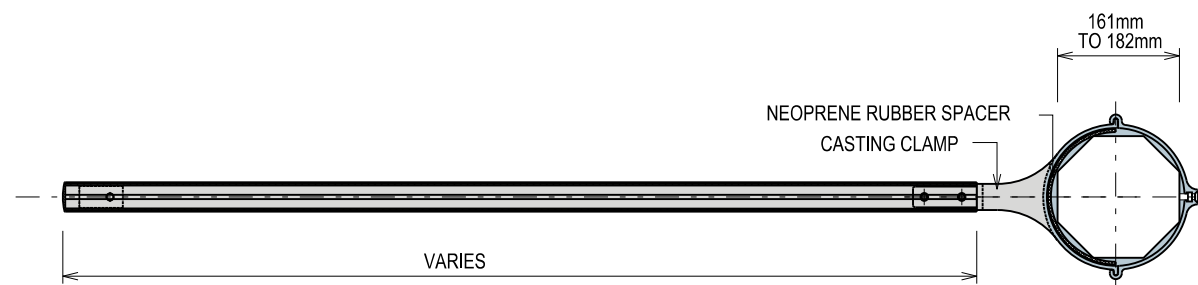

SECTION A-A
SCALE 1:10



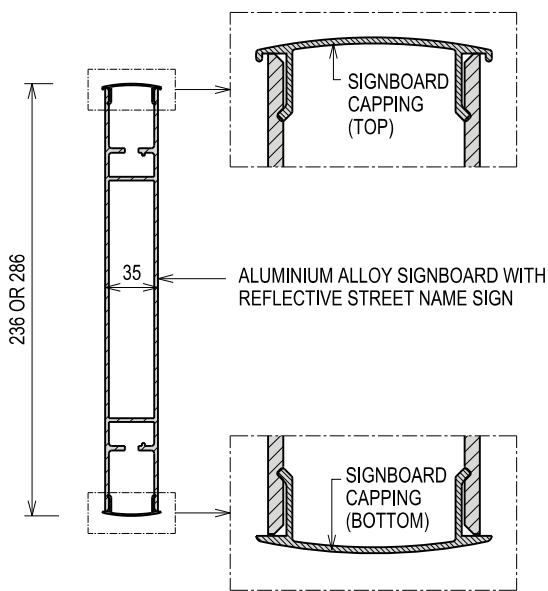


TYPICAL SIGNBOARD WITH CAPPINGS
SCALE 1:5

- NOTES:
1. ALL EXTRUDED SECTIONS SHALL BE FABRICATED FROM HIGH STRENGTH, MARINE GRADE ALUMINIUM ALLOYS OF DURABILITY RATING B TO BS EN 1999;
 2. ALL CASTING PARTS SHALL BE PRODUCED VIA PRESSURE DIE CAST METHOD. ALL STRUCTURAL CAST COMPONENTS SHALL BE FROM HIGH STRENGTH, MARINE GRADE ALUMINIUM ALLOYS OF DURABILITY RATING B TO BS EN 1999;
 3. ALL FASTENERS SHALL BE STAINLESS STEEL, AND ALL EXPOSED FASTENERS SHALL BE OF TAMPER-PROOF TYPE TO BS EN ISO 3506;
 4. ALL EXPOSED SURFACES SHALL BE POWDER COATED.

NOTES:
1. All Measurements indicated in the drawings are approximate and shall be taken as guide only.

STANDARD DETAIL		Land Transport Authority	
STREET NAME SIGN - CANTILEVER STREET NAME SIGN ON EXISTING LAMP POST		DRAWING NO. LTA/SDRE14/20/SNB7	
		DATE OF ISSUE	REV. A
		1st APR 2014	AS SHOWN
		SHEET NO. 1 OF 1	

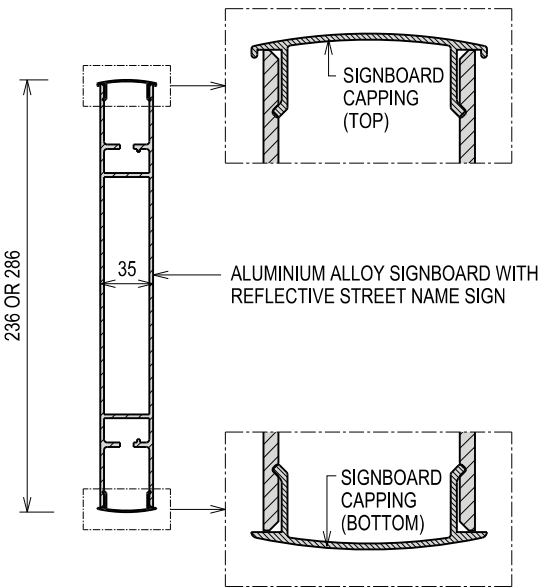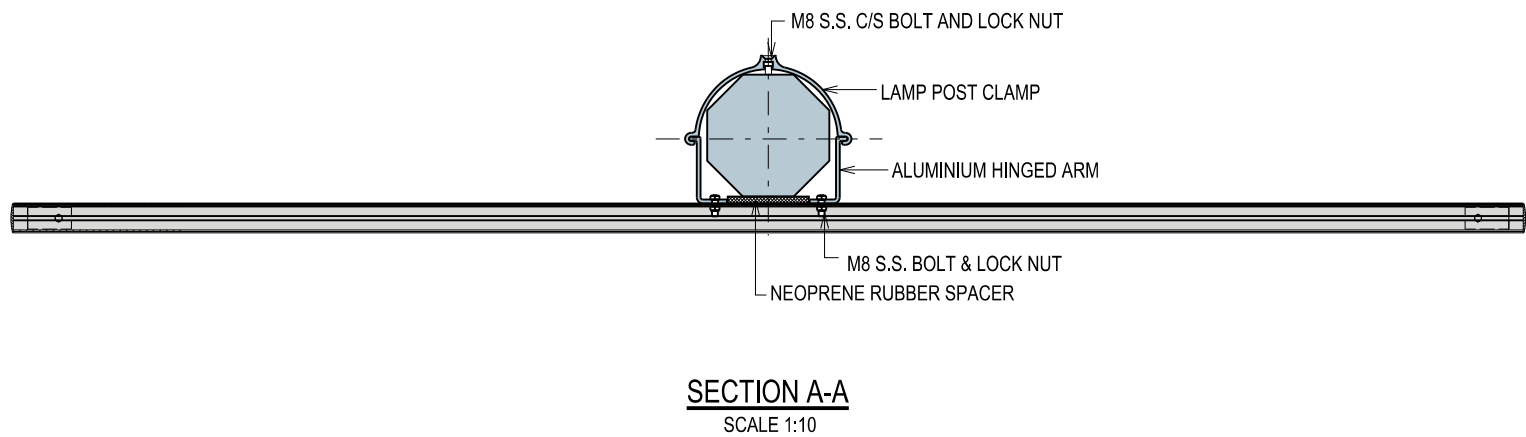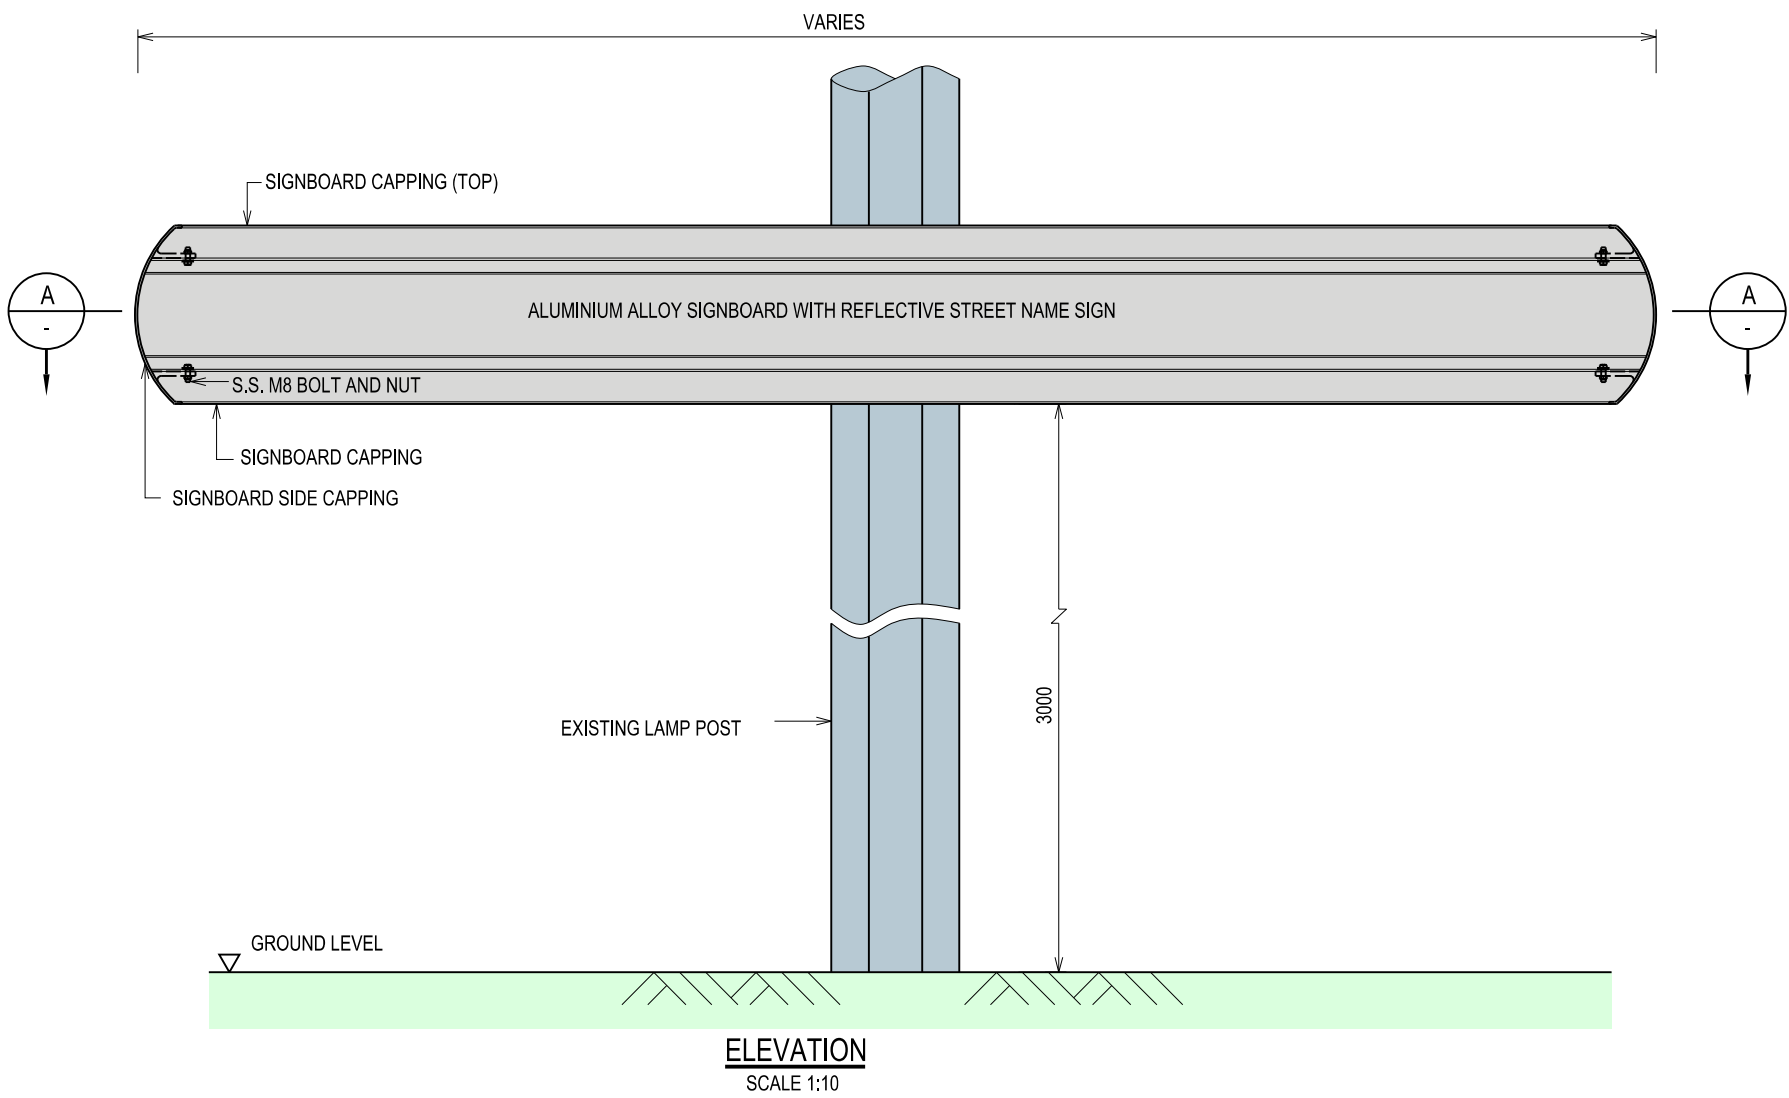






TYPICAL SIGNBOARD WITH CAPPINGS
SCALE 1:5

- NOTES:
- 1. ALL EXTRUDED SECTIONS SHALL BE FABRICATED FROM HIGH STRENGTH, MARINE GRADE ALUMINIUM ALLOYS OF DURABILITY RATING B TO BS EN 1999;
 - 2. ALL CASTING PARTS SHALL BE PRODUCED VIA PRESSURE DIE CAST METHOD. ALL STRUCTURAL CAST COMPONENTS SHALL BE FROM HIGH STRENGTH, MARINE GRADE ALUMINIUM ALLOYS OF DURABILITY RATING B TO BS EN 1999;
 - 3. ALL FASTENERS SHALL BE STAINLESS STEEL, AND ALL EXPOSED FASTENERS SHALL BE OF TAMPER-PROOF TYPE TO BS EN ISO 3506;
 - 4. ALL EXPOSED SURFACES SHALL BE POWDER COATED.

NOTES:

- 1. All Measurements indicated in the drawings are approximate and shall be taken as guide only.


STANDARD DETAIL		Land Transport Authority		
STREET NAME SIGN SINGLE SIDE STREET NAME SIGN ON EXISTING LAMP POST		DRAWING NO.		REV.
		LTA/SDRE14/20/SNB8		A
		DATE OF ISSUE	SCALE	SHEET NO.
		1st APR 2014	AS SHOWN	1 OF 1

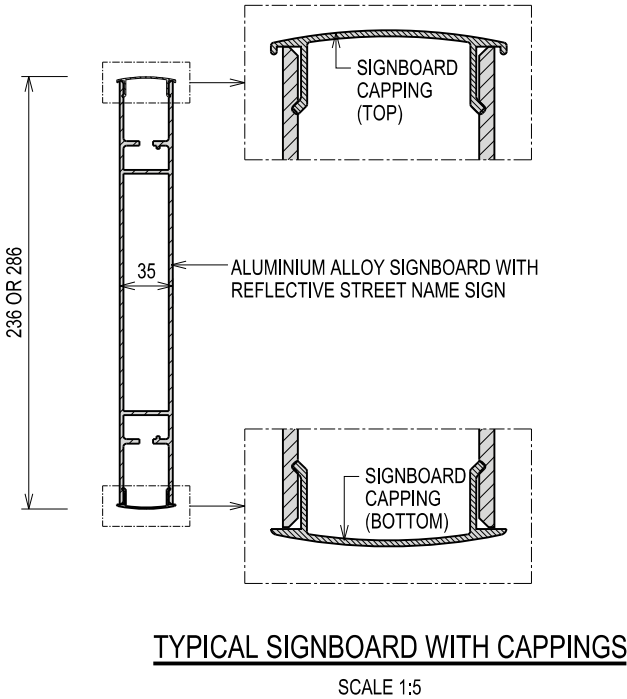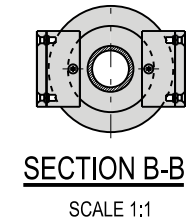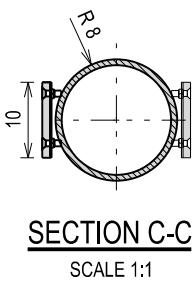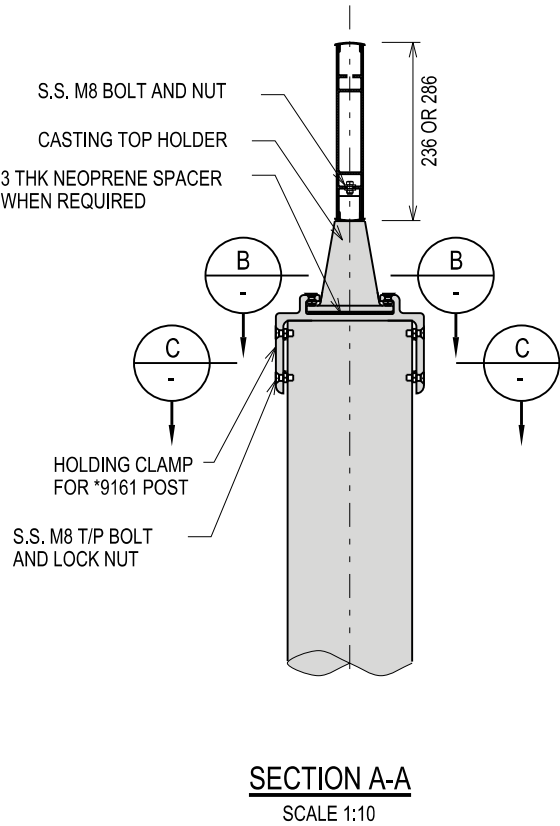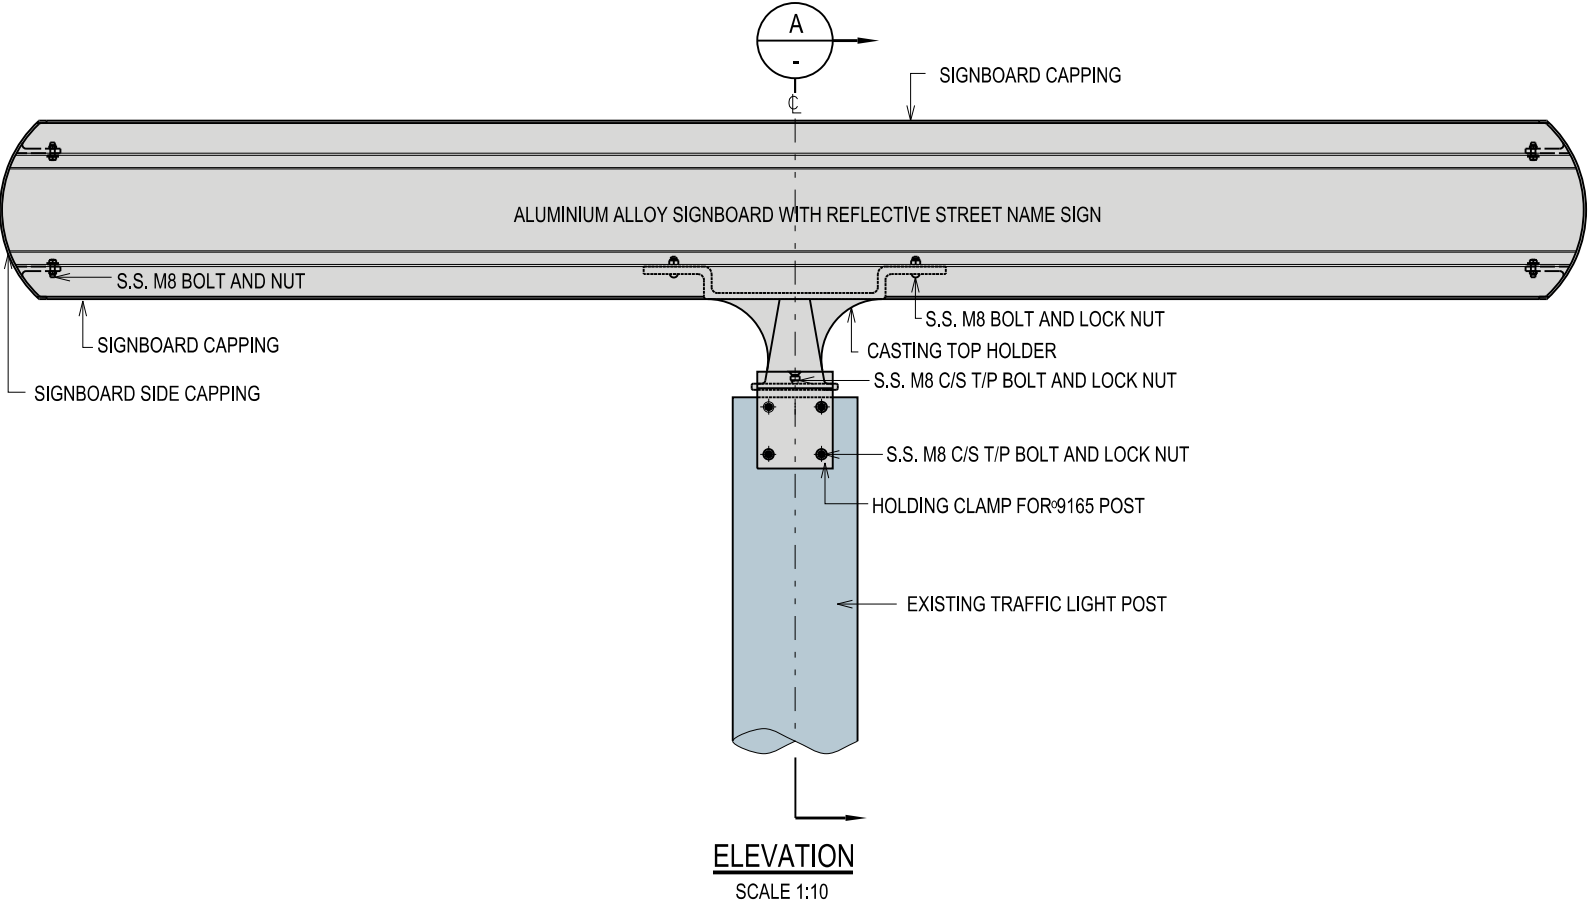


- NOTES:
1. ALL EXTRUDED SECTIONS SHALL BE FABRICATED FROM HIGH STRENGTH, MARINE GRADE ALUMINIUM ALLOYS OF DURABILITY RATING B TO BS EN 1999;
 2. ALL CASTING PARTS SHALL BE PRODUCED VIA PRESSURE DIE CAST METHOD. ALL STRUCTURAL CAST COMPONENTS SHALL BE FROM HIGH STRENGTH, MARINE GRADE ALUMINIUM ALLOYS OF DURABILITY RATING B TO BS EN 1999;
 3. ALL FASTENERS SHALL BE STAINLESS STEEL, AND ALL EXPOSED FASTENERS SHALL BE OF TAMPER-PROOF TYPE TO BS EN ISO 3506;
 4. ALL EXPOSED SURFACES SHALL BE POWDER COATED.

NOTES:
1. All Measurements indicated in the drawings are approximate and shall be taken as guide only.


			STANDARD DETAIL		Land Transport Authority	
			STREET NAME SIGN ON TRAFFIC POST			
					REV. A	
			DRAWING NO. LTA/SDRE14/20/SNB9			
A	OCT 2015		DATE OF ISSUE 1st APR 2014	SCALE AS SHOWN	SHEET NO. 1 OF 1	
REV.	DATE					

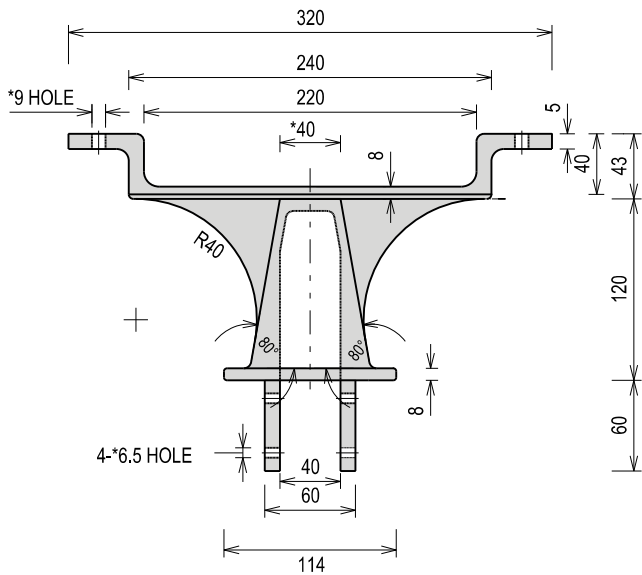


CASTING TOP HOLDER (C1)
SCALE 1:5

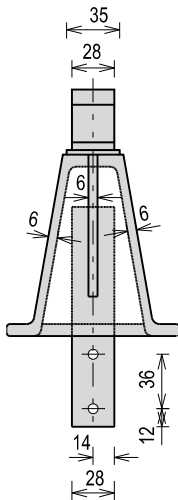


CASTING CLAMP (C2,C3)
FOR C2 H=236, FOR C3 H=286
SCALE 1:5

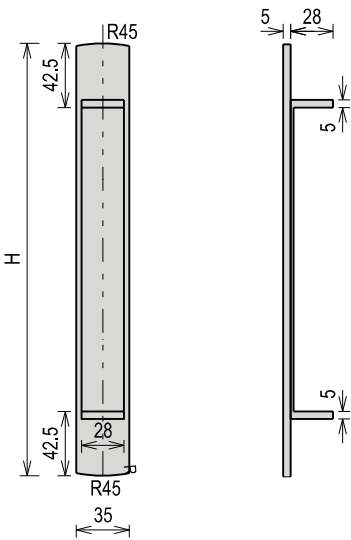


CASTING SIDE CAPPING (C7,C8)
FOR C7 H=236, FOR C8 H=286
SCALE 1:5

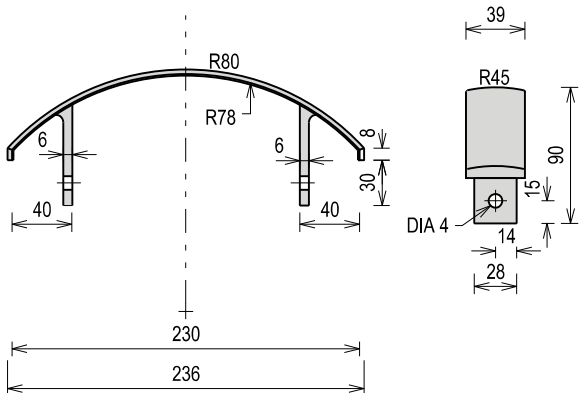


CASTING SIDE CAPPING (C4)
SCALE 1:5

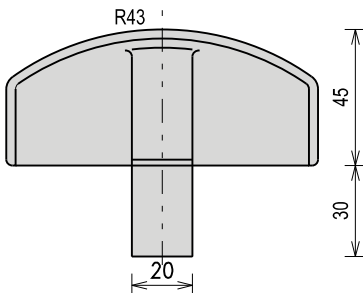

CASTING POST CAP (C9)
SCALE 1:2.5

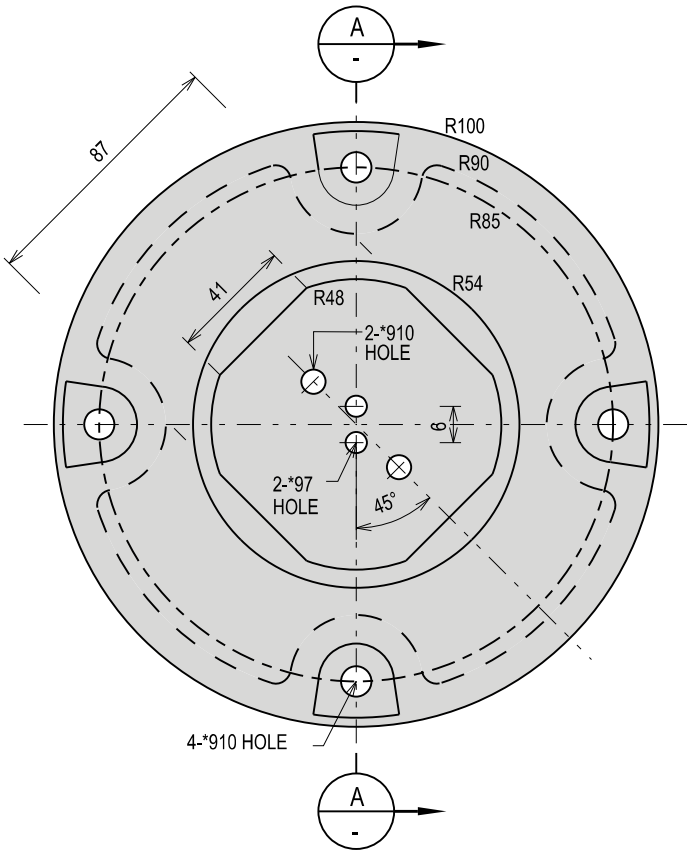

CASTING CAST BASE (C6)
SCALE 1:2.5

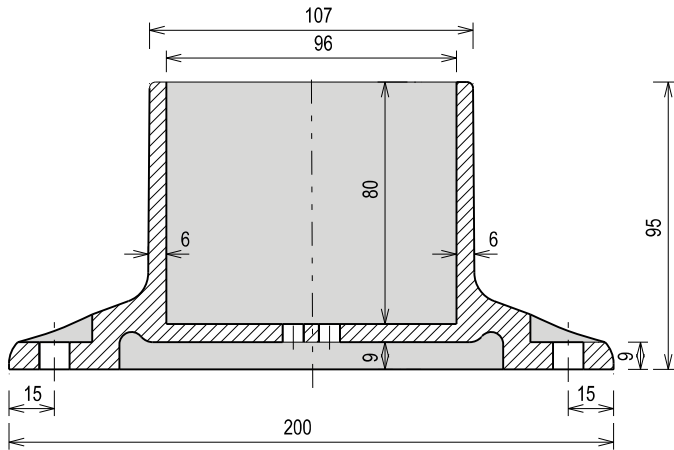

SECTION A-A
SCALE 1:2.5

- NOTES:
1. ALL CASTING PARTS SHALL BE PRODUCED VIA PRESSURE DIE CAST METHOD. ALL STRUCTURAL CAST COMPONENTS SHALL BE FROM HIGH STRENGTH MARINE GRADE ALUMINIUM ALLOYS OF DURABILITY RATING B TO BS EN 1999.
 2. ALL EXPOSED SURFACES SHALL BE POWDER COATED.

NOTES:
1. All measurements indicated in the drawings are approximate and shall be taken as guide only.

STANDARD DETAIL

Land Transport Authority

STREET NAME SIGN -
CASTING PARTS

DRAWING NO.
LTA/SDRE14/20/SNB11


REV.
A

DATE OF ISSUE
1st APR 2014


SCALE
AS SHOWN

SHEET NO.
1 OF 1




REV. DATE

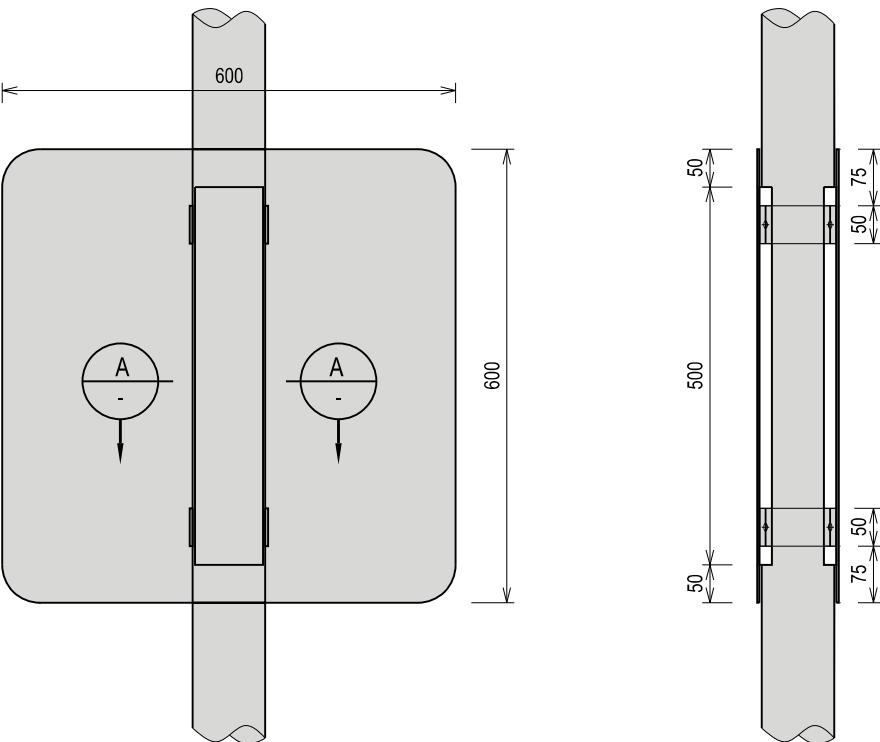


TRAFFIC SIGN ON SUPPORT POST
DOUBLE SIDE TYPE
SCALE 1:10

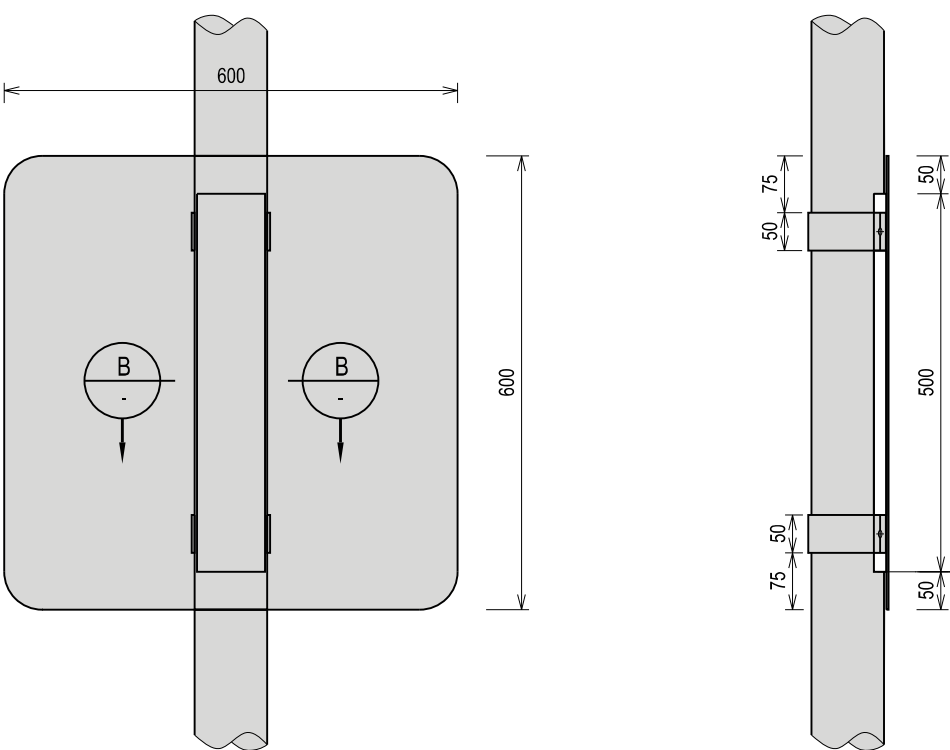


TRAFFIC SIGN ON SUPPORT POST
SINGLE SIDE TYPE
SCALE 1:10

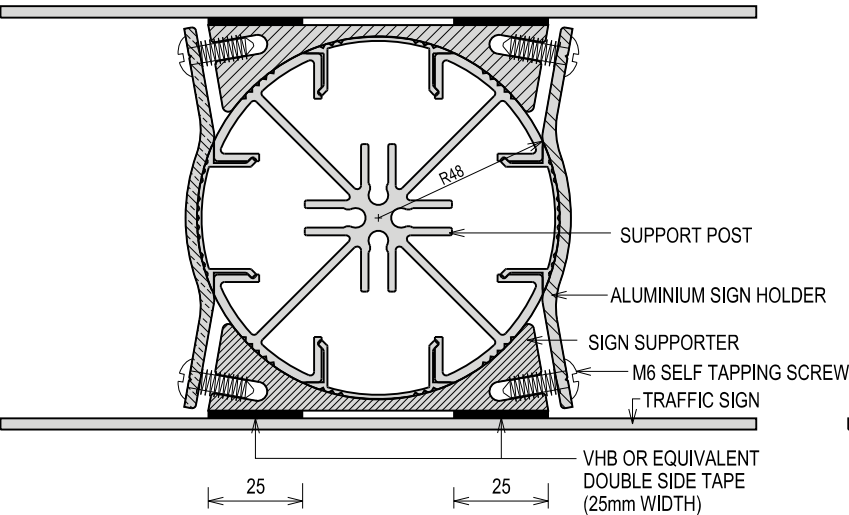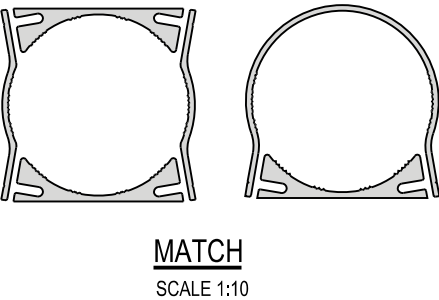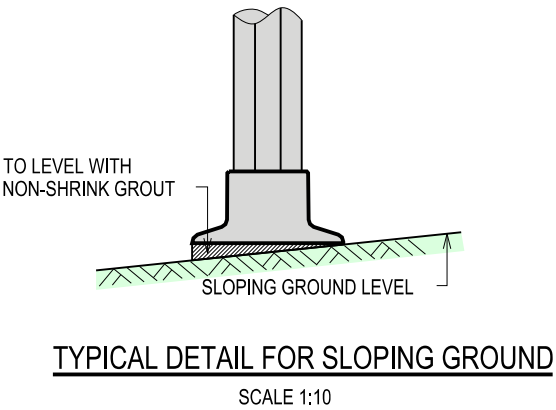


SECTION A-A
SCALE 1:2

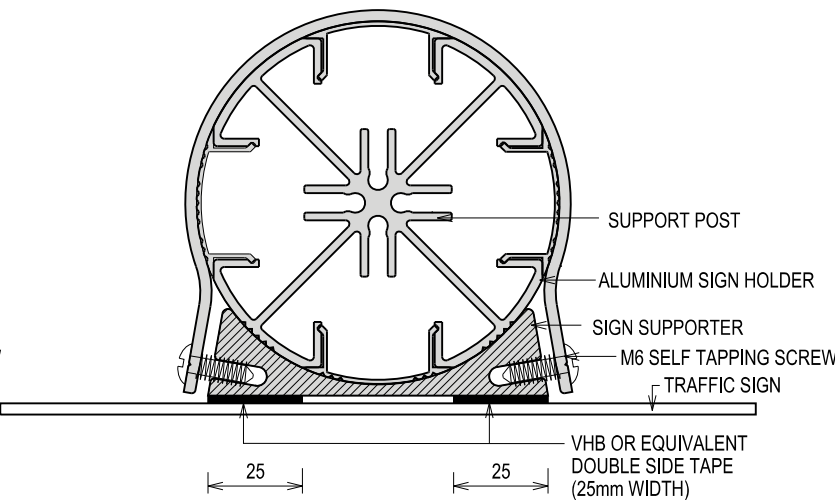


SECTION B-B
SCALE 1:2

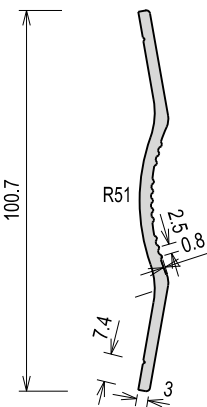

ALUMINIUM SIGN HOLDER
SCALE 1:2

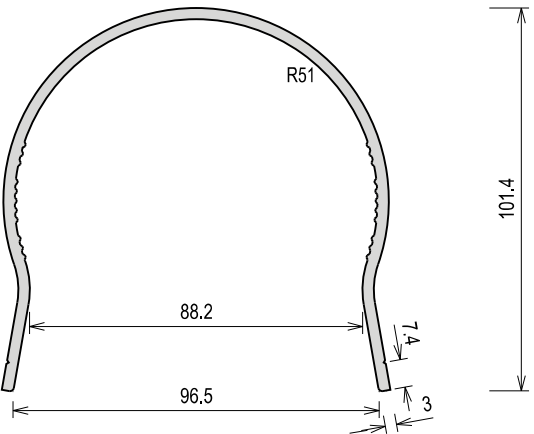

ALUMINIUM SIGN HOLDER
SCALE 1:2

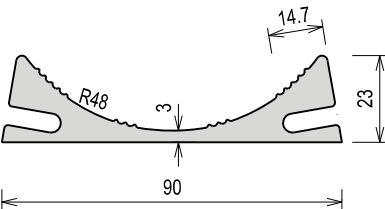

SIGN SUPPORTER
SCALE 1:2

NOTES:

1. All measurements indicated in the drawings are approximate and shall be taken as guide only.

STANDARD DETAIL		Land Transport Authority	
STREET NAME SIGN - TRAFFIC SIGN ON SUPPORT POST	DRAWING NO.	LTA/SDRE14/20/SNB12	
	DATE OF ISSUE	SCALE	SHEET NO.
	1st APR 2014	AS SHOWN	1 OF 1
REV.	DATE		