


CHAPTER 7

DIRECTIONAL SIGNS


DRAWING TITLE	DRAWING NO.	REVISION
LETTERINGS FOR DIRECTIONAL SIGNS - UPPER CASE (SHEET 1 OF 2)	LTA/SDRE14/7/DIR1	-
LETTERINGS FOR DIRECTIONAL SIGNS - UPPER CASE (SHEET 2 OF 2)	LTA/SDRE14/7/DIR2	-
LETTERINGS FOR DIRECTIONAL SIGNS - LOWER CASE (SHEET 1 OF 2)	LTA/SDRE14/7/DIR3	-
LETTERINGS FOR DIRECTIONAL SIGNS - LOWER CASE (SHEET 2 OF 2)	LTA/SDRE14/7/DIR4	-
NUMBERS FOR DIRECTIONAL SIGNS	LTA/SDRE14/7/DIR5	-
ARROWS FOR DIRECTIONAL SIGNS	LTA/SDRE14/7/DIR6	-
NOTES FOR DIRECTIONAL SIGNS (SHEET 1 OF 2)	LTA/SDRE14/7/DIR7	A
NOTES FOR DIRECTIONAL SIGNS (SHEET 2 OF 2)	LTA/SDRE14/7/DIR8	A

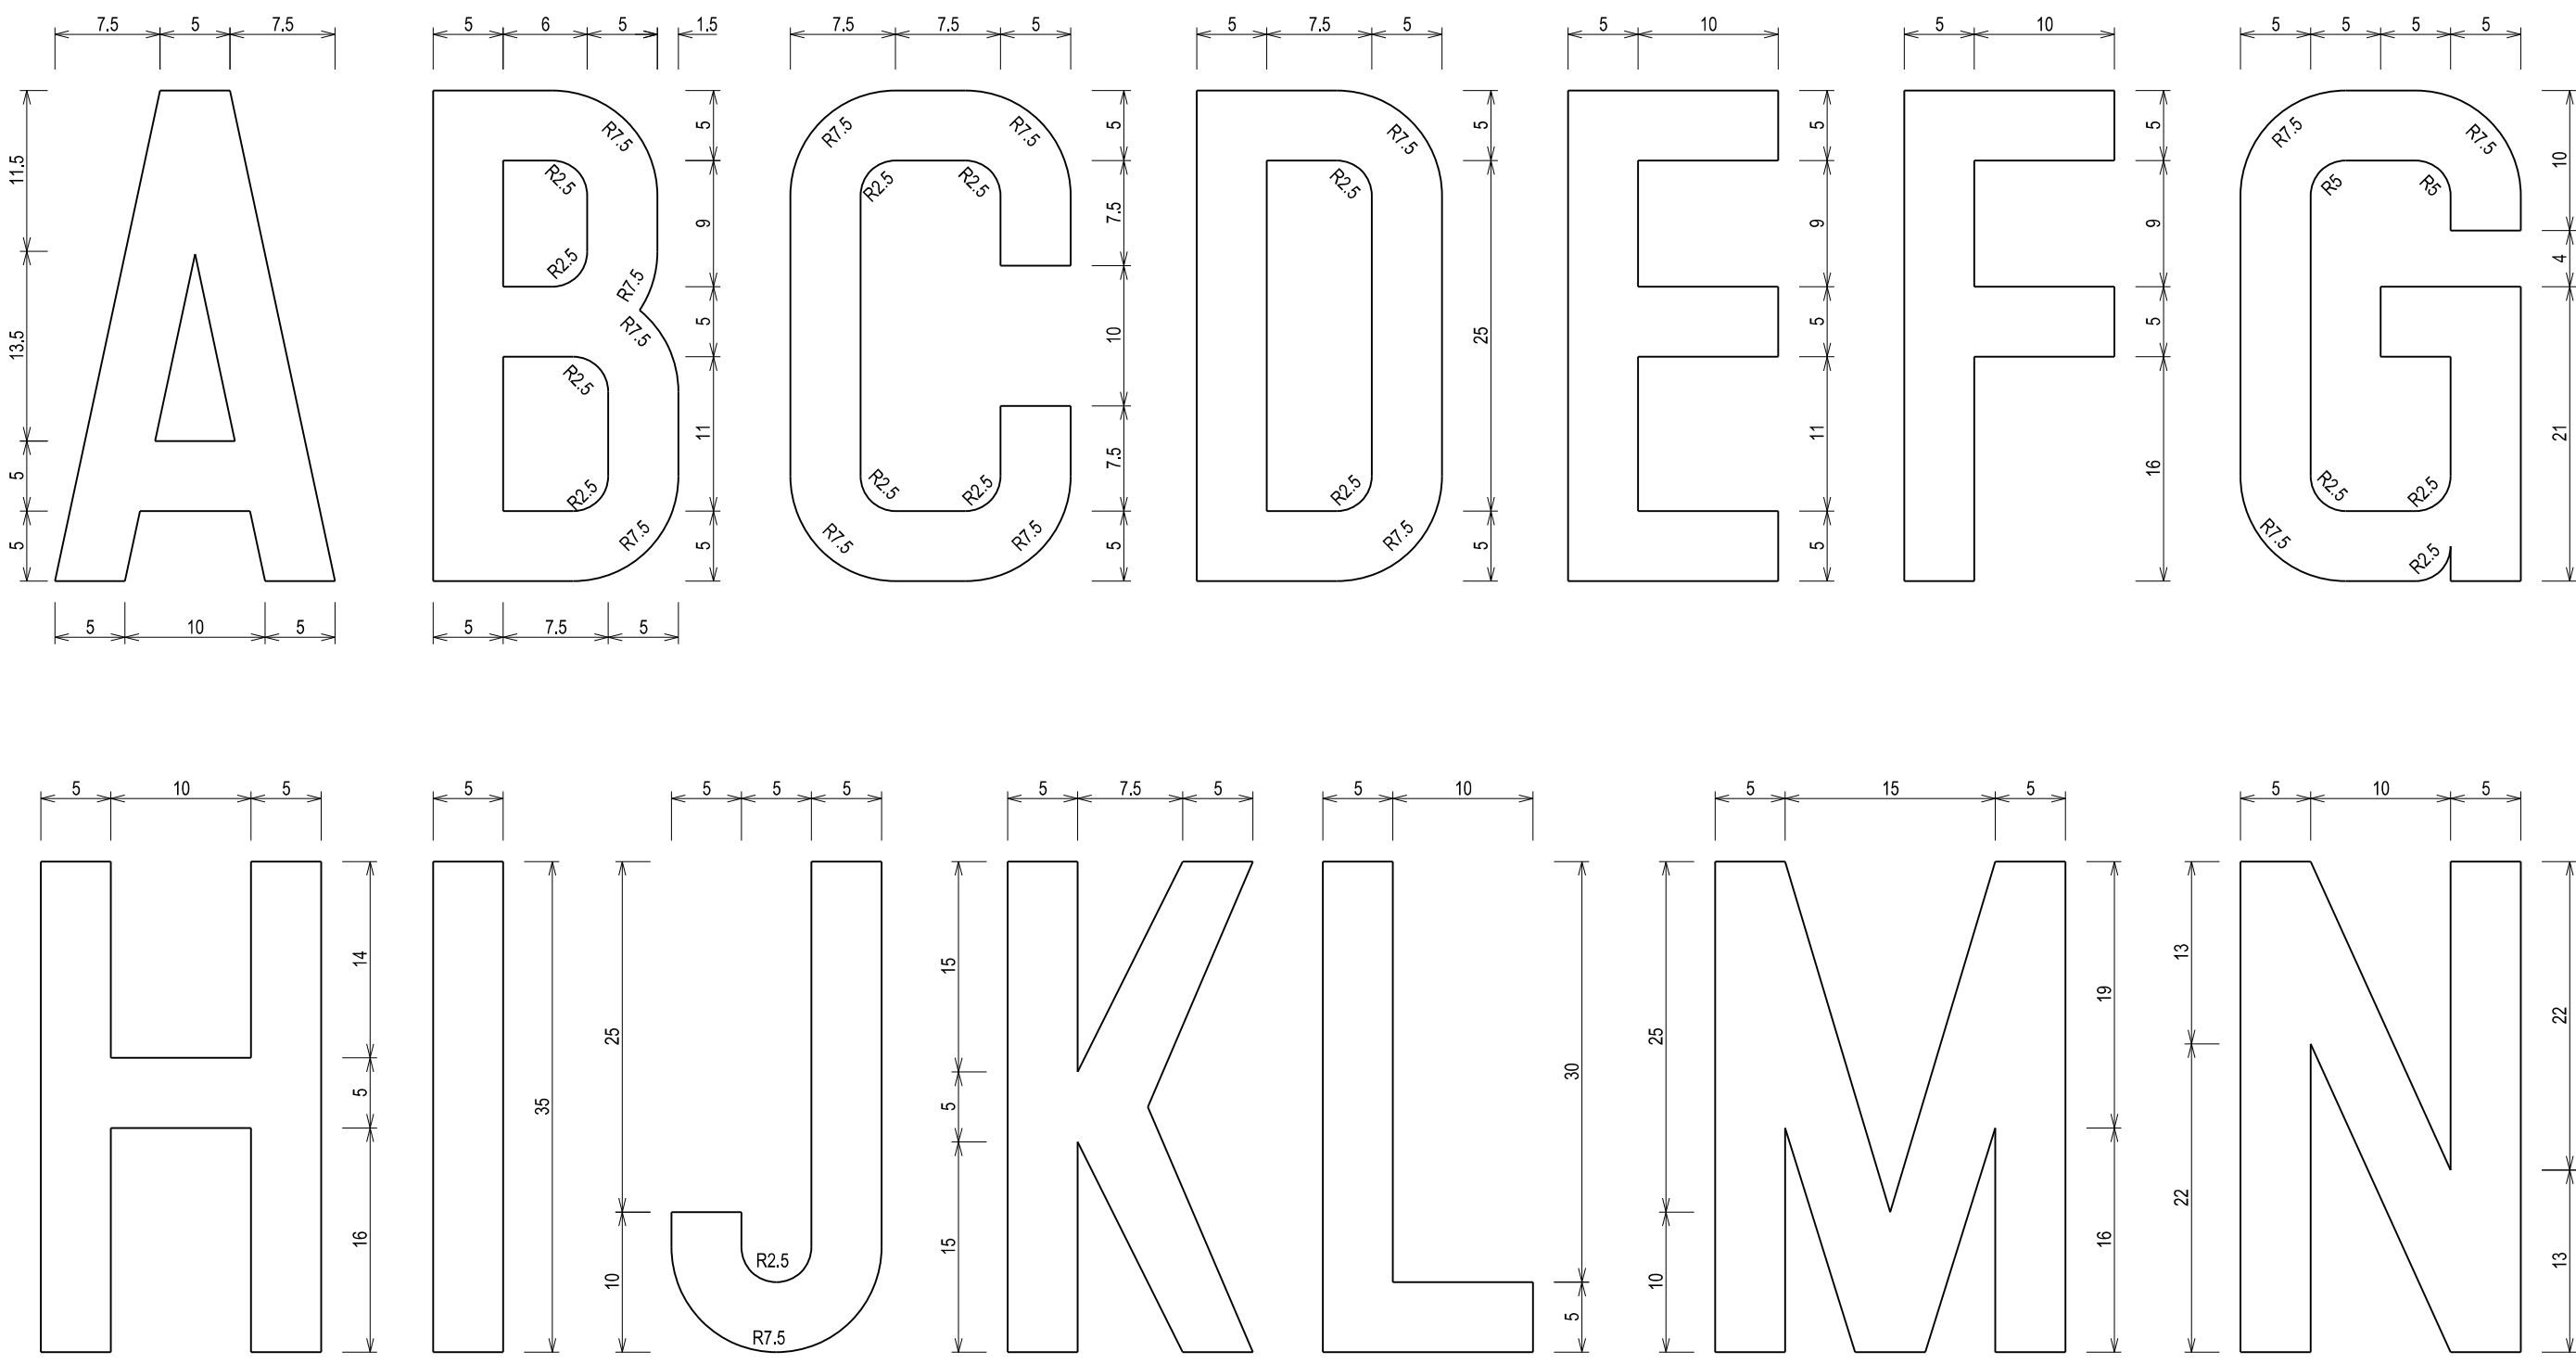


NOTES:

1. For colour combinations, sizes / dimensions and standard spacing between 2 letters, refer to Drawings No LTA/SDRE14/7/DIR7 & 8.

	</
--	--	----

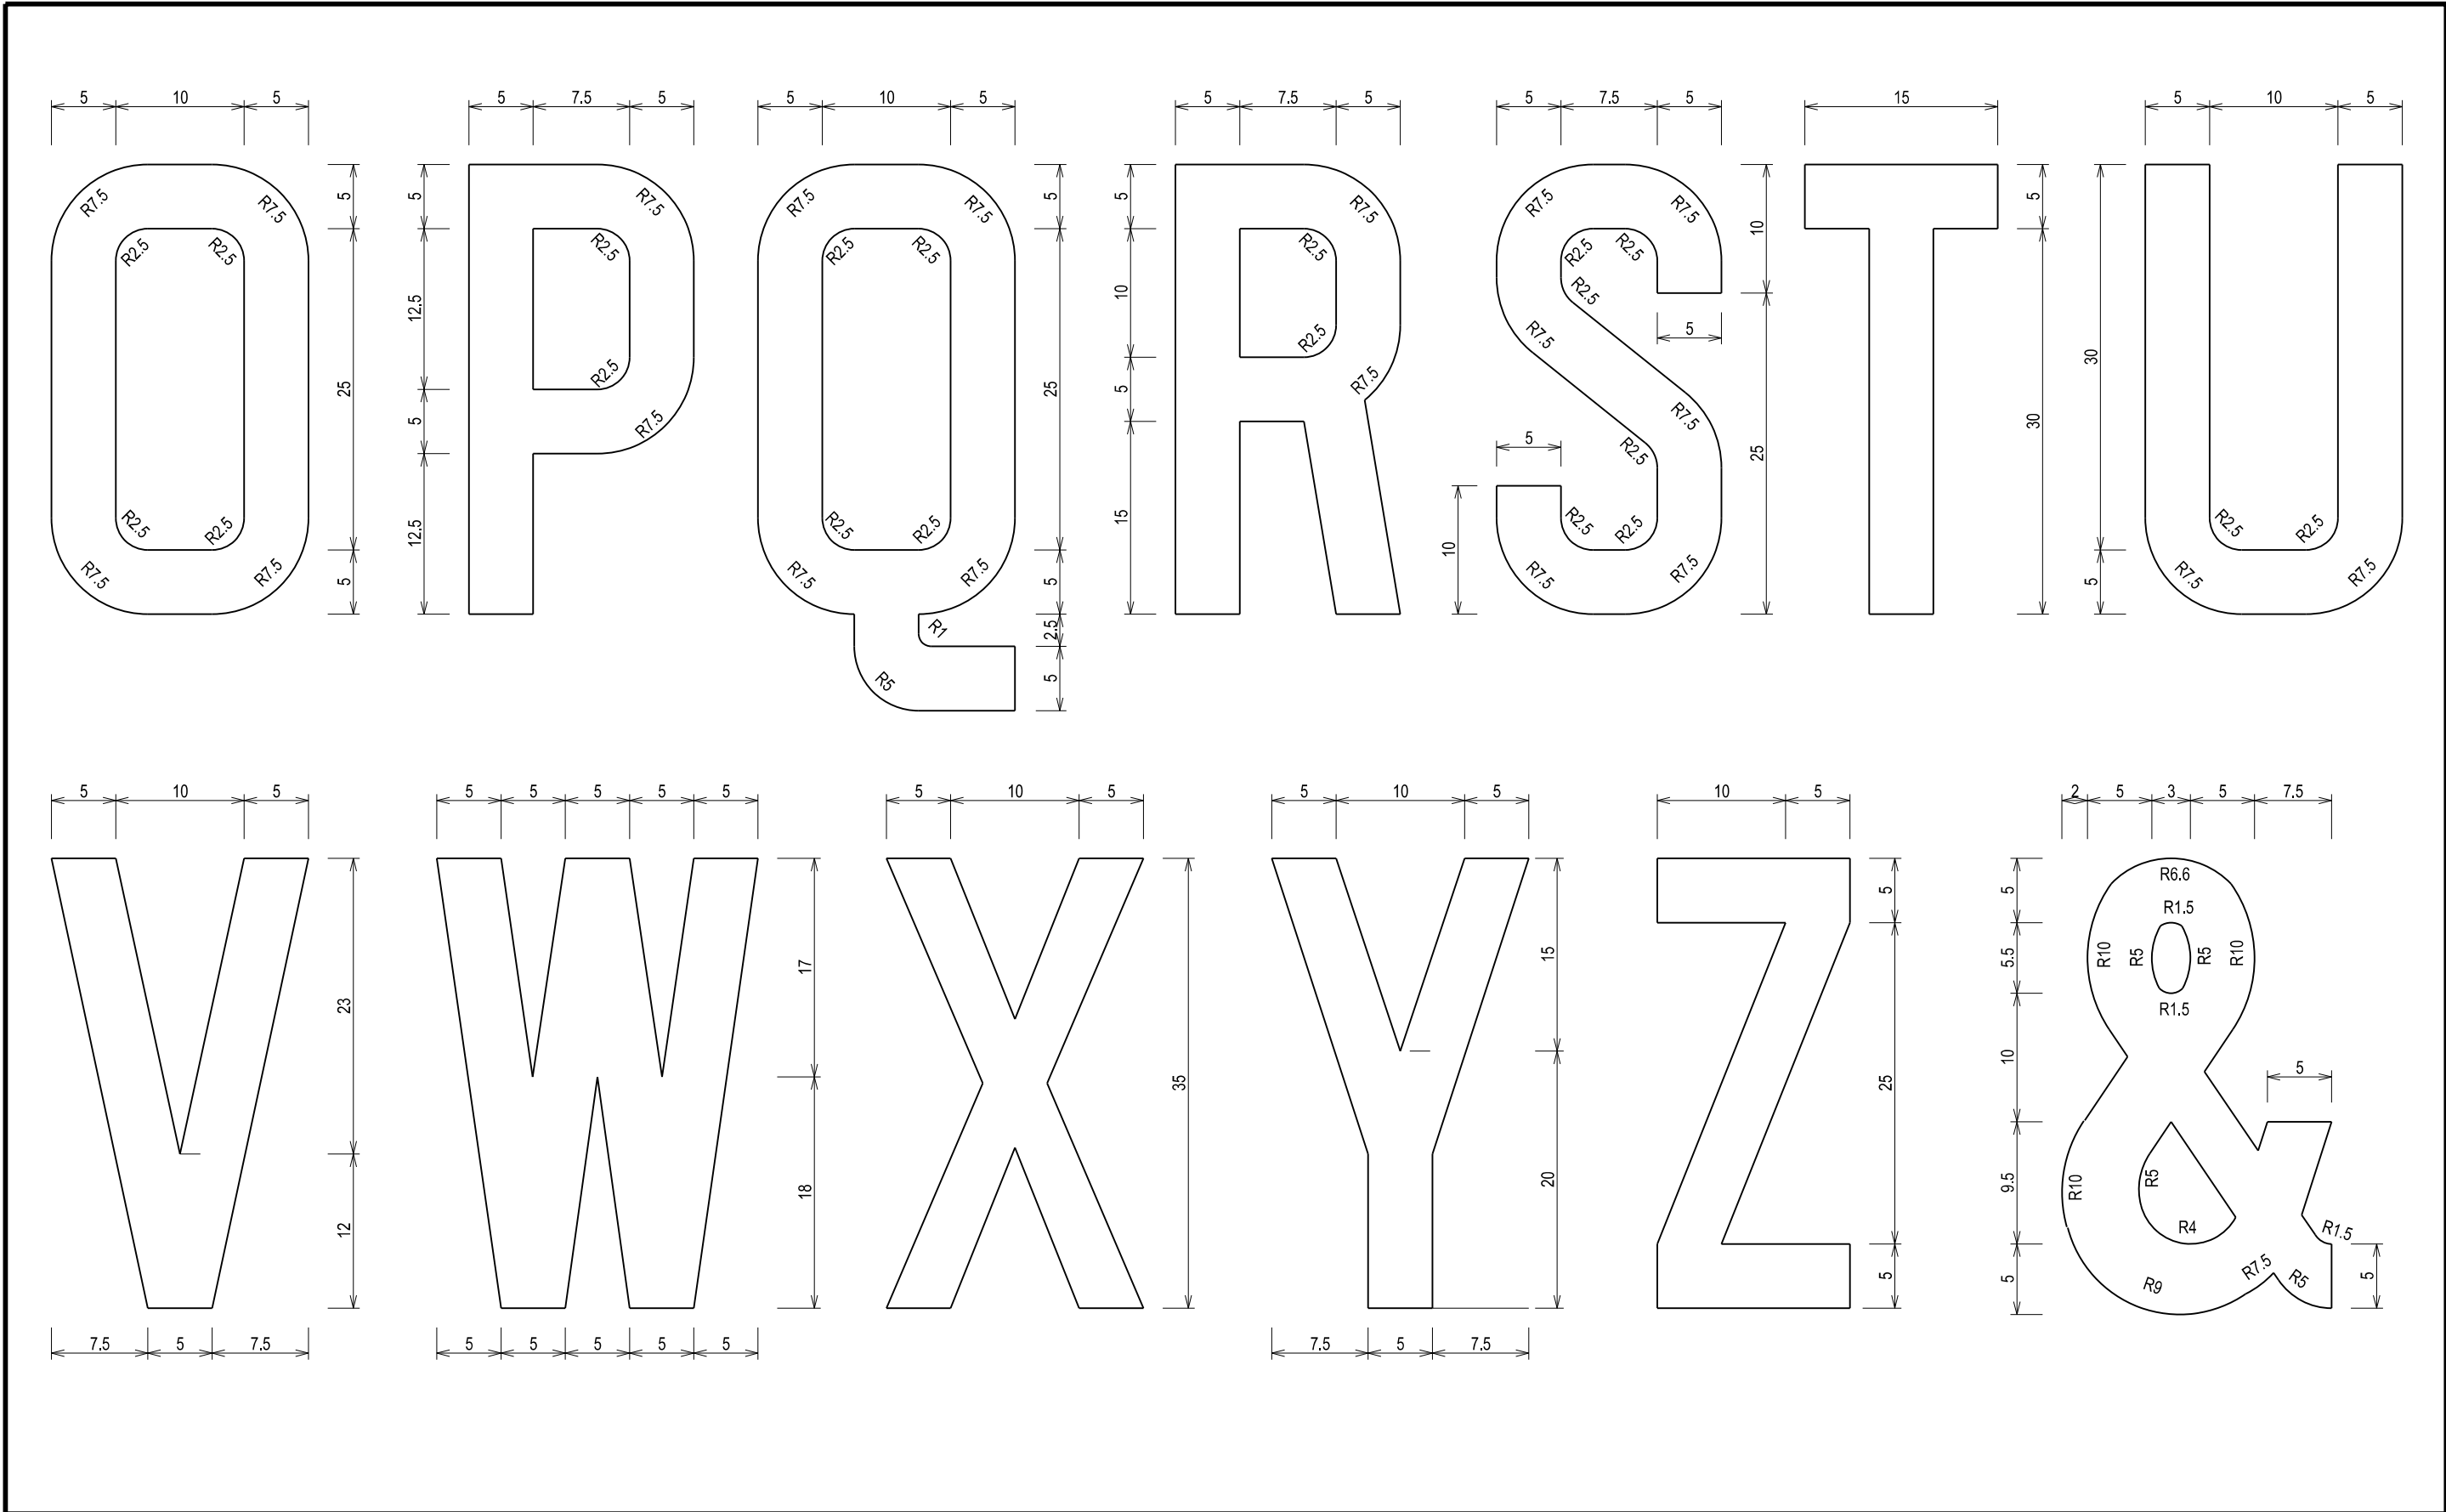


	</
--	--	----

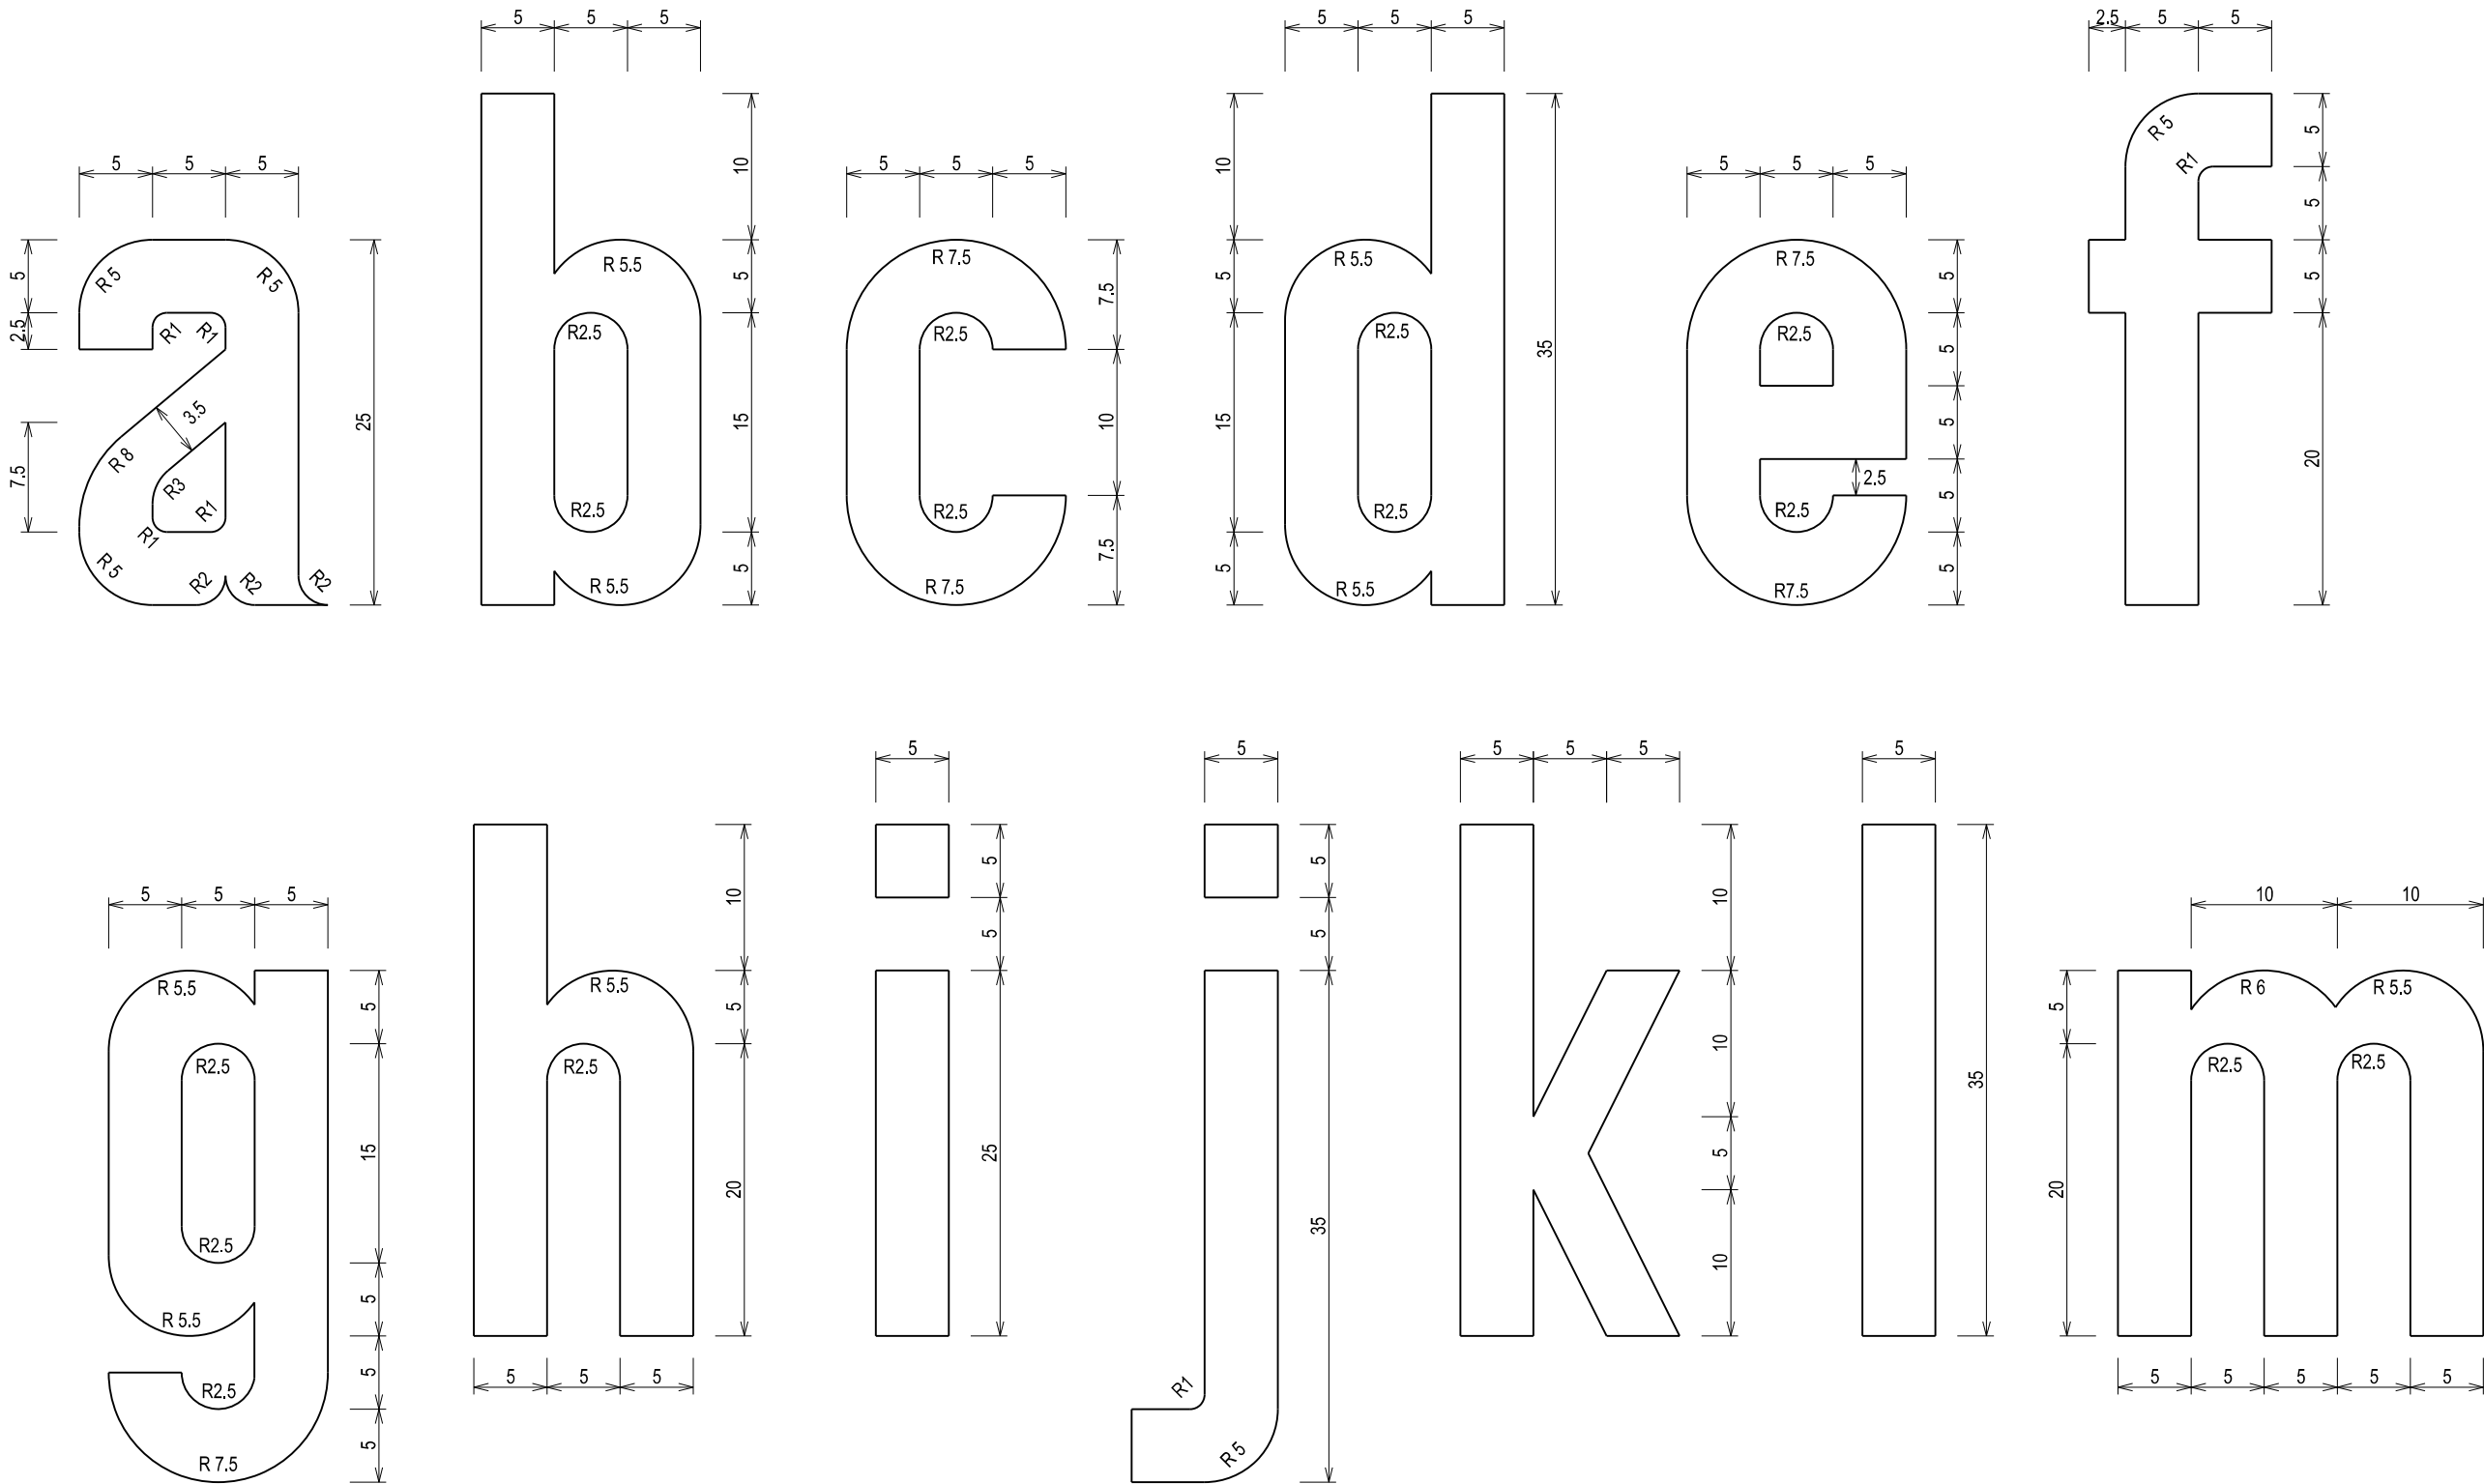


NOTES:
1. For colour combinations, sizes / dimensions and standard spacing between 2 letters, refer to Drawings No. LTA/SDRE14/7/DIR7 & 8.

	</
--	--	----

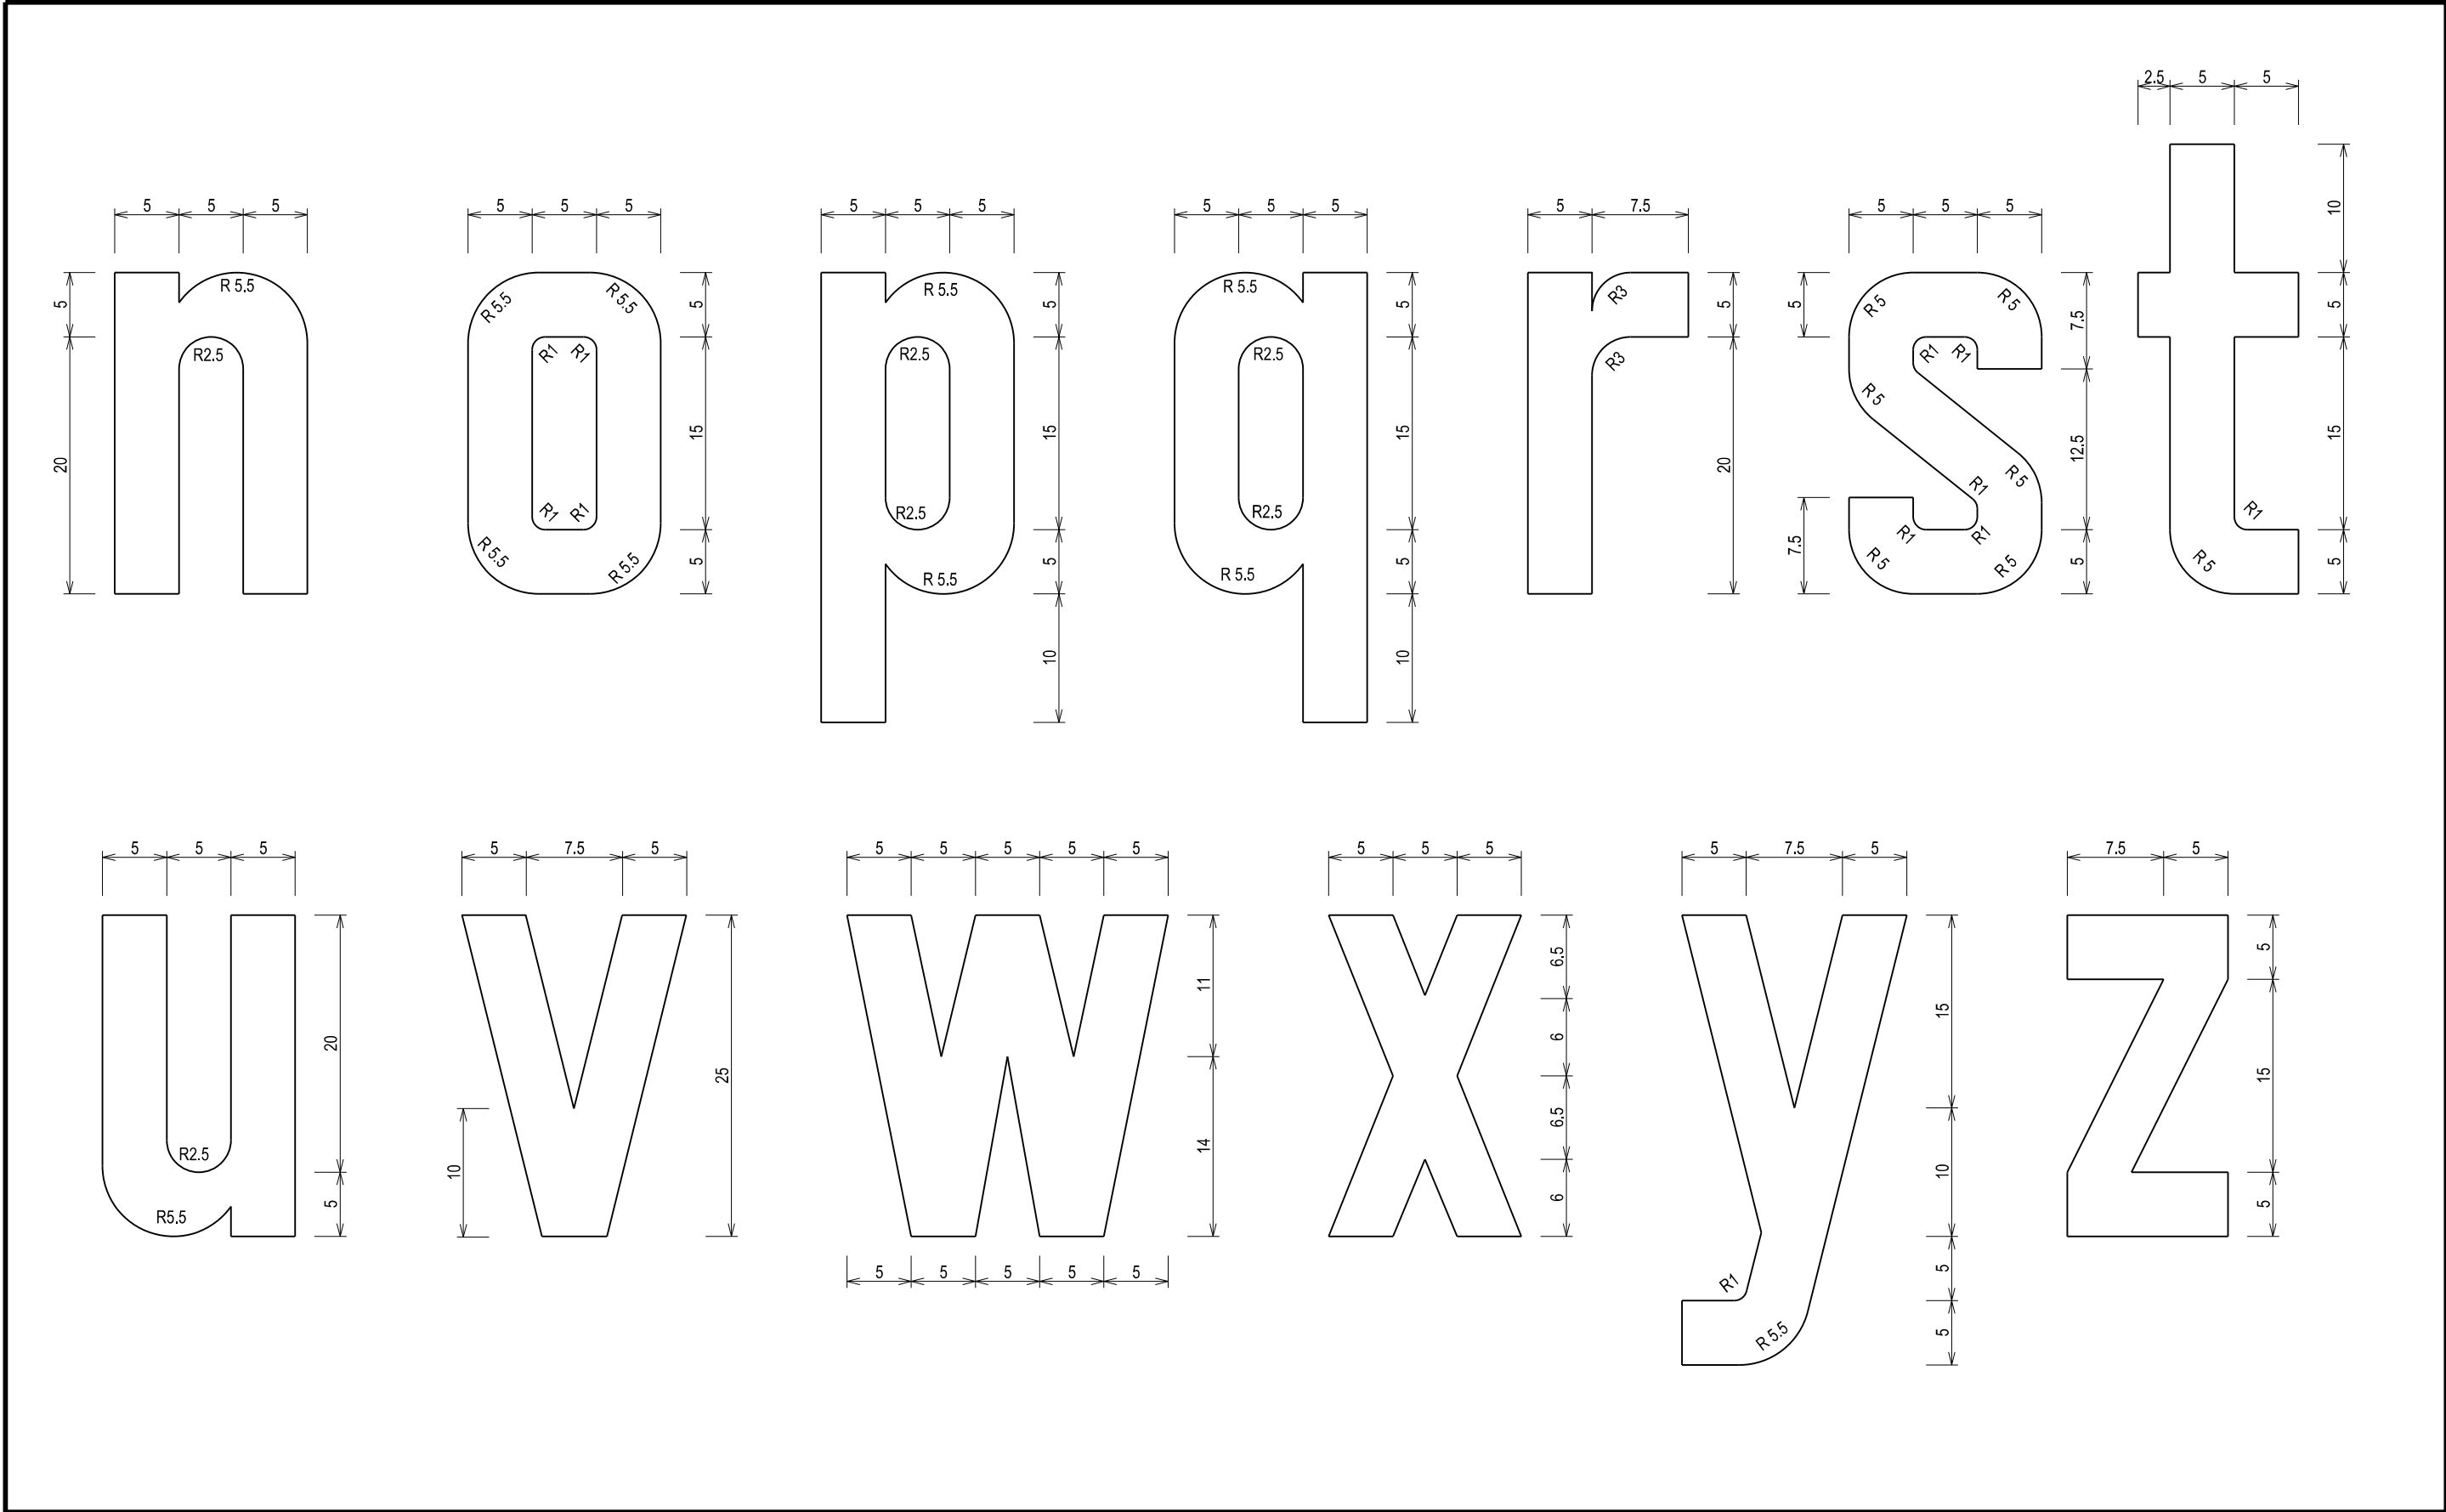


	</
--	--	----




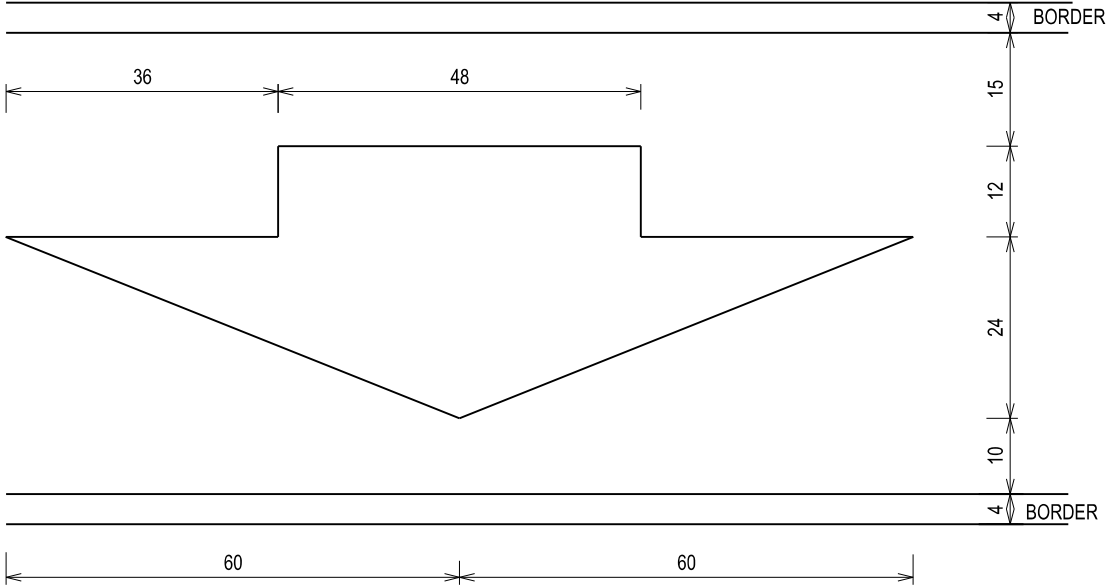

SCALE 1:1000

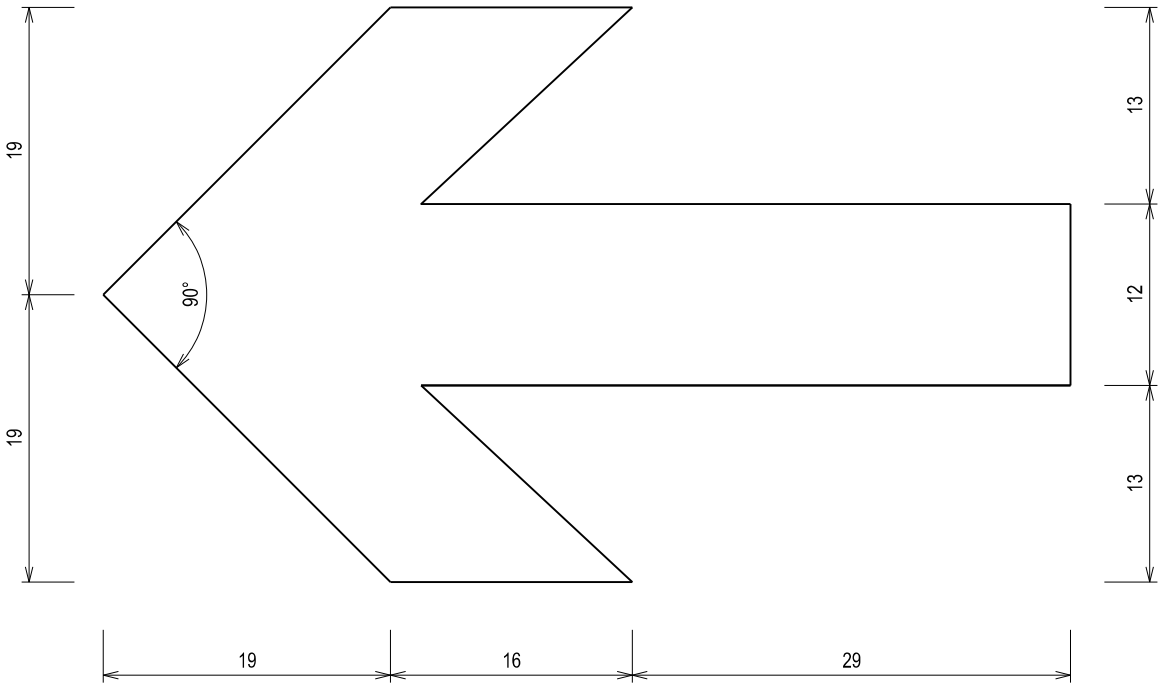

SCALE 1:500

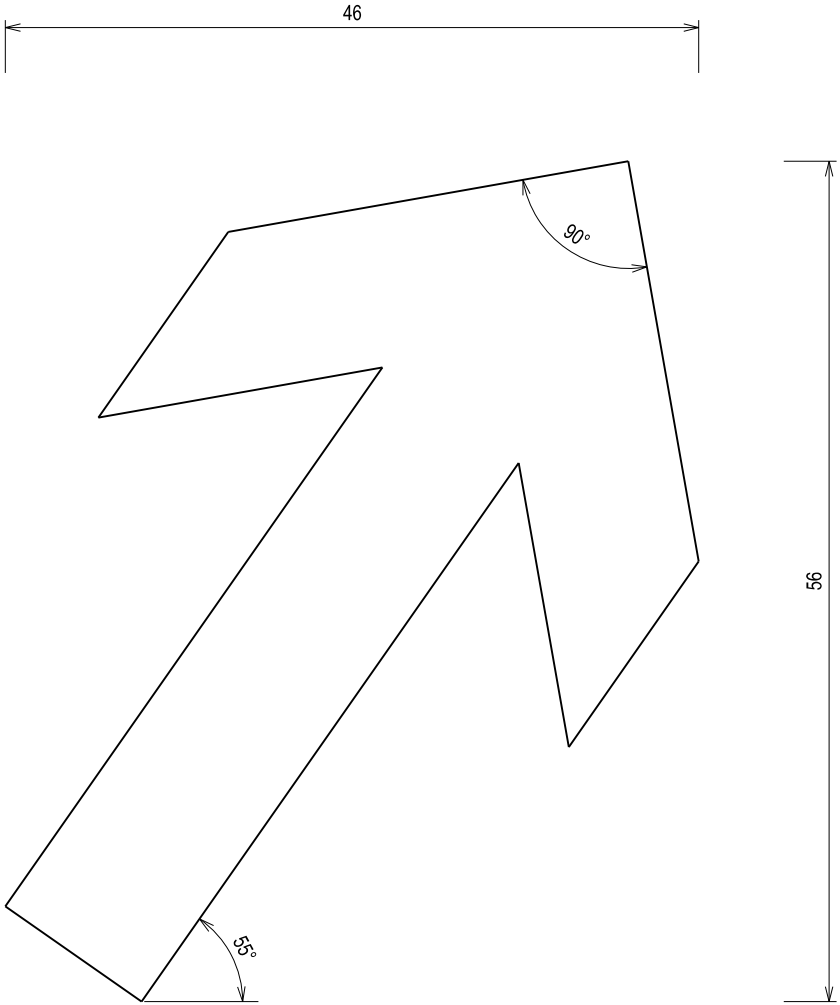

SCALE 1:500

NOTES:

1. For colour combinations, sizes / dimensions and standard spacing between 2 letters, refer to LTA/SDRE14/7/DIR7 & 8.

--	--	

TABLE 3:
RECOMMENDED SPACING BETWEEN INITIAL CAPITAL AND LOWER CASE LETTERS

INITIAL	WHEN COMBINED WITH LOWER-CASE LETTERS	LETTER SPACING *
ALL	) (CLOSE BRACKET)	2 7
A, C, E	v, w f, t, x, y ALL OTHERS	3 4 5
B, D, G, H, I J, M, N, O, Q, R, S, U	f, t, v, w, x, y ALL OTHERS	4 5
F, K, P, T, V W, X, Y, Z	v, w, x, y ALL OTHERS	3 4
L	f, t, v, w, x, y ALL OTHERS	3 4
' (APOSTROPHE)	ALL	5
, (COMMA)	ALL	10
/	ALL	20
((OPEN BRACKET)	ALL	7

1. *Factor 6 is used if the sign is mounted with one or more directional signs on the same frame, if on its own, factor 4 is recommended.
2. #Factor 12 is preferred if space on the gantry sign permits.
3. () Figures in bracket are the x-heights of the actual sizes of characters.

TABLE 4:
RECOMMENDED SPACING BETWEEN UPPER CASE LETTERS

LETTERS	WHEN COMBINED WITH LETTERS	LETTER SPACING *
ALL	) (CLOSE BRACKET)	7
A, L, V, Y	ALL	4
B, C, D, E, F, G, H, I, J, K, M, N, O, P, Q, R, S, T, U, W, X, Z	A, J, V, Y ALL OTHERS	4 5
' (APOSTROPHE)	ALL	5
, (COMMA)	ALL	10
/	ALL	20
(((OPEN BRACKET)	ALL	7

* For x-heights of 100mm, 150mm, 250mm and 300mm, the actual letter and numeral spacings will be multiplied by 4, 6, 10 & 12 respectively.

For x-heights of 100mm, 150mm, 250mm and 300mm, the actual letter and numeral spacings will be multiplied by 4, 6, 10 & 12 respectively.

[illegible]

TABLE 7:
COLOUR CODE

COLOUR CODE	LETTERING ARROW & BORDER	BACKGROUND	REMARKS
A	WHITE (Within Blue Box)	GREEN	EXPRESSWAY NAMES ON DIRECTIONAL SIGNS
B	WHITE	GREEN	(a) DIRECTIONAL SIGNS (b) STREET NAME SIGNS- STAND ALONE SIGNS
C	BLACK	WHITE	(a) FACILITY SIGNS (b) STREET NAME ON DIRECTIONAL SIGNS
D	WHITE	BLUE	INFORMATION SIGNS
E	WHITE	BROWN	TOURISTS

TABLE 8:
EXPRESSWAY LOGO

TABLE 11:
DIRECTIONAL SIGNS

TABLE 6:
RECOMMENDED SPACING

TABLE 9:
MULTIPLICATION FACTORS FOR EXPRESSWAY LOGO

TABLE 12:
OTHER SIGNS

TABLE 10:
SPACING BETWEEN NUMERAL AND ALPHABET IN 'EXIT NUMBER' SIGNS

STANDARD DETAIL

NOTES FOR
DIRECTIONAL SIGNS
(SHEET 2 OF 2)REV.
A

7-8