



CHAPTER 9

TRAFFIC MANAGEMENT MEASURES


DRAWING TITLE	DRAWING NO.	REVISION
SPEED REGULATING STRIPS	LTA/SDRE14/9/TMM1	A
CHANNELISING ISLANDS & U-TURN	LTA/SDRE14/9/TMM2	B
PHYSICAL NOSING WITH DRAINAGE - FOR EXPRESSWAY & NON-EXPRESSWAY	LTA/SDRE14/9/TMM3	A
PAVEMENT MARKINGS FOR PEDESTRIAN CROSSINGS	LTA/SDRE14/9/TMM4	D
RAISED ZEBRA CROSSING	LTA/SDRE14/9/TMM5	C
ROAD HUMP	LTA/SDRE14/9/TMM6	A
BUS FRIENDLY ROAD HUMP	LTA/SDRE14/9/TMM7	-
BUS FRIENDLY ROAD HUMP CUM RAISED ZEBRA CROSSING	LTA/SDRE14/9/TMM8	C
WAITING AREA FOR MOTORCYCLISTS	LTA/SDRE14/9/TMM9	C

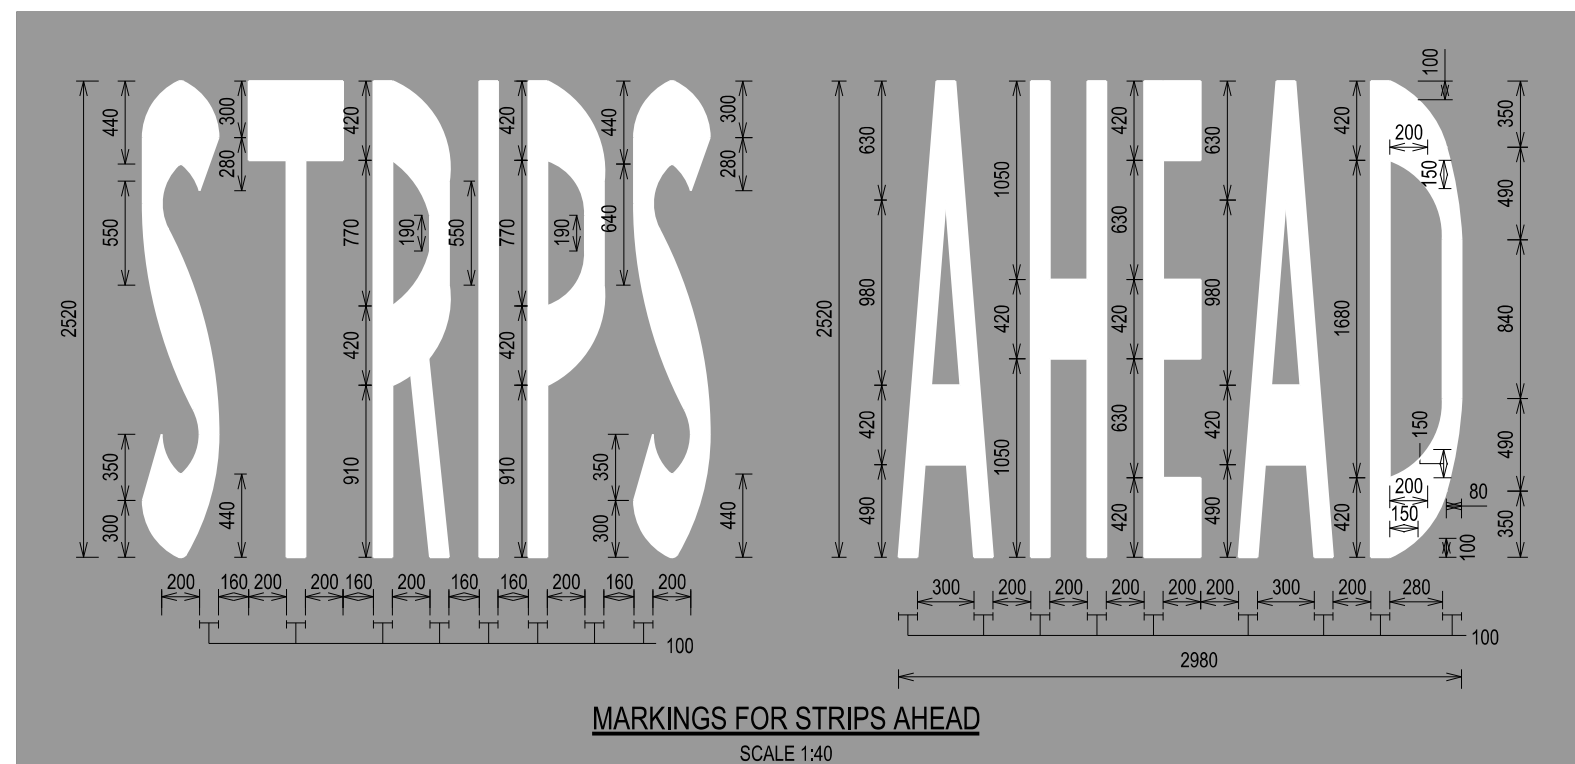


A	SEP 2017
REV.	DATE

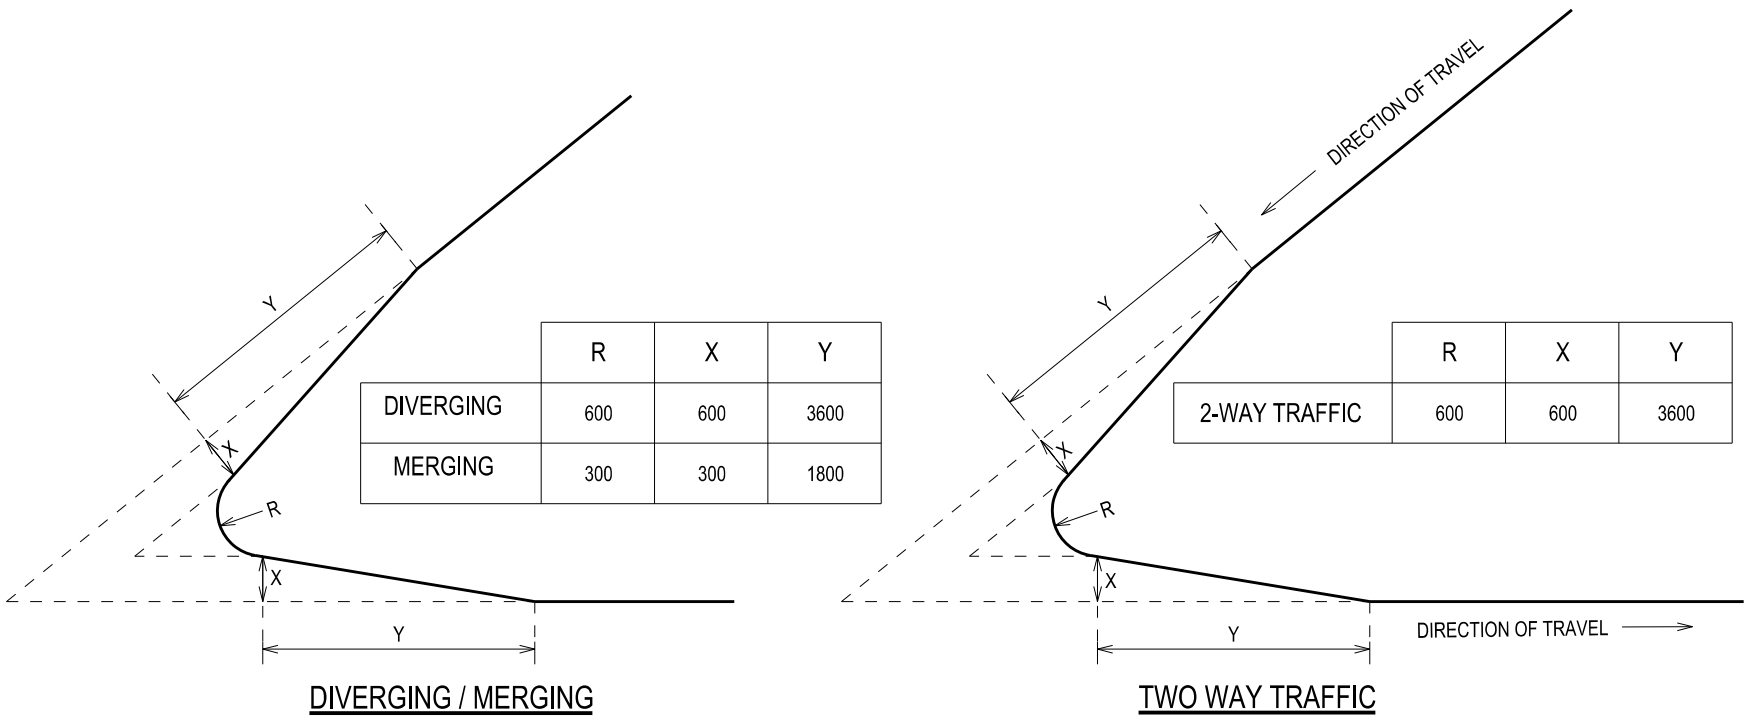

NOSING AT CHANNELISING ISLAND
SCALE 1:100

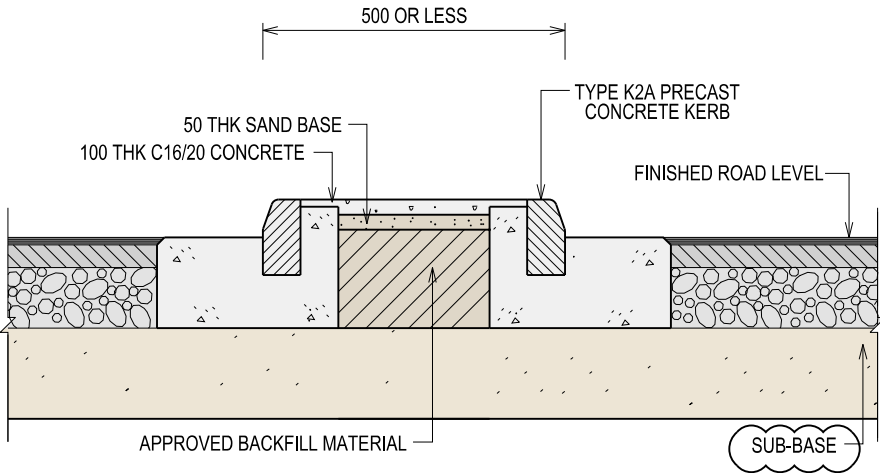


DETAILS OF PAVED SURFACE
SCALE 1:25

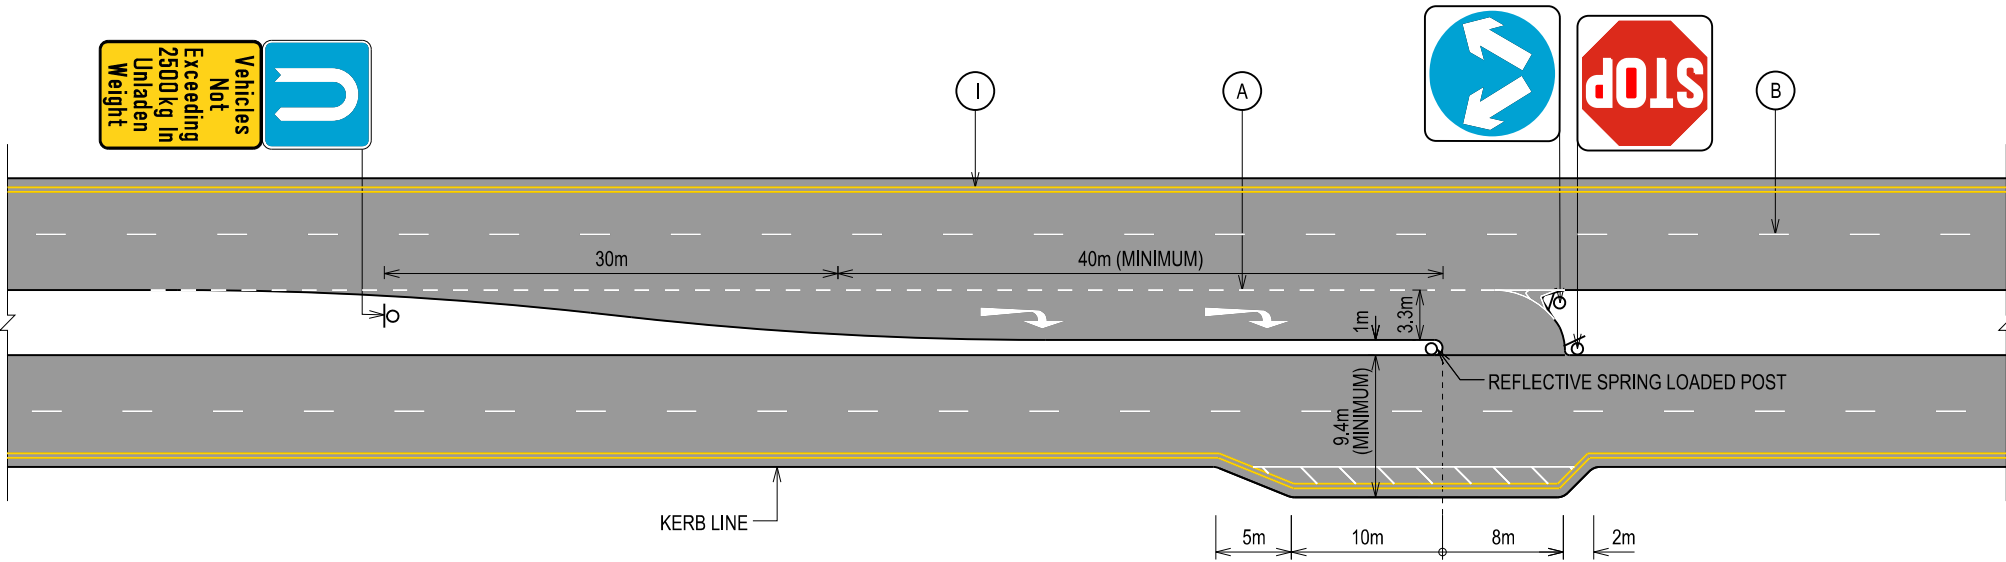





DETAIL OF U-TURN
LESS THAN 2500kg (2 LANES CARRIAGEWAY)
SCALE 1:500

NOTES:
1. Centre median of width less than 500mm shall be paved.

B A REV.		SEP 2017 OCT 2015 DATE	STANDARD DETAIL CHANNELISING ISLANDS & U-TURN	Land Transport Authority		
				DRAWING NO. LTA/SDRE14/9/TMM2		
				DATE OF ISSUE	SCALE	SHEET NO.
				1st APR 2014	AS SHOWN	1 OF 1
				REV. B		

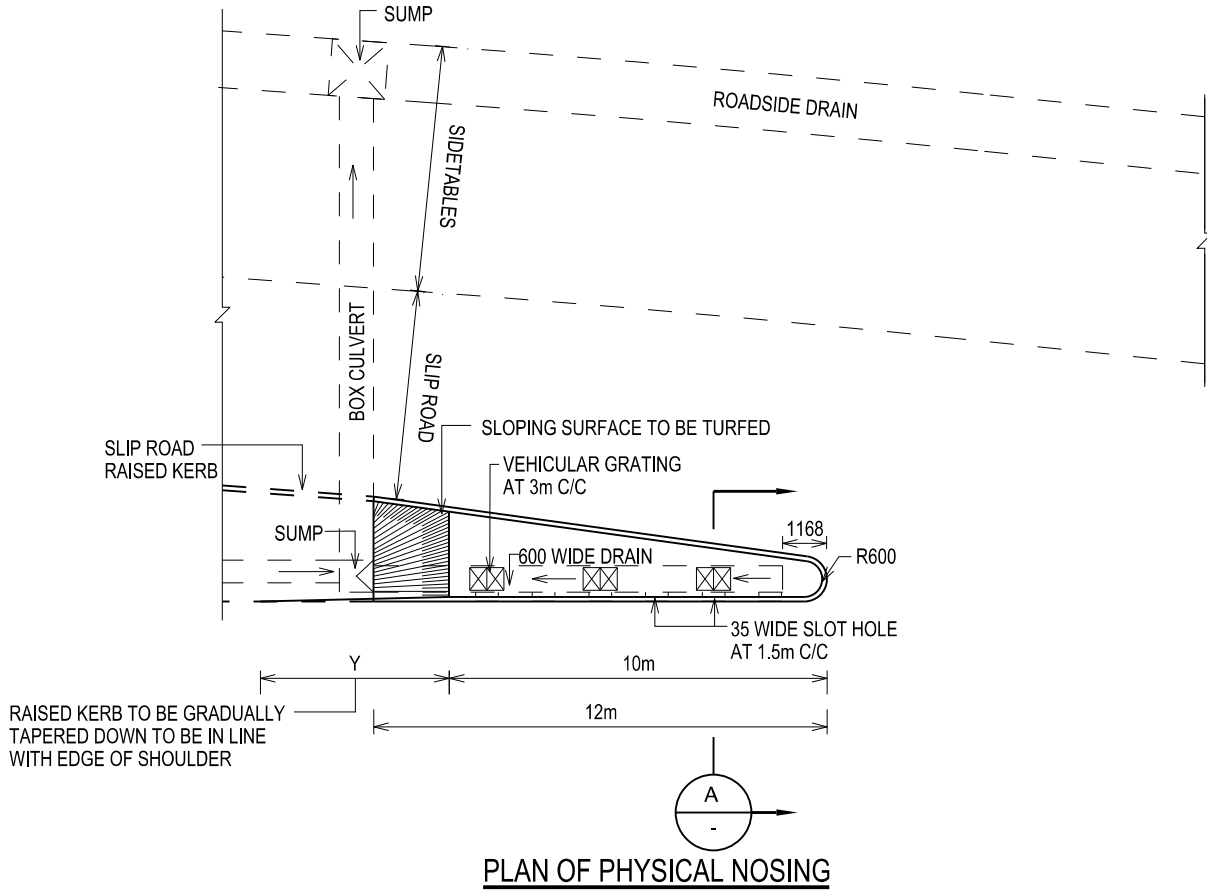

TYPE OF ROAD	TYPE OF KERB	X (mm)	Y (m)
EXPRESSWAY	MOUNTABLE KERB	100	2
NON-EXPRESSWAY	K2A KERB	125	-

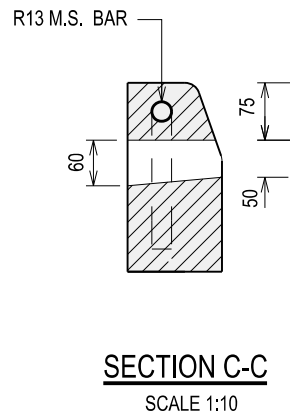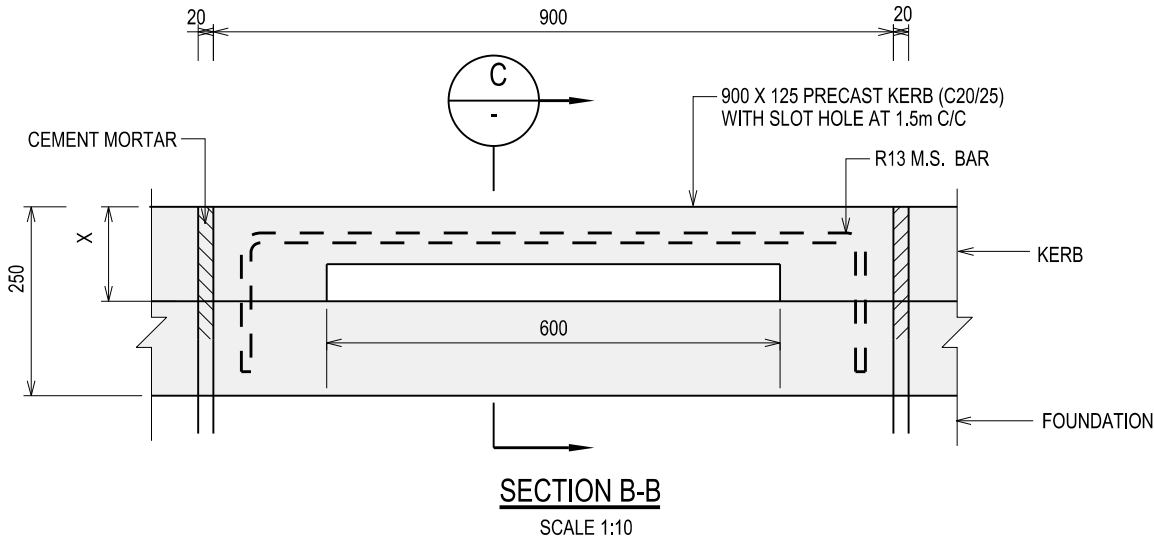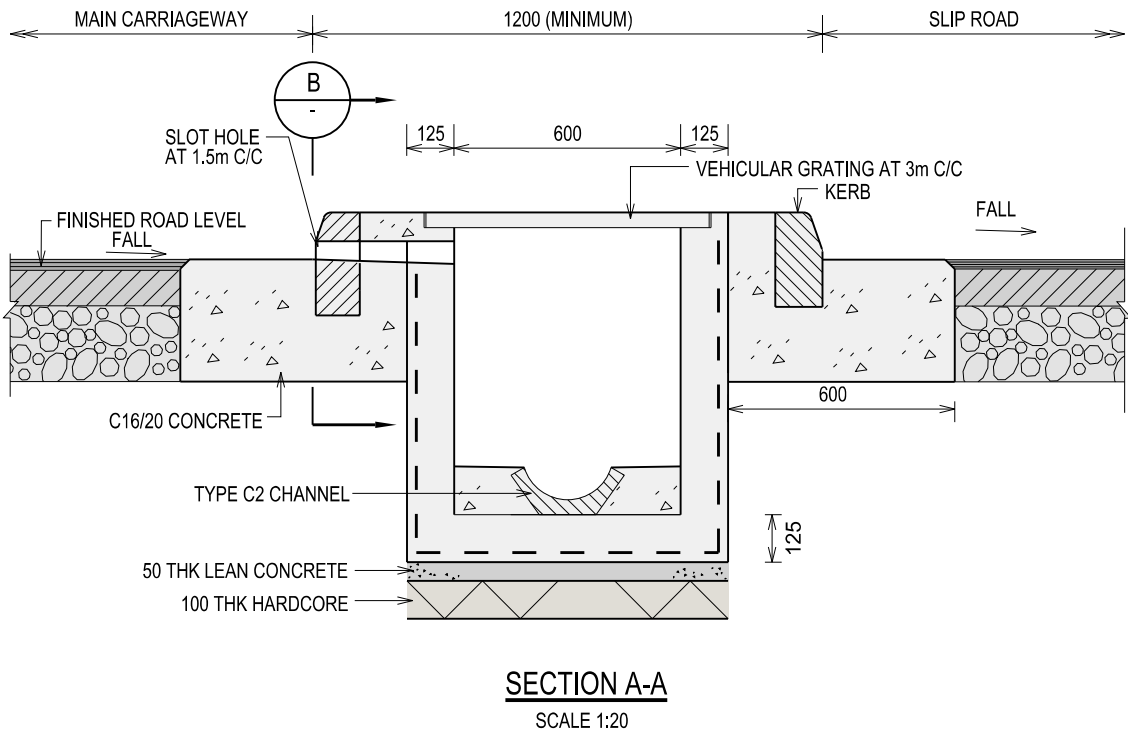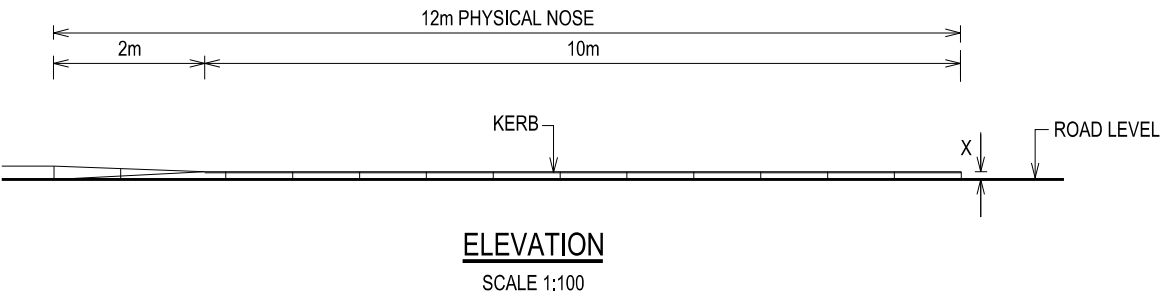


NOTES:
1. This detail is also applicable for the off-ramp nosing where crash cushion is not required.
(Refer to Drawing No. LTA/SDRE14/6/VIG3A, if a crash cushion is required)

A OCT 2015 REV. DATE	STANDARD DETAIL	Land Transport Authority		
		DRAWING NO. LTA/SDRE14/9/TMM3		
		REV. A		
		DATE OF ISSUE 1st APR 2014	SCALE AS SHOWN	SHEET NO. 1 OF 1

LEGEND


-  PRIMARY SIGNAL
-  SECONDARY SIGNAL
-  PEDESTRIAN SIGNAL
-  REFER TO LANE MARKINGS
-  FLASHING BEACON WITH 'PEDESTRIAN CROSSING' SIGN
-  RAISED REFLECTIVE PAVEMENT MARKERS (AMBER)
-  HOMOGENEOUS TACTILE TILES
-  'PEDESTRIAN CROSSING PROHIBITION' SIGN
TO BE PLACED PERPENDICULAR TO
THE 'ARROW' SIGN
-  'ARROW' SIGN TO BE PLACED PARALLEL TO
SIDE OF ROAD

ALL SIGNS TO BE CLAMPED ONTO THE NEAREST
EXISTING LAMPPOSTS WHEREVER POSSIBLE AND
SUBJECT TO SO'S APPROVAL

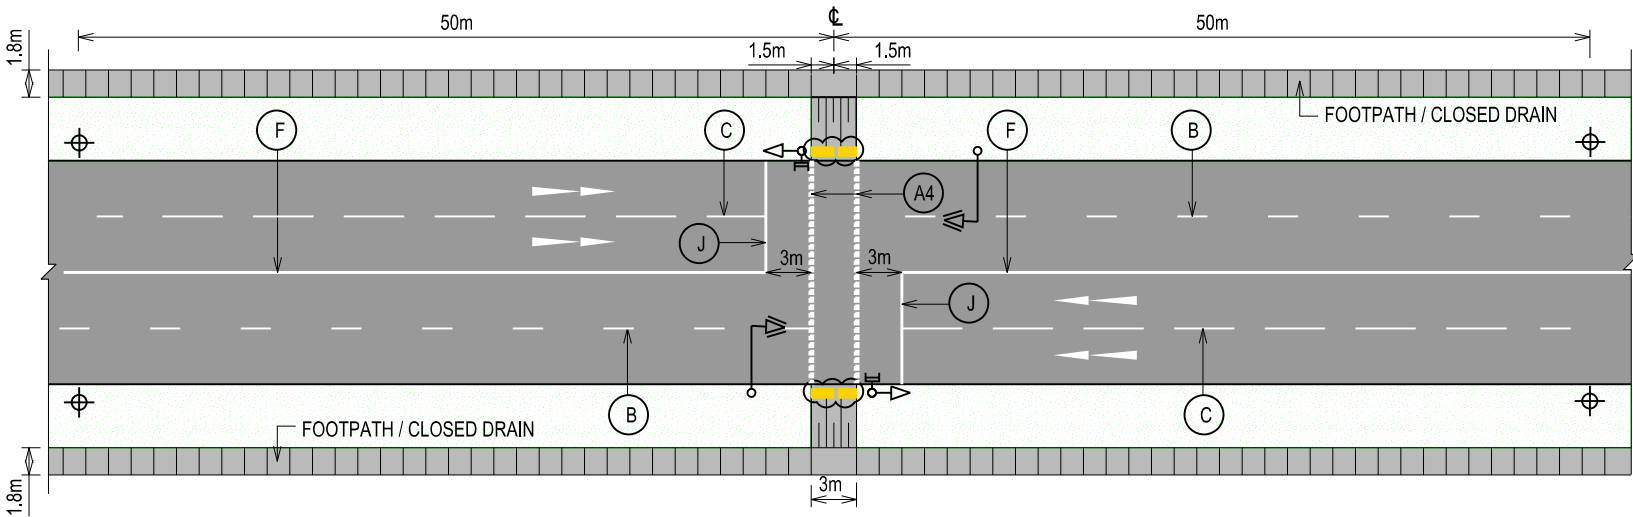

SIGNALISED PEDESTRIAN CROSSING


SCALE 1:500

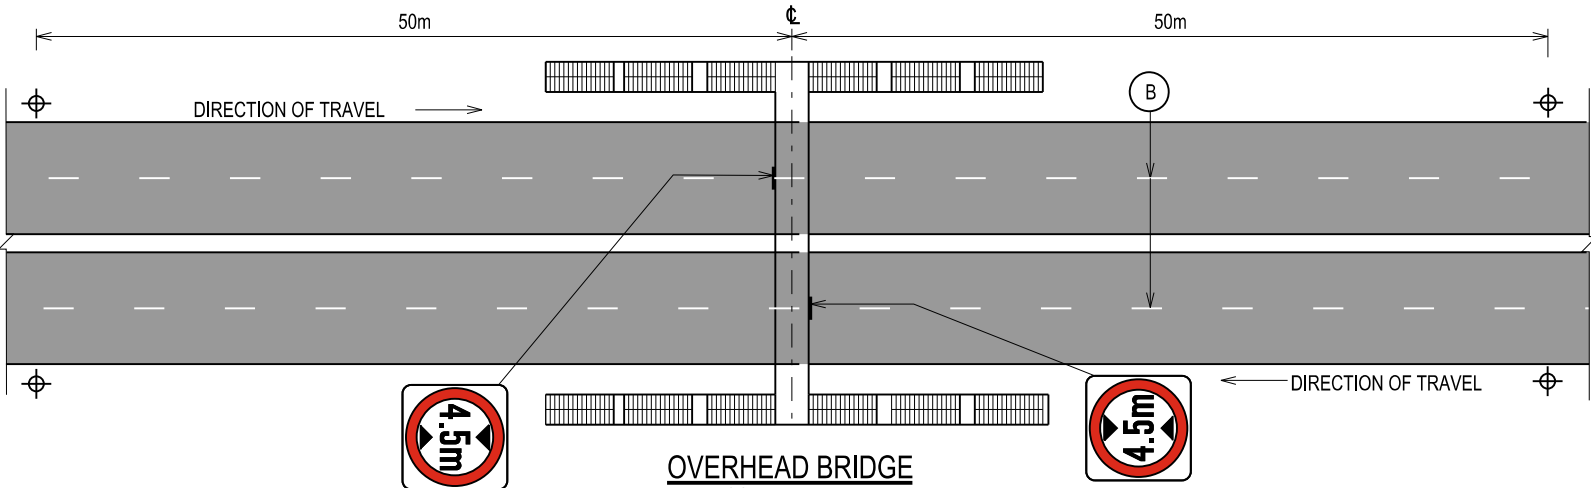

OVERHEAD BRIDGE

SCALE 1:500

50m

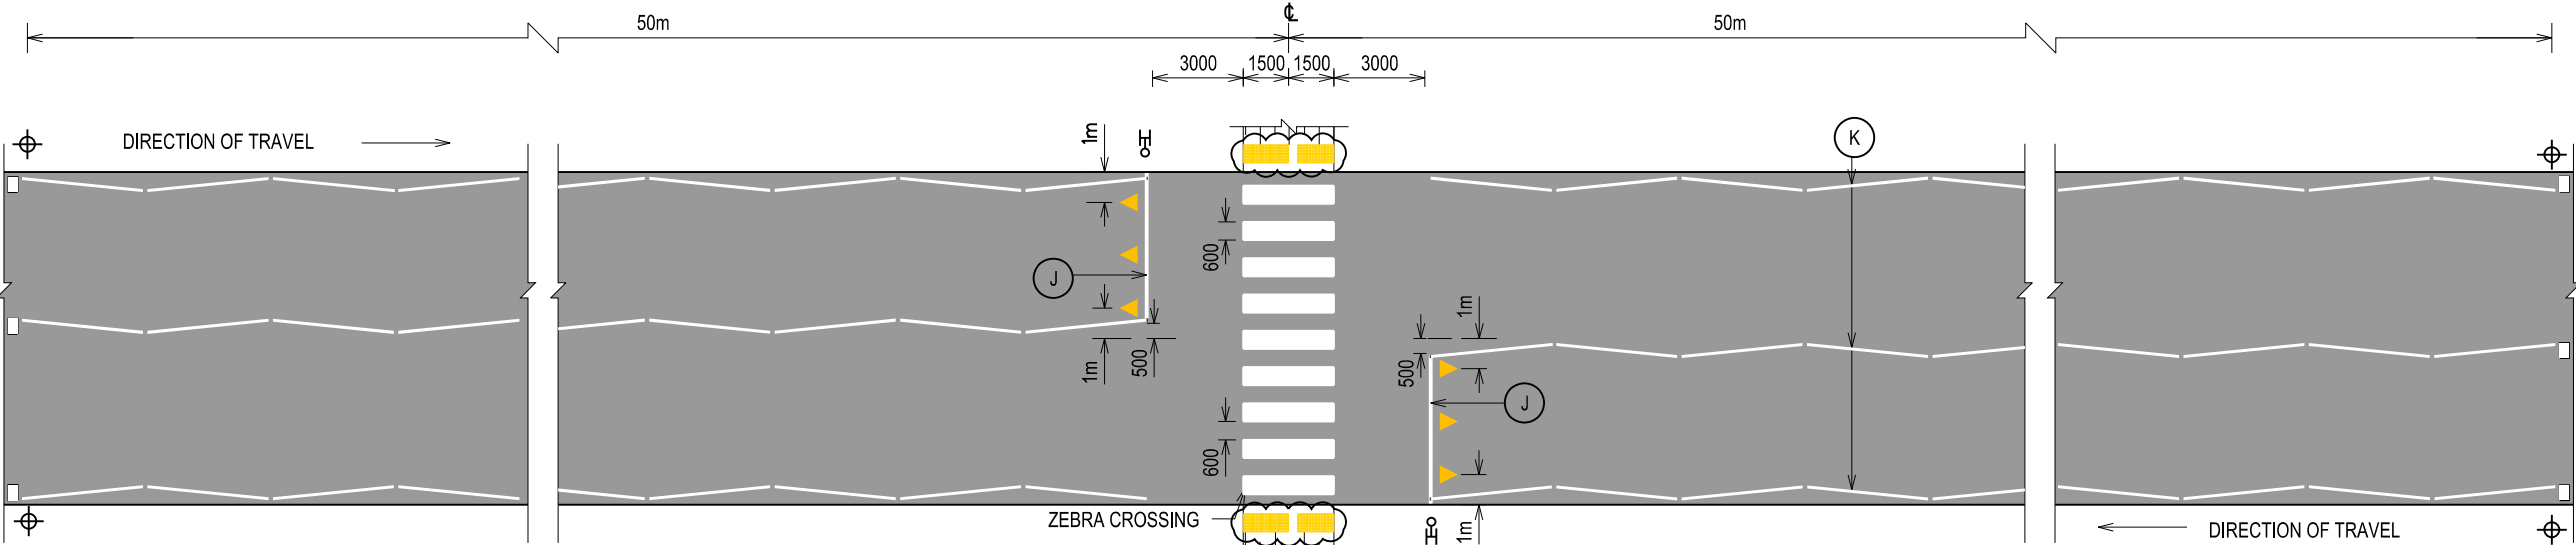

ZEBRA CROSSING AND ZIG ZAG MARKING

SCALE 1:250





NOTES:

1. Pedestrian crossing with green and red man aspect is to be painted white.
2. Pedestrian crossing without green and red man aspect is to be painted yellow.
3. The zig zag markings must not overlap existing double yellow lines.
4. The zig zag markings shall be 350mm away from the road kerb.
5. The raised reflective pavement markers shall comply with the requirements laid down in BS 8442:2006, BS EN 12899-1:2007, BS EN 1643-1:2014.
6. The 'Pedestrian Crossing' sign shall face the oncoming traffic and erect away from the road kerb.

7. The 'Pedestrian Crossing' sign is to be erected on existing lampost / traffic light pole / any sign pole that is located less than 1m away from the flashing beacon pole.
8. No additional loading is to be added onto the flashing beacon pole other than 'Pedestrian Crossing' signs.
9. 'Pedestrian Prohibition Crossing' signs is not applicable for expressway.


STANDARD		DETAIL	
D C B A REV. DATE		PAVEMENT MARKINGS FOR PEDESTRIAN CROSSINGS	
		Land Transport Authority	
		DRAWING NO. LTA/SDRE14/9/TMM4	
		REV. D	
		DATE OF ISSUE 1st APR 2014	
		SCALE AS SHOWN	
		SHEET NO. 1 OF 1	



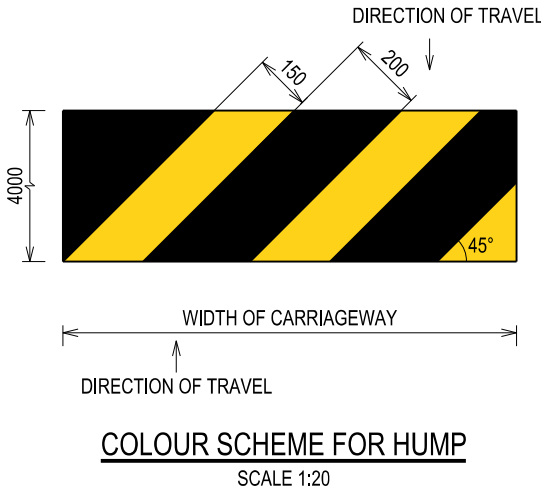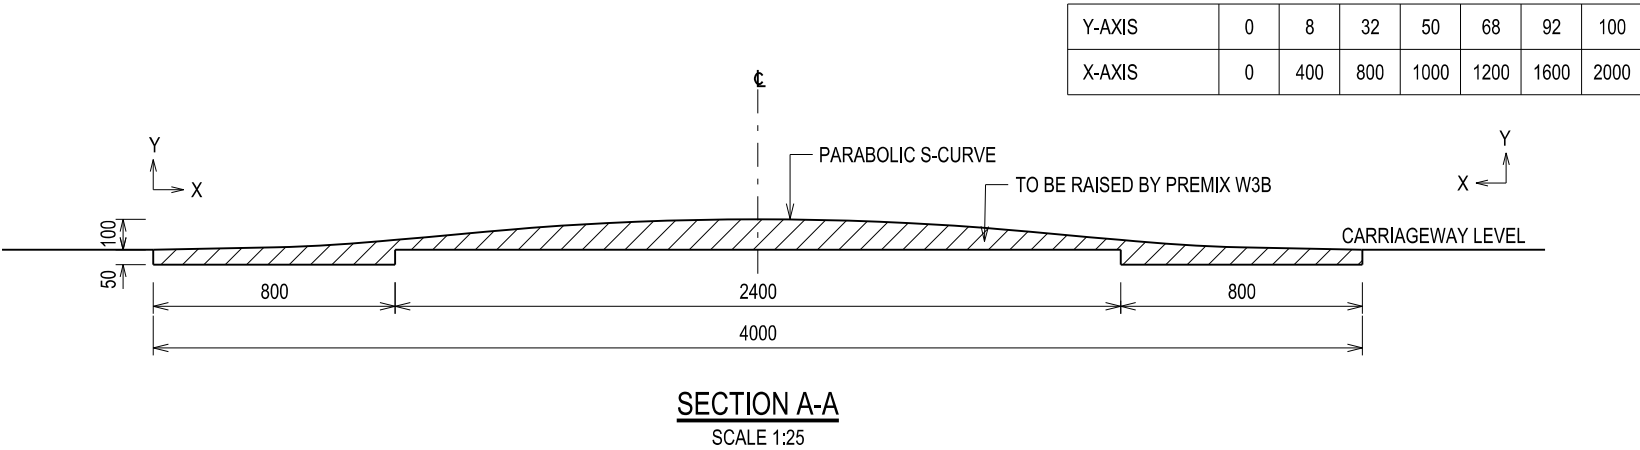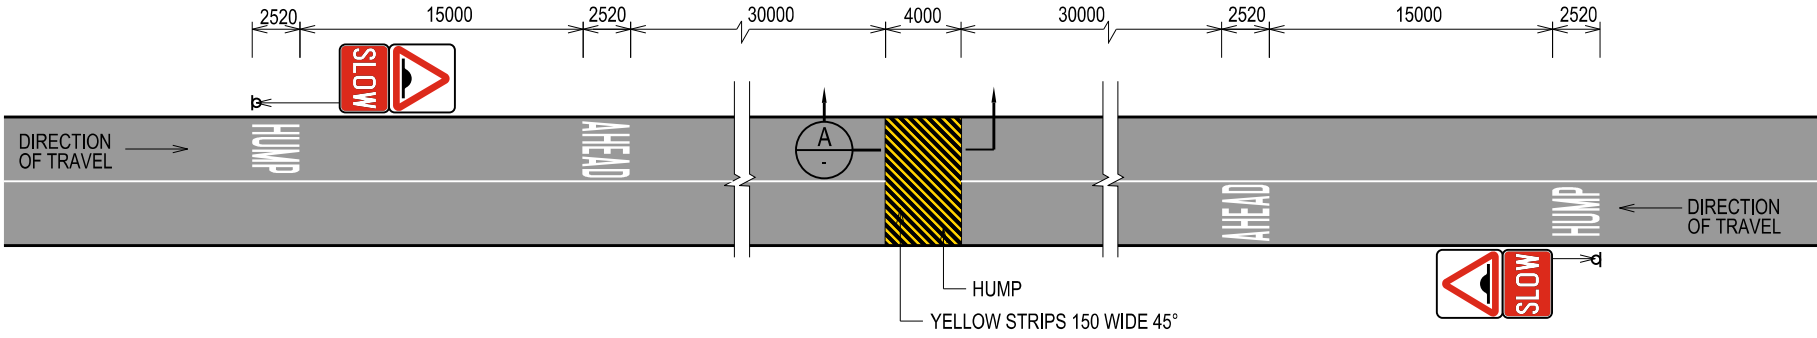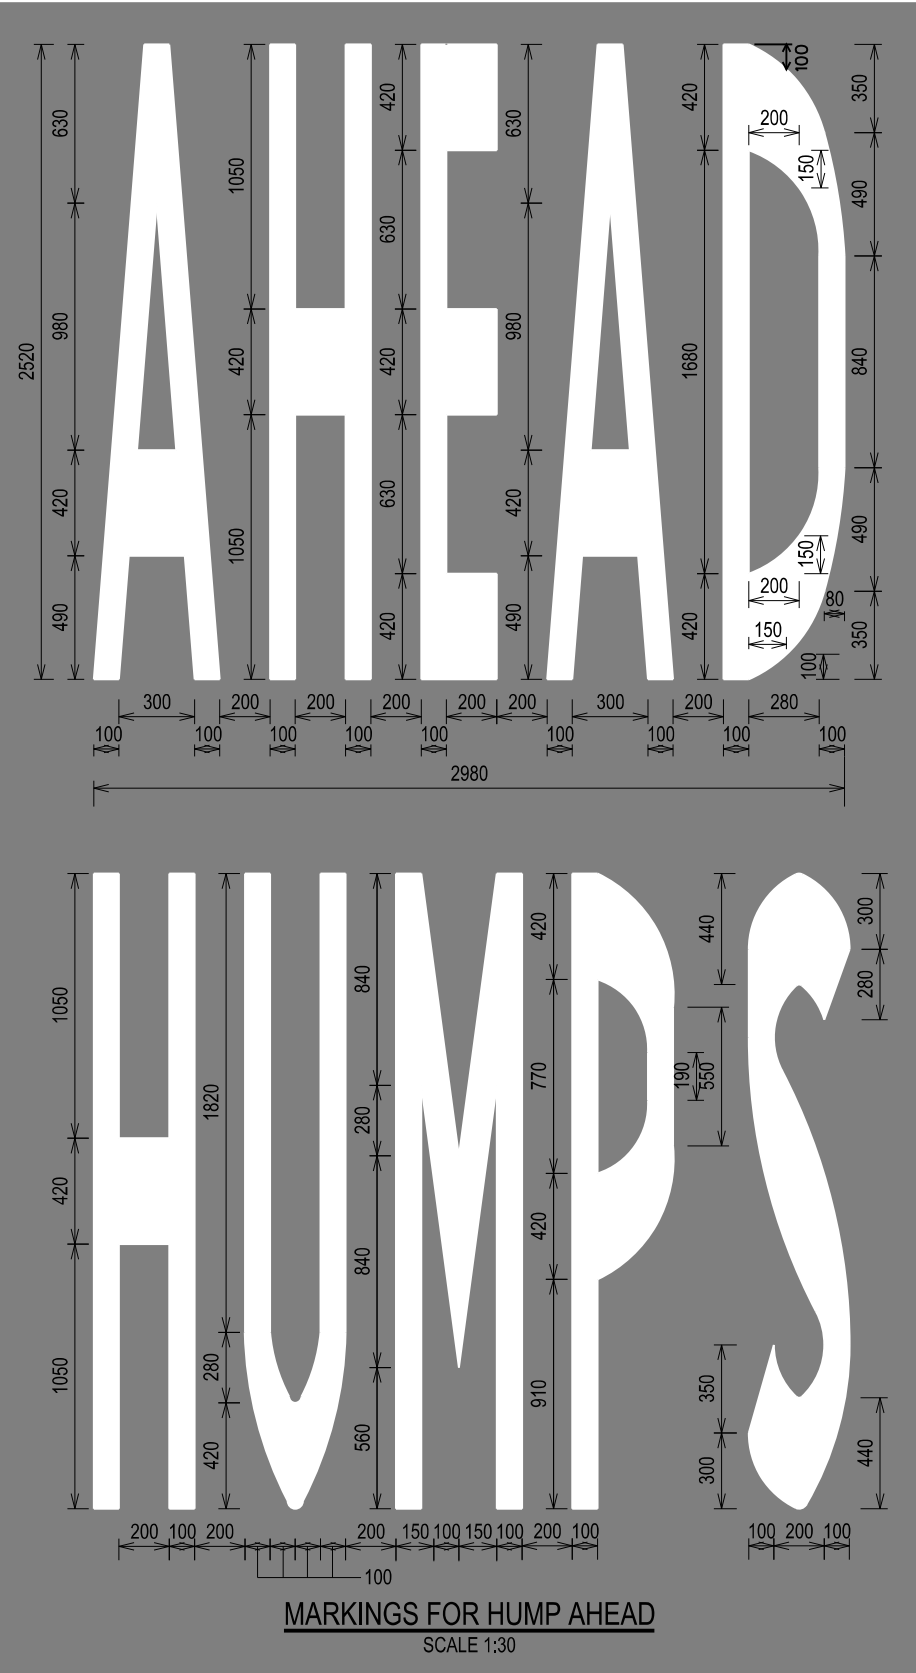

NOTES:
1. Thickness of thermoplastic paint for hump ahead marking is 3mm.


			STANDARD DETAIL			
			ROAD HUMP		DRAWING NO.	REV.
					LTA/SDRE14/9/TMM6	A
A	SEP 2017				DATE OF ISSUE	SHEET NO.
REV.	DATE				1st APR 2014	1 OF 1
					SCALE	
					AS SHOWN	

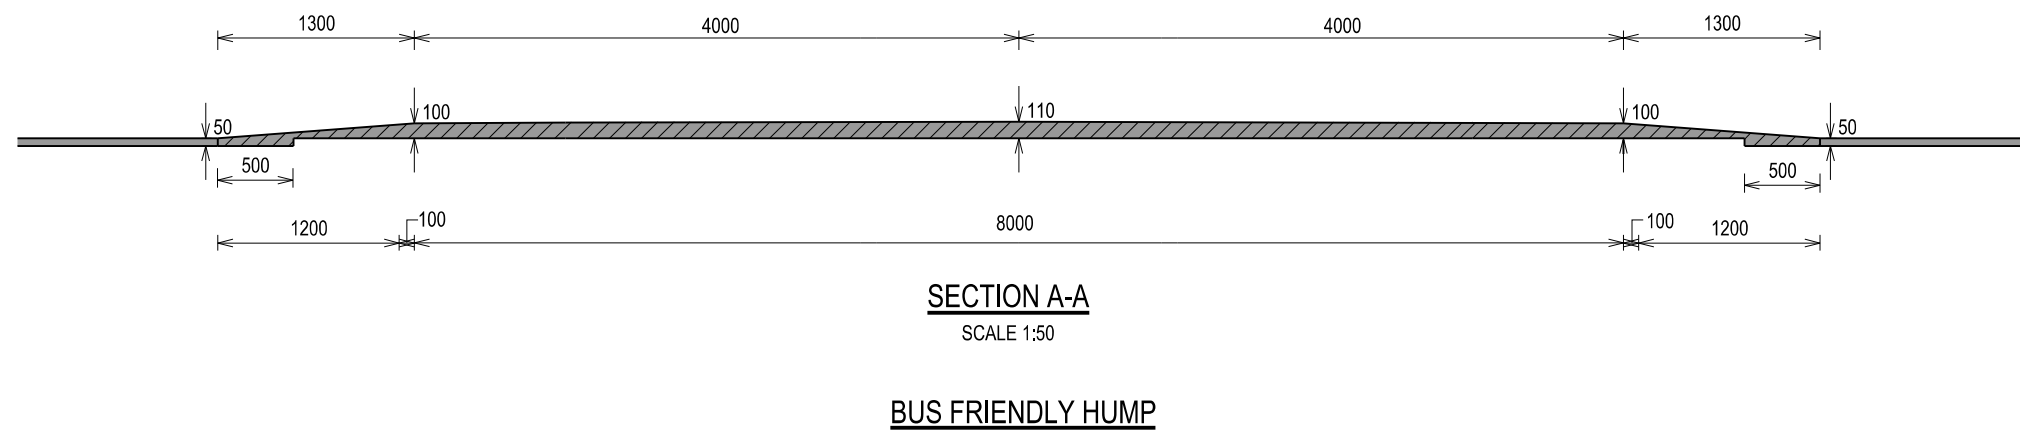[illegible]


LEGEND

-  RAISED REFLECTIVE PAVEMENT MARKERS (AMBER)
-  REFER TO LANE MARKINGS
-  FLASHING BEACON WITH 'PEDESTRIAN CROSSING' SIGNS
-  HOMOGENEOUS TACTILE TILES

-  'PEDESTRIAN CROSSING PROHIBITION' SIGN
TO BE PLACED PERPENDICULAR TO
THE 'ARROW' SIGN
-  'ARROW' SIGN TO BE PLACED PARALLEL TO
SIDE OF ROAD
- ALL SIGNS TO BE CLAMPED ONTO THE NEAREST
EXISTING LAMPPOSTS WHEREVER POSSIBLE AND
SUBJECT TO SO'S APPROVAL

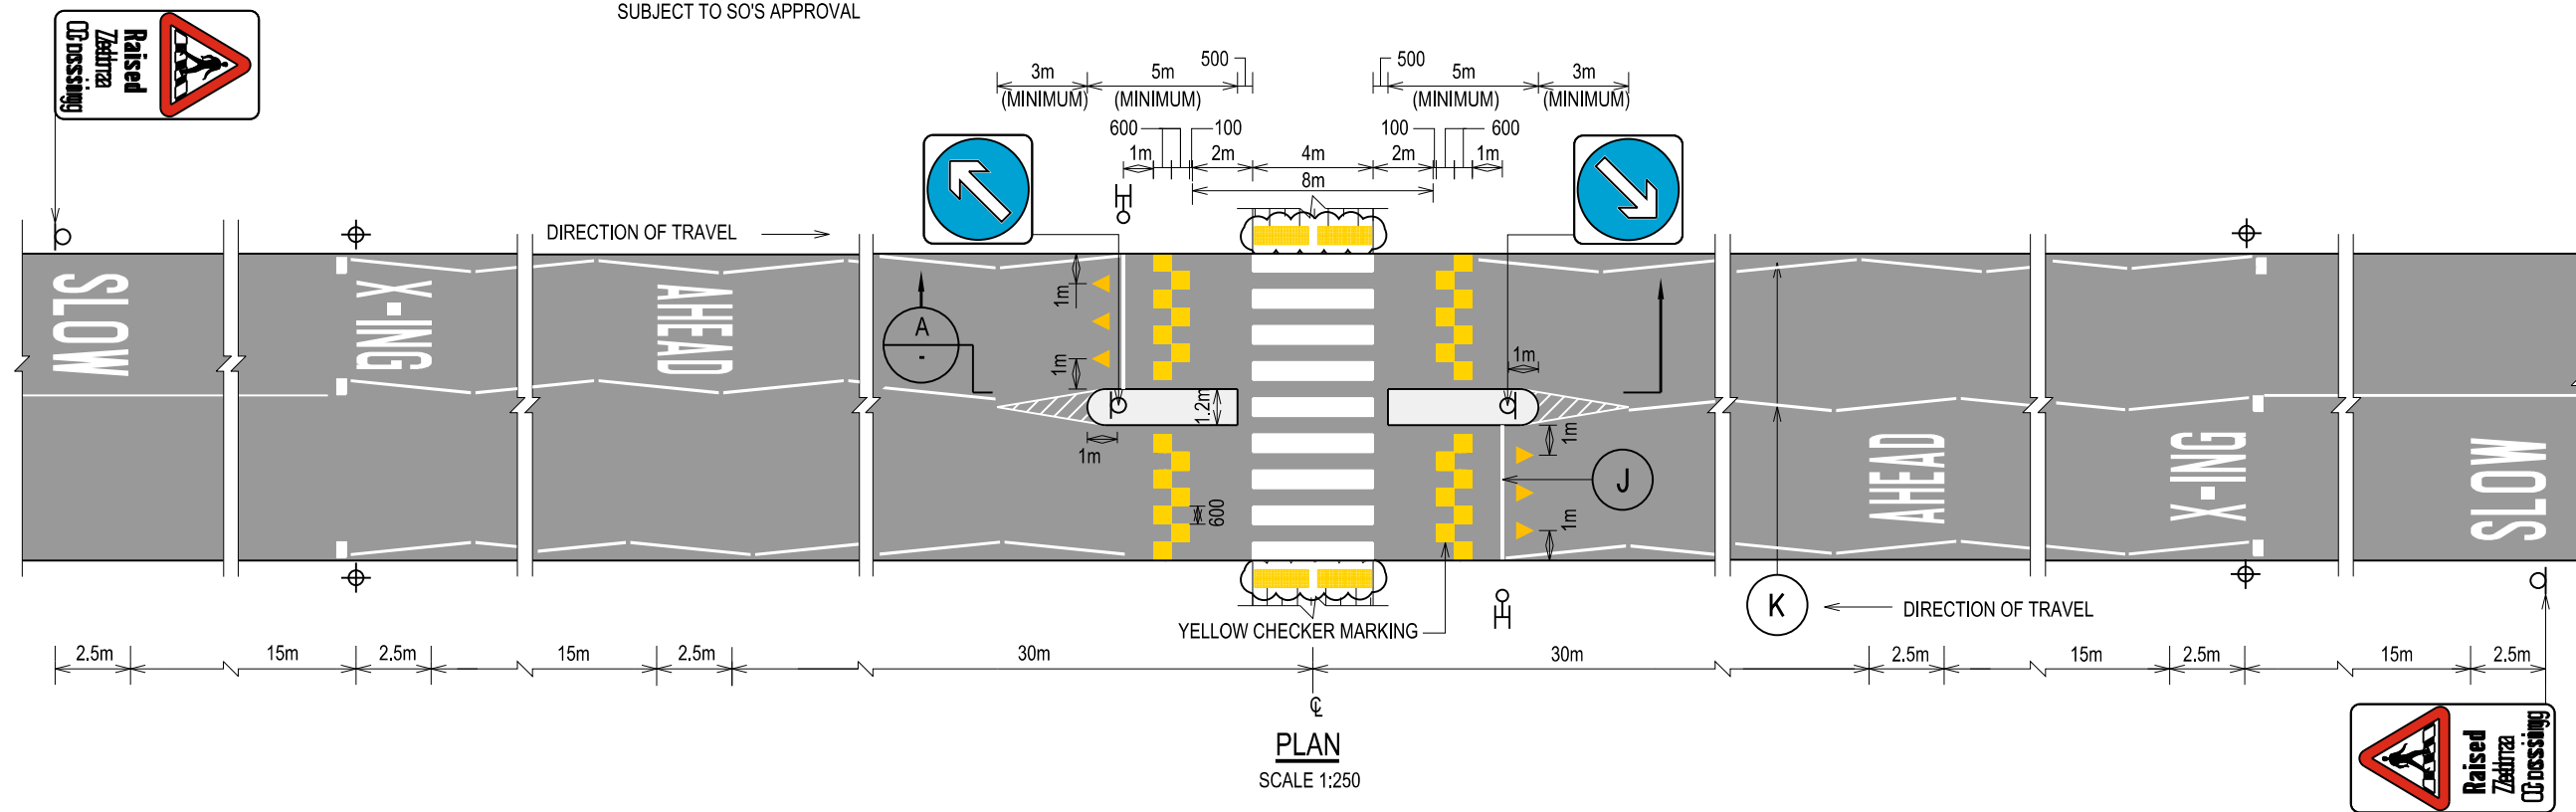

PLAN
SCALE 1:250

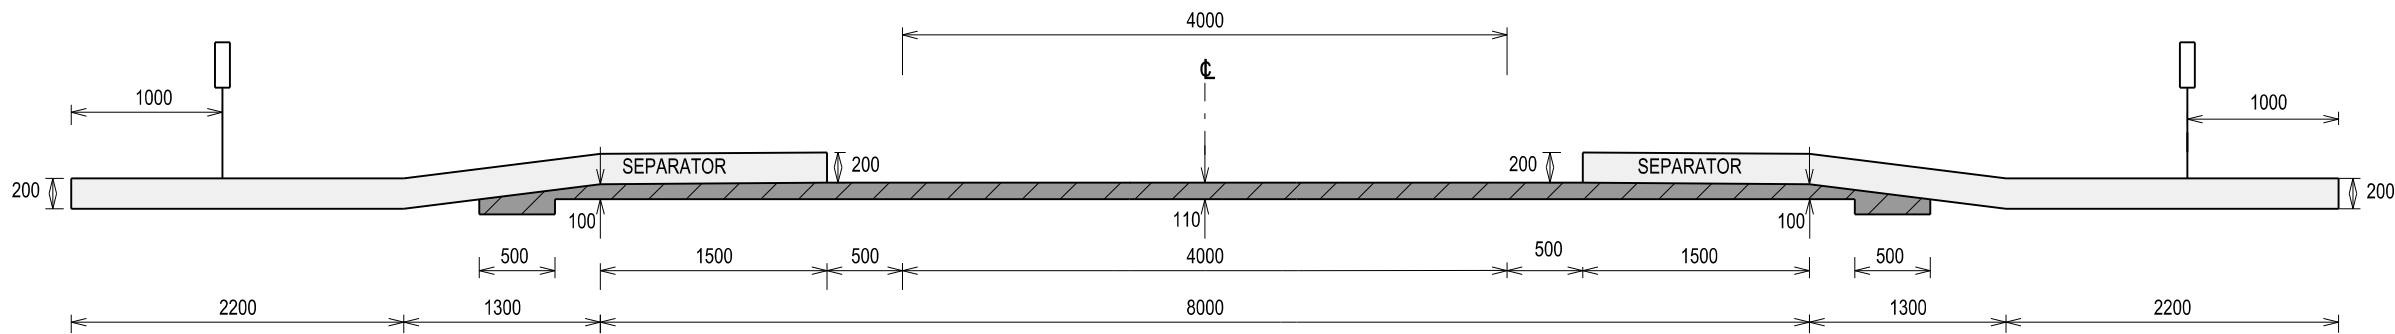

SECTION A-A
SCALE 1:50

BUS FRIENDLY HUMP CUM RAISED ZEBRA CROSSING

NOTES:


1. Footpath joining pedestrian crossings shall be flushed with zebra crossing.
2. Center refuge island shall terminate near a lamp pole.
3. Floodlight to be provided if necessary.

STANDARD DETAIL


BUS FRIENDLY HUMP
CUM RAISED ZEBRA
CROSSING




DRAWING NO.		REV.
LTA/SDRE14/9/TMM8		C
DATE OF ISSUE	SCALE	SHEET NO.
1st APR 2014	AS SHOWN	1 OF 1

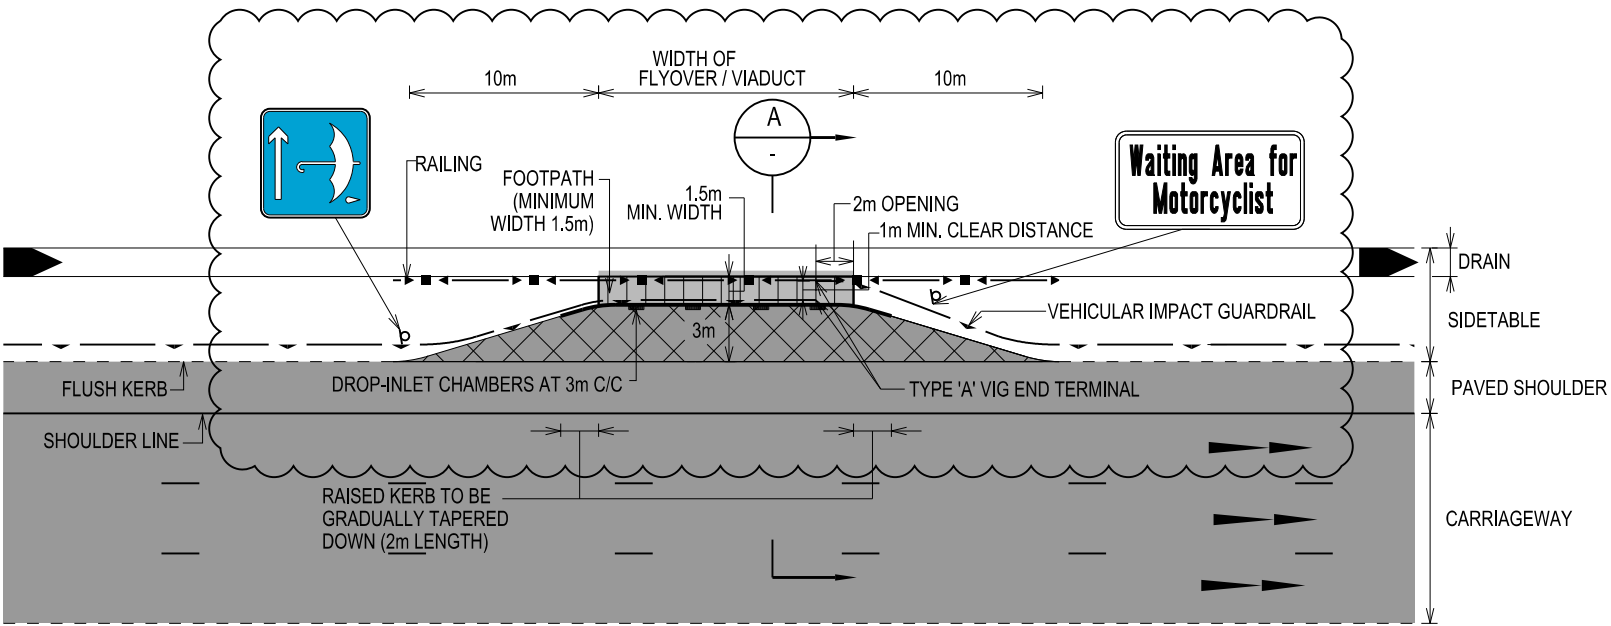


PLAN
SCALE 1:400

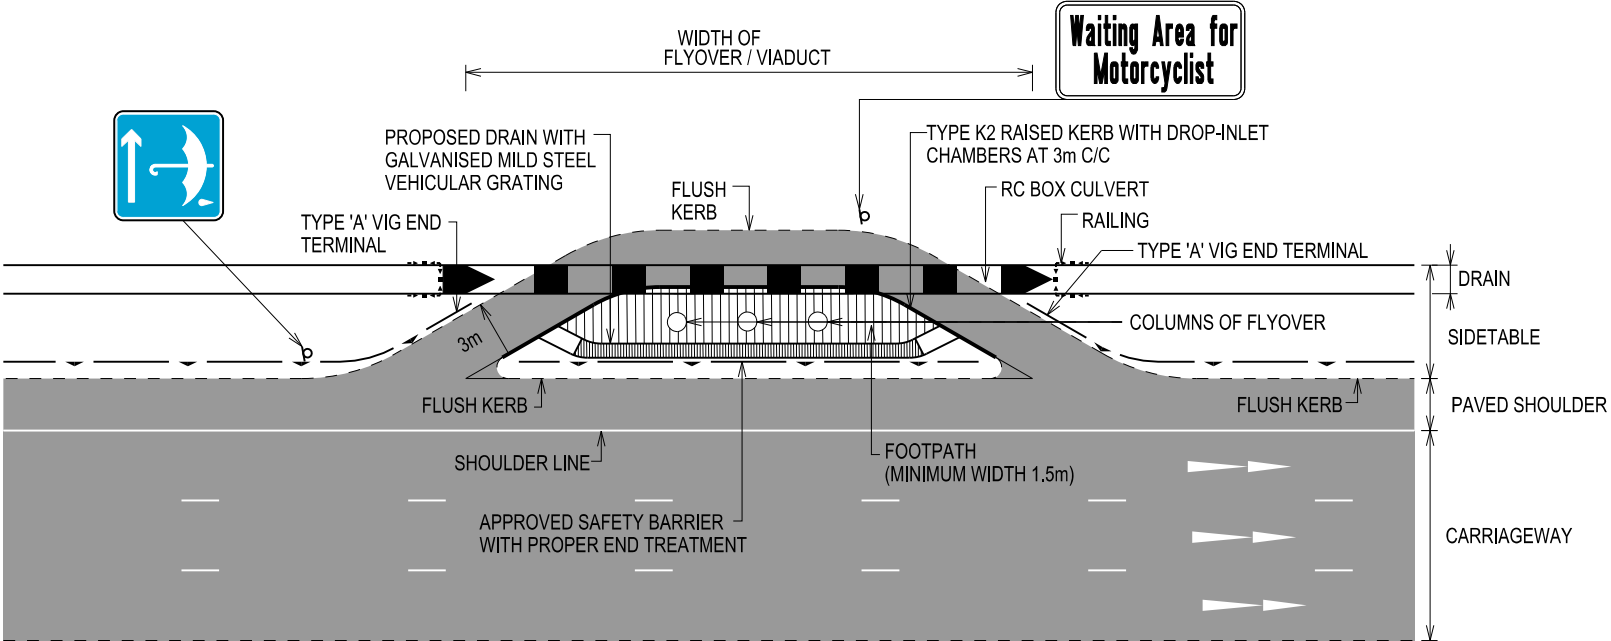

PLAN
SCALE 1:400

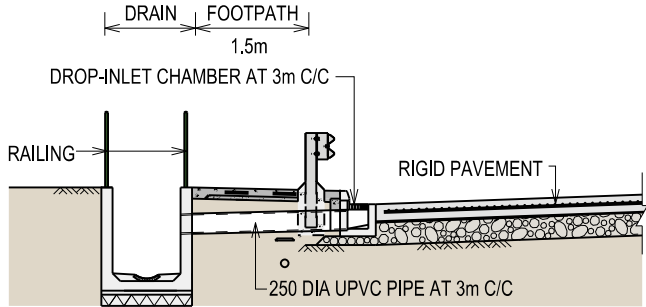


SECTION A-A
SCALE 1:100

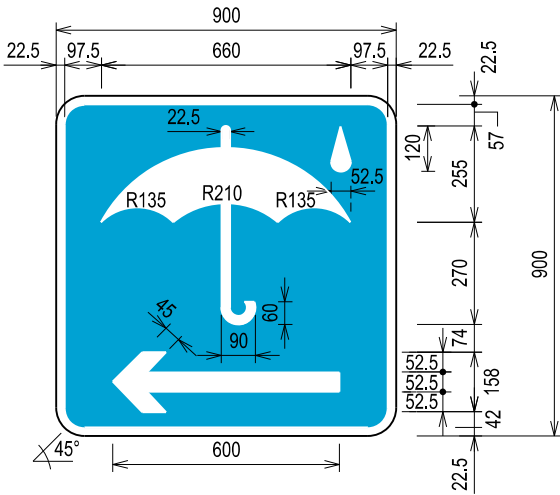

RAIN SHELTER SIGN


SCALE 1:20

SIZE : 900mm X 900mm
COLOUR : BLUE BACKGROUND, WHITE LOGO,
ARROW AND BORDER

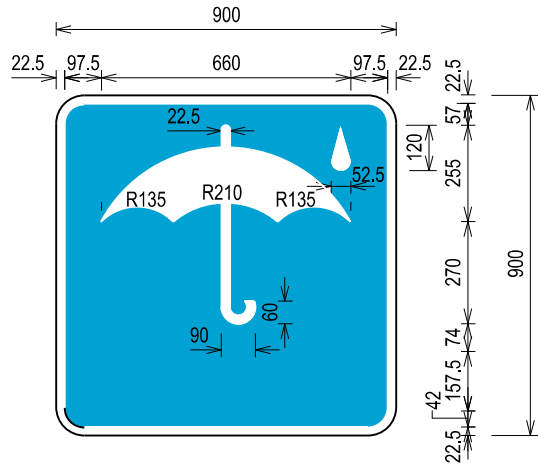

SCALE 1:20

SIZE : 900mm X 900mm
COLOUR : BLUE BACKGROUND, WHITE LOGO
AND BORDER

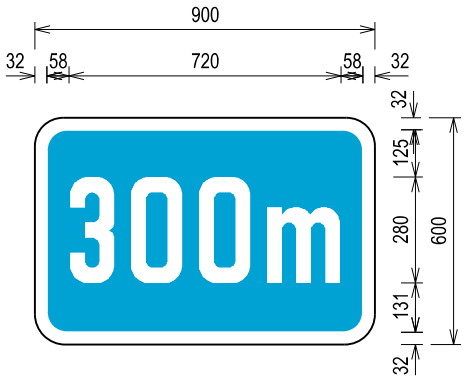

ADVANCED RAIN SHELTER SIGN

SCALE 1:20

SIZE : 900mm X 600mm
COLOUR : BLUE BACKGROUND, WHITE LOGO
AND BORDER

--	--	