


CHAPTER 21

CYCLING PATH


DRAWING TITLE	DRAWING NO.	REVISION
TREATMENT AT MAJOR JUNCTION	LTA/SDRE17/21/CYC1	D
TREATMENT AT OTHER JUNCTIONS	LTA/SDRE17/21/CYC2	D
TREATMENT AT DEVELOPMENT / CARPARK ACCESS (SHEET 1 OF 2)	LTA/SDRE17/21/CYC3	C
TREATMENT AT DEVELOPMENT / CARPARK ACCESS WITH / WITHOUT SIDE FOOTPATH	LTA/SDRE17/21/CYC4	C
ACCESS FROM DEVELOPMENT		
BICYCLE CROSSING	LTA/SDRE17/21/CYC5	D
SHARED TRACK TREATMENT AT DEVELOPMENT / CARPARK ACCESS WITH / WITHOUT	LTA/SDRE17/21/CYC6	D
SIDE FOOTPATH ACCESS FROM DEVELOPMENT		
TREATMENT AT BUS STOP WITH BUS BAY	LTA/SDRE17/21/CYC7	D
TREATMENT AT BUS STOP WITHOUT BUS BAY	LTA/SDRE17/21/CYC8	D
CYCLING PAVEMENT MARKING DETAILS	LTA/SDRE17/21/CYC9	D
CYCLING SIGNS (SHEET 1 OF 2)	LTA/SDRE17/21/CYC10	B
CYCLING SIGNS (SHEET 2 OF 2)	LTA/SDRE17/21/CYC11	-
CYCLING TRACK LIGHTING	LTA/SDRE17/21/CYC12	A

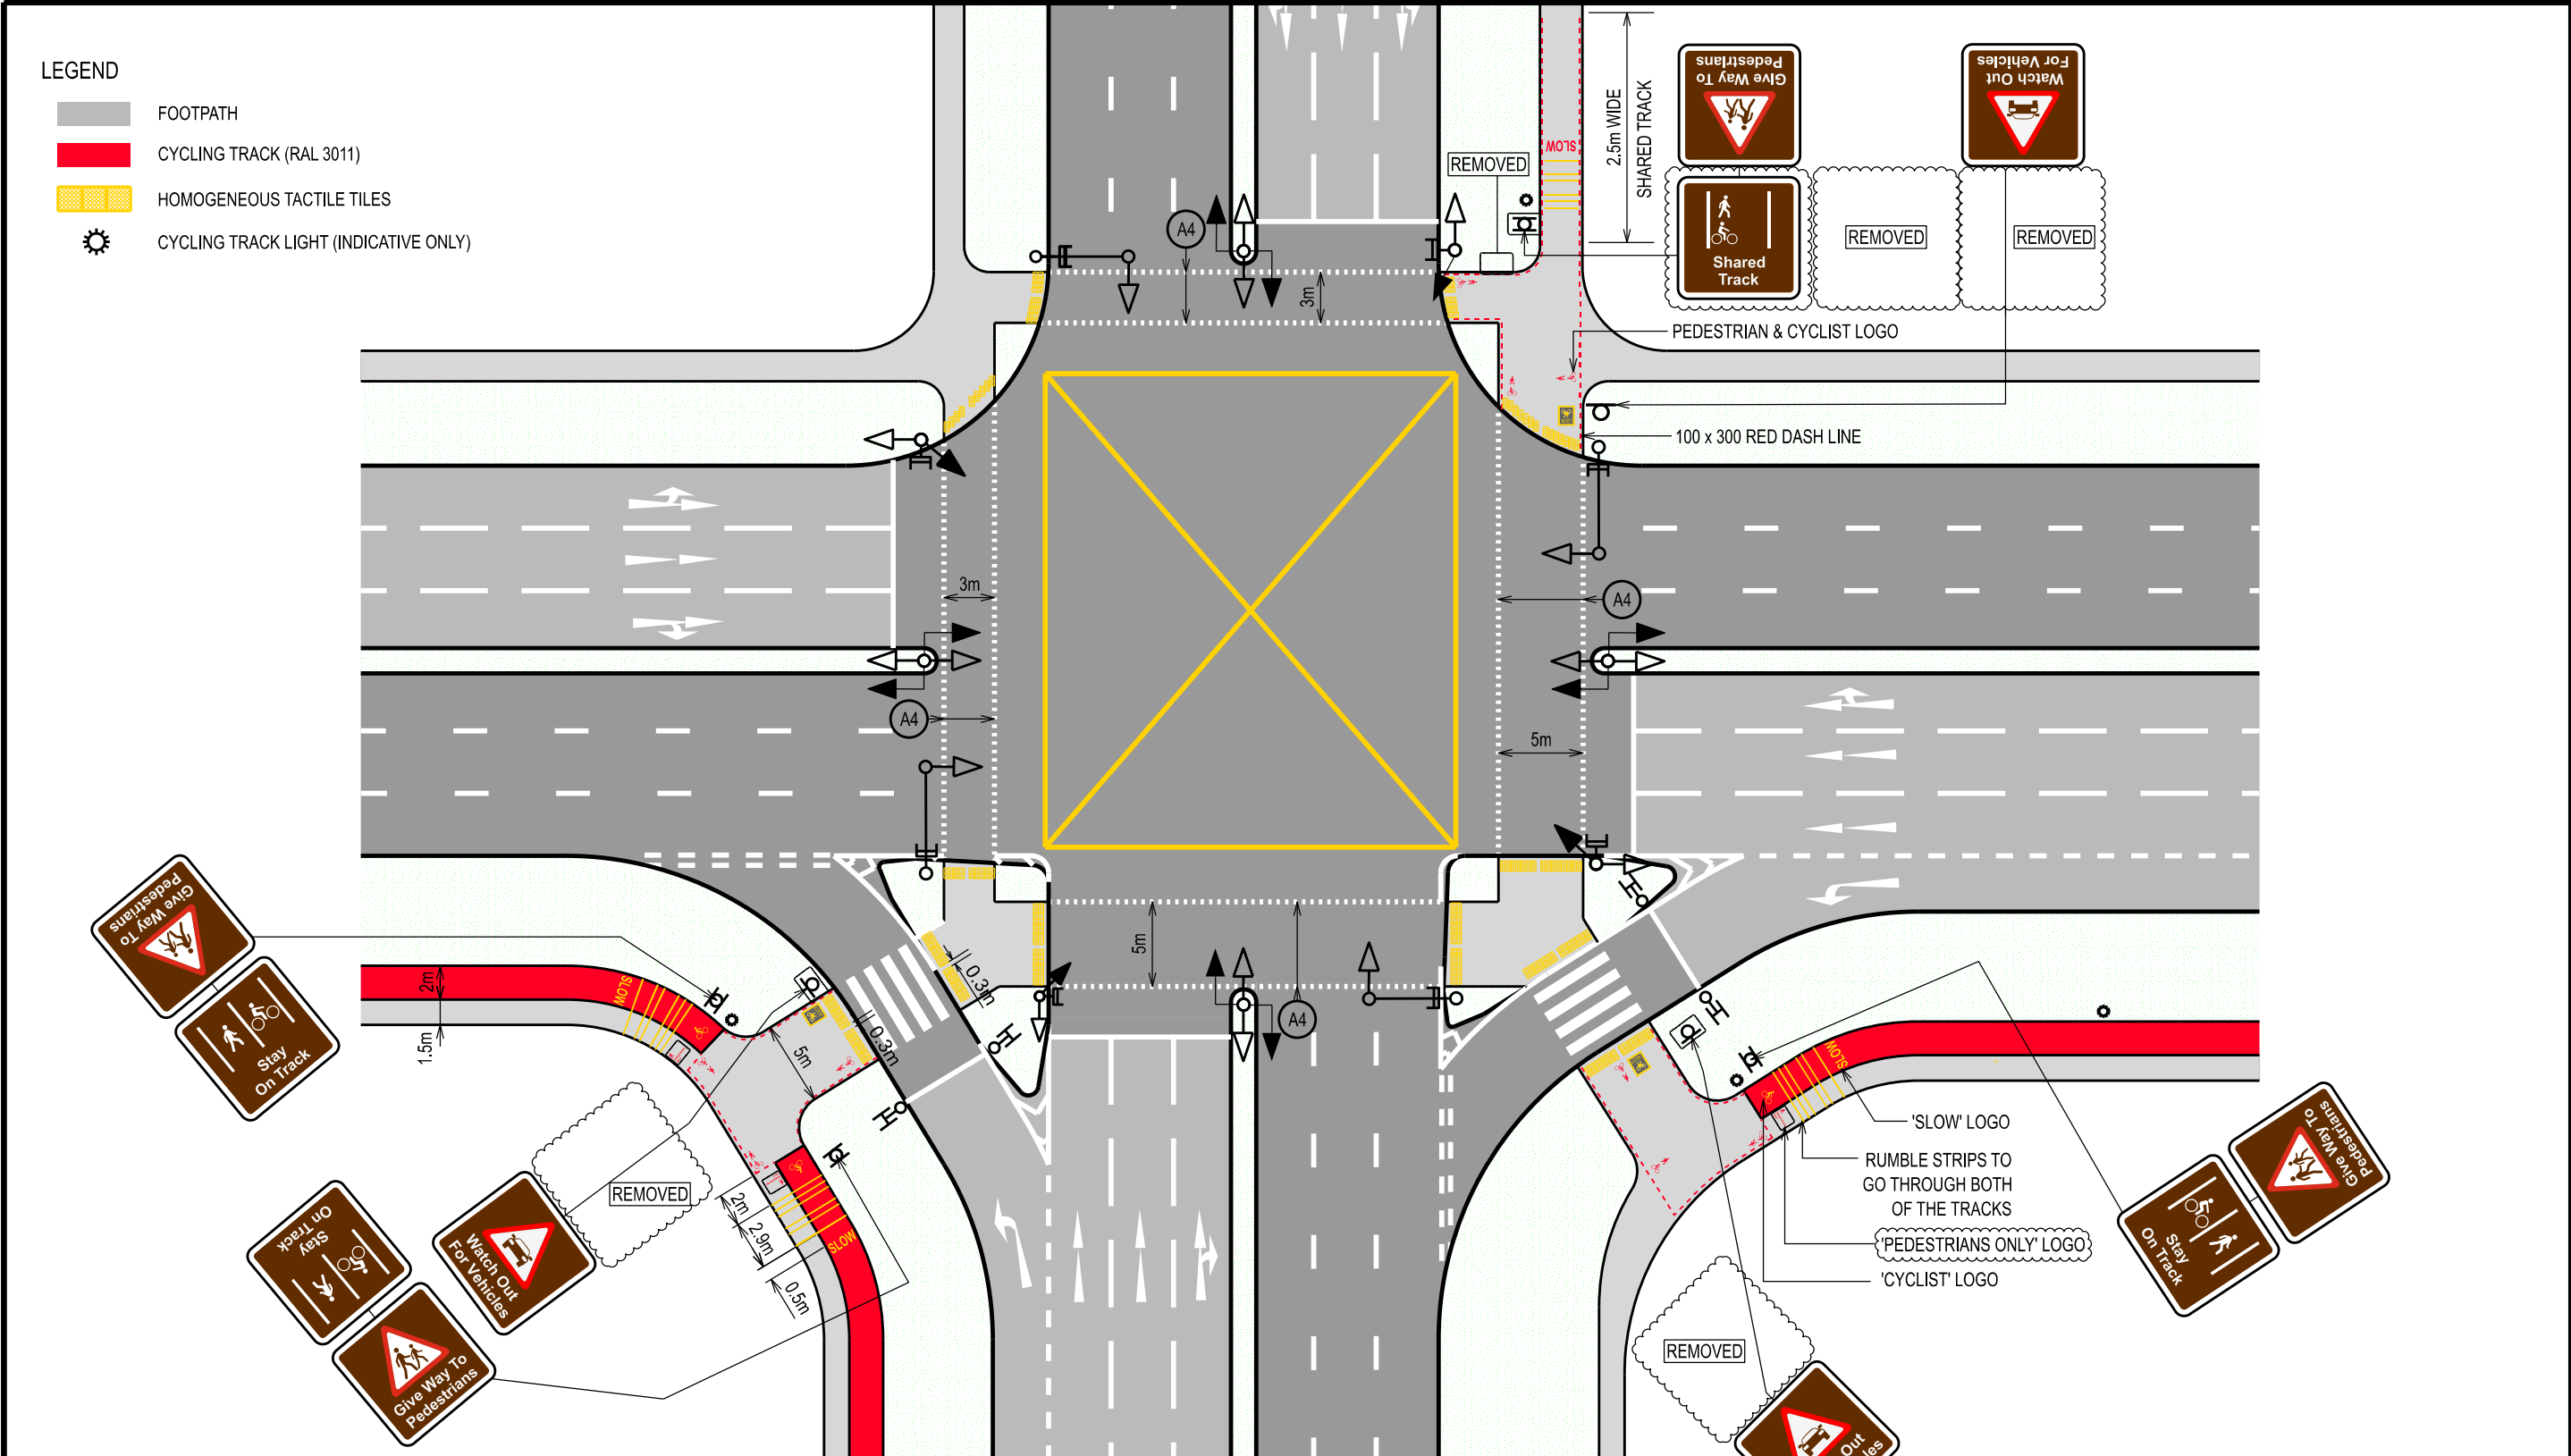

- NOTES:**
- Cyclist logo & signage provided at the first entry point to cycling track from a pedestrian crossing. Pedestrian-only logo to be provided at the first entry point to pedestrian-only paths next to dedicated cycling path.
 - Additional strips and other signage shall be applied if there is further need to slow down and warn the cyclist.
 - Wherever pedestrians/cyclists are likely to join the cycling track or pedestrian-only path, additional cyclist logo and pedestrian-only logo shall be provided.
 - Where the cycling track crosses a covered linkway, a reflective strip shall be pasted on the walkway roof/column to warn the cyclists.
 - All markings that are off carriageway shall use coloured high strength coating system (RAL 1003) or (RAL 3011) unless otherwise stated.

- Cycling track signages shall be installed on cycling track lighting poles if the intended location of the signages are next to it.
- Gratings/sumps that are on cycling track or shared track are to use pedestrian concrete in-filled grating unless otherwise stated. Details to follow drawing No. LTA/SDRE14/4/GRA2-3.
- Pavement details of cycling track to follow drawing No. LTA/SDRE14/3/KER11.
- For cycling track lighting reference shall be made to LTA/SDRE17/21/CYC12.
- For all road markings reference shall be made to LTA/SDRE14/8/RMS1-3.
- Cyclist, shared track (pedestrian & cyclists), or pedestrian-only marking to be placed at minimum 50m intervals at alternate orientations if there are no markings to indicate to users that they are travelling on the cycling track or shared track or pedestrian only path.
- All associated road markings, signages and road elements shall be adjusted accordingly in compliance with SDRE standards when crossings are widened.

		STANDARD	DETAIL	Land Transport Authority		
D	MAR 2025	TREATMENT AT MAJOR JUNCTION		DRAWING NO.		REV.
C	APR 2024			LTA/SDRE17/21/CYC1		D
B	APR 2022					
A	APR 2019					
REV.	DATE			DATE OF ISSUE	SCALE	SHEET NO.
				SEP 2017	1:400	1 OF 1

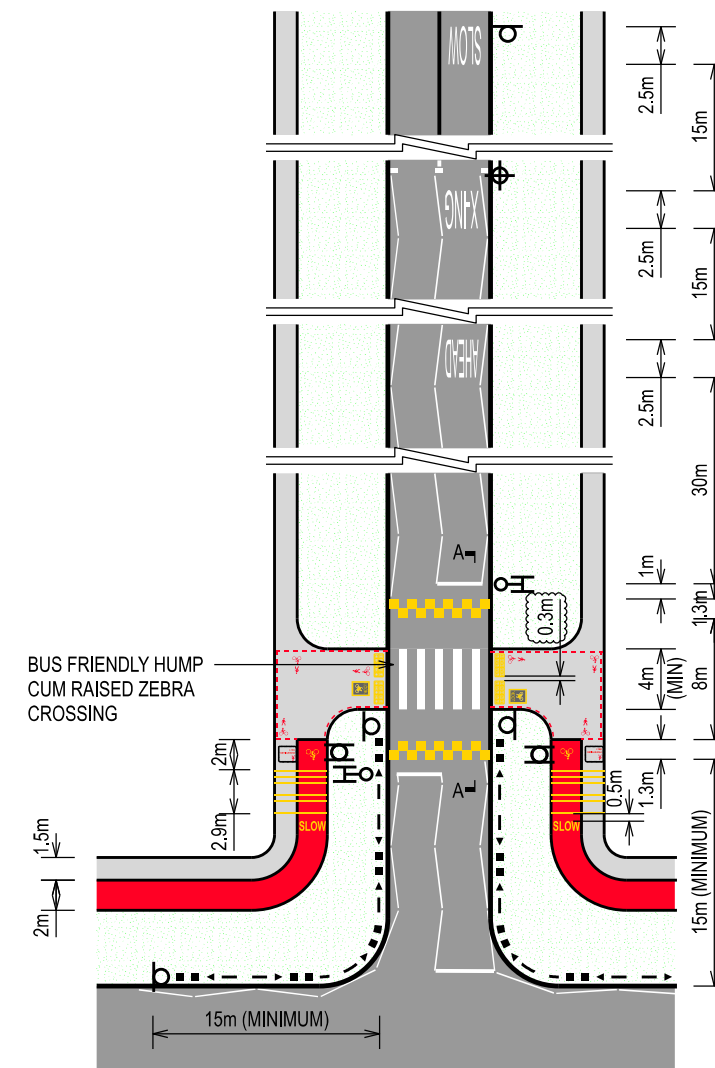


TREATMENT AT UNSIGNALISED JUNCTION

(DIMENSION)
SCALE 1:500




1. Notes refer to Drawing No. LTA/SDRE17/21/CYC1.
2. Refer for other details for bus friendly hump cum raised zebra crossing.
3. To add zebra crossing at unsignalised junction with minimum setback of 15m.

		STANDARD DETAIL	Land Transport Authority			
D	MAR 2025	TREATMENT AT OTHER JUNCTIONS	DRAWING NO. LTA/SDRE17/21/CYC2		REV. D	
C	APR 2024					
B	APR 2022		DATE OF ISSUE SEP 2017		SCALE AS SHOWN	SHEET NO. 1 OF 1
A	APR 2019					
REV.	DATE					

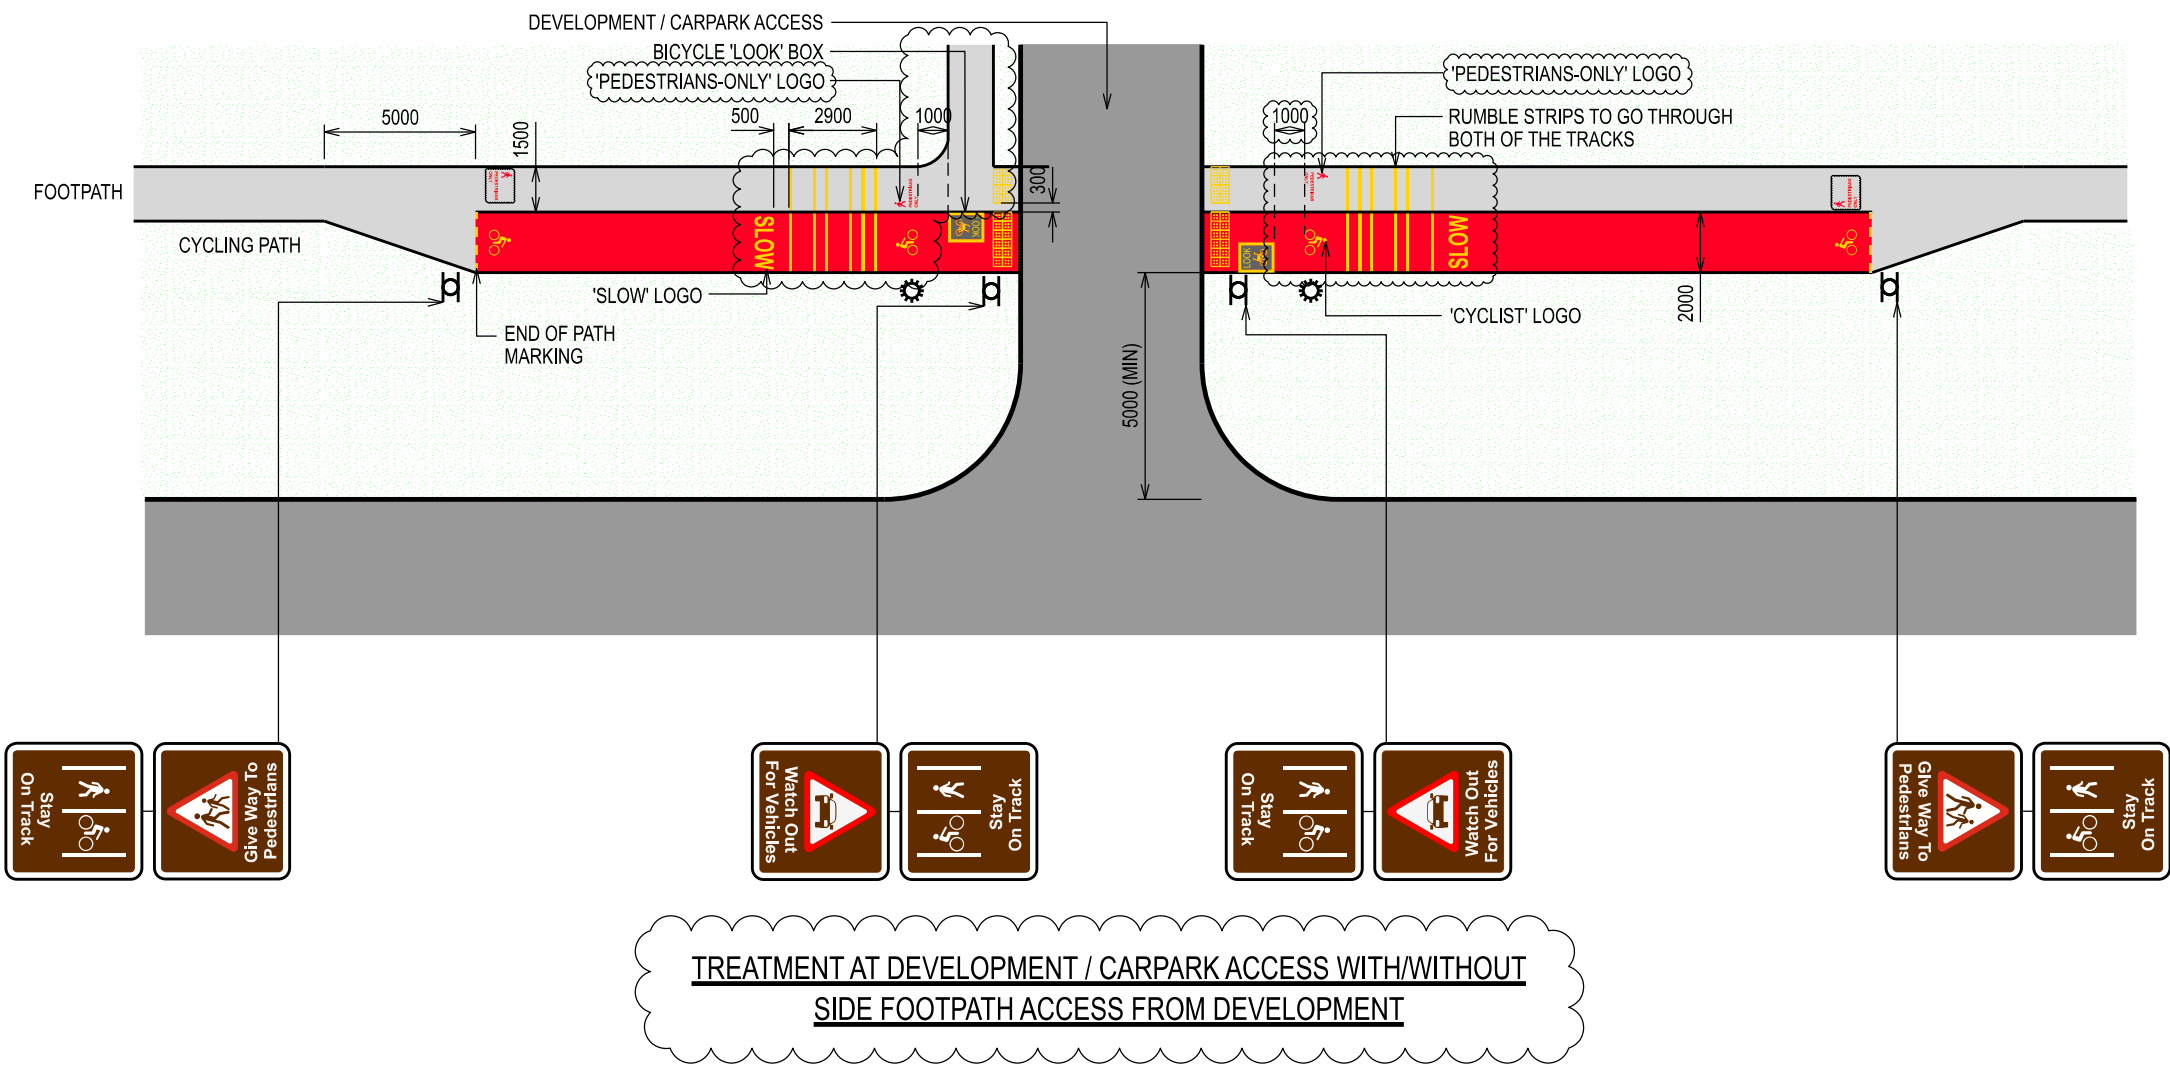



NOTES:
1. Notes refer to Drawing No. LTA/SDRE17/21/CYC1.

STANDARD DETAIL		Land Transport Authority	
TREATMENT AT DEVELOPMENT / CARPARK ACCESS WITH / WITHOUT SIDE FOOTPATH ACCESS FROM DEVELOPMENT		DRAWING NO.	REV.
		LTA/SDRE17/21/CYC4	C
REV.	DATE	DATE OF ISSUE	SHEET NO.
C	MAR 2025	SEP 2017	1 OF 1
B	APR 2024	SCALE	
A	APR 2022	1:250	

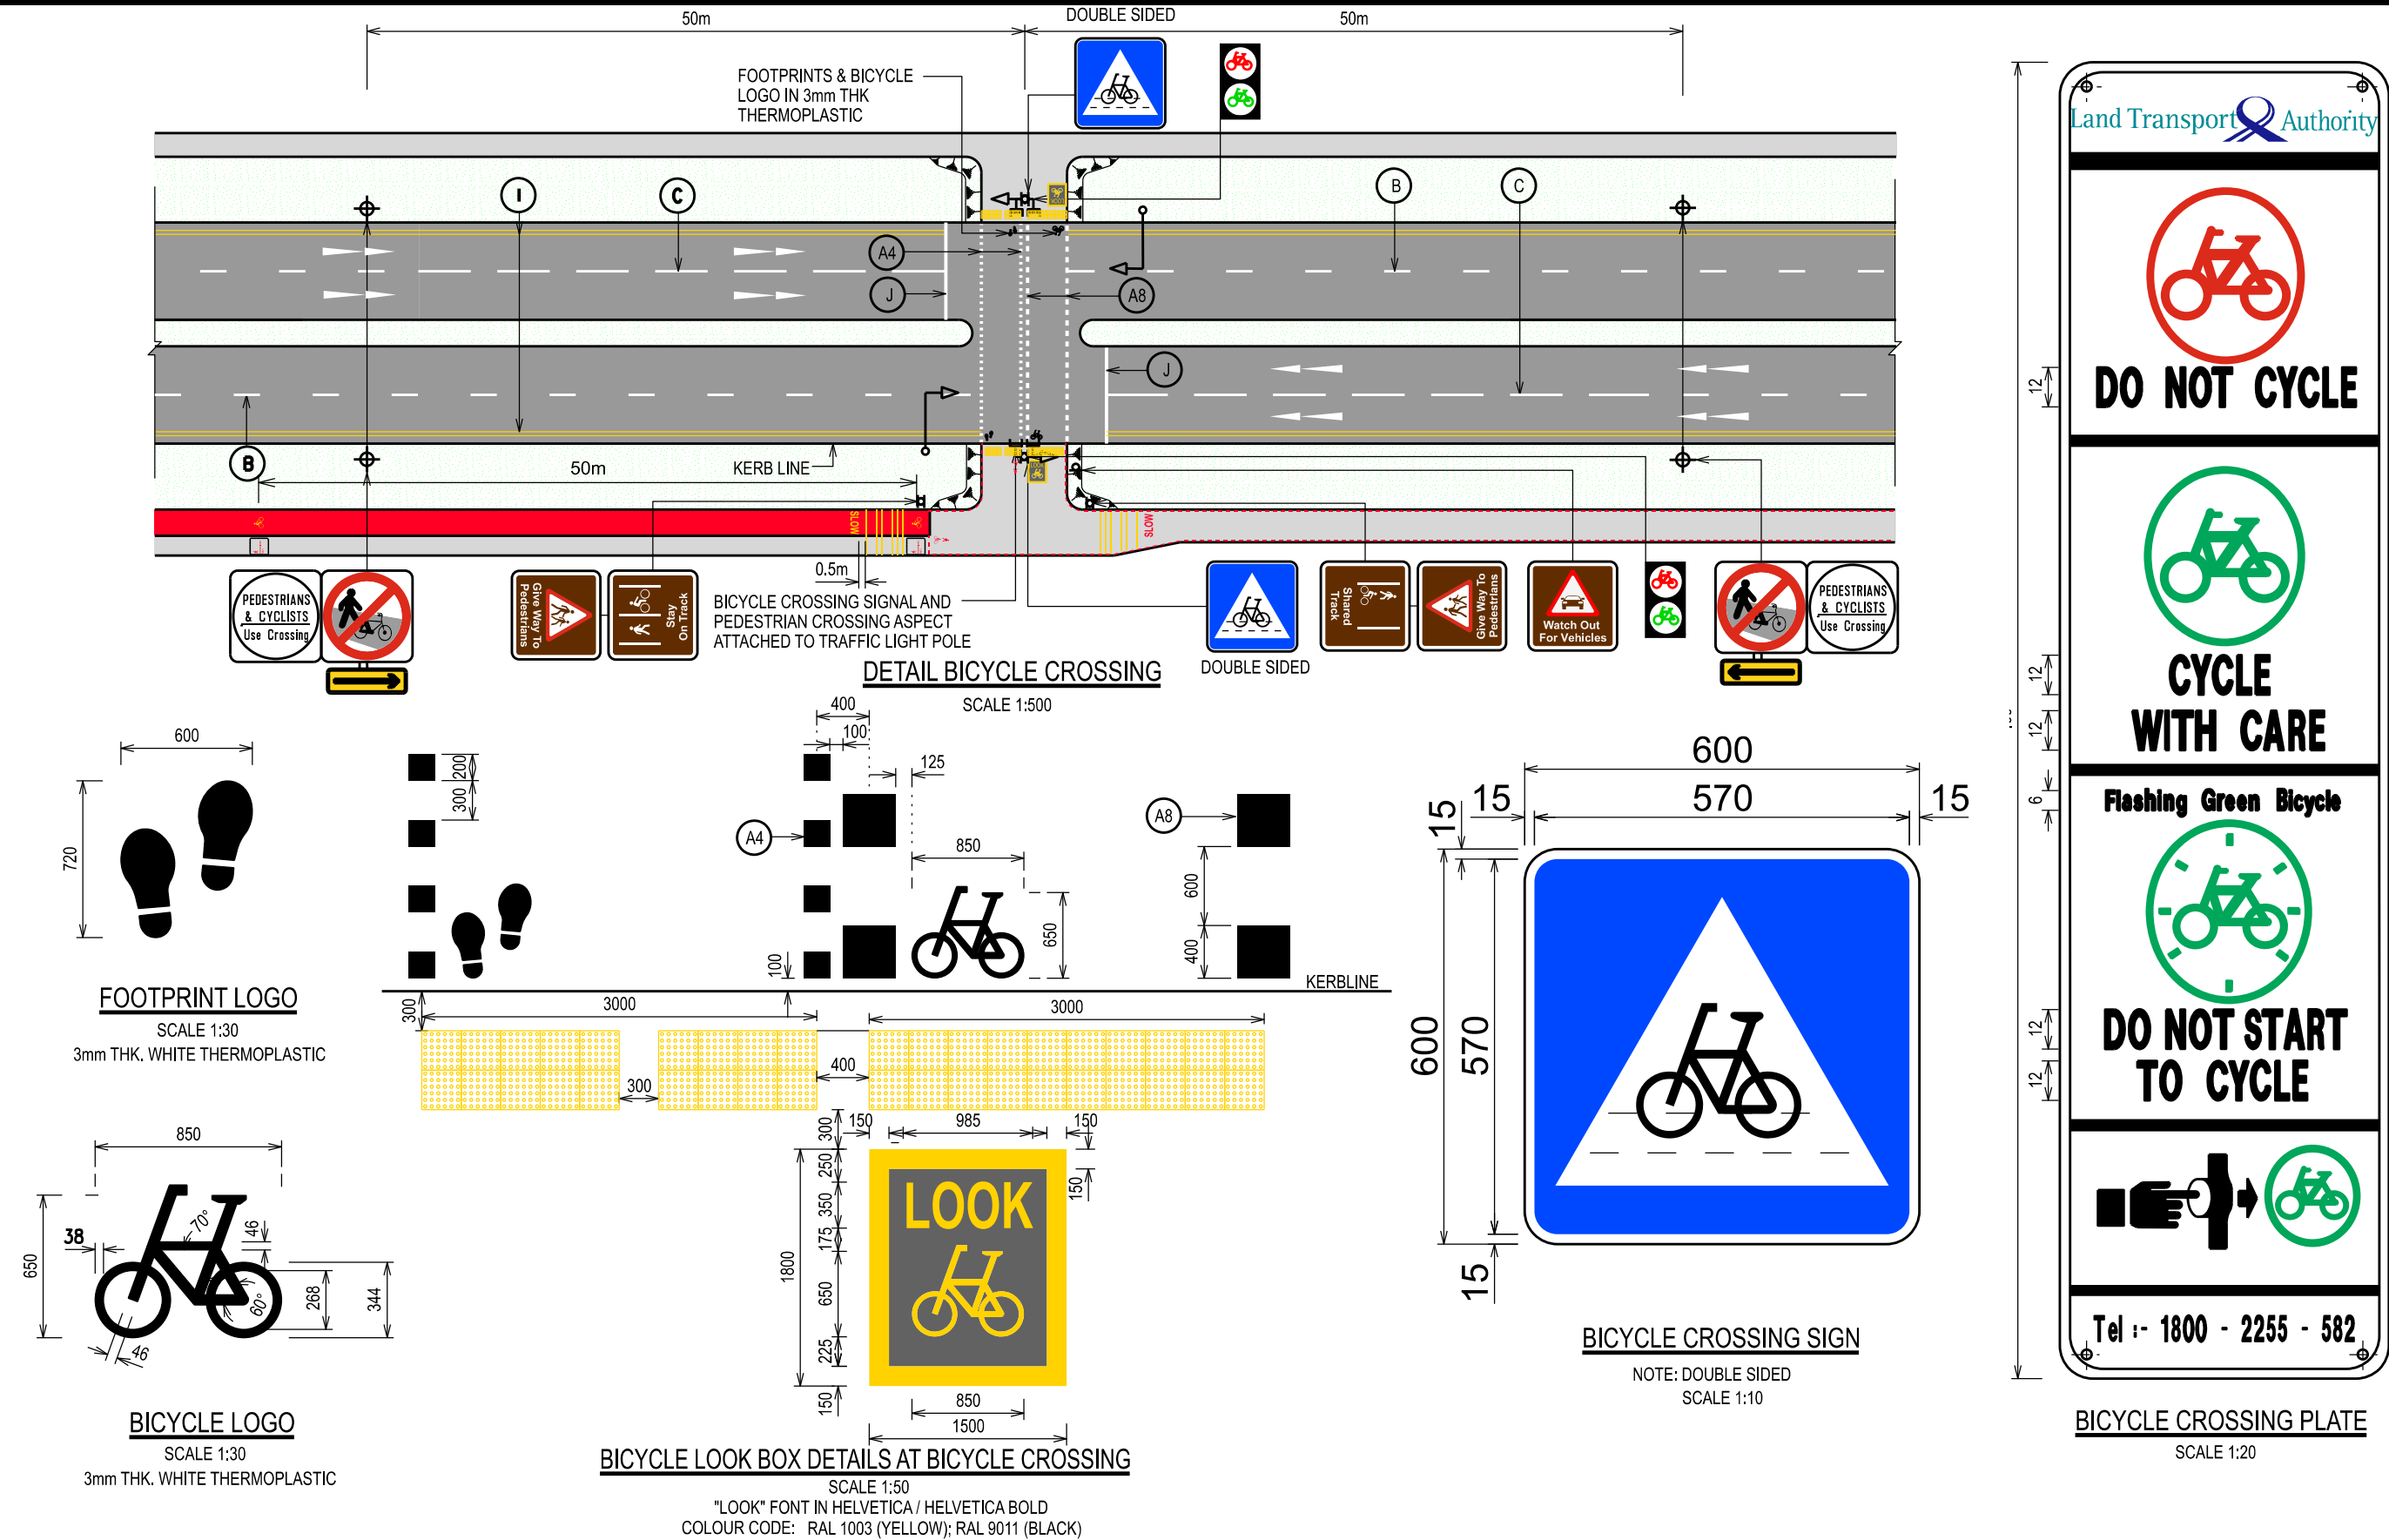


- NOTES:**
1. Bicycle crossing is to be situated at the side that is nearer to the cycling path or bicycle parking facilities.
 2. Bicycle crossing plate is to be placed on cycling path traffic pole.
 3. Notes refer to Drawing No. LTA/SDRE17/21/CYC1.
 4. Headroom clearance for all signs is 2.4m. Refer to "Support for Road Signs" chapter for details.
 5. For all road markings reference shall be made to LTA/SDRE14/8/RMS1-3.

STANDARD		DETAIL	
D		MAR 2025	
C		APR 2024	
B		APR 2022	
A		APR 2019	
REV.		DATE	
BICYCLE CROSSING		BICYCLE CROSSING	
DRAWING NO.		LTA/SDRE17/21/CYC5	
DATE OF ISSUE		SEP 2017	
SCALE		AS SHOWN	
SHEET NO.		1 OF 1	

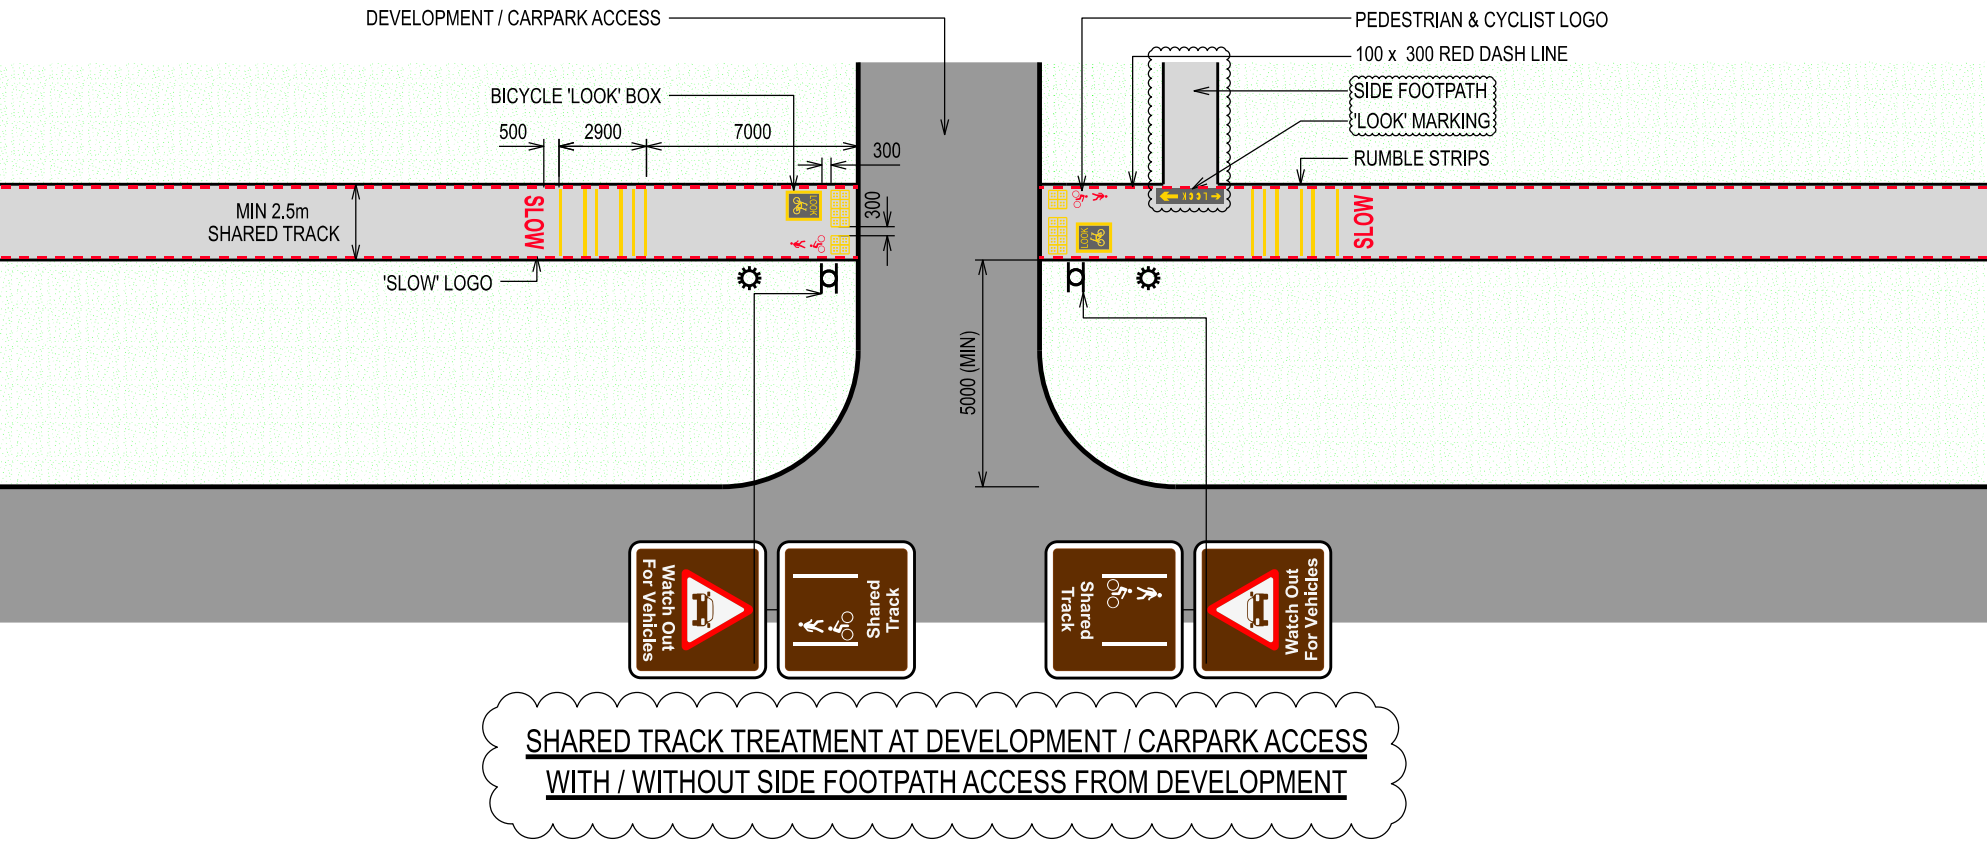
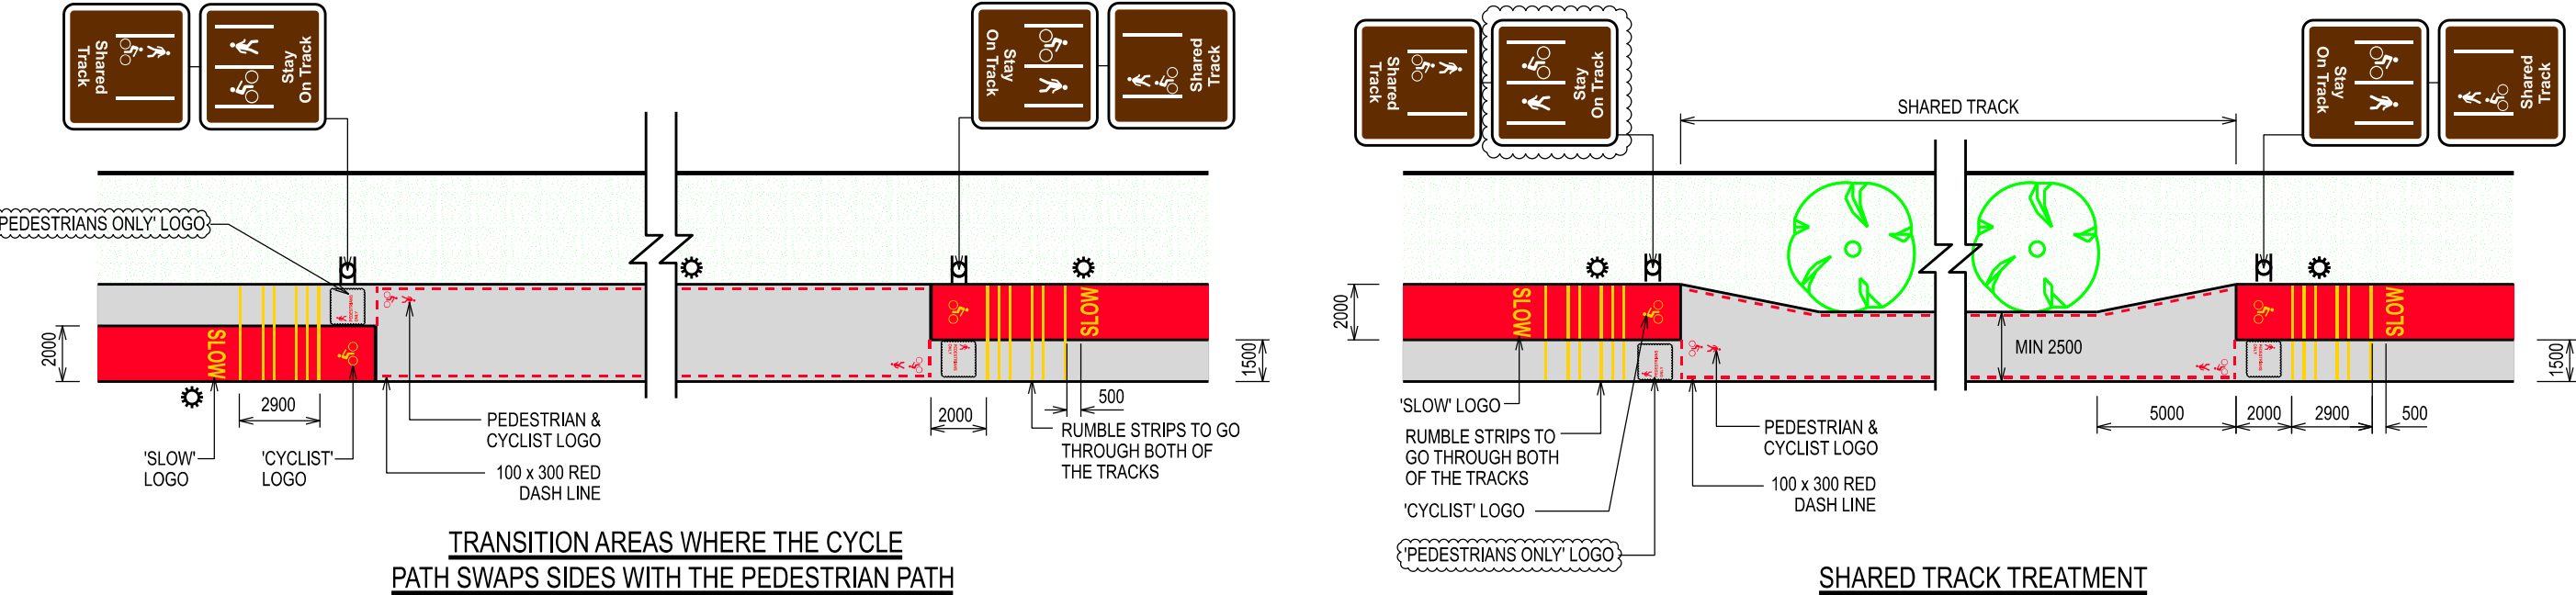


NOTES:
1. Only applicable when there are site constraint and subject to authorities approval.


STANDARD DETAIL		Land Transport Authority		
D MAR 2025 C APR 2024 B APR 2022 A APR 2019 REV. DATE		SHARED TRACK TREATMENT AT DEVELOPMENT / CARPARK ACCESS WITH / WITHOUT SIDE FOOTPATH ACCESS FROM DEVELOPMENT		DRAWING NO. LTA/SDRE17/21/CYC6
				REV. D
				DATE OF ISSUE SEP 2017
				SCALE 1:250
				SHEET NO. 1 OF 1

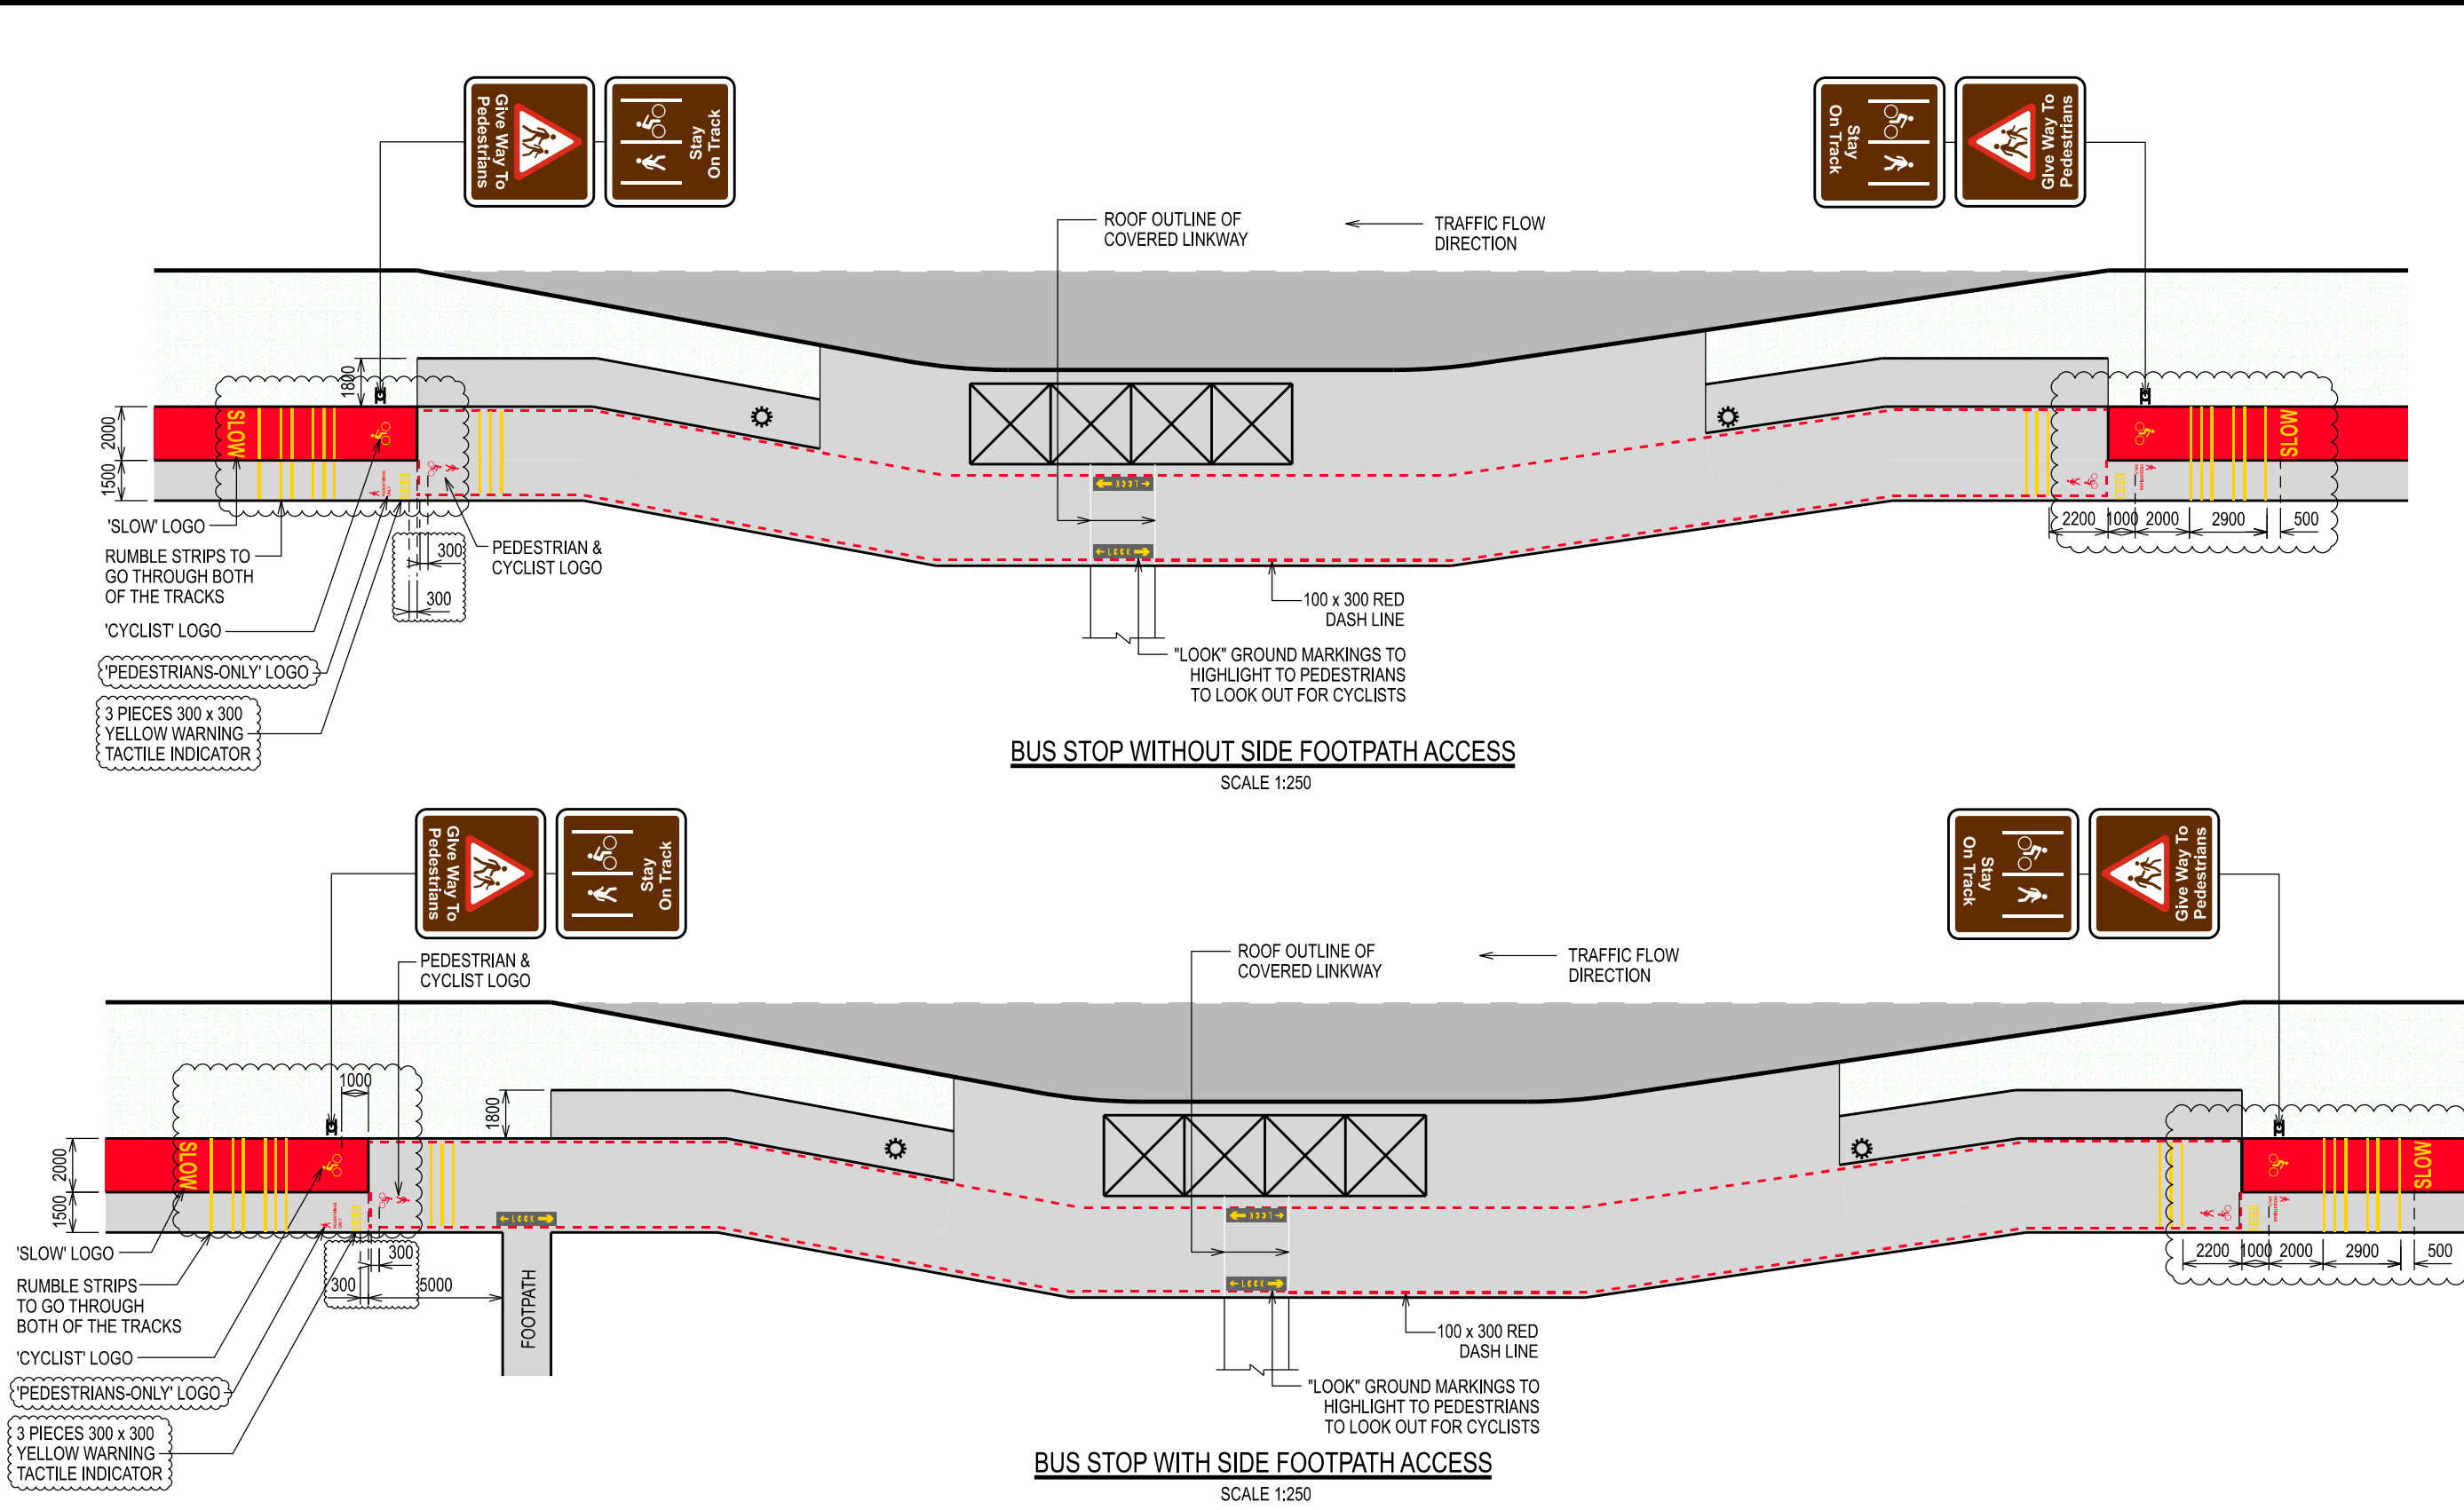

STANDARD DETAIL		Land Transport Authority		
TREATMENT AT BUS STOP WITH BUS BAY		DRAWING NO. LTA/SDRE17/21/CYC7		REV. D
		DATE OF ISSUE SEP 2017	SCALE AS SHOWN	SHEET NO. 1 OF 2
REV.	DATE			
A	APR 2019			
B	APR 2022			
C	APR 2024			
D	MAR 2025			

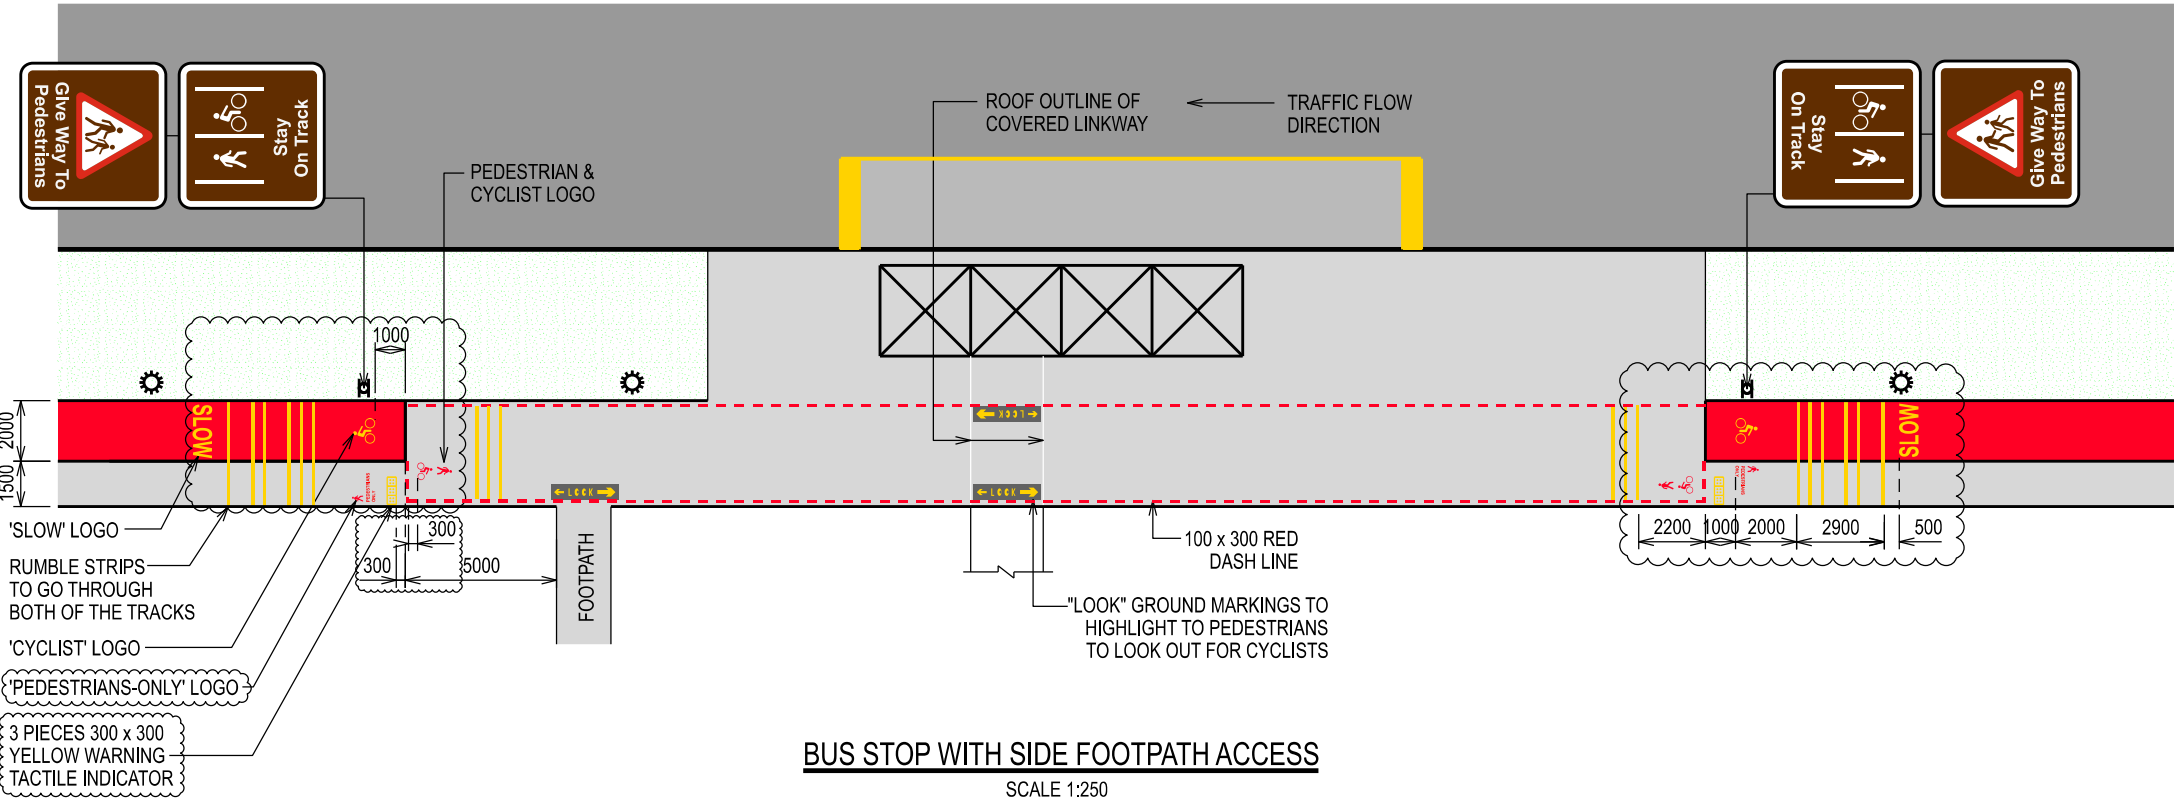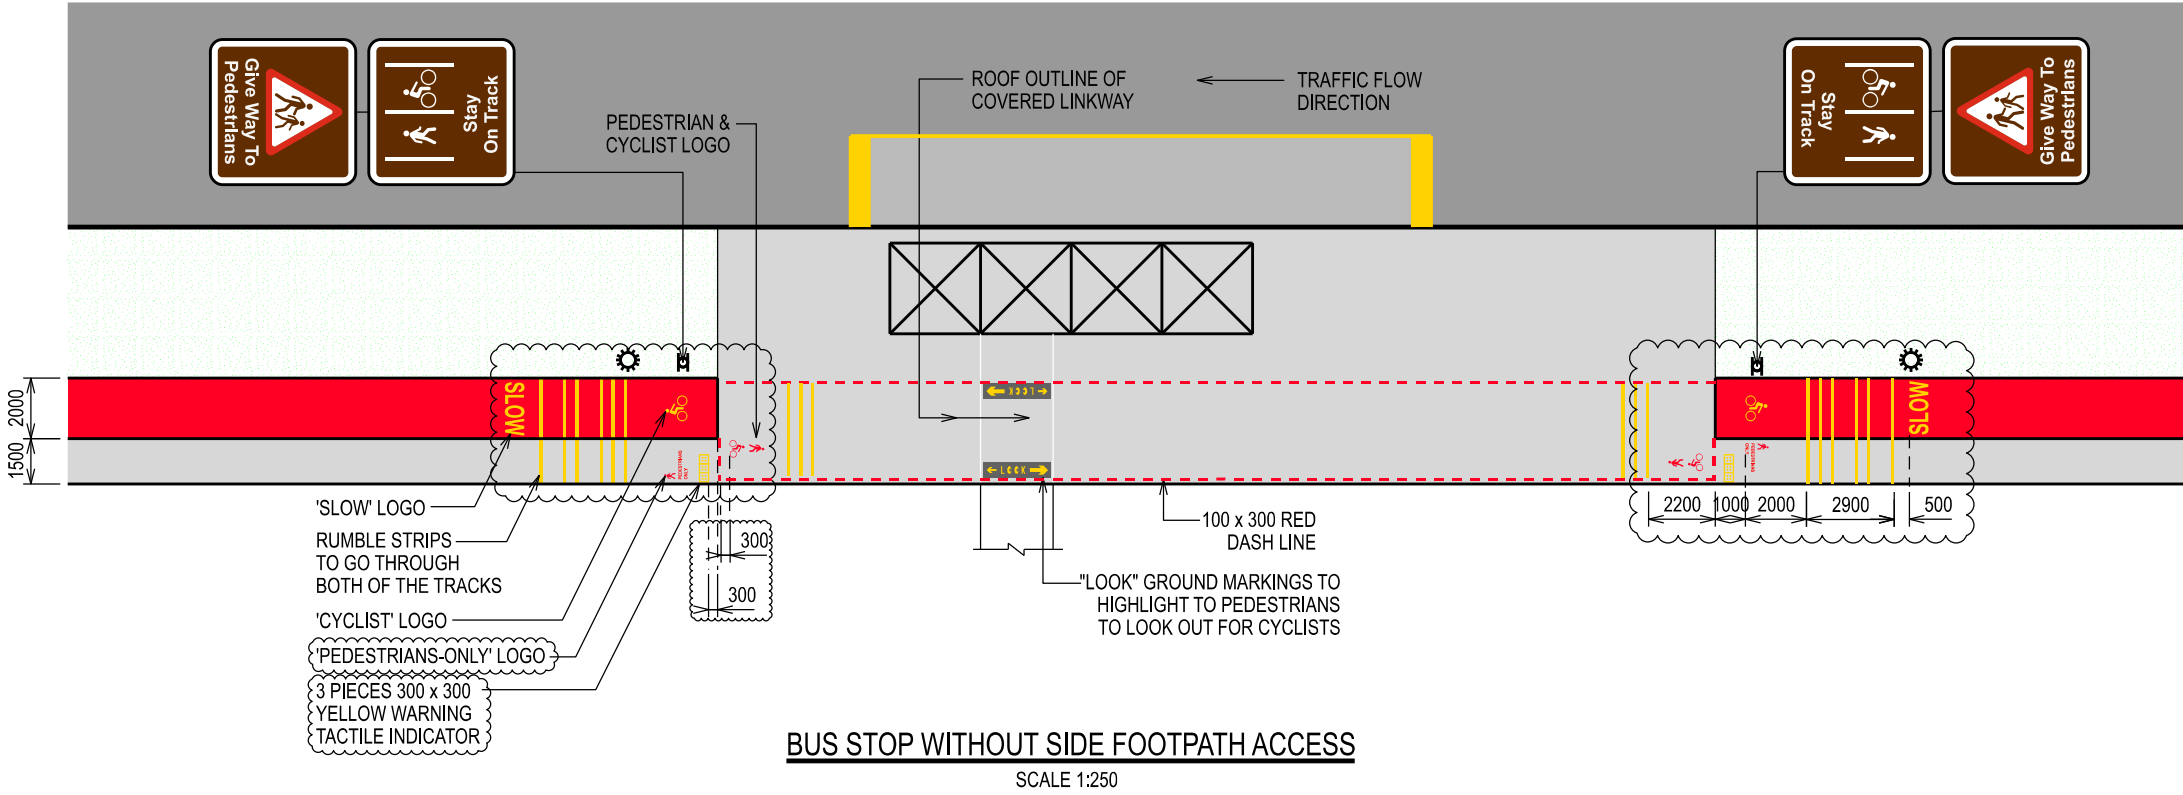


		STANDARD DETAIL	Land Transport Authority			
D	MAR 2025		TREATMENT AT BUS STOP WITHOUT BUS BAY	DRAWING NO. LTA/SDRE17/21/CYC8		REV. D
C	APR 2024					
B	APR 2022	DATE OF ISSUE SEP 2017		SCALE AS SHOWN	SHEET NO. 2 OF 2	
A	APR 2019					
REV.	DATE					

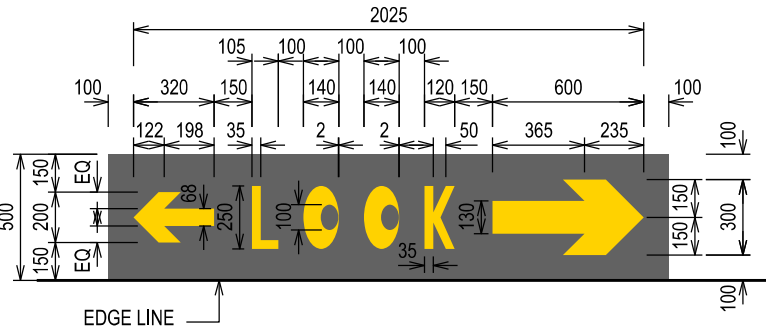


"LOOK" MARKING

SCALE 1:30
COLOUR CODE: RAL 1003 (YELLOW)
RAL 9011 (BLACK)

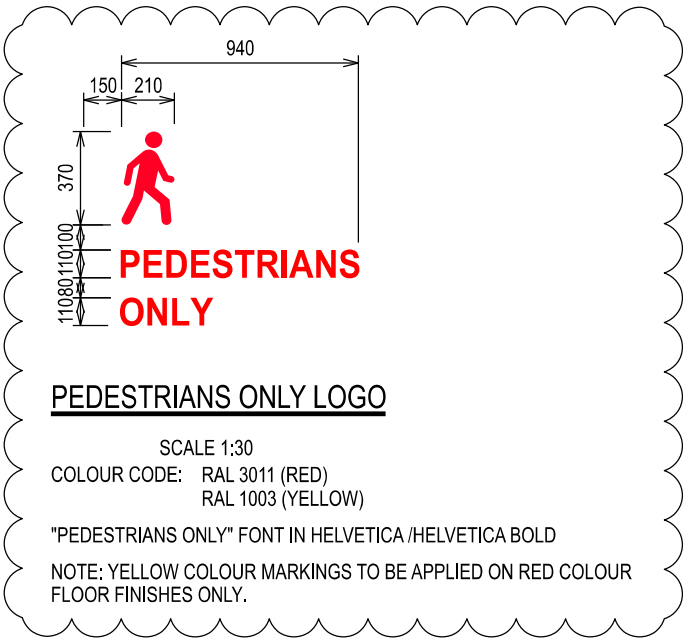

PEDESTRIANS ONLY LOGO


SCALE 1:30
COLOUR CODE: RAL 3011 (RED)
RAL 1003 (YELLOW)
"PEDESTRIANS ONLY" FONT IN HELVETICA/HELVETICA BOLD
NOTE: YELLOW COLOUR MARKINGS TO BE APPLIED ON RED COLOUR FLOOR FINISHES ONLY.

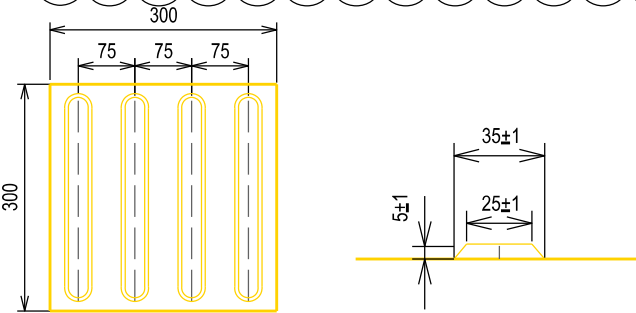

TOP VIEW
SCALE 1:10

ELONGATED PATTERN DETAIL
SCALE 1:3

DIRECTIONAL TACTILE TILE

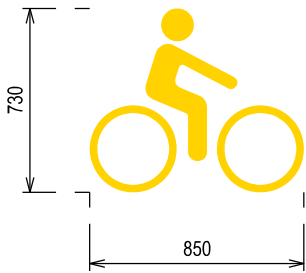


CYCLIST LOGO

SCALE 1:30
COLOUR CODE: RAL 1003 (YELLOW)
RAL 3011 (RED)
NOTE: YELLOW COLOUR MARKINGS ON RED COLOUR PATH FINISHES. RED COLOUR MARKINGS ON OTHER FINISHES.




SLOW LOGO

SCALE 1:30
COLOUR CODE: RAL 1003 (YELLOW)
RAL 3011 (RED)
"SLOW" FONT IN HELVETICA / HELVETICA BOLD
NOTE: YELLOW COLOUR MARKINGS ON RED COLOUR PATH FINISHES. RED COLOUR MARKINGS ON OTHER FINISHES.

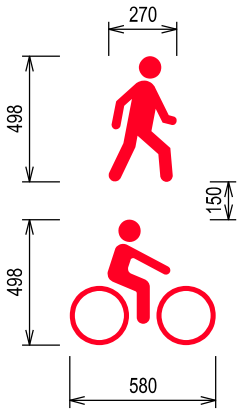


PEDESTRIAN & CYCLIST LOGO

SCALE 1:30
COLOUR CODE: RAL 3011 (RED)
RAL 1003 (YELLOW)
NOTE: YELLOW COLOUR MARKINGS TO BE APPLIED ON RED COLOUR FLOOR FINISHES ONLY.

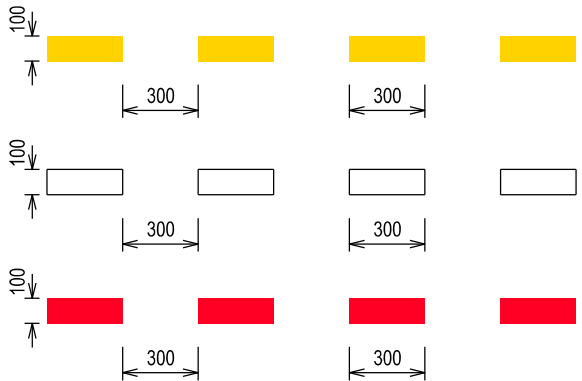


DASH LINE MARKING /
END OF PATH MARKING

SCALE 1:30
COLOUR CODE: RAL 3011 (RED)
RAL 1003 (YELLOW)
WHITE
NOTE: YELLOW COLOUR MARKINGS TO BE APPLIED ON RED COLOUR FLOOR FINISHES ONLY. RED COLOUR MARKINGS ON OTHER FINISHES.

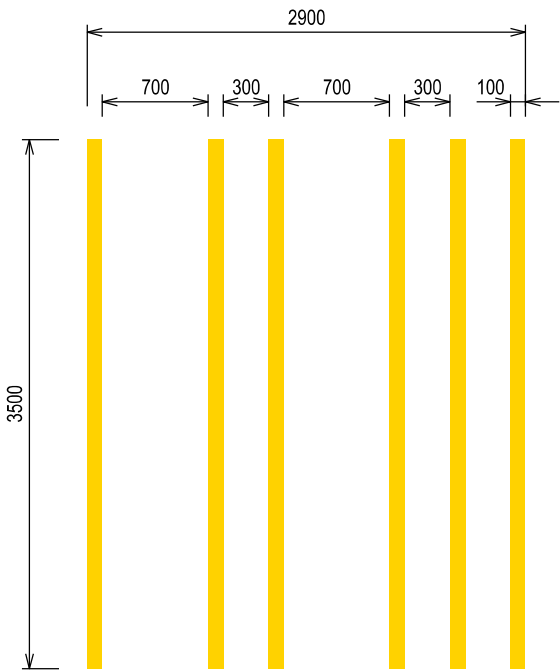


RUMBLE STRIPS

SCALE 1:50
STRIPS THICKNESS: 3mm THERMOPLASTIC

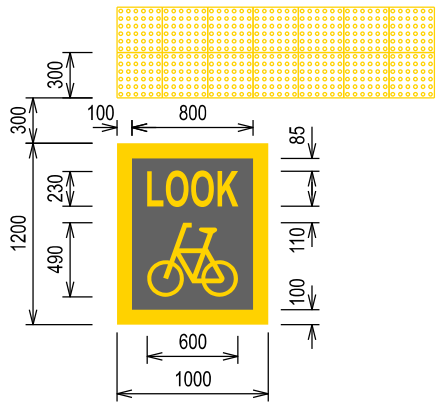

BICYCLE LOOK BOX DETAIL

SCALE 1:50
"LOOK" FONT IN HELVETICA / HELVETICA BOLD
COLOUR CODE: RAL 1003 (YELLOW)
RAL 9011 (BLACK)

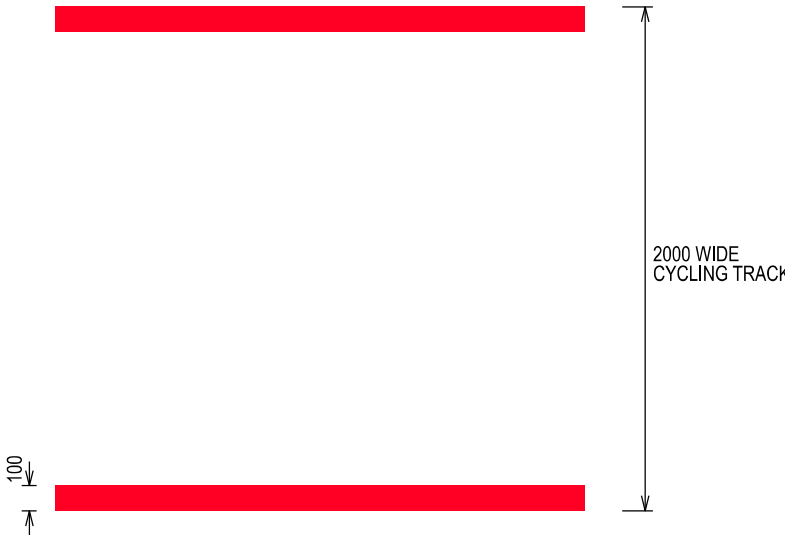

SOLID LINE MARKING TO DEMARCAT
CYCLING TRACK (NON-CONCRETE FINISHES ONLY)

SCALE 1:30
COLOUR CODE: RAL 3011 (RED)
RAL 1003 (YELLOW)
NOTE: YELLOW COLOUR MARKINGS TO BE APPLIED ON RED COLOUR FLOOR FINISHES ONLY.

NOTES:

1. All markings shall be minimum 50mm offset from adjacent markings unless otherwise stated.
2. All footpaths within road reserve line (RRL) beside cycling tracks are to be designated as pedestrian-only paths with pedestrian-only logo.

STANDARD DETAIL


CYCLING PAVEMENT
MARKINGS DETAILS




DRAWING NO. LTA/SDRE17/21/CYC9		REV. D
DATE OF ISSUE SEP 2017	SCALE AS SHOWN	SHEET NO. 1 OF 1



WATCH OUT FOR CYCLISTS
THIS SIGN INFORMS PEDESTRIANS TO LOOKOUT FOR APPROACHING CYCLISTS

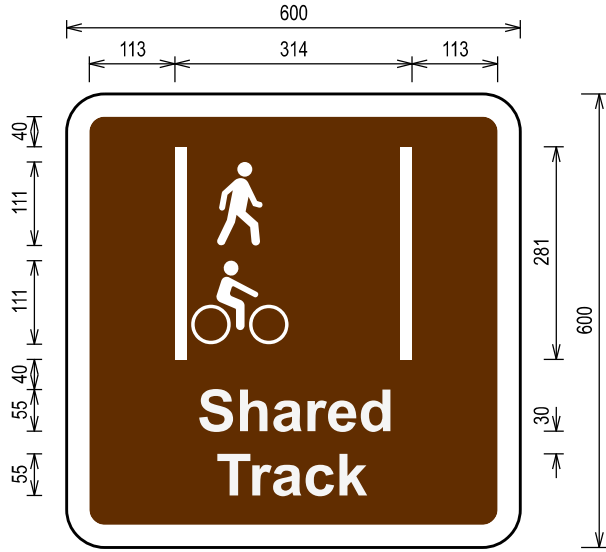

SHARED TRACK
THIS SIGN IS USED TO INDICATE A SHARED TRACK. USUALLY PLACED AT THE START OF THE TRACK.

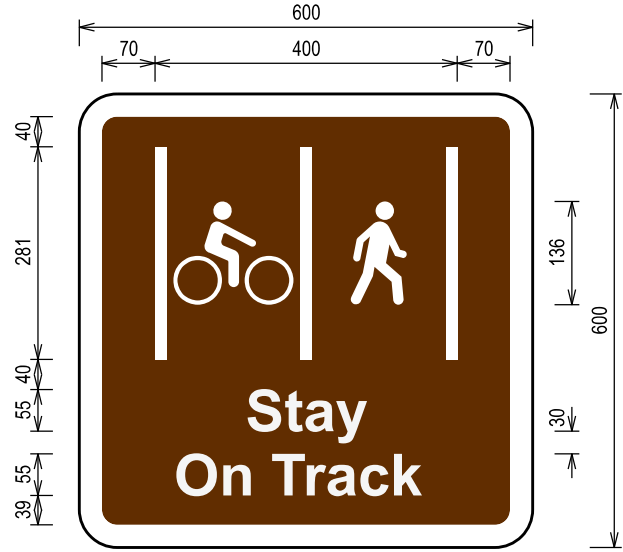


STAY ON TRACK
THESE SIGNS ARE USED TO INDICATE A SEGREGATED TRACK. USUALLY PLACED AT THE START OF THE TRACK.




GIVE WAY TO PEDESTRIANS
THIS SIGN INFORMS CYCLISTS TO GIVE WAY TO PEDESTRIANS ESPECIALLY AT AREAS WHERE THE PEDESTRIANS PATH SUCH AS STAIRCASES, RAMPS, BUS-STOPS, FOOTPATH ETC INTERSECTS THE CYCLING TRACK.



WATCH OUT FOR VEHICLES
THIS SIGN INFORMS CYCLISTS TO LOOKOUT FOR APPROACHING VEHICLES AT CARPARK ACCESSES/ UNSIGNALISED JUNCTIONS/ SIGNALISED JUNCTIONS/ CROSSINGS. THIS SIGN MAY ALSO BE USED FOR OTHER AREAS WHERE CYCLING PATHS INTERFERE WITH ROADS.

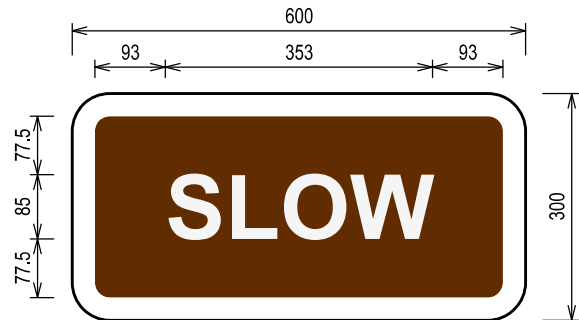

SLOW (SUPPLEMENTARY)
TO BE PLACED BELOW STANDARD SIGNAGE, WHERE NECESSARY.

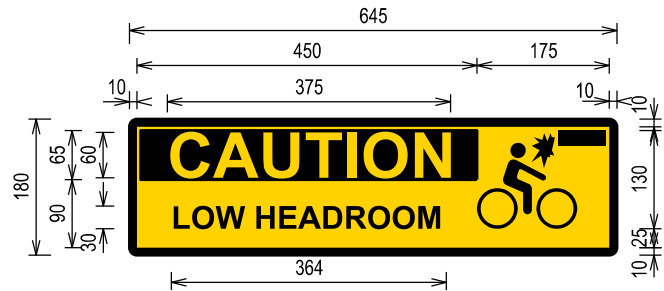

CAUTION LOW HEADROOM
THIS SIGN WARNS CYCLISTS OF THE LOW HEADROOM AHEAD.
COLOUR CODE: RAL 1018 (YELLOW)
RAL 9011 (BLACK)
NOTE: FOR CLEAR HEIGHT LESS THAN 2.4m


NOTES:

1. Design details:


Text: Helvetica / Helvetica Bold
Material: Refer to M&W Specification For Civil And Structural Works (Revision A1, June 2010 Edition) including all other subsequent amendments.
Fixture: Refer to SDRE (2014 Edition) including all other subsequent amendments.
All signs are colour brown background (RAL 8011, Nut Brown), red triangle with white lettering, line & border unless otherwise stated.

2. Headroom clearance for all signs is 2.4m. Refer to "Support for Road Signs" chapter for details.


			STANDARD DETAIL		Land Transport Authority			
			CYCLING SIGNS		DRAWING NO.		REV.	
					LTA/SDRE17/21/CYC10		B	
					DATE OF ISSUE		SCALE	SHEET NO.
					SEP 2017		1:10	1 OF 2
B	MAR 2025							
A	APR 2019							
REV.	DATE							

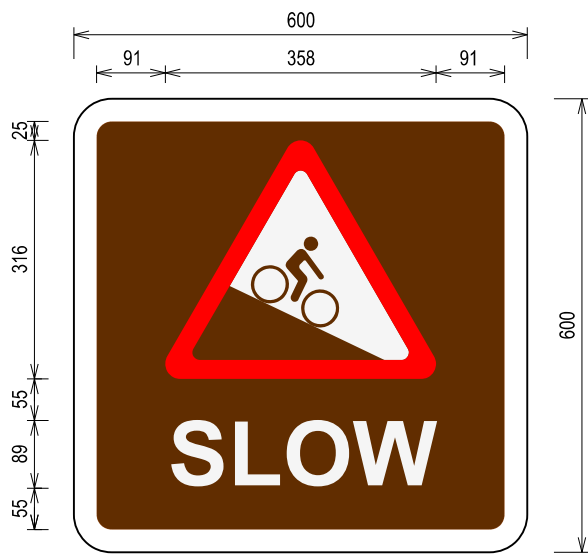

SLOPE AHEAD
THIS SIGN INFORMS CYCLISTS
THERE IS SLOPE AHEAD AND
TO SLOW THEIR SPEED

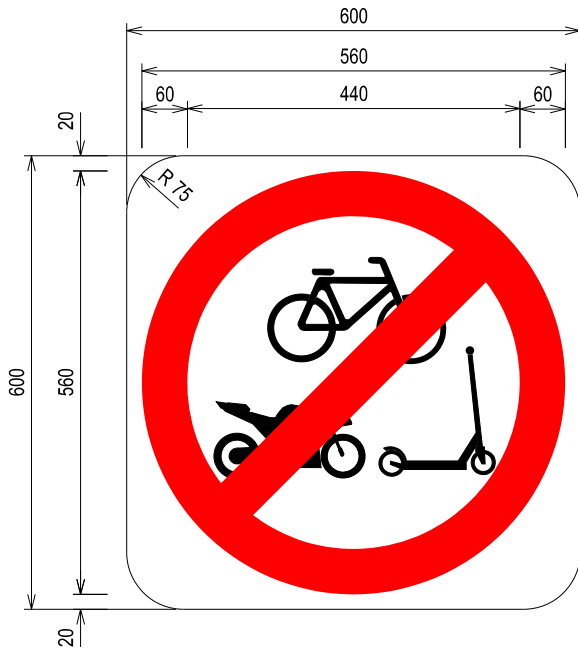


NO RIDING
THIS SIGN IS USED TO INDICATE PROHIBITION ON RIDING.
USUALLY PLACED AT THE START AND END OF THE PATH.

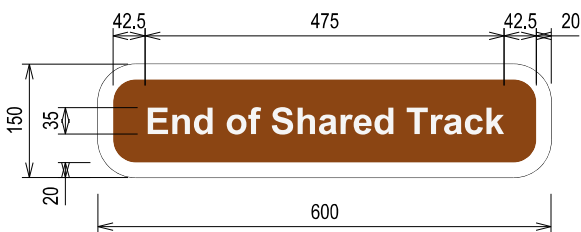

END OF SHARED TRACK
THIS SIGN IS USED TO INDICATE THE END OF SHARED TRACK.
USUALLY PLACED AT THE END OF THE TRACK.

	</
--	--	----

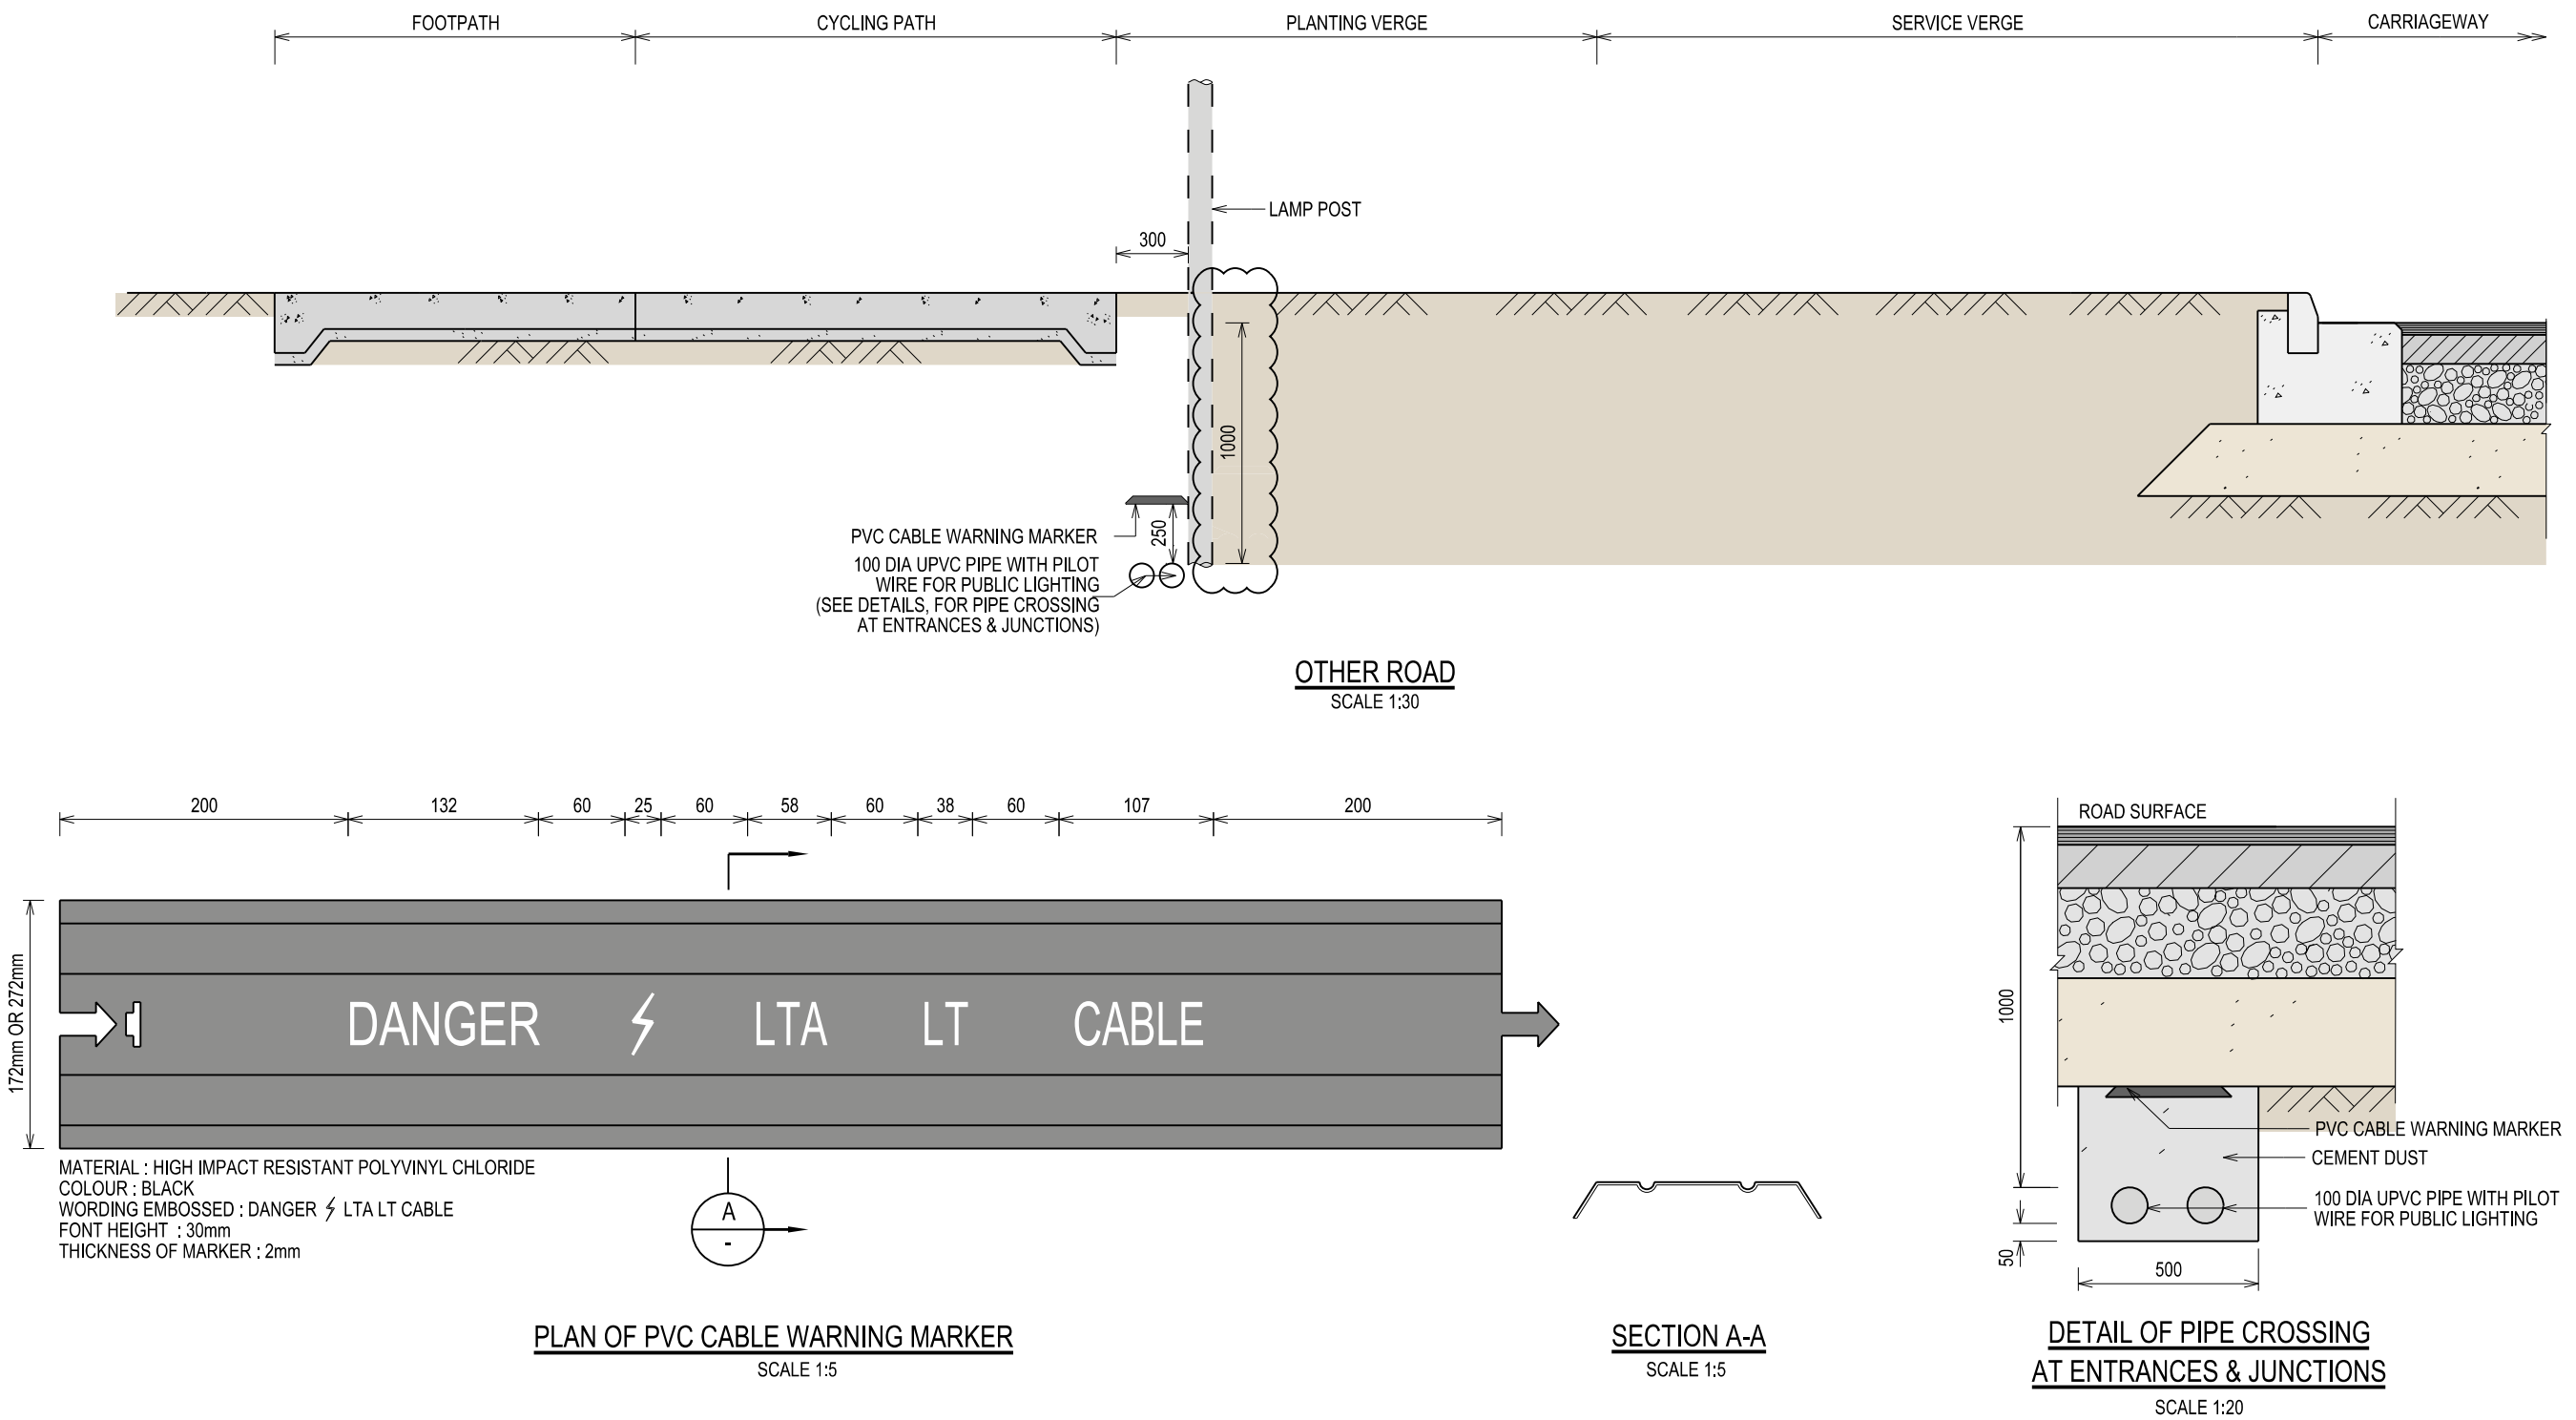

NOTES:

- Where there are opportunities to leverage on lightings from adjacent covered linkways, etc., there will be no need for additional lighting poles along cycling track. The additional lighting poles shall be considered for cycling tracks only when the lighting levels do not meet the minimum cycling track lighting (lux) requirements.
- Lighting design
 - For lighting design specification, to refer to the latest street lighting installation guidelines.
 - Cycling track upvc pipes for cable and cable warning marker shall be laid at the side of the cycling track.

- Where there is LTA commuter facilities abutting the cycling track e.g. covered linkway, the luminaire shall be mounted on the structure.
- Cement dust
 - The composition of cement dust consists of one part of cement and ten parts of granite dust.
 - The cement dust mixture shall be sprinkled with water and compacted in layers to achieve a hardened layer.
- Capping / stoppers should be provided for the pipes when not in use.

--	--	